


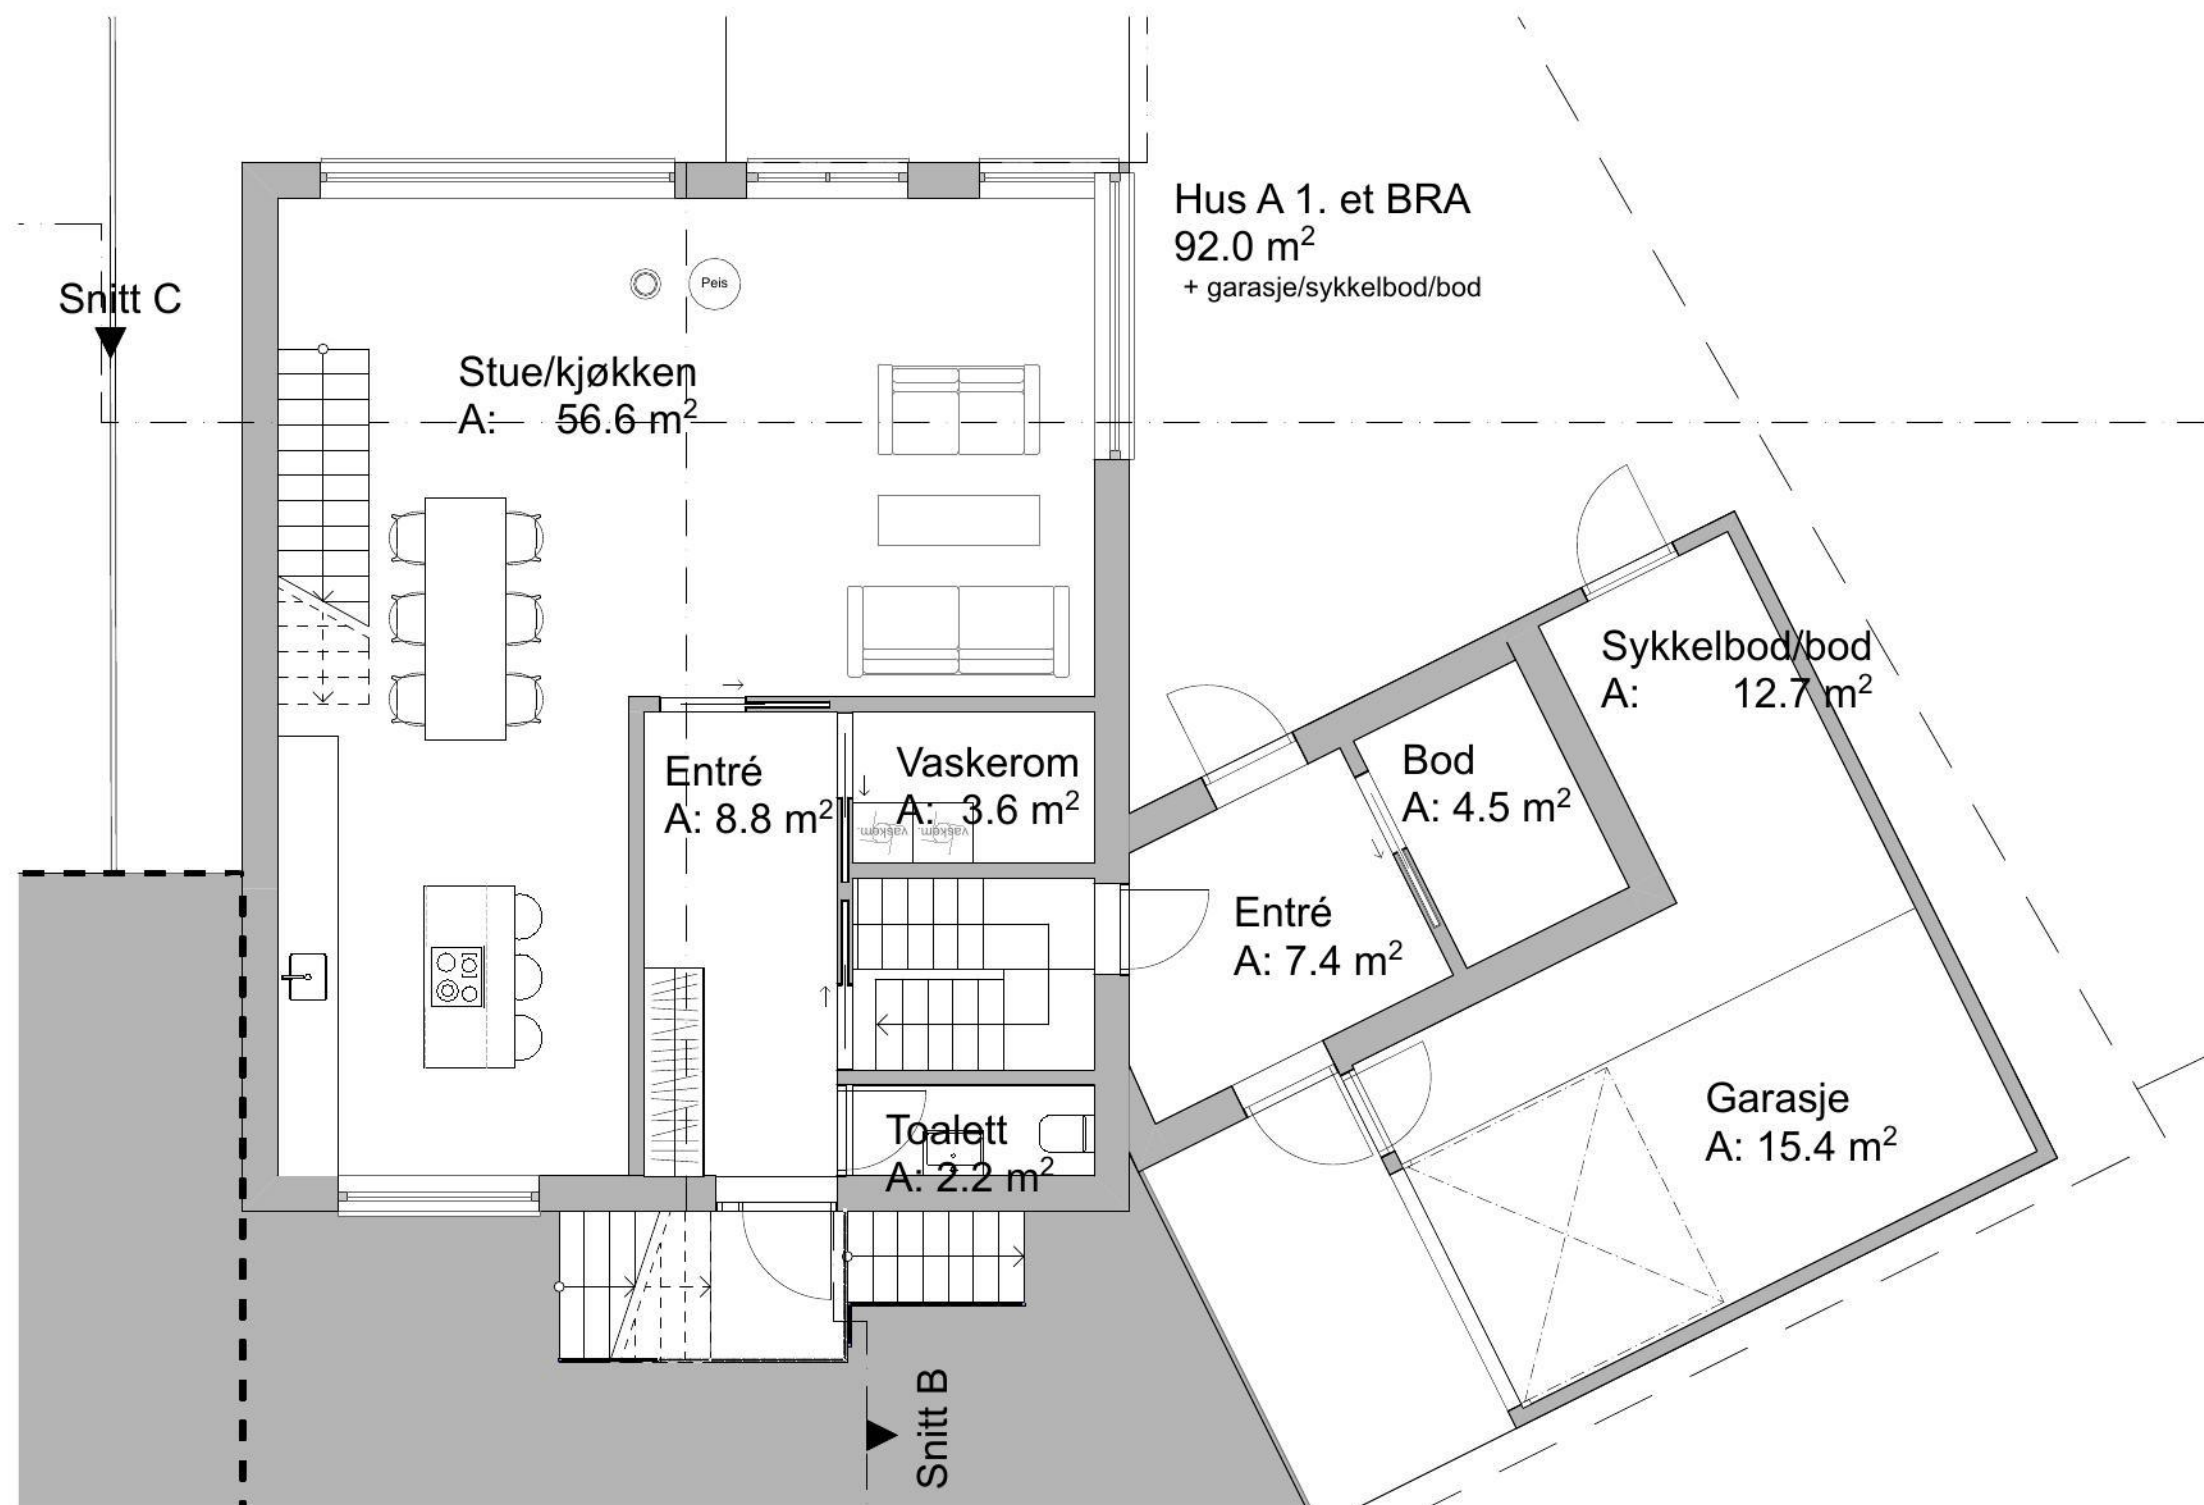

Prosjekt:
Reindsdyrveien 20

Tegning:
P 01 Plan 1. etasje hus A

Målestokk:
1:100 i A4

Tiltakshaver:
Espen Øverås
Prosjektadresse:
Reindsdyrveien 20 4323 Sandnes
Eiendom:
47/451
Saksnr:
PLAN22/00835

Tegnet av:
TA
Kontrollert av:
TA

Versjon	Dato	Revisjonstekst	Fase
05	25.09.2023	Søknad	Planendring
04	20.09.2023	Søknad	Planendring
03	01.06.2023	Søknad	Planendring
02	02.05.2023	Søknad	Utkast planendring
01	10.02.2023	Søknad	Utkast planendring