


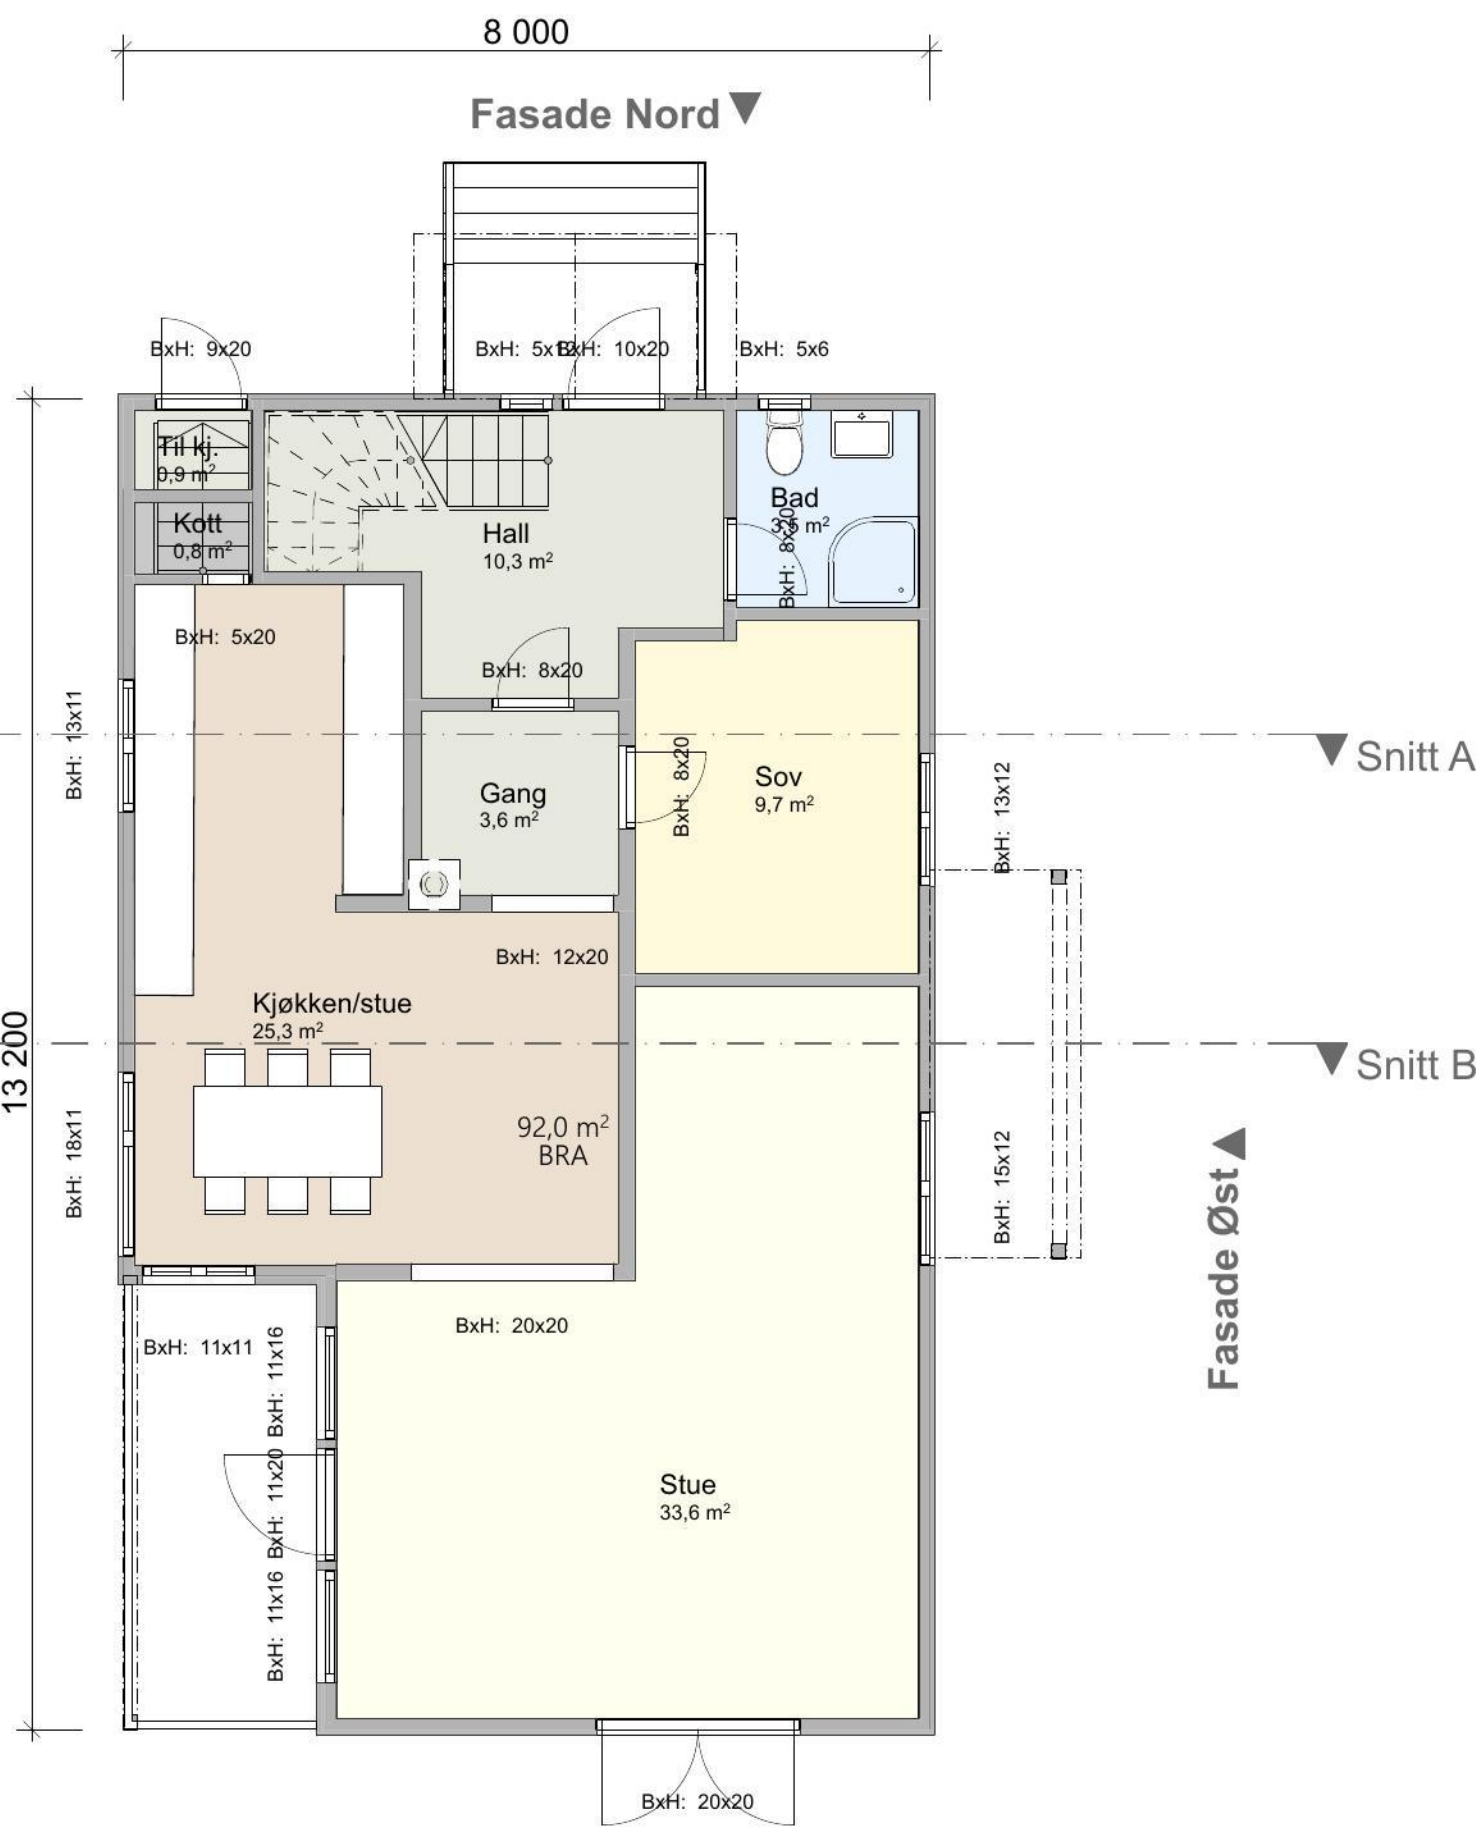

BRA:
Kjeller = 28m2
1. etg. = 92m2
2. etg. = 81m2

Dato endret:
29.11.2023

Prosjekt: Rønneldveien 358	Gnr./Bnr. 1097/10
Tiltakshaver: Thorbjørn Rostad Stupeveien 13 1718 Greåker	
Prosjekterende: Marberg Bygg- og Tegneservice Svartedalskroken 25 1739 Borgenhaugen	Tlf: 48 18 44 65 clas@marberg.no
© Alle rettigheter tilhører Marberg Bygg- og Tegneservice. Kopiering eller bruk av disse tegningene er forbudt uten skriftlig samtykke	
Tegning: Plan 1. etasje	Dato opprettet: 11.08.2023
	Målestokk: 1:100
	Tegningsnr.: A20-02