


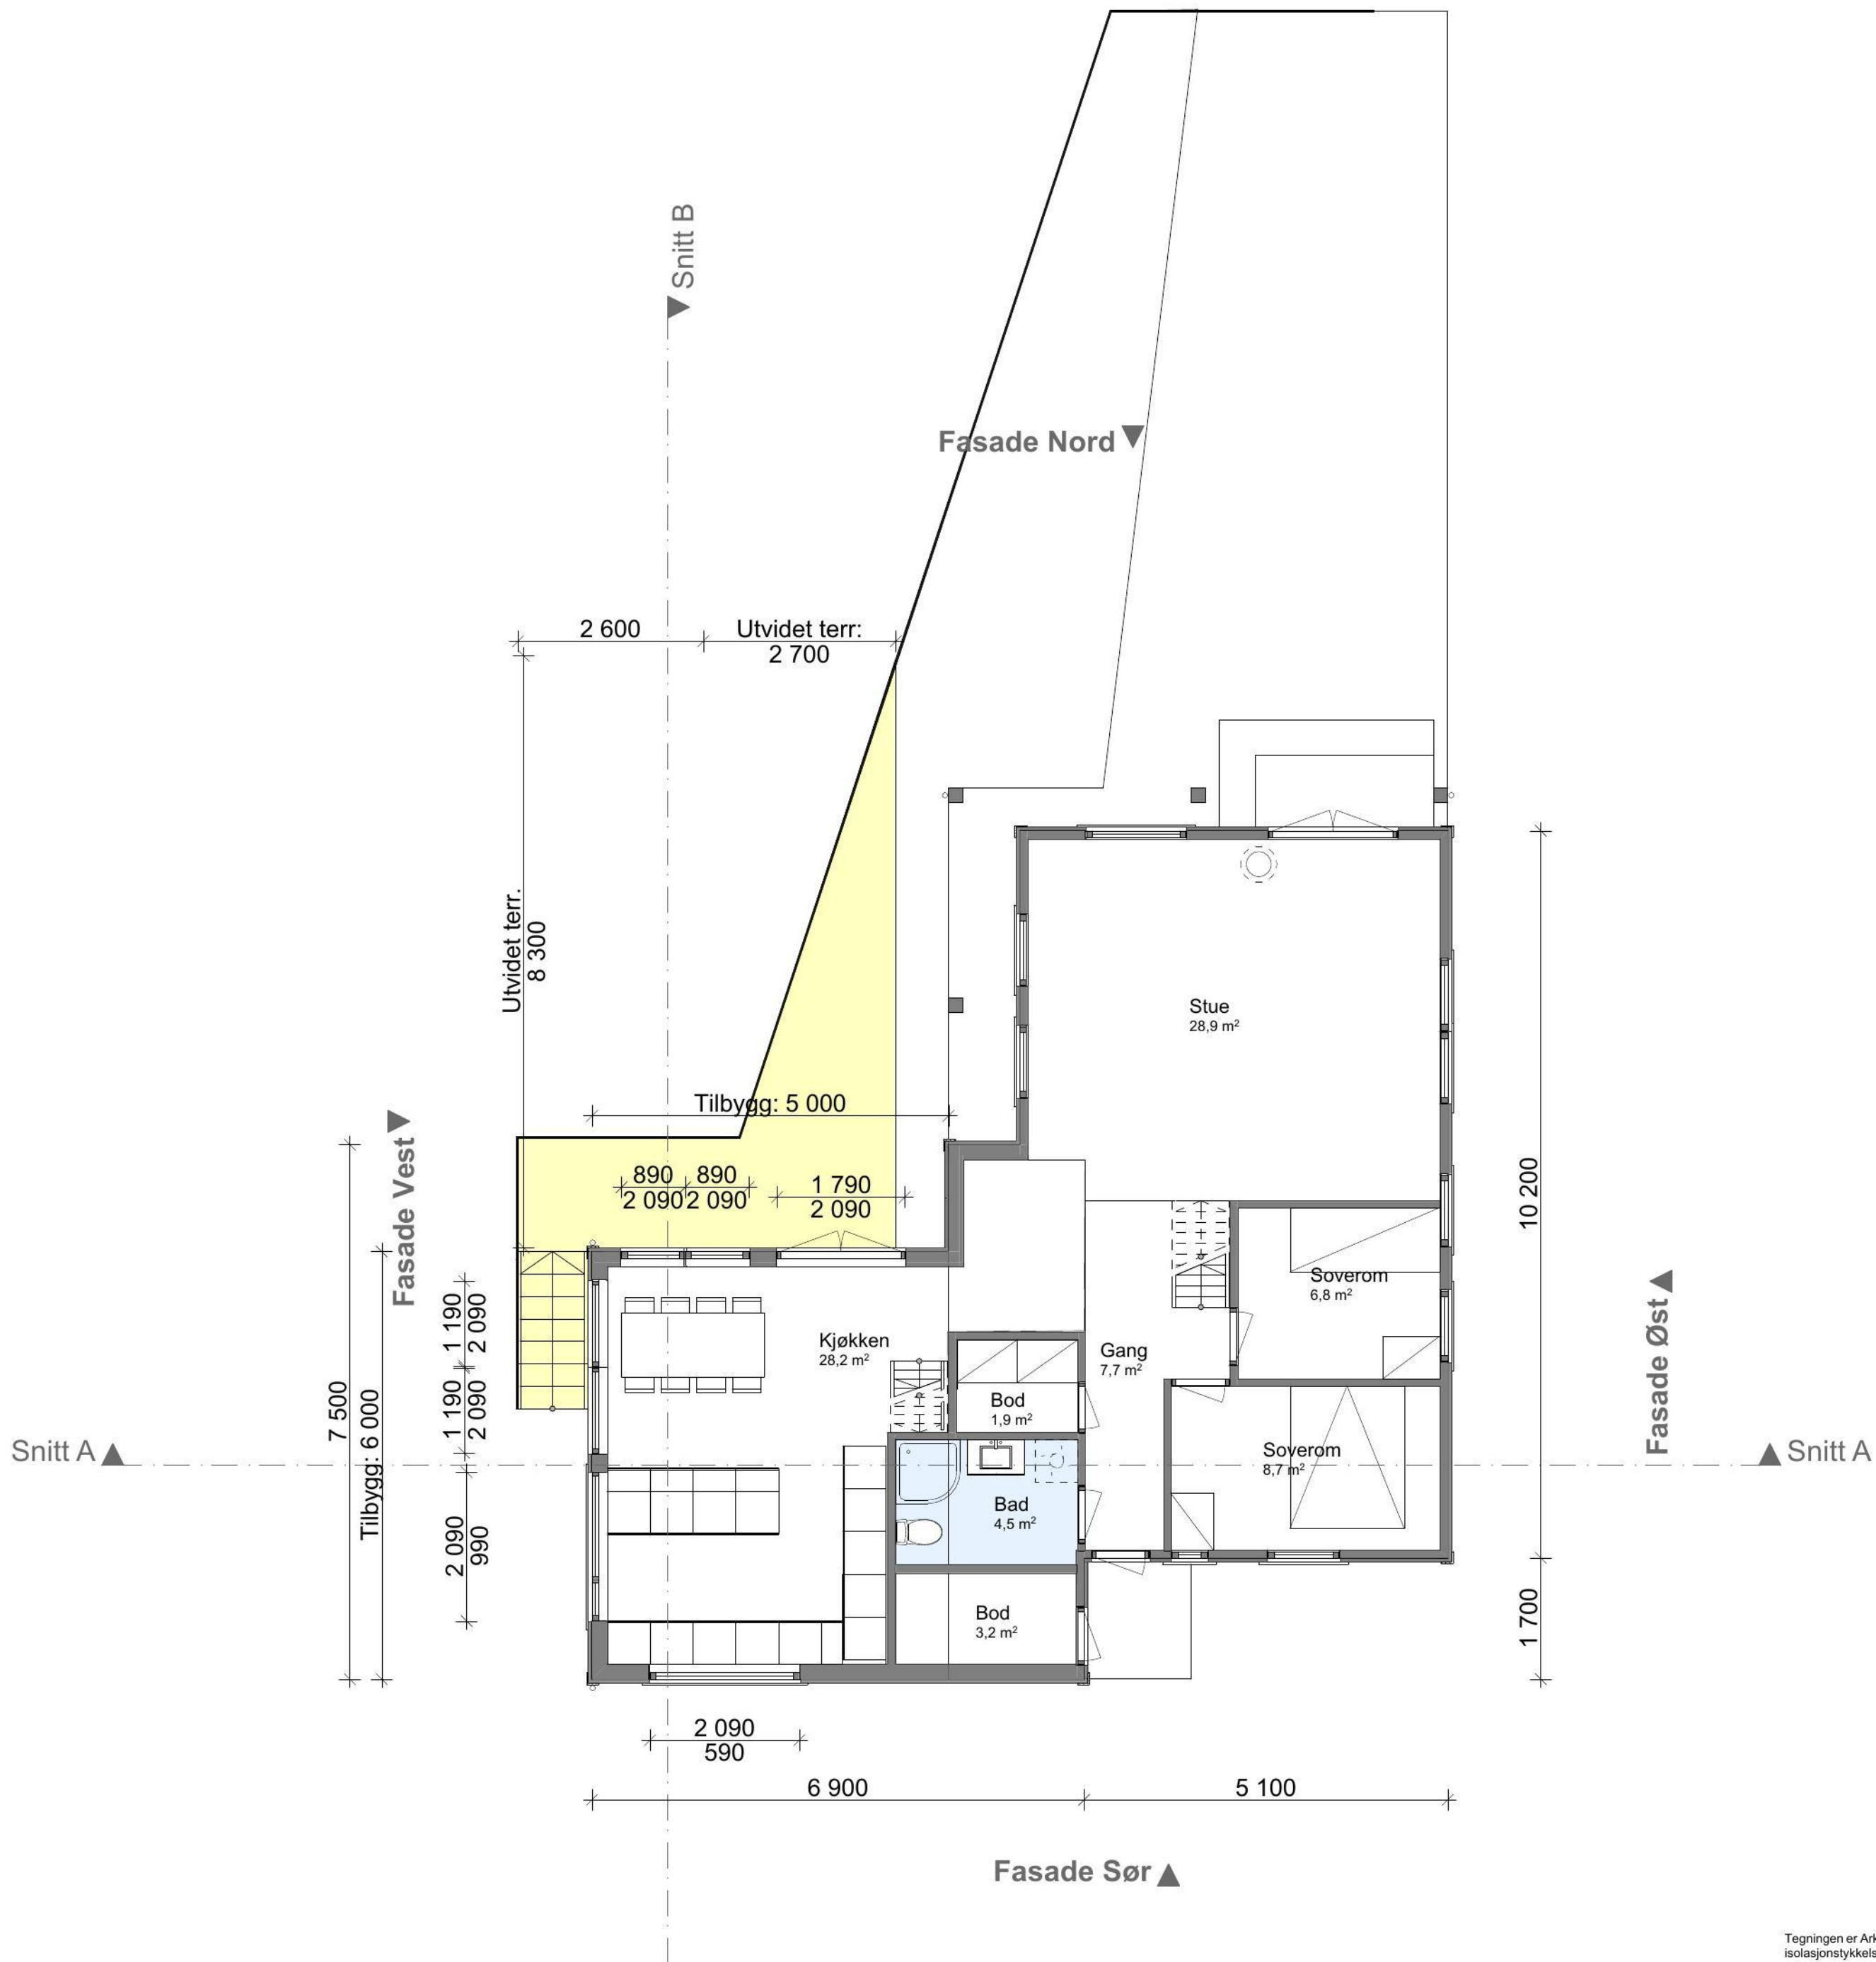

Tegningen er Arkitektonisk prosjektert. Dimensjoner, isolasjonstykkelser, vindusstørrelser, porter m.m. er basert på erfaringstall, men må dimensjoneres og kontrolleres. Tegningen er Molo consulting AS sin eiendom inntil varen er betalt. Kopiering eller bruk av tegningen tillates ikke uten tillatelse.

Eksisterende bebyggelse må kontrolleres opp mot faktiske forhold

Situasjonskartet er hentet fra kommunens kart base, men kan inneholde feil.			
-	-	-	-
-	-	-	-
-	-	-	-
-	-	-	-
-	-	-	-
-	-	-	-
Rev.:	Dato:	Beskrivelse:	Sign:
Prosjekt:		MOLO Molo Consulting AS post@molo.no www.molo.no Signatur: F.B. Kontroll: - Arkitektonisk Prosjekterende: Molo Consulting AS	
Tilbygg og arealoverføring			
Byggeadresse:			
Røstadvdeien 244 4640 Kristiansand Gnr./Bnr./Festnr. 435/34			
Tiltakshaver:			
Stian Ramsland Eidsåvegen 2 4645 Nodeland			
Tegningsfase:			
Søknad		Format:	Dato opprettet:
		A3 1:100	29.11.2023
Tegning:		Prosjektnr.:	
E10-01	Plan 1. etasje	23080	