
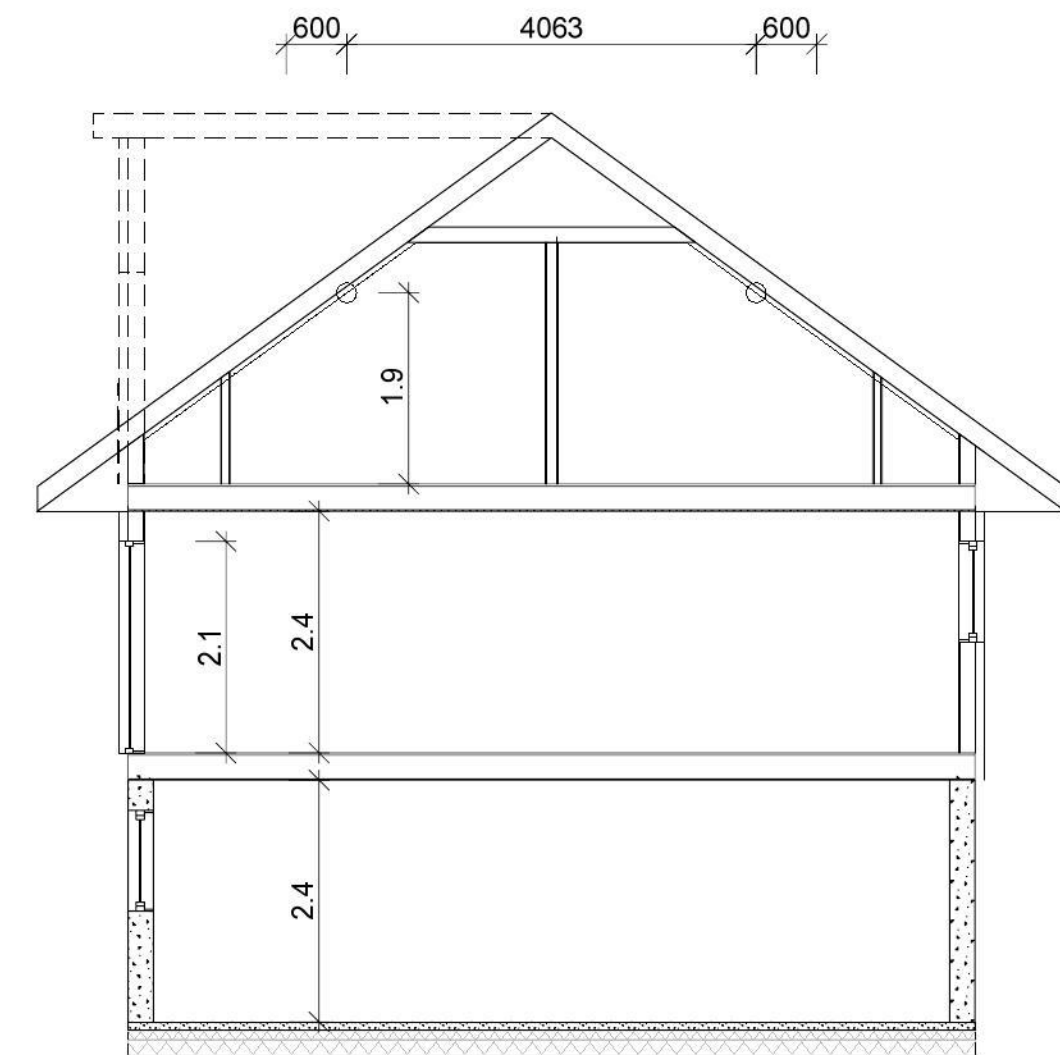


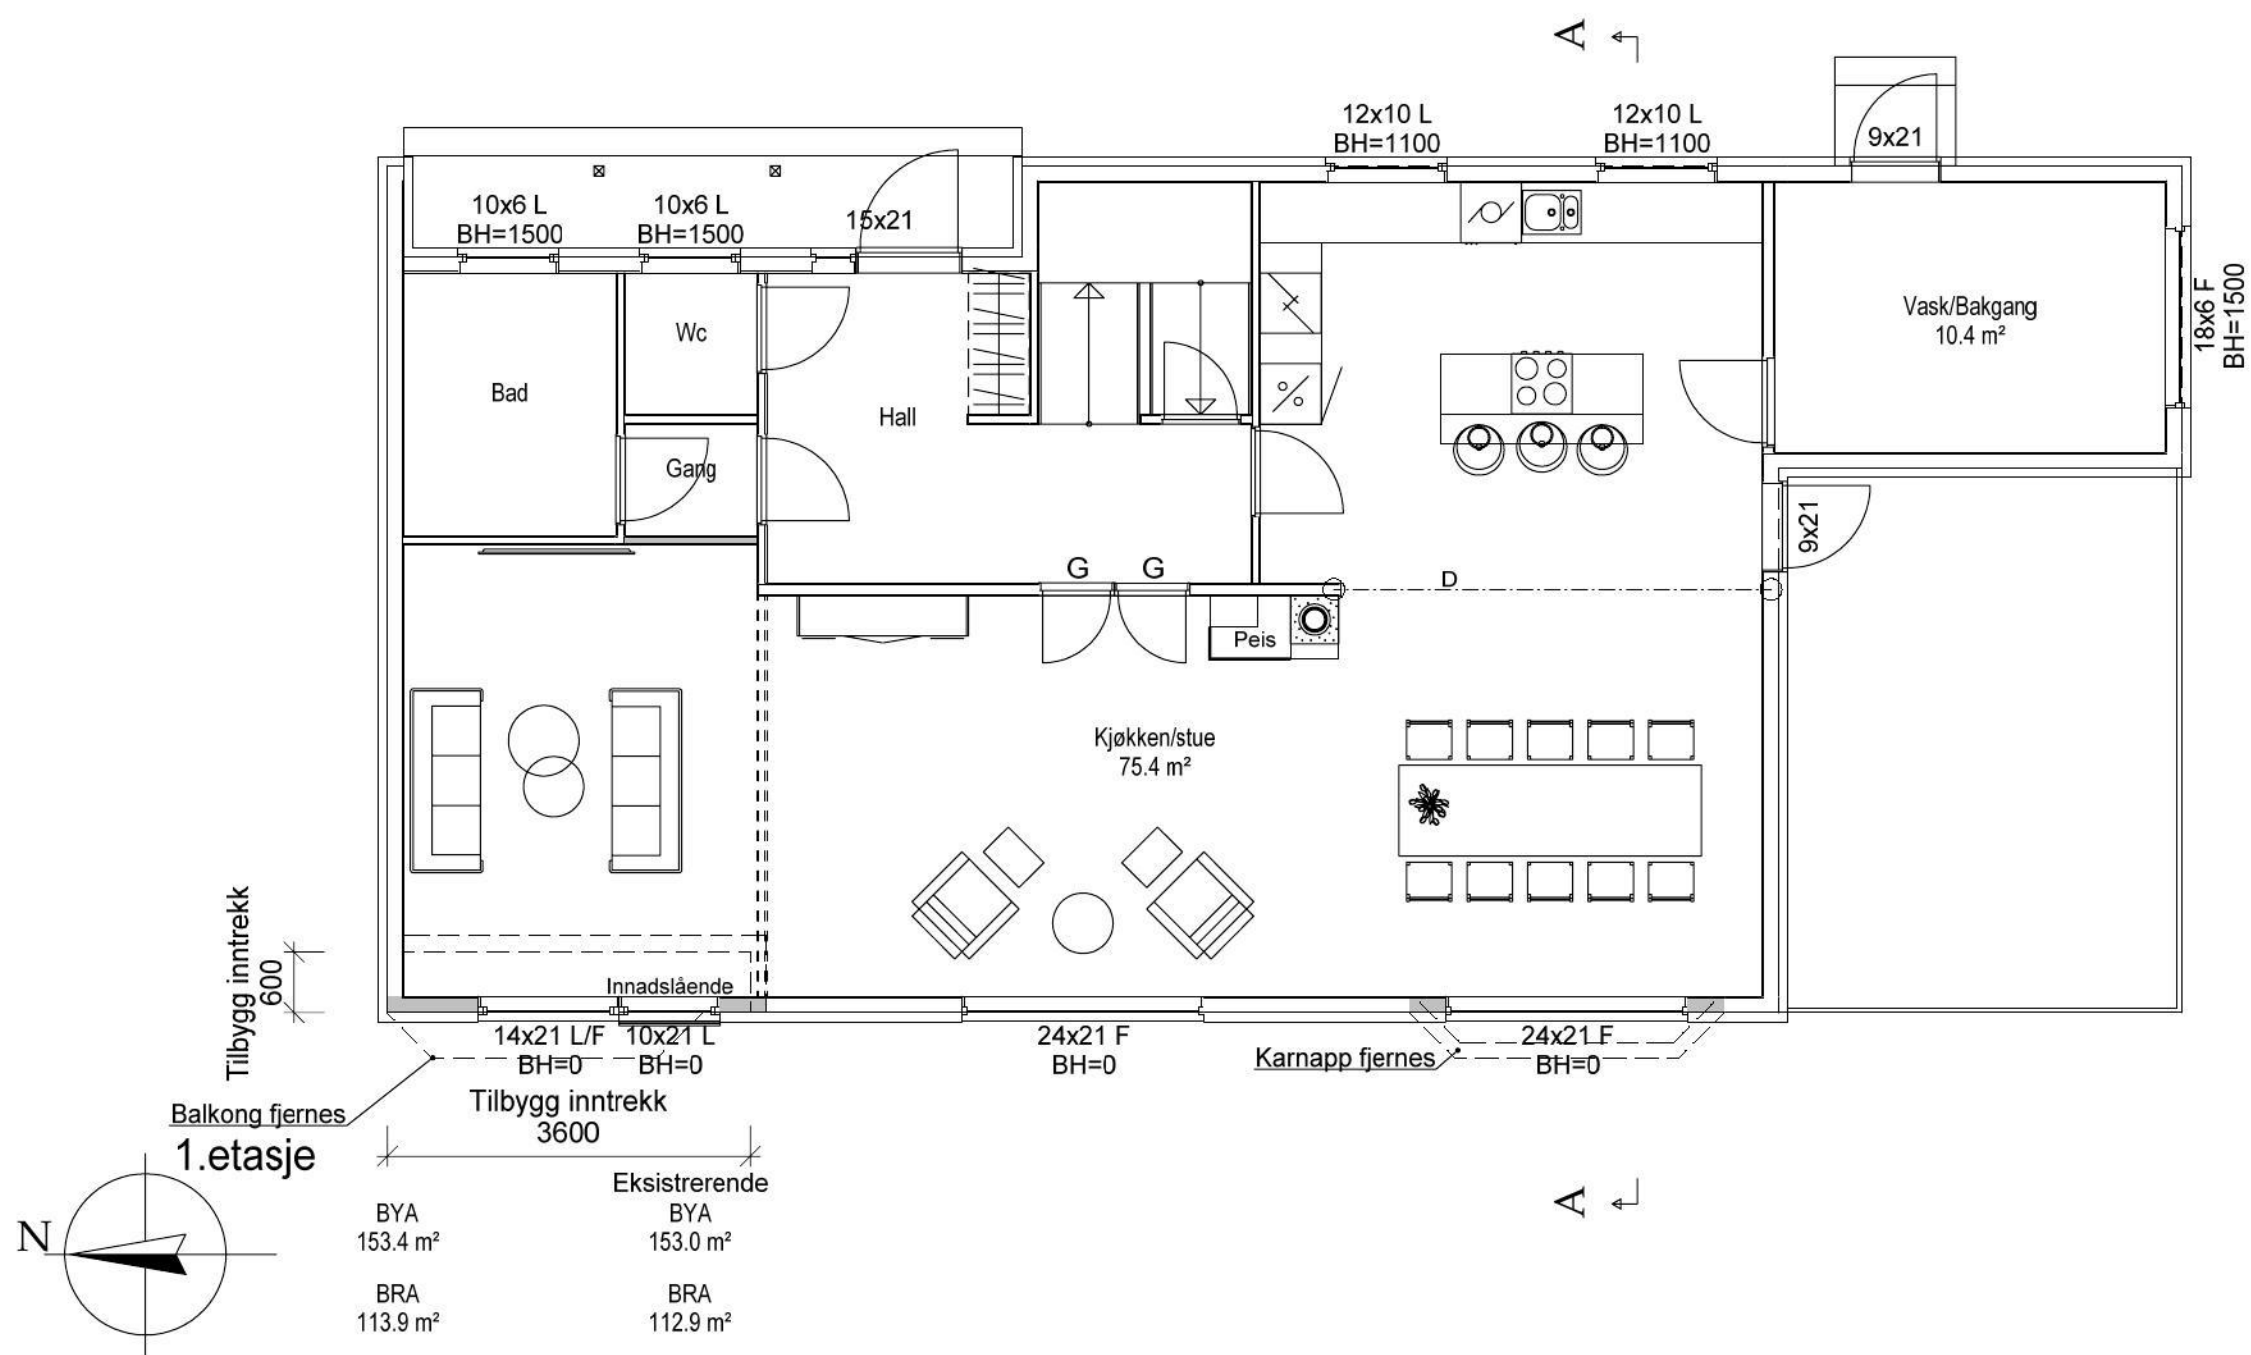


Snitt A-A

- vegg fjernes
- eks. vegger beholdes
- nye vegger

Tilbygg/Påbygg/Ombygg:

Alle mål må kontrollmåles både for prosjektering og utførelse på byggeplass av utførende byggefirma.

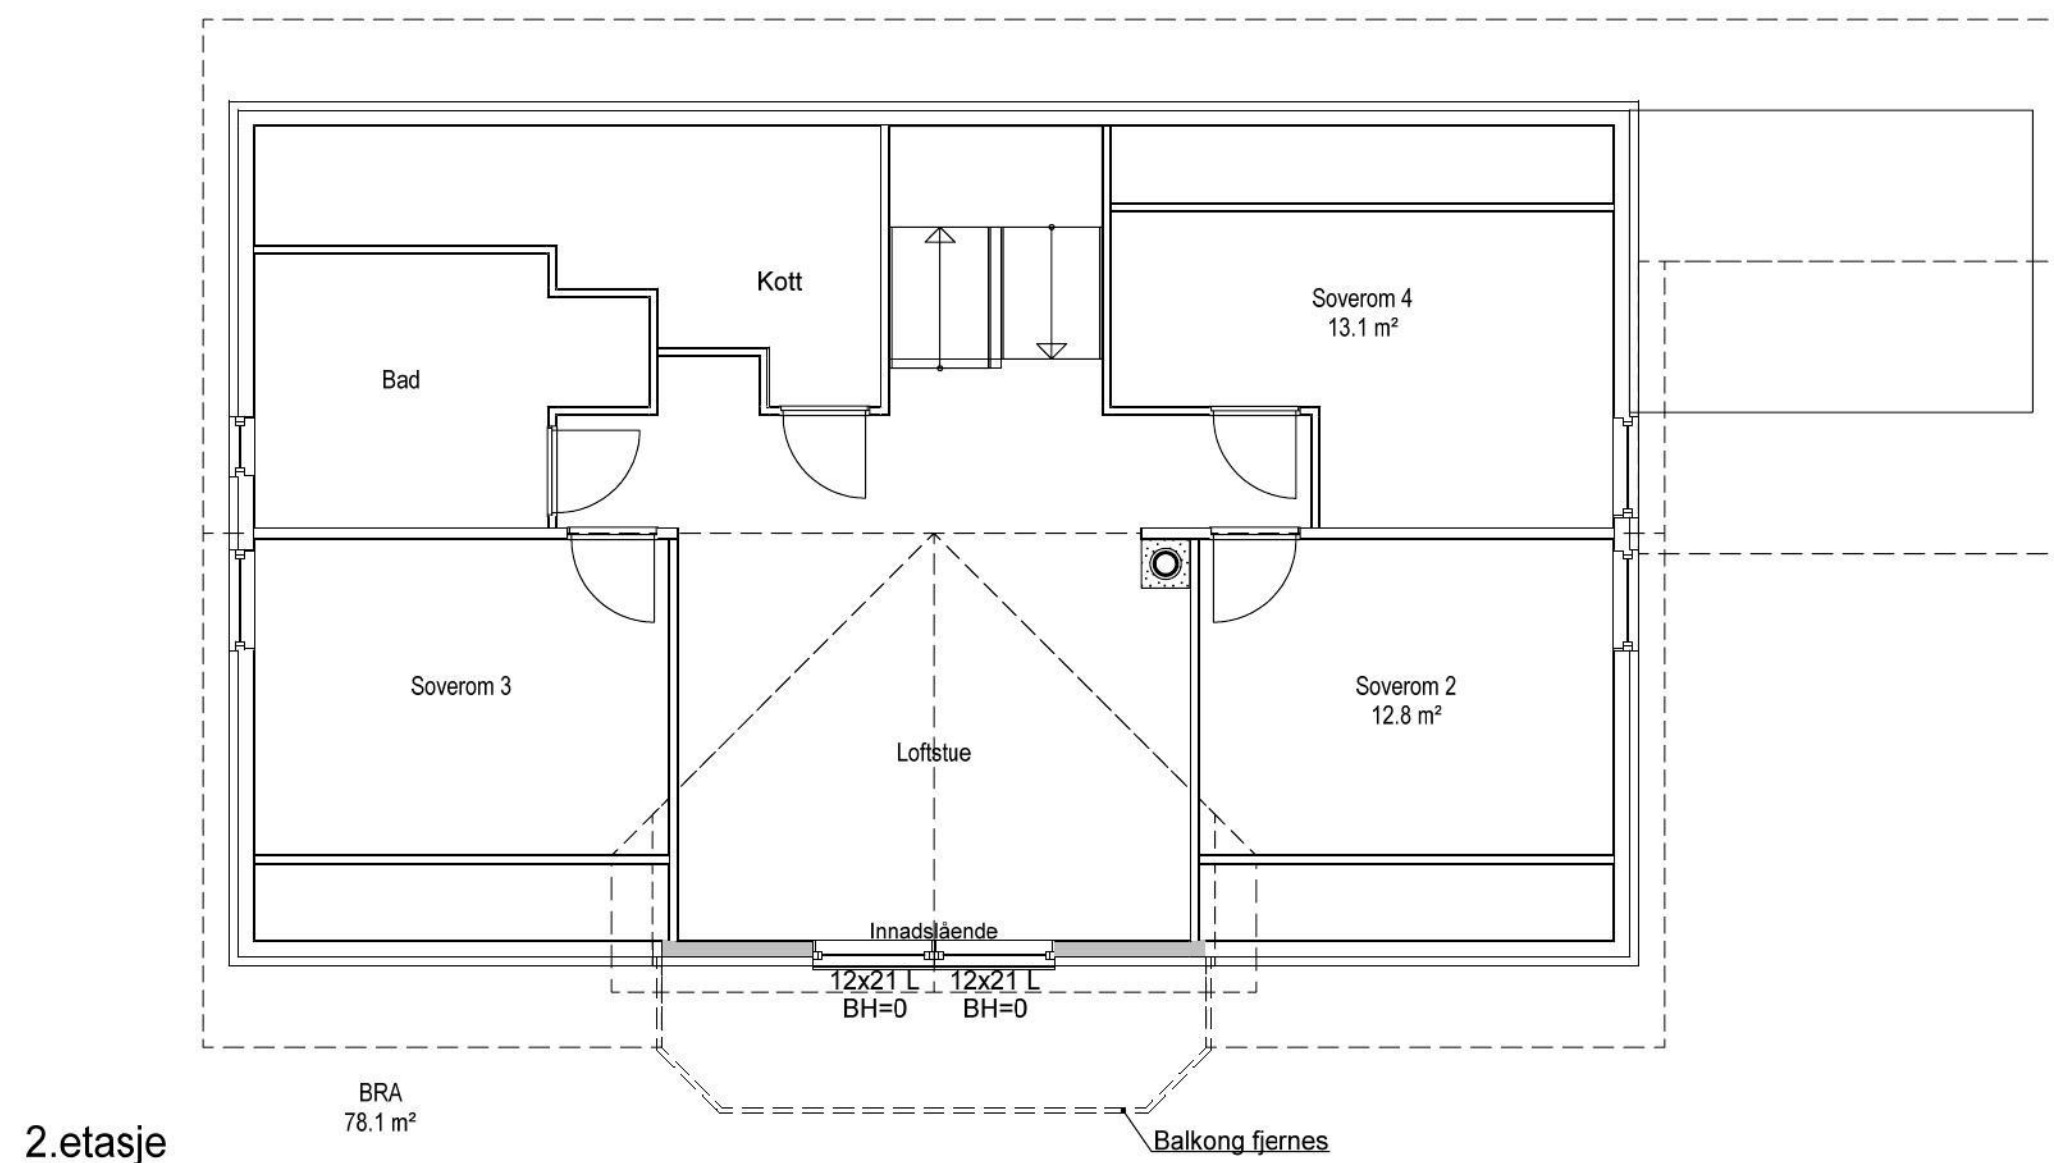

Plan

	Tiltakshaver: Annette og Kirsten Risa Skovmose			Utført av:	
	Byggeplass: Skaraveien 48				
	Kommune: Sandnes G.nr: 34 B.nr: 270				
	Tegn: HS	Arkitekt:	Type:		
	Dato: 22.12.23	Tegn.nr: 501			
	Mål: 1 : 100		Prosjekt nr DDS/IHT: skar / 8879		www.iht.no
Tegningen må verken helt eller delvis kopieres eller benyttes ved utførelse av arbeider som rettighetsinnehaver ikke medvirker i.					