



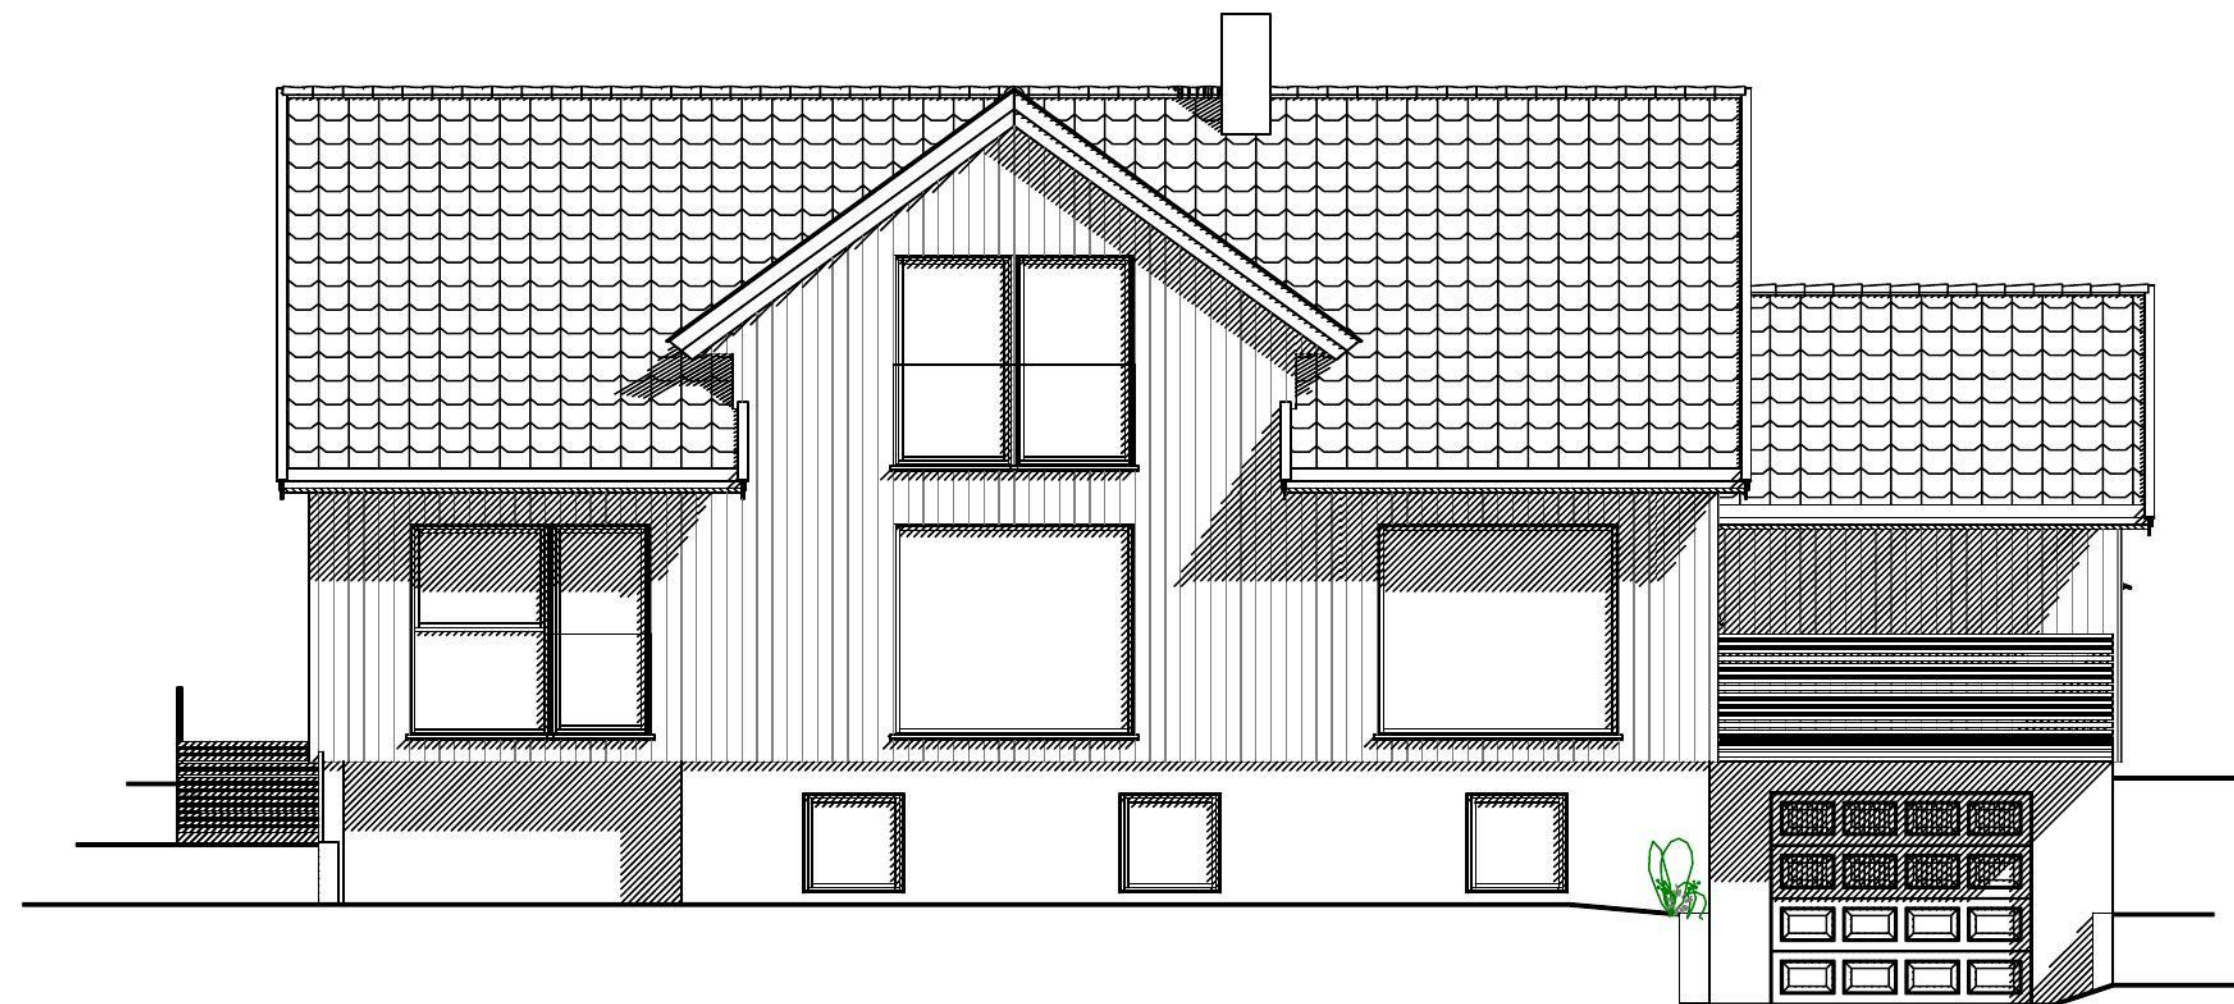

Fasade Vest

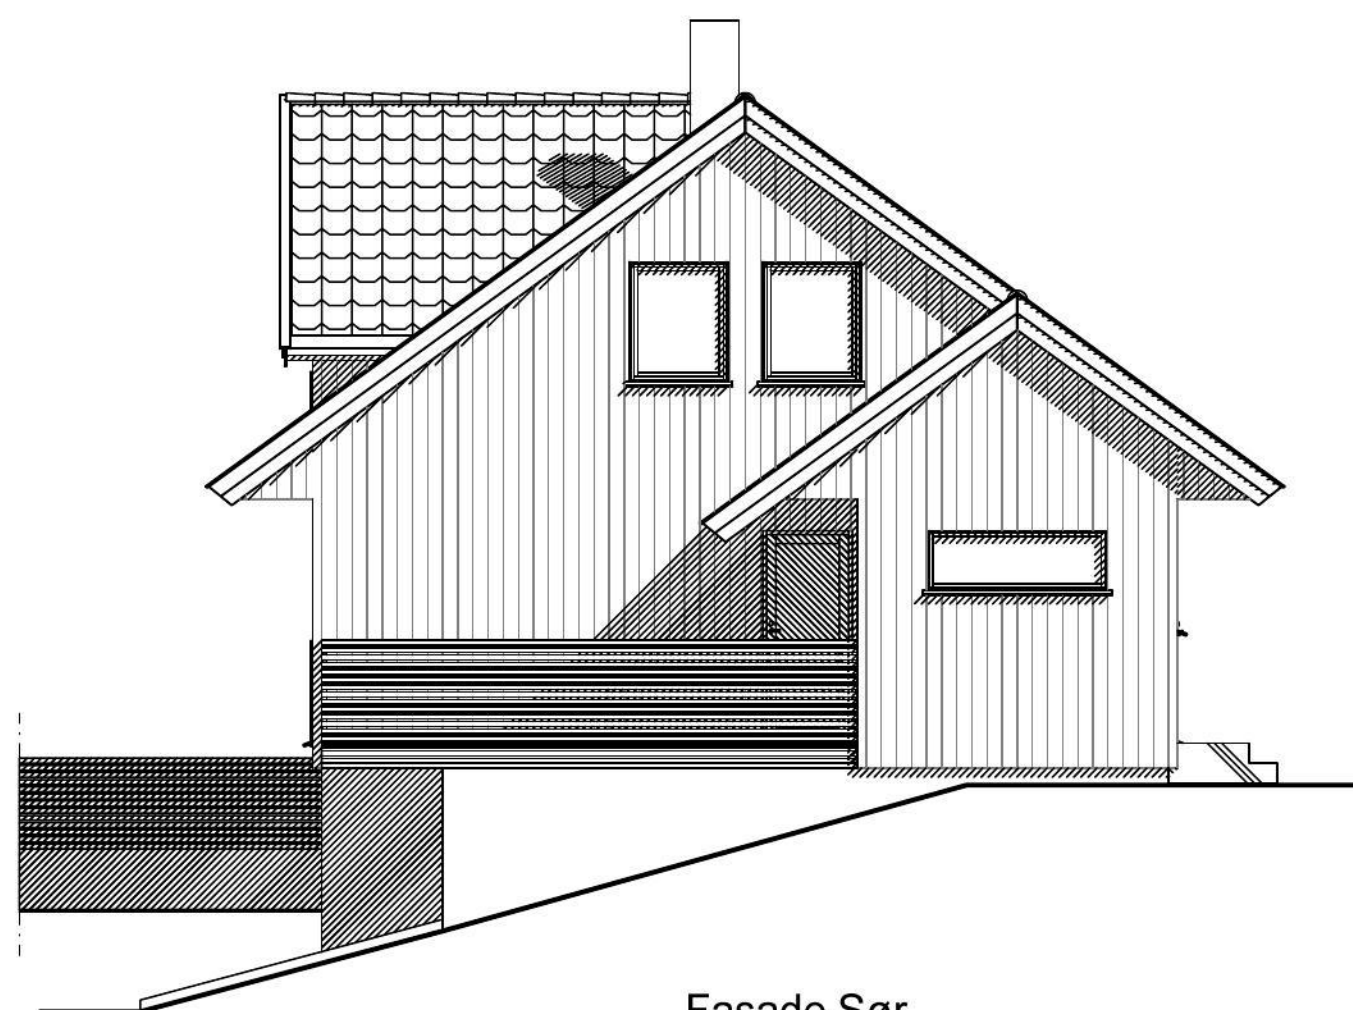

Fasade Sør

Uendret terreng i forhold til dagens situasjon

Tilbygg/Påbygg/Ombygg:

Alle mål må kontrollmåles både for prosjektering og utførelse på byggeplass av utførende byggefirma.

Arealberegninger i hht. NS 3940	Bruksareal BRA kvm			
	Pr etasje	Utyendig bod/garasje	Tilbygg	Sum BRA
Underetasje	92.6	25.8	0.0	118.4
1. etasje	112.9	0.0	1.0	113.9
2. etasje	78.1	0.0	0.0	78.1
SUM :	283.6	25.8	1.0	310.4
BYA :	153.0	0.0	0.4	153.4

Fasader



DATA DESIGN SYSTEM

Tiltakshaver:	Annette og Kirsten Risa Skovmose		Utført av:
Byggeplass:	Skaraveien 48		ARKITEKT KONTORET IHT www.iht.no
Kommune:	Sandnes	G.nr: 34 B.nr: 270	
Tegn: HS	Arkitekt:	Type:	
Dato: 09.01.24	Tegn.nr: 510		
Mål: 1 : 100	Prosjekt nr DDS/IHT: skar / 8879		

Tegningen må verken helt eller delvis kopieres eller benyttes ved utførelse av arbeider som rettighetsinnehaver ikke medvirker i.