
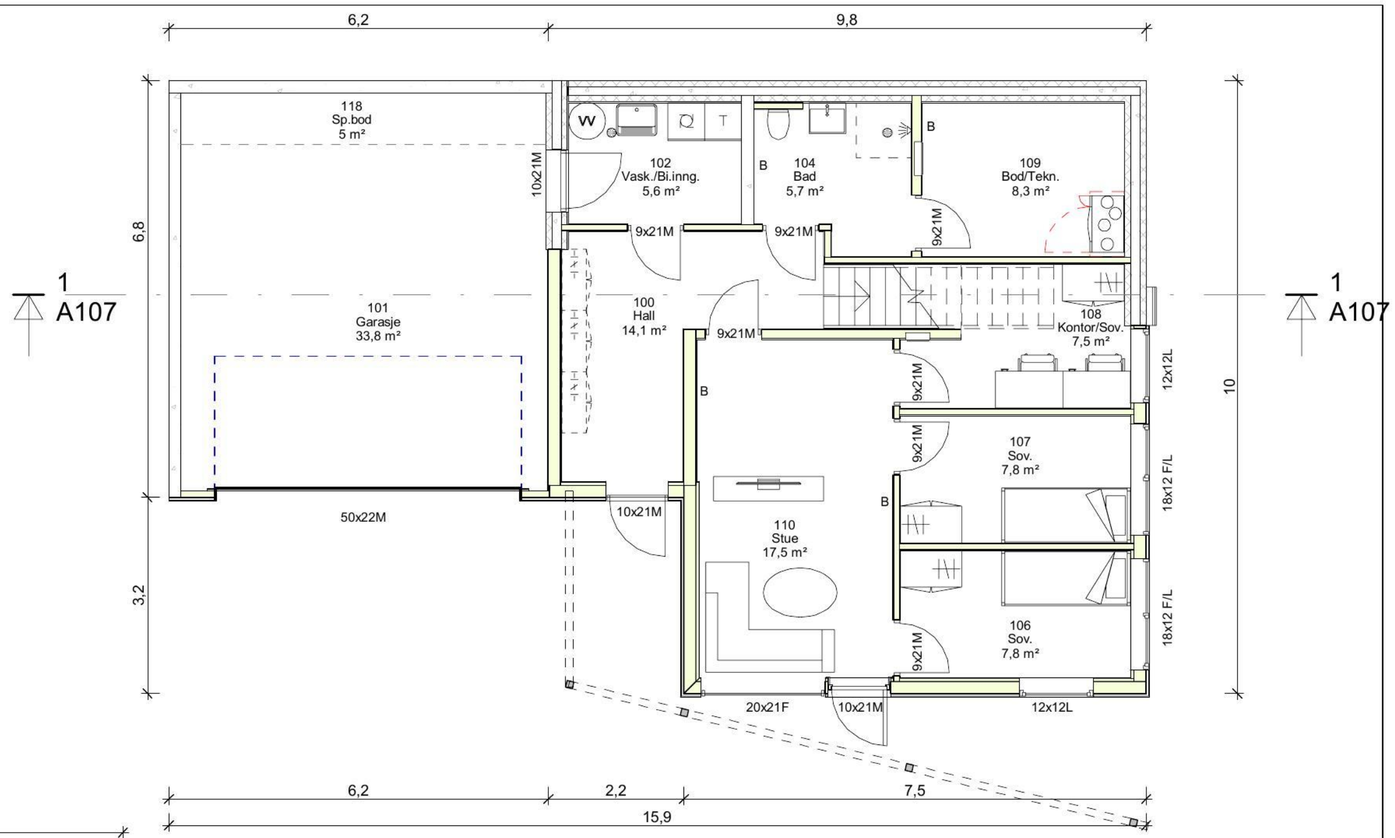


1 A107

1 A107

Plan 1 Etasje
1 : 100

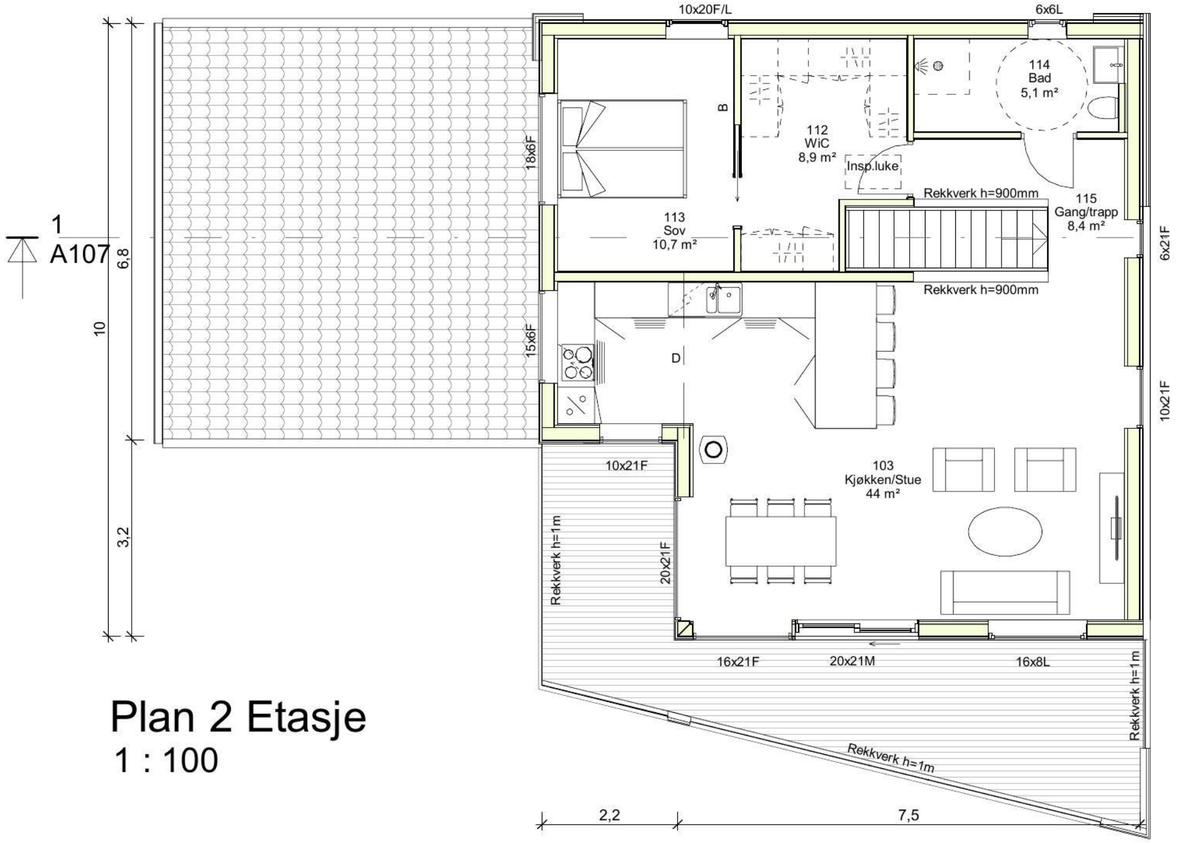

1 A107

1 A107

Plan 2 Etasje
1 : 100

BRA etter NS3940	
Navn	BRA

1 Etg	80,9 m²
2 Etg	80,5 m²
Garasje	38,8 m²
Utvendig overbygd	11,8 m²
Sum	212 m²

BYA Etter NS3940	
Navn	Areal
BYA	145,8 m²

Rev.	Revisjonen gjelder	Utført	Kontr.	Dato

Sagen Bolig
Skippergata 14

Plan

Målestokk 1 : 100	Dato	24.11.23
	Tegnet	AM
	Kontr.	EK
Arkstørrelse A3	Prosjektnr.	359
Tegningsnr. A106	Rev.	

TYTEK
Kong Carls gate 14
4010 Stavanger
Tlf: 976 56 526
tormod@tytek.no

27.11.2023 10:04:26