


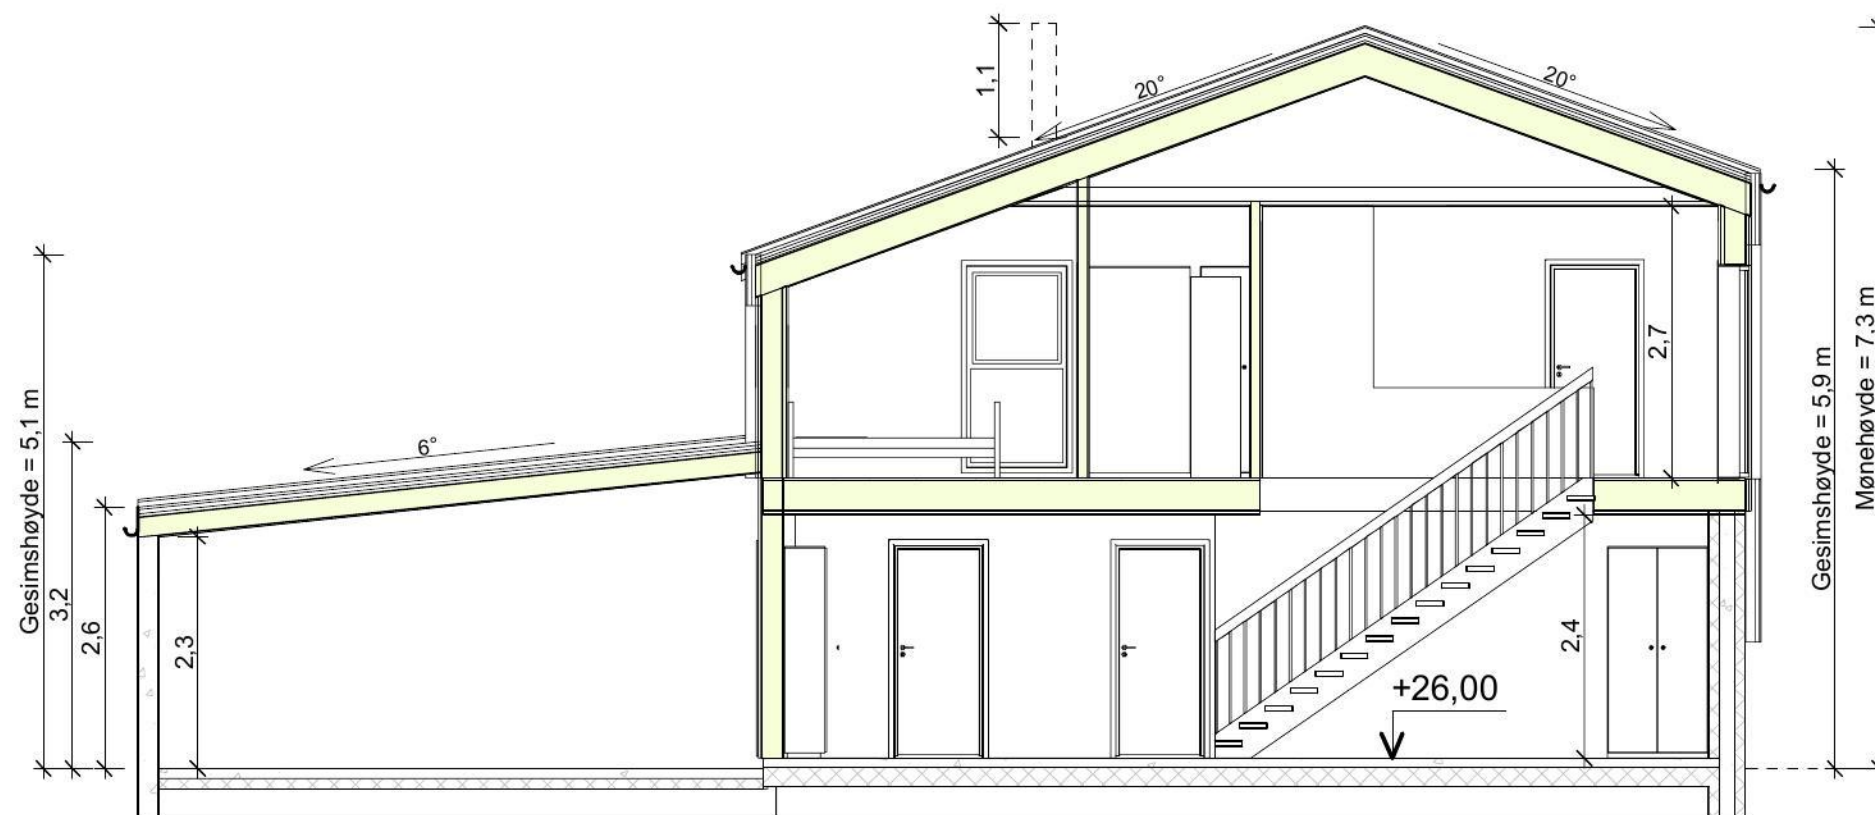

Rev.	Revisjonen gjelder	Utført	Kontr.	Dato
	Sagen Bolig Skippergata 14	Målestokk	Dato	27.11.23
		1 : 100	Tegnet	AM
			Kontr.	EK
	Snitt	Arkstørrelse A4	Prosjektnr.	359
		Tegningsnr. A107	Rev.	

Isolasjon i bygningsdeler iht energiberegning.



Kong Carls gate 14
4010 Stavanger
Tlf: 976 56 526
tormod@tytek.no