


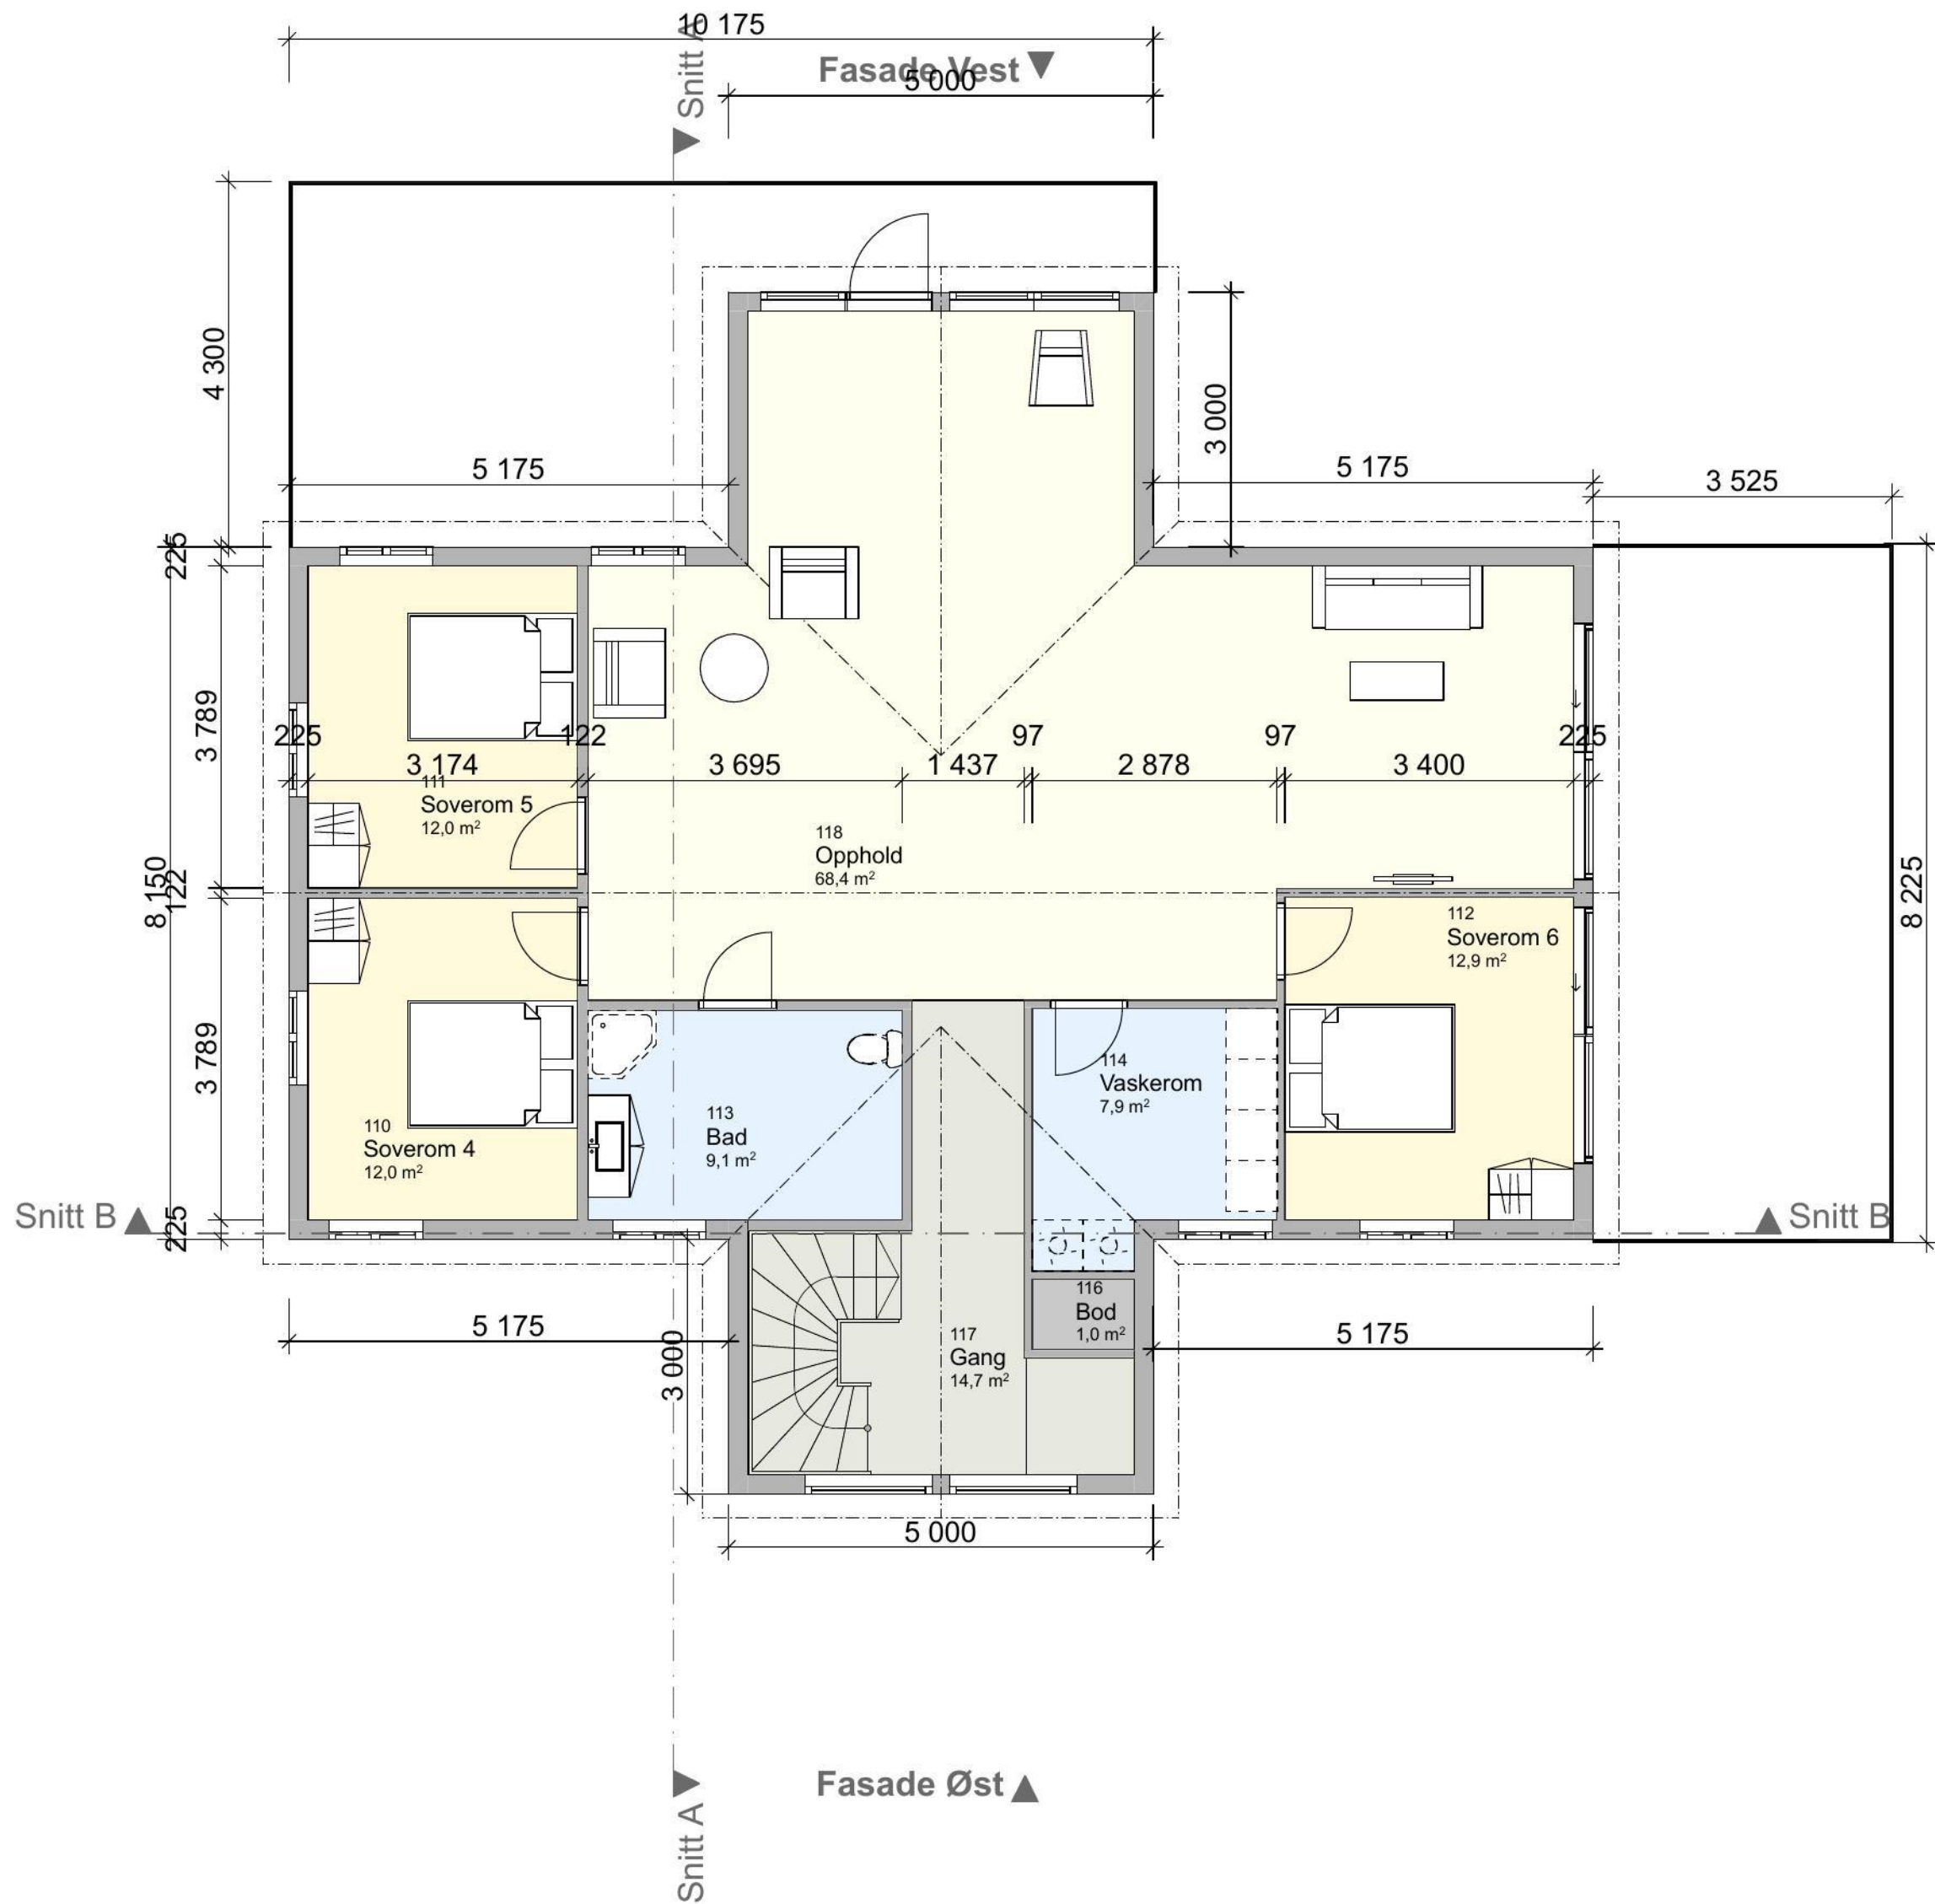

Prosjekt: Skjulstadveien 188	Kontroll prosjekt:	
	Sign.:	Kontroll:
Tiltakshaver: Pål Alexandersen Skjulstadveien 188 1746 Skjeberg	Gnr./Bnr./Festenr.: Gnr 1104/Bnr 6	
Prosjekterende: Dammyr Bygg As Tomteveien 21 1618 Fredrikstad		
© Alle rettigheter tilhører utførende for prosjektering, kopiering eller bruk av disse tegningene er forbudt uten skriftlig samtykke	Dato: Dato oppr.	
Tegning: Plan 2 etg	Målestokk: 1:100	
	Tegningsnr.:	Rev.:
	A20-2	