




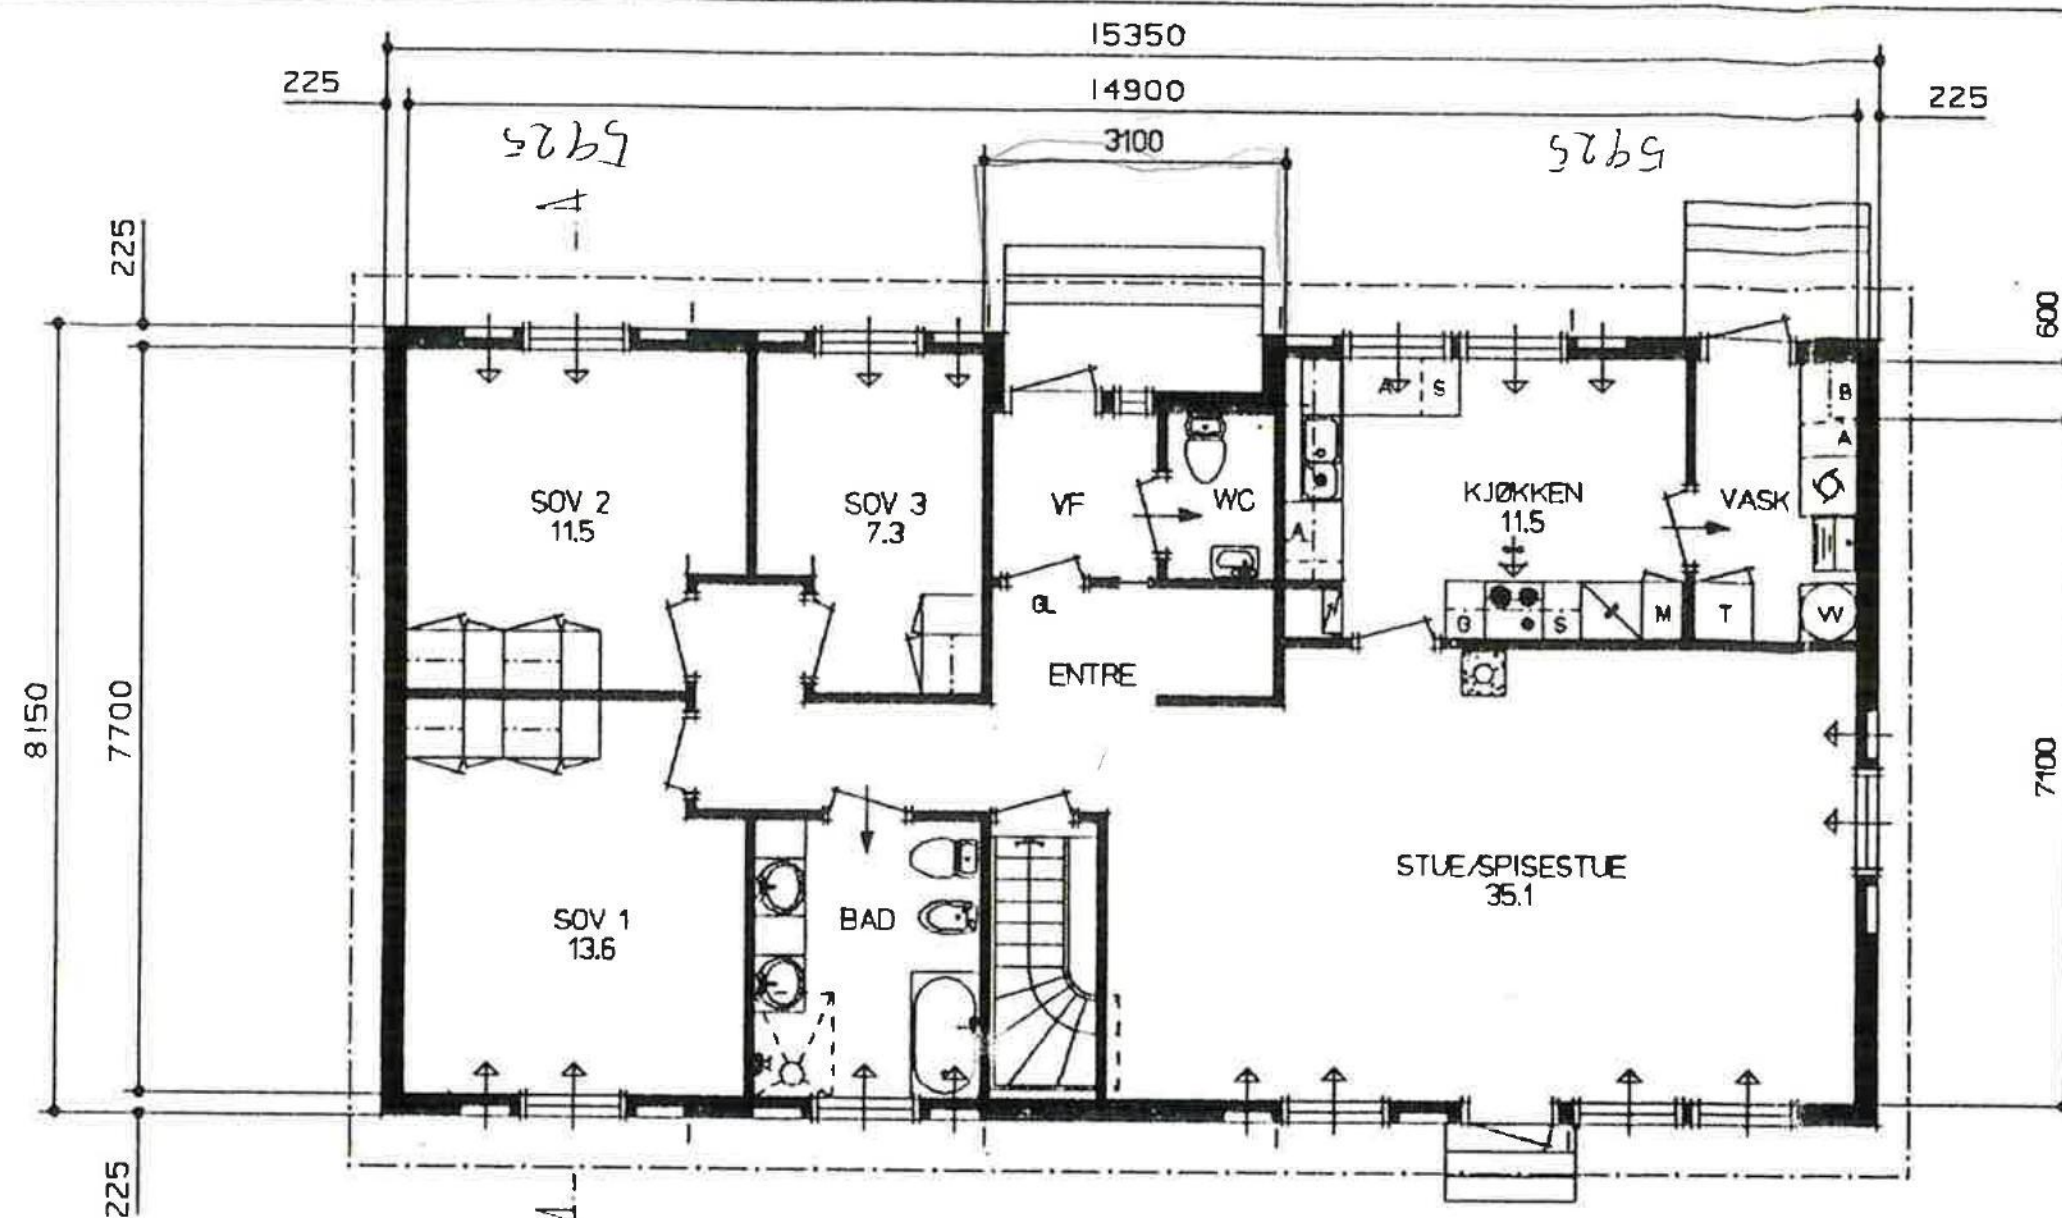

PLAN MK.410.07-P-MOD

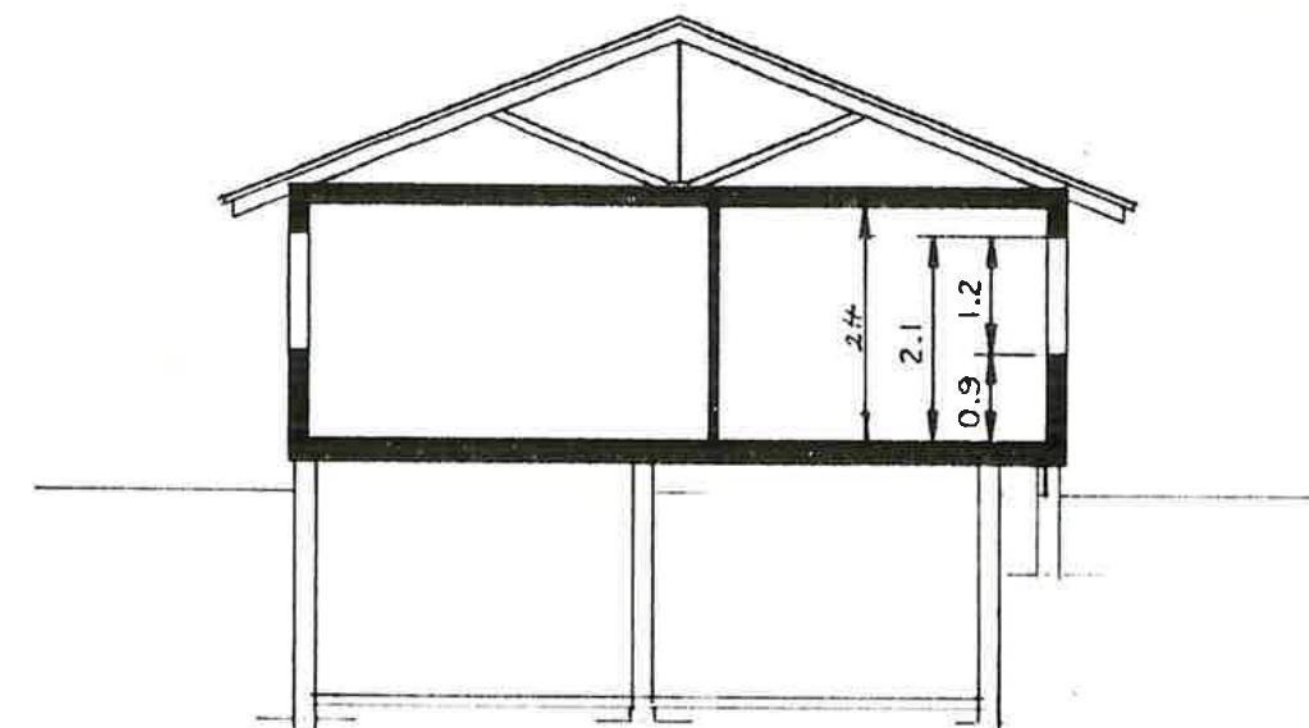

SNITT

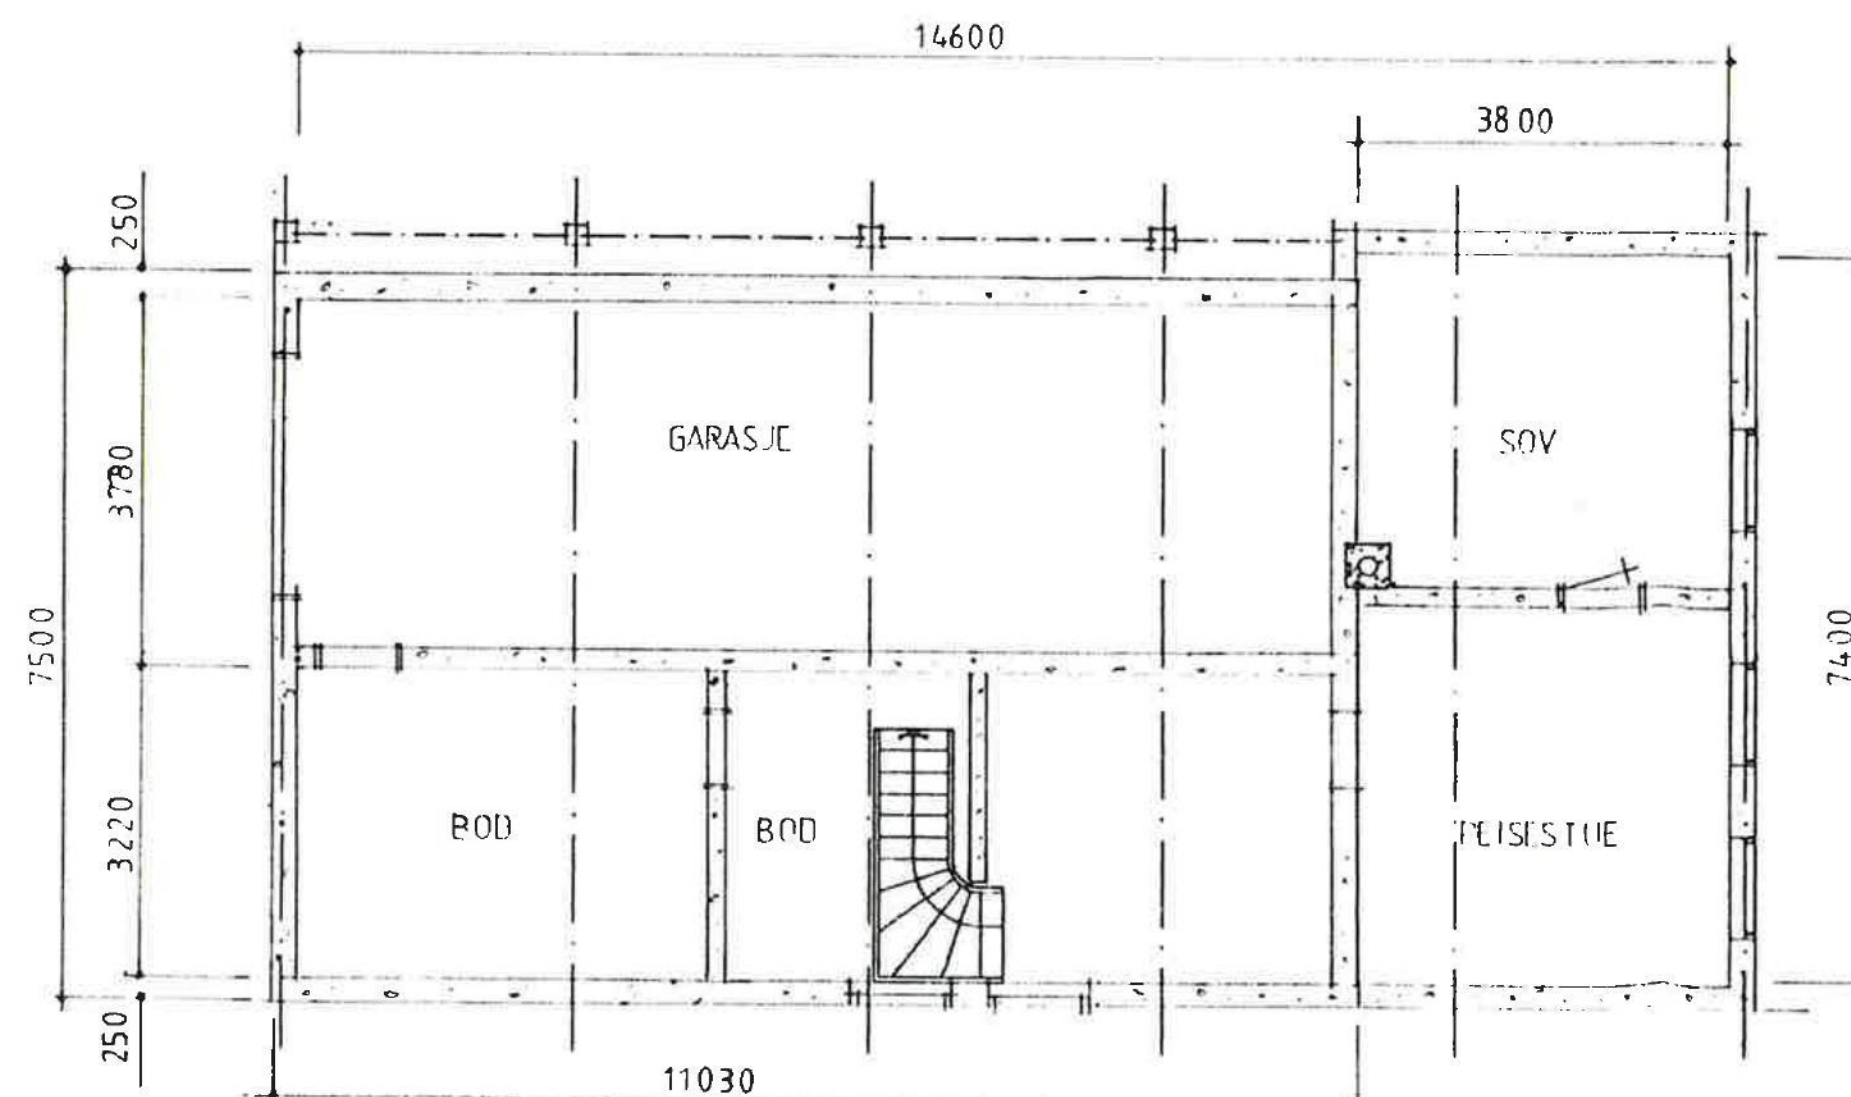

MIDLERTIDIG FUNDAMENTPLAN
MÅ IKKE BENYTTES SOM ARBEIDSTEGNING

BRUKSAREAL	BRA :	BEREGNET AREAL	BA :
HOVEDPLAN	1129. KVM	BA	$112.9 \times 1.0 = 112.9$ KVM
KJELLERPLAN	620		$62.0 \times 0.2 = 12.4$
SUM	BRA 1749 KVM	SUM	BA 125 KVM

Godkjent. Skjeborg
3/9 1985. Sam. 478,85

MOELVEN SEKSJONSHUS TYPE : MK.410.07-P-MOD
BYGGERRE : KJUT KLEVEN, SYVERSTAD, 1745 SKJEBERG
BYGGEPLASS : SYVERSTAD, 1745 SKJEBERG

PLANER
OG SNITT

ERSTATNING FOR

ERSTATNET AV

TEGN.	DATO 850801	M=	MOELVEN	A/S MOELVEN BRUG 2391 MOELV TELEFON (065) 68000	NR. 2.19465-1	REV.
KONF	GODKJ.	1 : 100				