



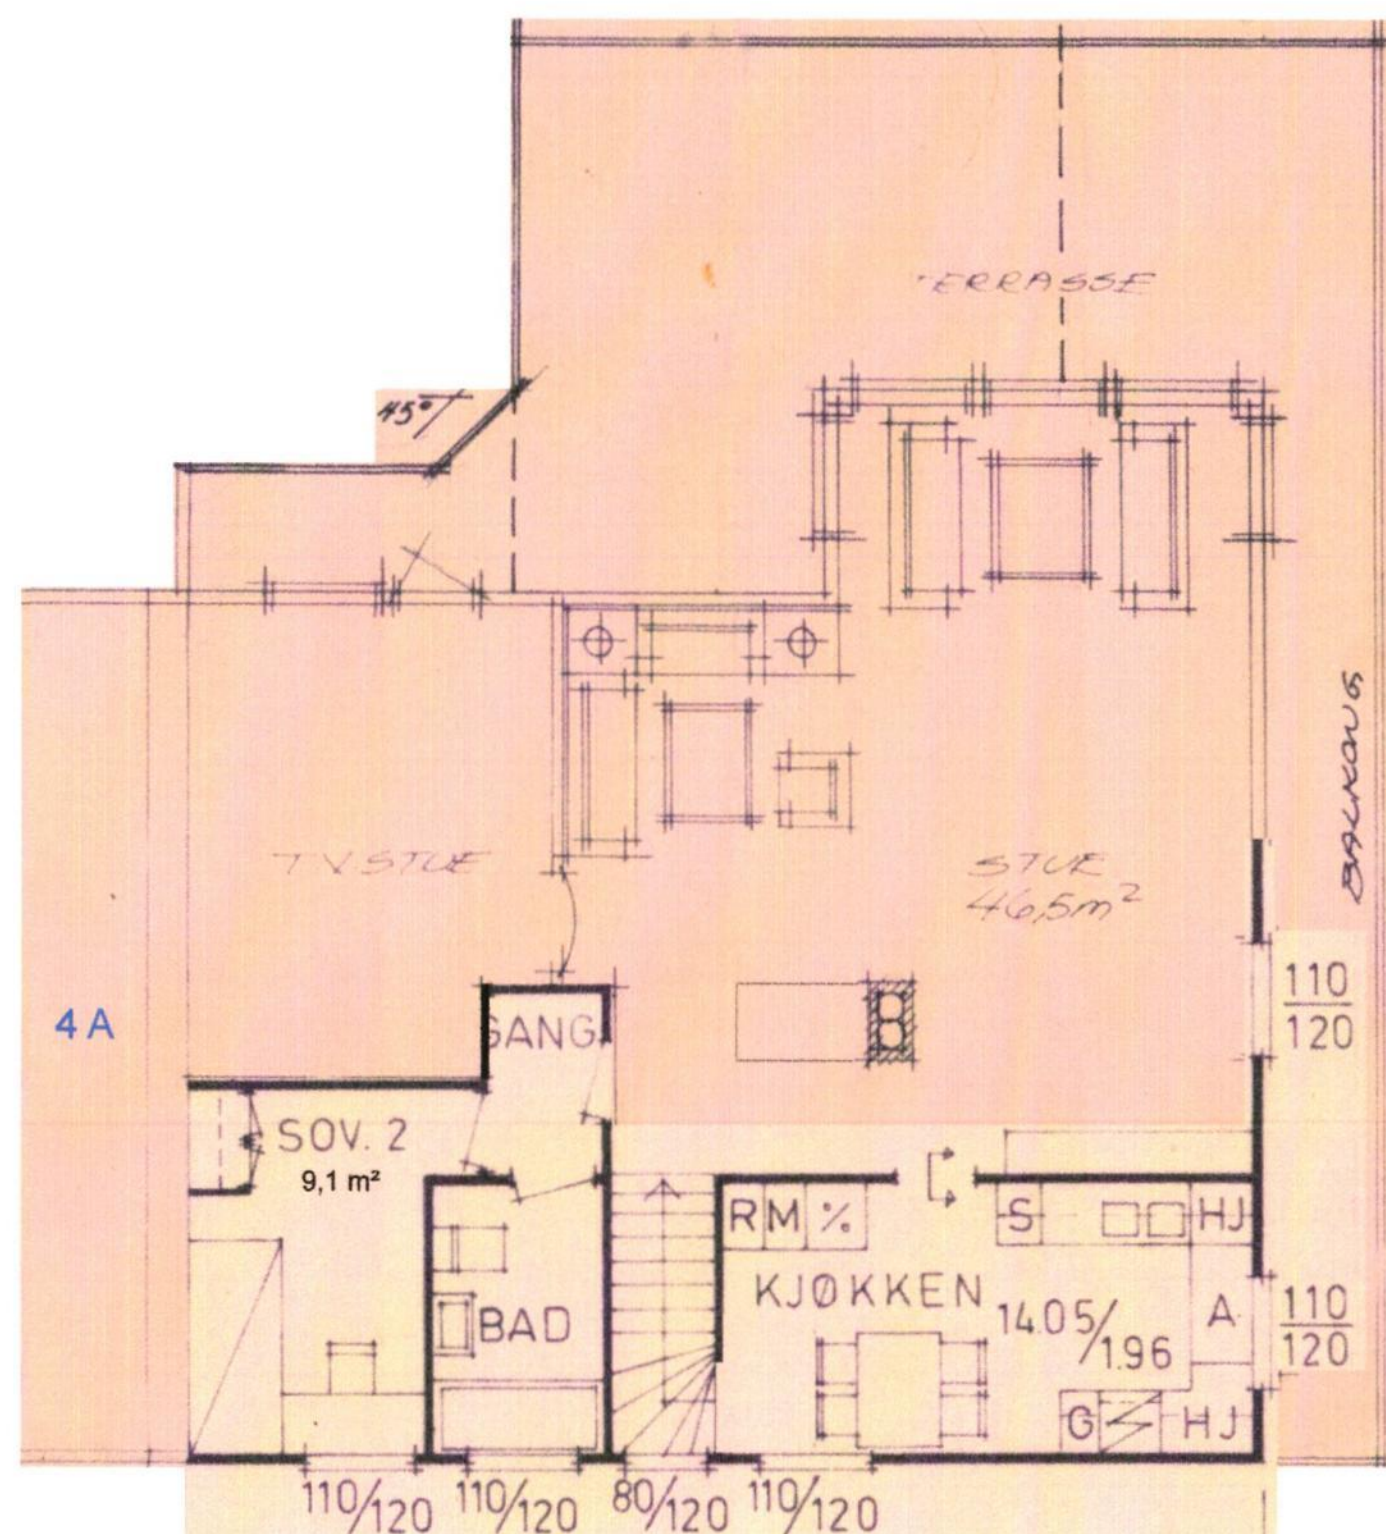

Plan 1. Etasje 1:100

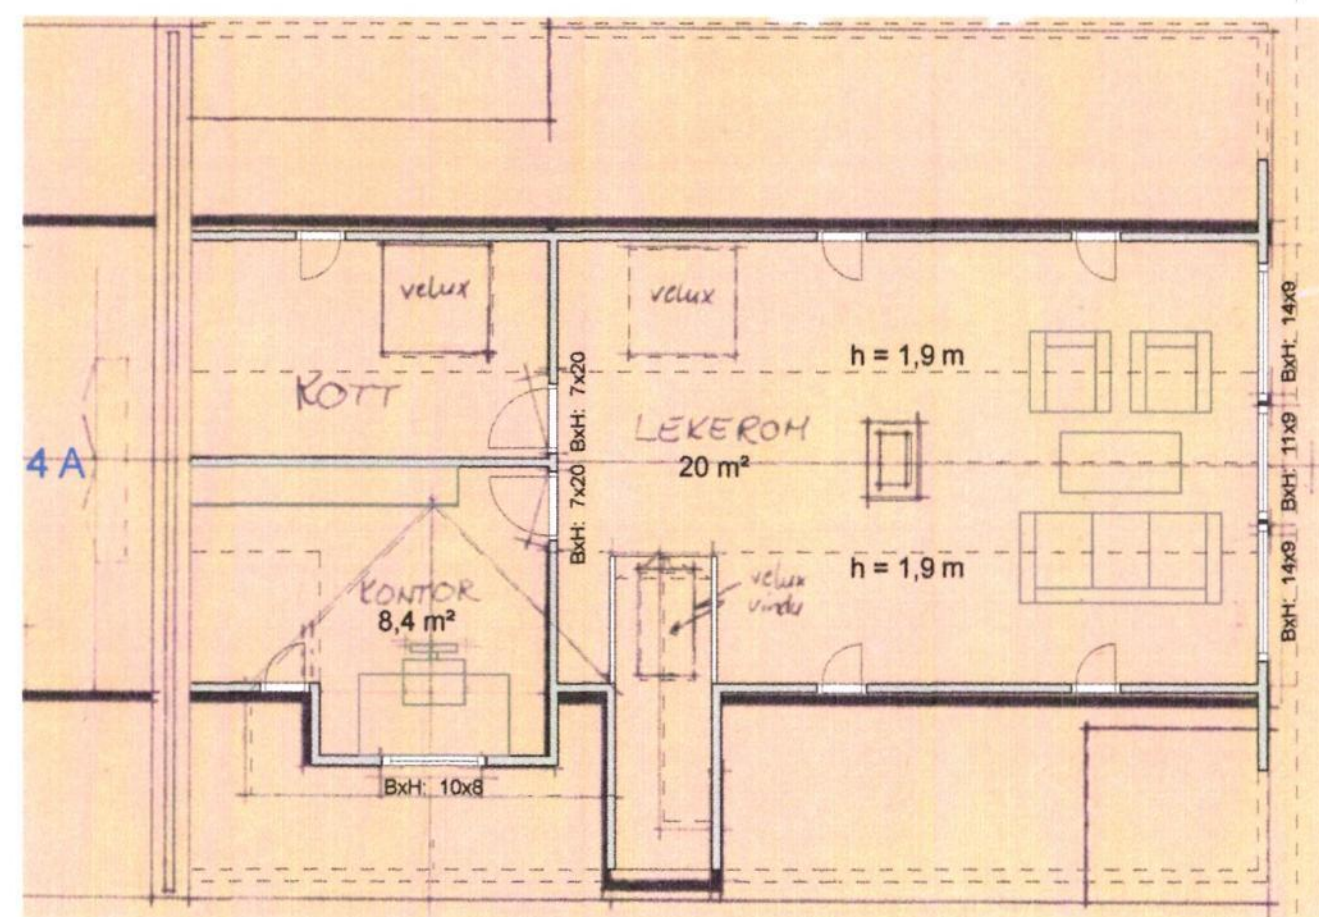


Plan Loft 1:100

BYA:
 BYA Bolig = 126,2 m²
 BYA Dobbelt-garasje = 48,1 m²
Total BYA = 174,3 m²

Arealberegninger	Bruksareal BRA i m²	
i hht. NS 3940	Pr. Etasje	Sum BRA
Loft:	35,1 m²	35,1 m²
1. etg. plan:	97,3 m²	97,3 m²
Underetg. plan inkl Dobbelt Garasje:	155,9 m²	155,9 m²
Total BRA	= 288,3 m²	288,3 m²

 BRUKSENDRE

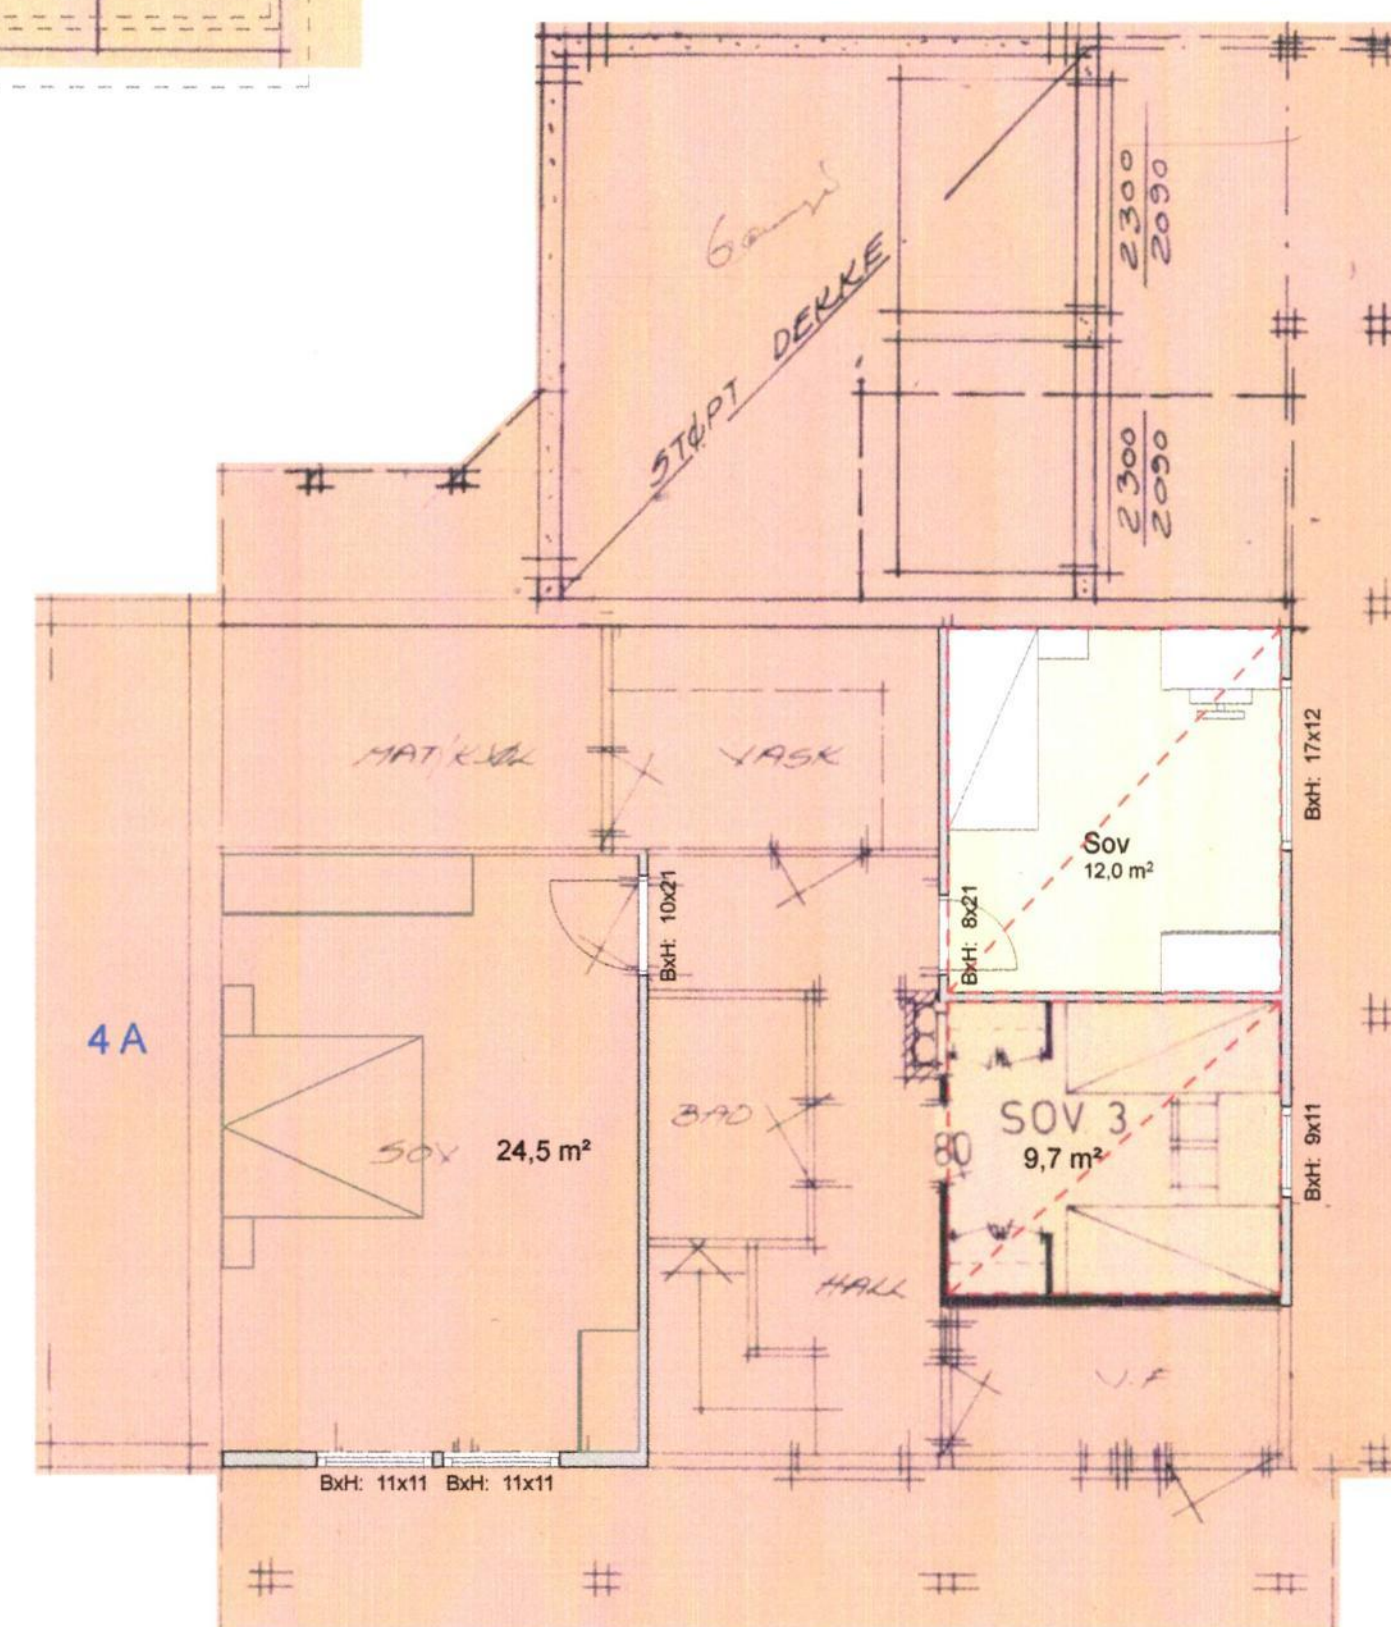

Plan Underetasje 1:100

Prosjekt:
SKOLEVEIEN 4B, 4328 SANDNES

Tegning:
Planer

Fase: **SKISSEPROSJEKT**
 Målestokk: 1:100
 Tegningsnr.: A20-01
 Dato: 05.12.23

FLYT ARKITEKTUR AS

© Alle rettigheter tilhører utførende for prosjekteringen, kopiering eller bruk av disse tegningene er forbudt uten skriftlig samtykke

Tiltakshaver:
 Åse Tansø
 Skoleveien 4B, 4328 Sandnes
 Mob: 476 41 983
 aasetanso@gmail.com

Prosjekterende:
 FLYT Arkitektur AS v/ Gro Tansø
 Langgt. 19, 3. etg., 4306 Sandnes
 Tlf: 971 53 703
 post@flytarkitektur.no