


Eiendom: 111/795  
Adresse: Slynggata 12  
Dato: 15.12.2023  
Målestokk: 1:500

Area =  $522 \text{ m}^2$

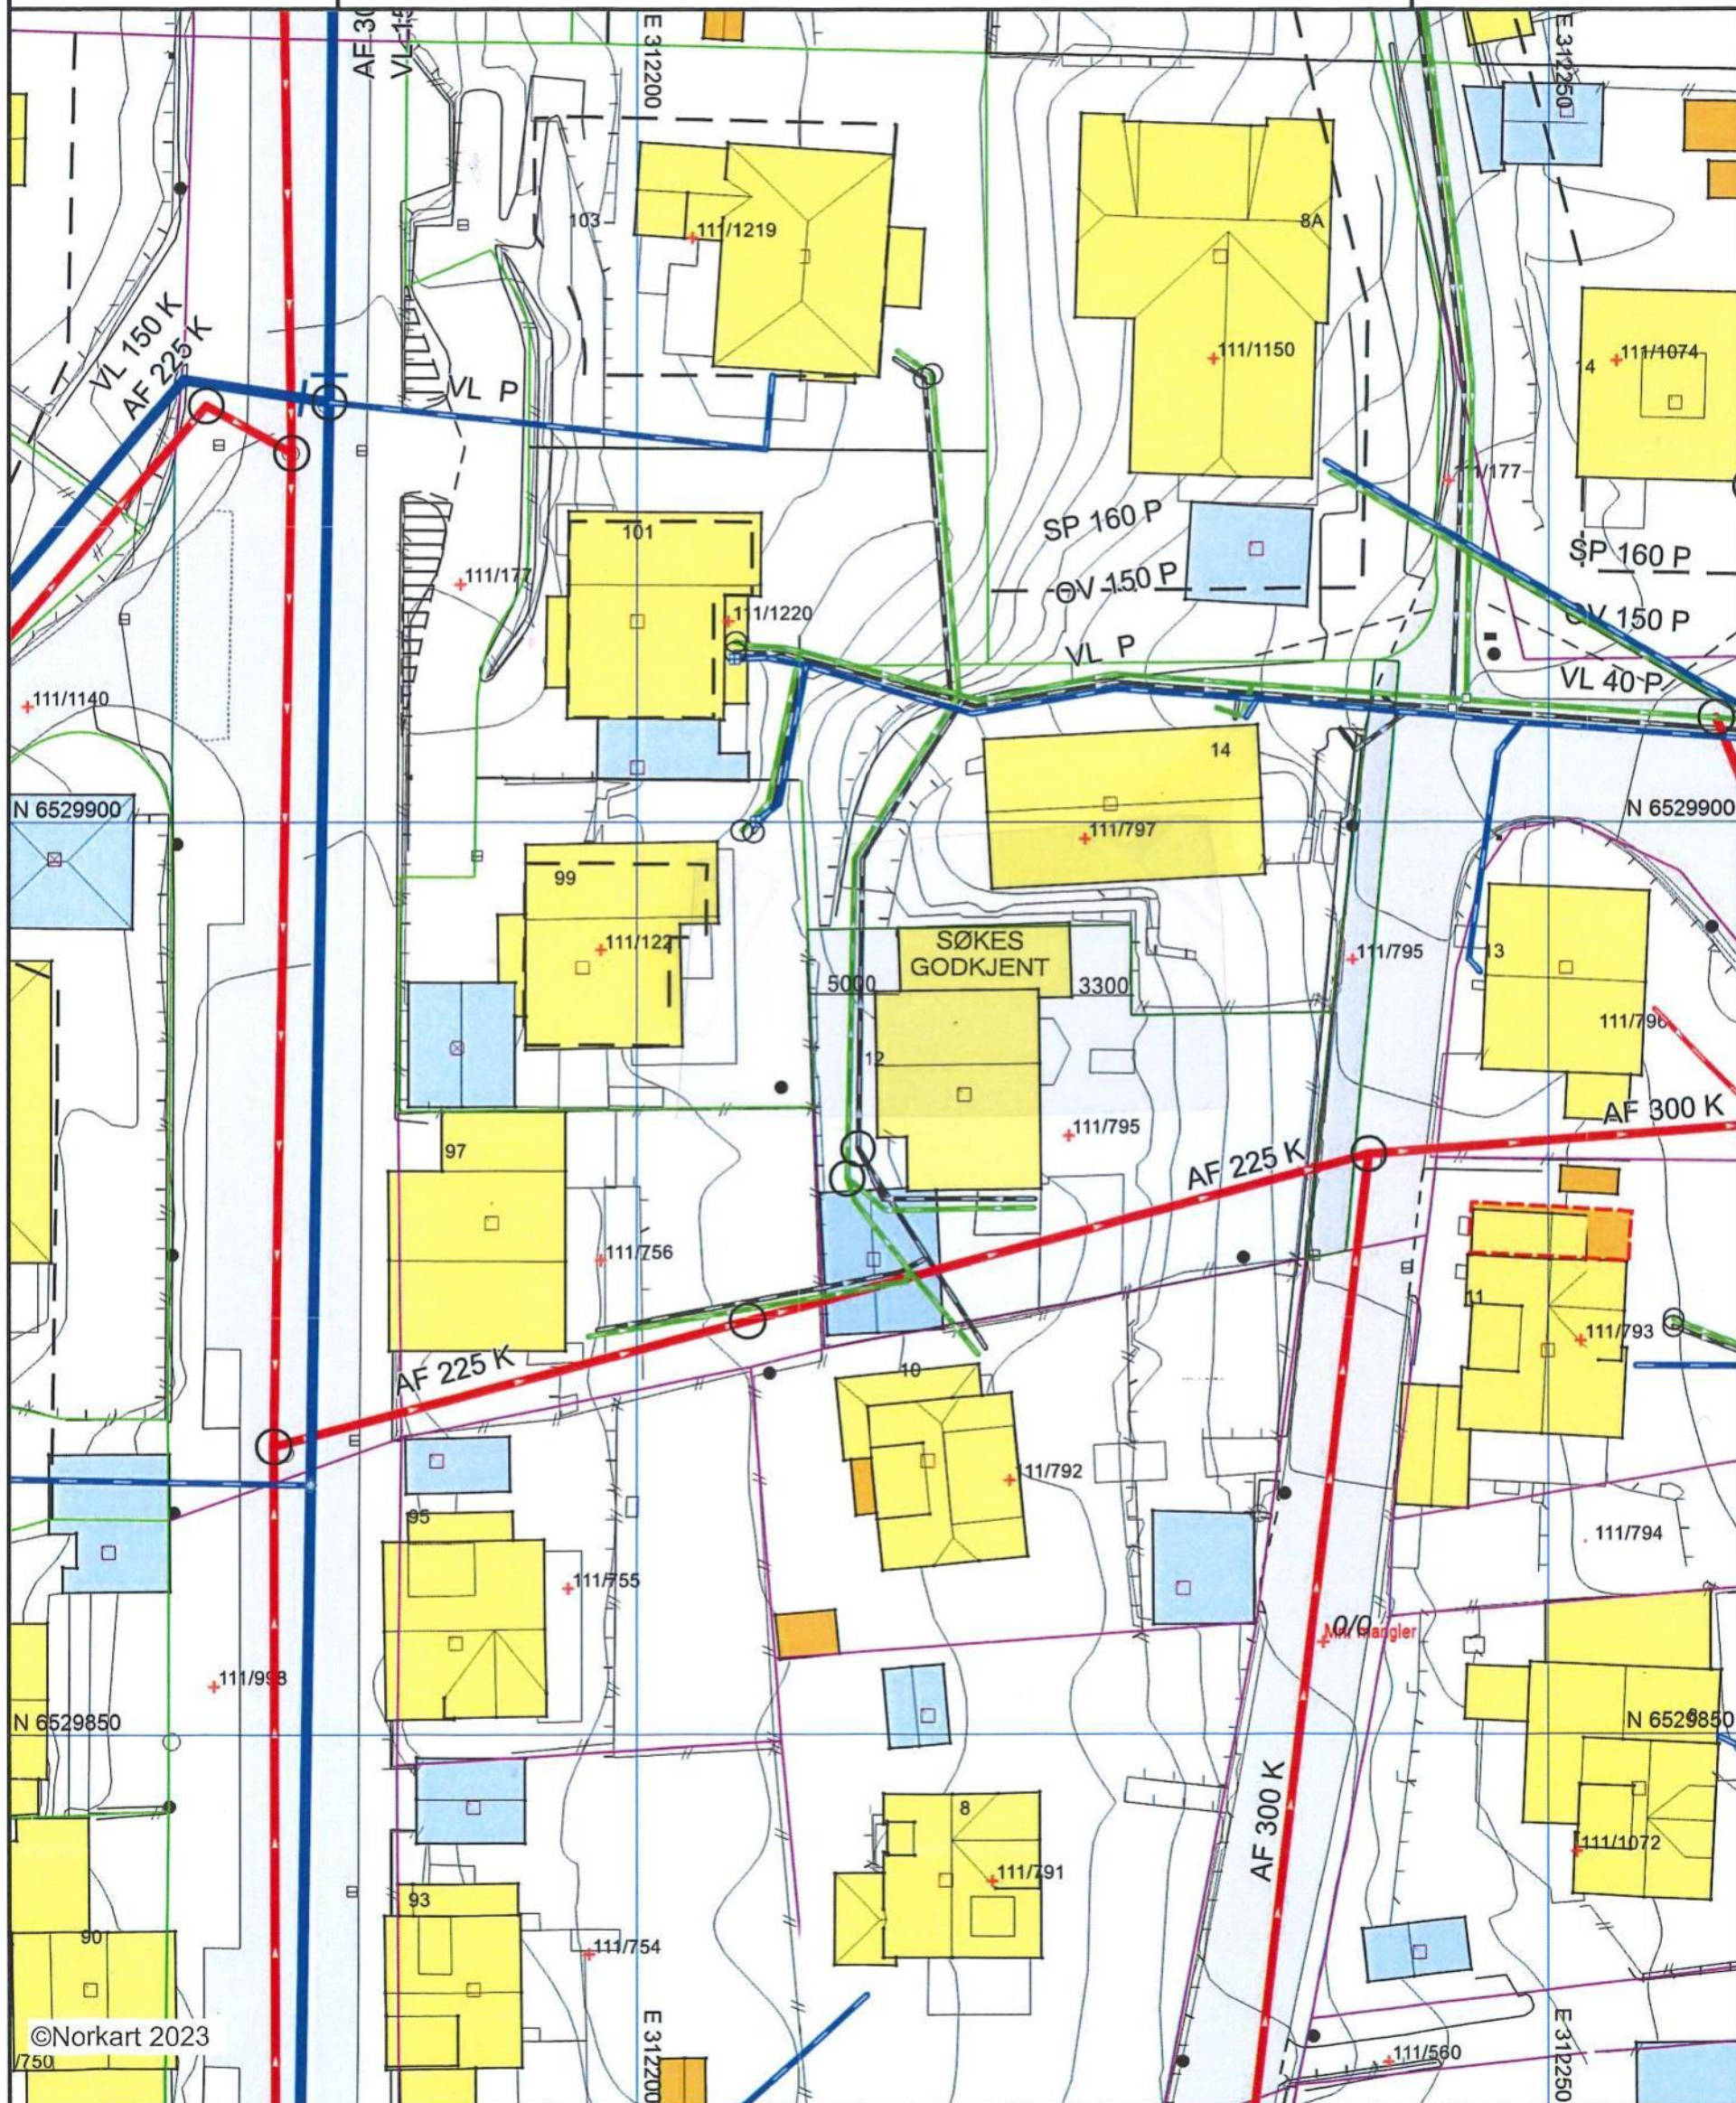

UTM-32



- 1) Det tas forbehold om feil i kartgrunnlaget  
2) Ved utskrift fra PDF-fil kan målestokken bli unøyaktig