


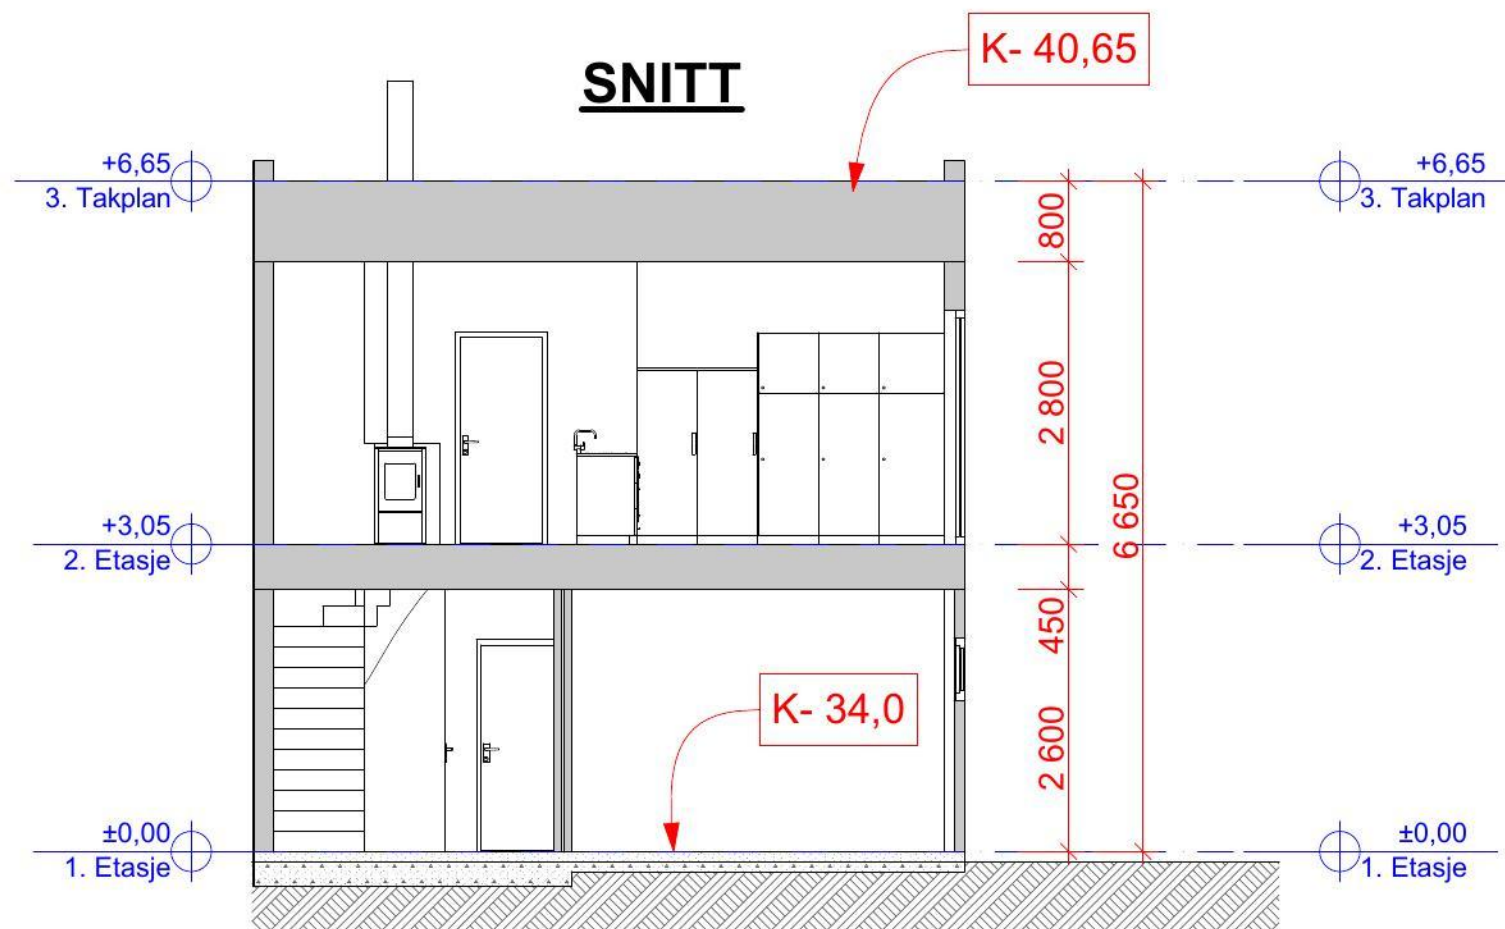

Tomten er ferdig planert

Tegningsnr.: A30-01		Revisjon nr.:	
Type tegning: Snitt			
Index	Dato	Beskrivelse	Sign Kontr.
ARKICON AS Arkitekttjeneste, byggrådgivning, prosjektering, byggesøknader, uavhengig kontroll og byggeledelse Besøksadresse: Kjøita 37, 4. etg Postadr: Kjøita 37, 4630 Kristiansand Knut Ove Kristiansen Tlf: 916 84 510 Mail: knut.ove@arkiconas.no			
Prosjekteringsgruppen:			
☒ ARK : Knut Ove Kristiansen Tlf. 916 84 510 ☐ RIB : Rådg. ing. Bygg veien 0 0000 Stedet Tlf. 00 00 00 00 Fax. 00 00 00 00 ☐ RIE : Rådg. ing. Elektro veien 0 0000 Stedet Tlf. 00 00 00 00 Fax. 00 00 00 00 ☐ RIV : Rådg. ing. Vent. veien 0 0000 Stedet Tlf. 00 00 00 00 Fax. 00 00 00 00			
Fase: Søknadstegninger			
Gnr: 37 Bnr: 1040			
Tittel: Krag Bolig AS Enebolig med garasje Soleieveien 46 Postnr Kristiansand		Godkjent:	
		Kontroll prosjekt	
		Sign.:	Kontroll:
		Filnavn: Soleieveien 46 V3.pln	
		Dato: 27.02.2023	
		Målestokk: 1:100	
		Kontroll utførende	
		Sign.:	Kontroll:
Prosjektnr.: Prosjektnr.		Tegningsnr.: A30-01	
Type tegning: Snitt		Prosjektnr. for prosjekterende/lev	