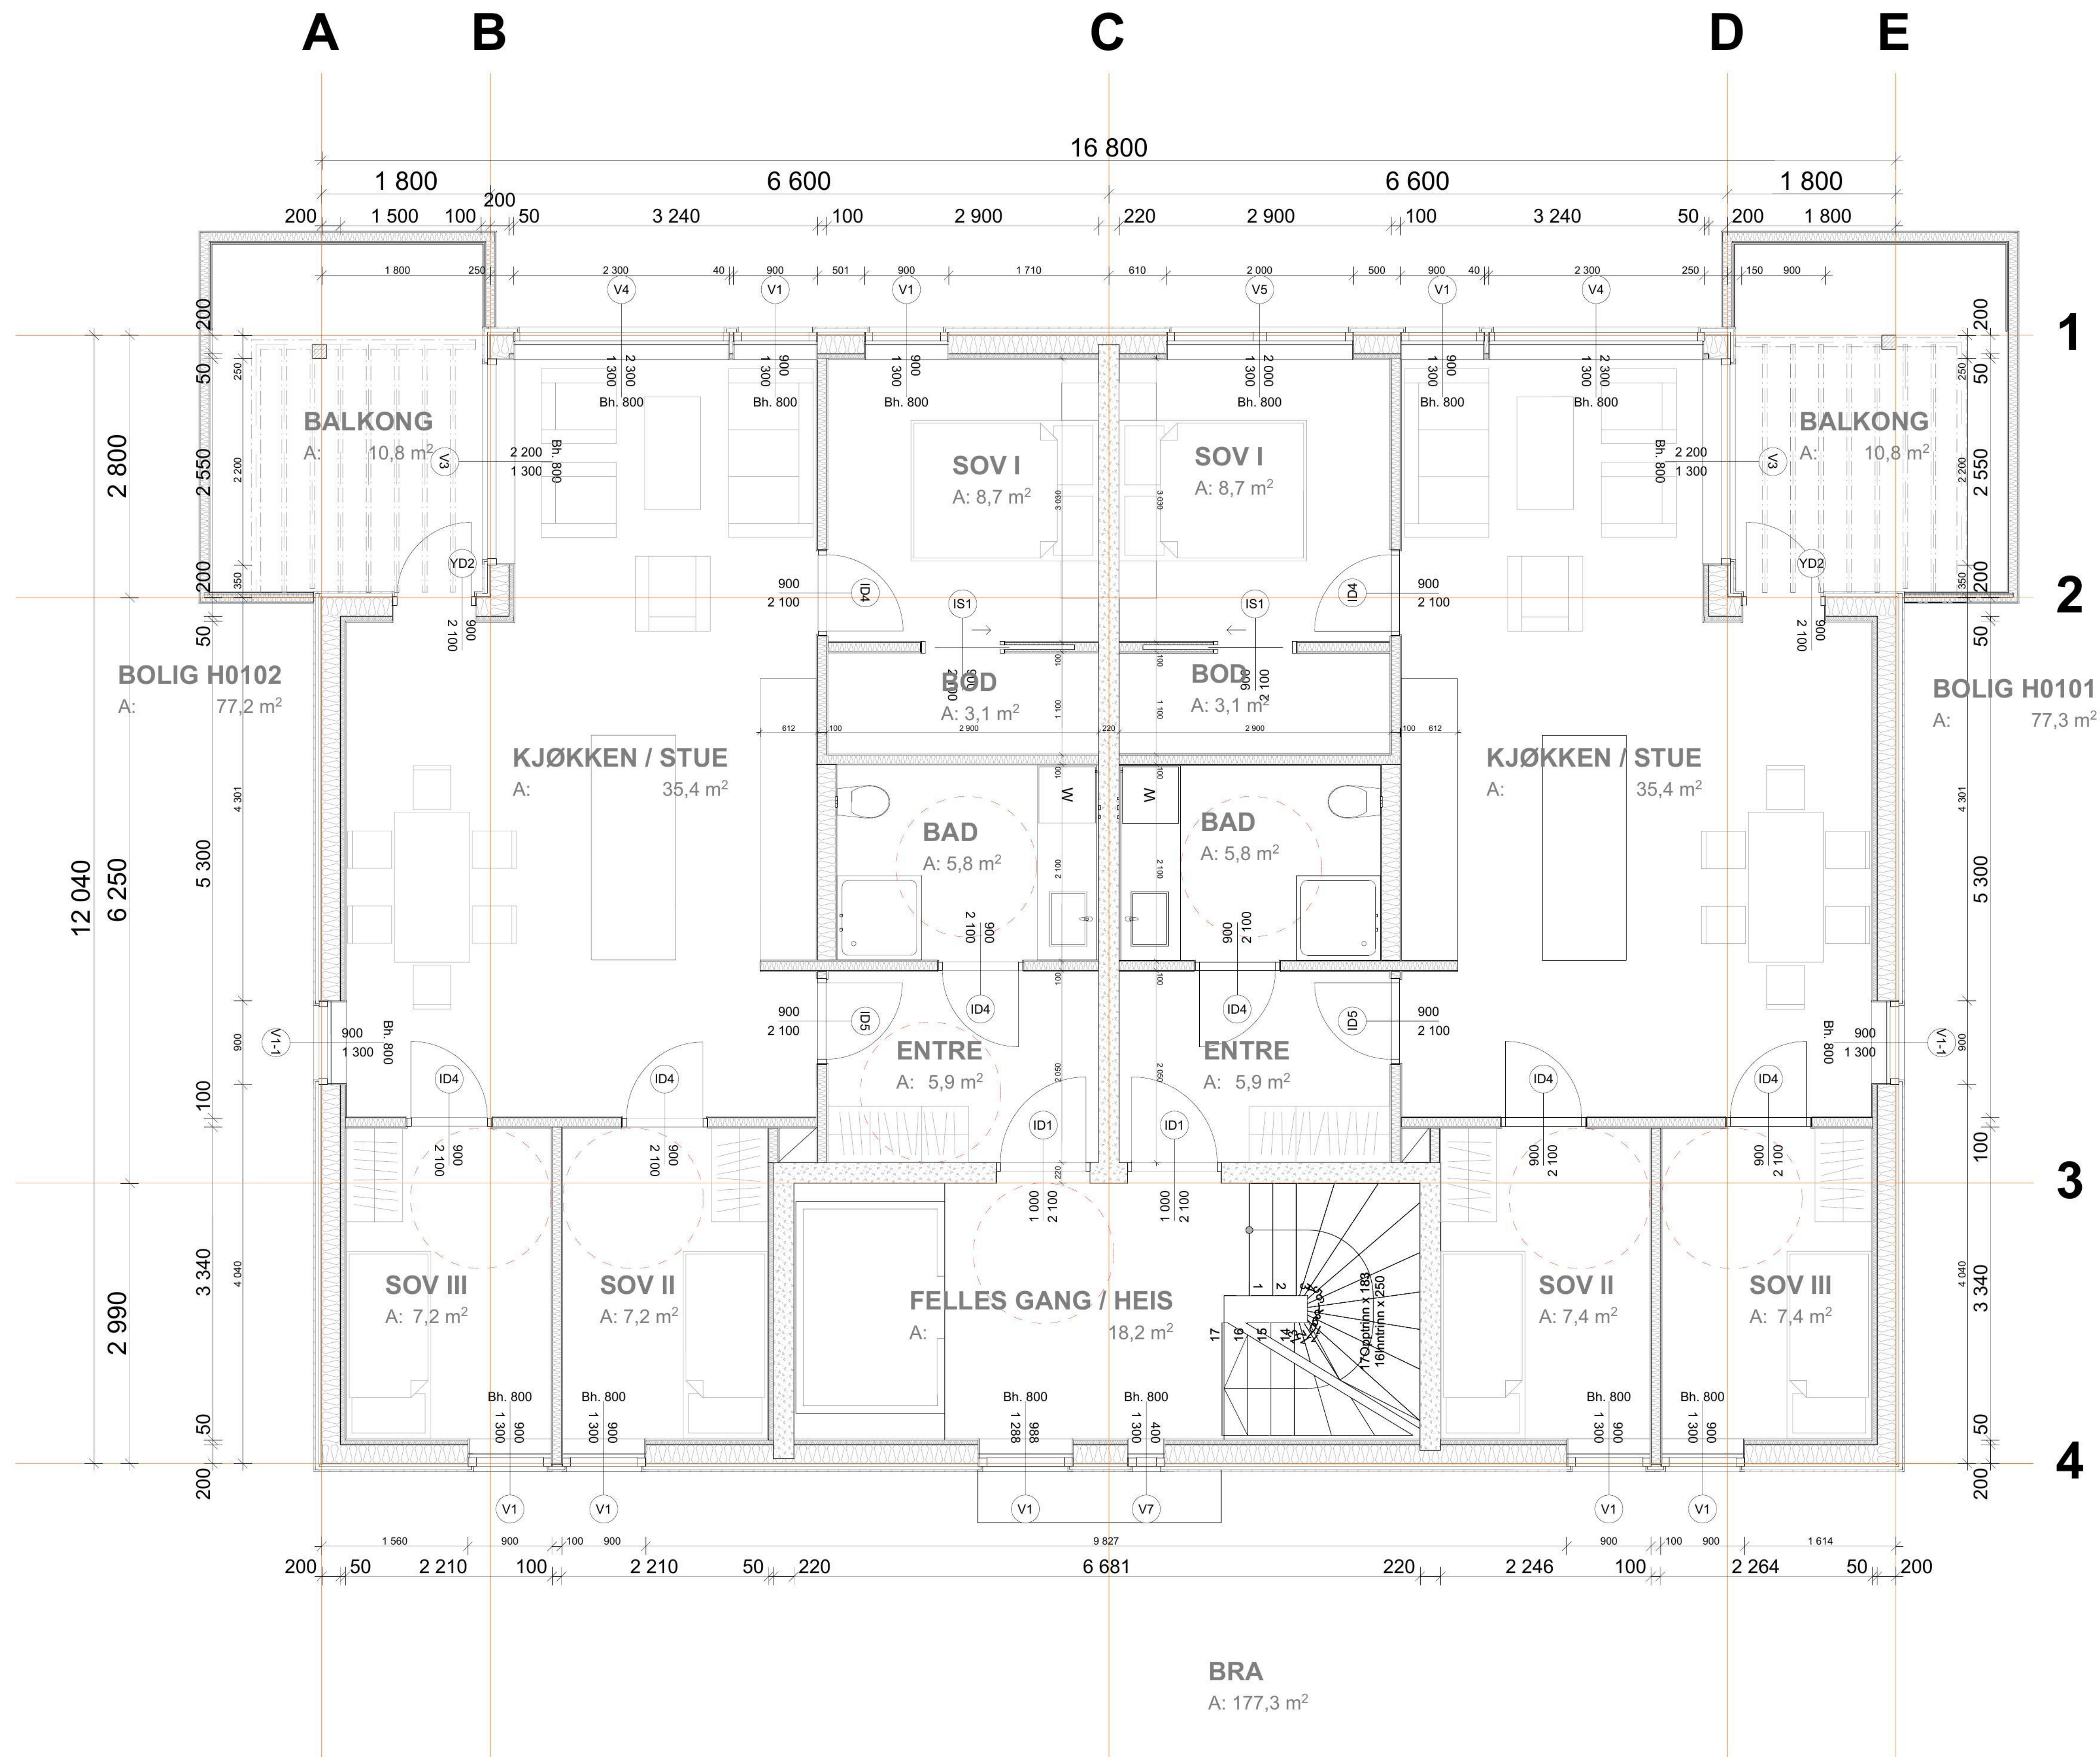


[illegible]

Lokaliseringsfigur:

**Prosjekteringsgruppen:**

- ARK : EGG ARKITEKTUR AS
- Nodeviga 110  
4010 KRISTIANSTAD  
tlf: 03 06 73 33  
e: jao@egg-ark.no
- RIB :
- RIE :
- RIV :

odeviga 18  
510 KRISTIANSTAD  
: 93 06 73 33  
: iso@egg-ark.no

**SØKNAD BYGGETILLATELSE**

**Tittel:**

**SOLEIEVEIEN 63**

Krag Bolig AS

Kjøita 37  
4630 KRISTIANSAND

Prosjektnr.:  
1715

Tegningsnr.:  
ARK.22.02.01

Type tegning:  
**Etasjeplan - 2. etasje**

---

|           |  |
|-----------|--|
| Godkjent: |  |
|-----------|--|

|                   |
|-------------------|
| Kontroll prosjekt |
|-------------------|

|        |           |
|--------|-----------|
| Sign.: | Kontroll: |
|--------|-----------|

|      |  |
|------|--|
| ja ø |  |
|------|--|

Filnavn: 4346

1715  
Soleie63\_20230315.pl

**Dato:** \_\_\_\_\_

15.06.2023

Målestokk:  
1:50

|      |                    |
|------|--------------------|
| 1.30 | Kontroll utførende |
|------|--------------------|

|                    |                 |
|--------------------|-----------------|
| Kontroll utførende |                 |
| Sign.: _____       | Kontroll: _____ |

| Sign... | Kontroll... |
|---------|-------------|
|---------|-------------|

|  |  |                |
|--|--|----------------|
|  |  |                |
|  |  | Projektnr. for |

prosjekterende/lev

[illegible]

100