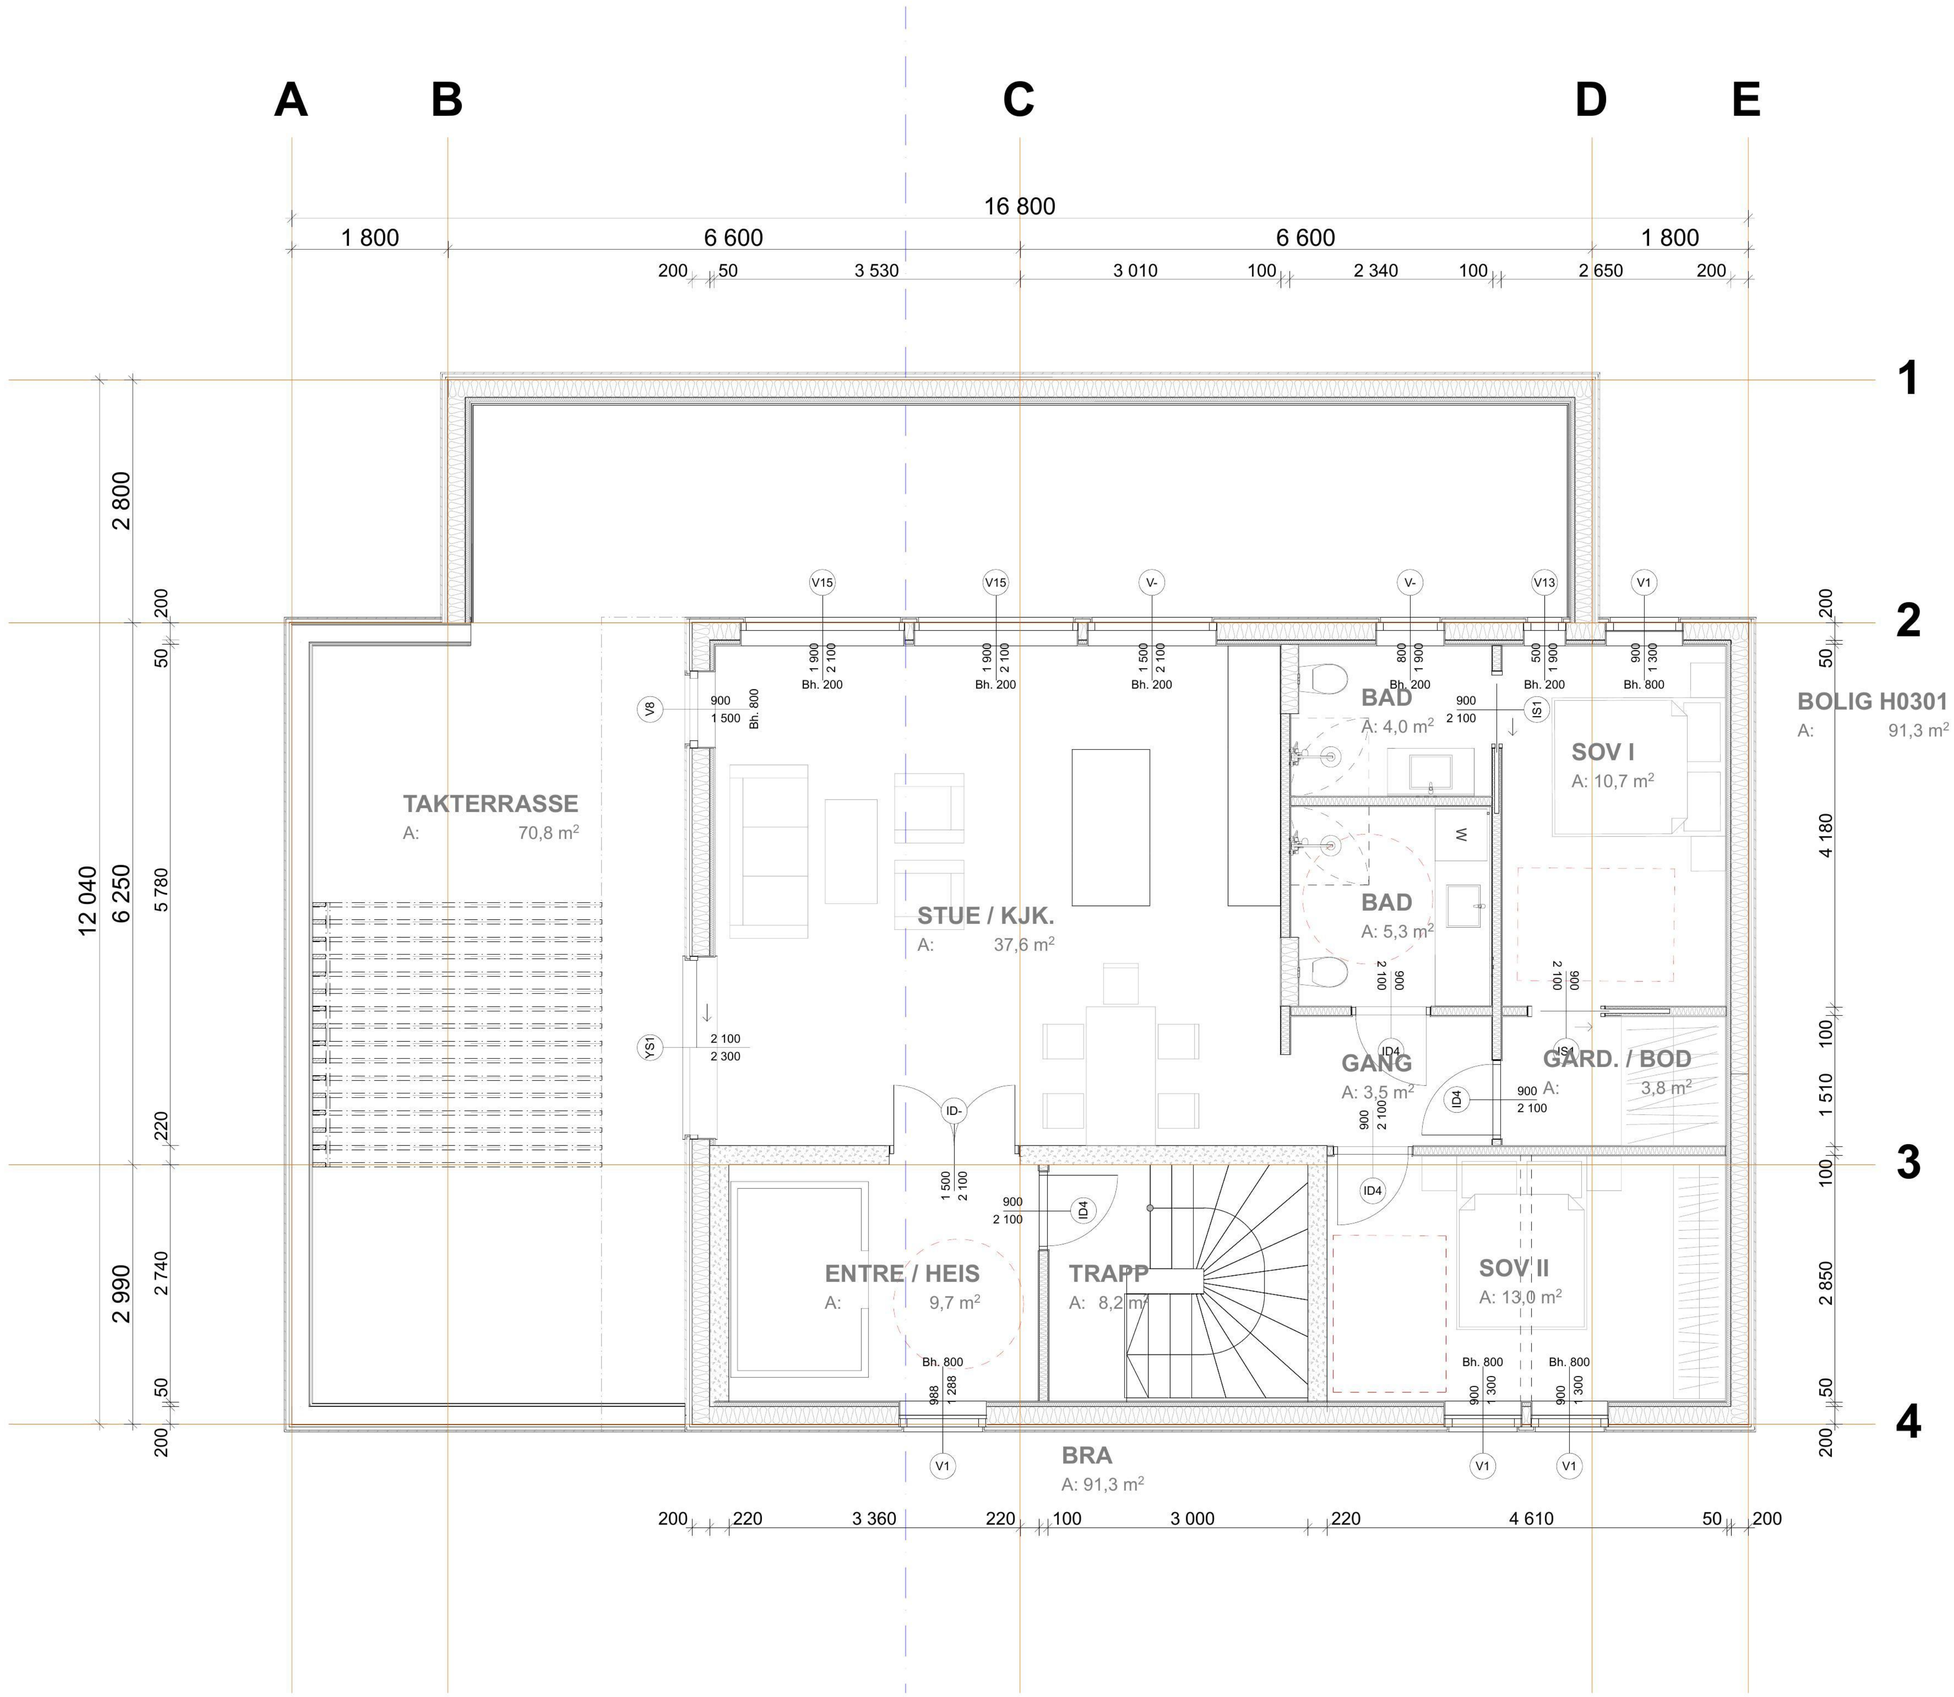


Tegningsnr.: ARK.22.03.01

Revisjon nr.:

Type tegning: **Etasjeplan - 3. etasje**

Index	Dato	Beskrivelse	Sign	Kontr.

Lokaliseringsfigur:

Prosjekteringsgruppen:

ARK : EGG ARKITEKTUR AS
Nodeviga 18
4610 KRISTIANSAND
tlf: 93 06 73 33
e : jao@egg-ark.no

RIB :

RIE :

RIV :

SØKNAD BYGGETILLATELSE

egg arkitektur as

Tittel:

SOLEIEVEIEN 63

KRAG BOLIG AS

Kjøita 37
4630 KRISTIANSAND

Godkjent:

Kontroll prosjekt

Sign.: ja ø | Kontroll:

Filnavn: 1715 Soleie63_20230315.pln

Dato: **15.06.2023**

Målestokk: **1:50**

Kontroll utførende

Sign.: | Kontroll:

Prosjektnr.: 1715

Tegningsnr.: ARK.22.03.01

Prosjektnr. for prosjekterende/lev

Type tegning: **Etasjeplan - 3. etasje**