


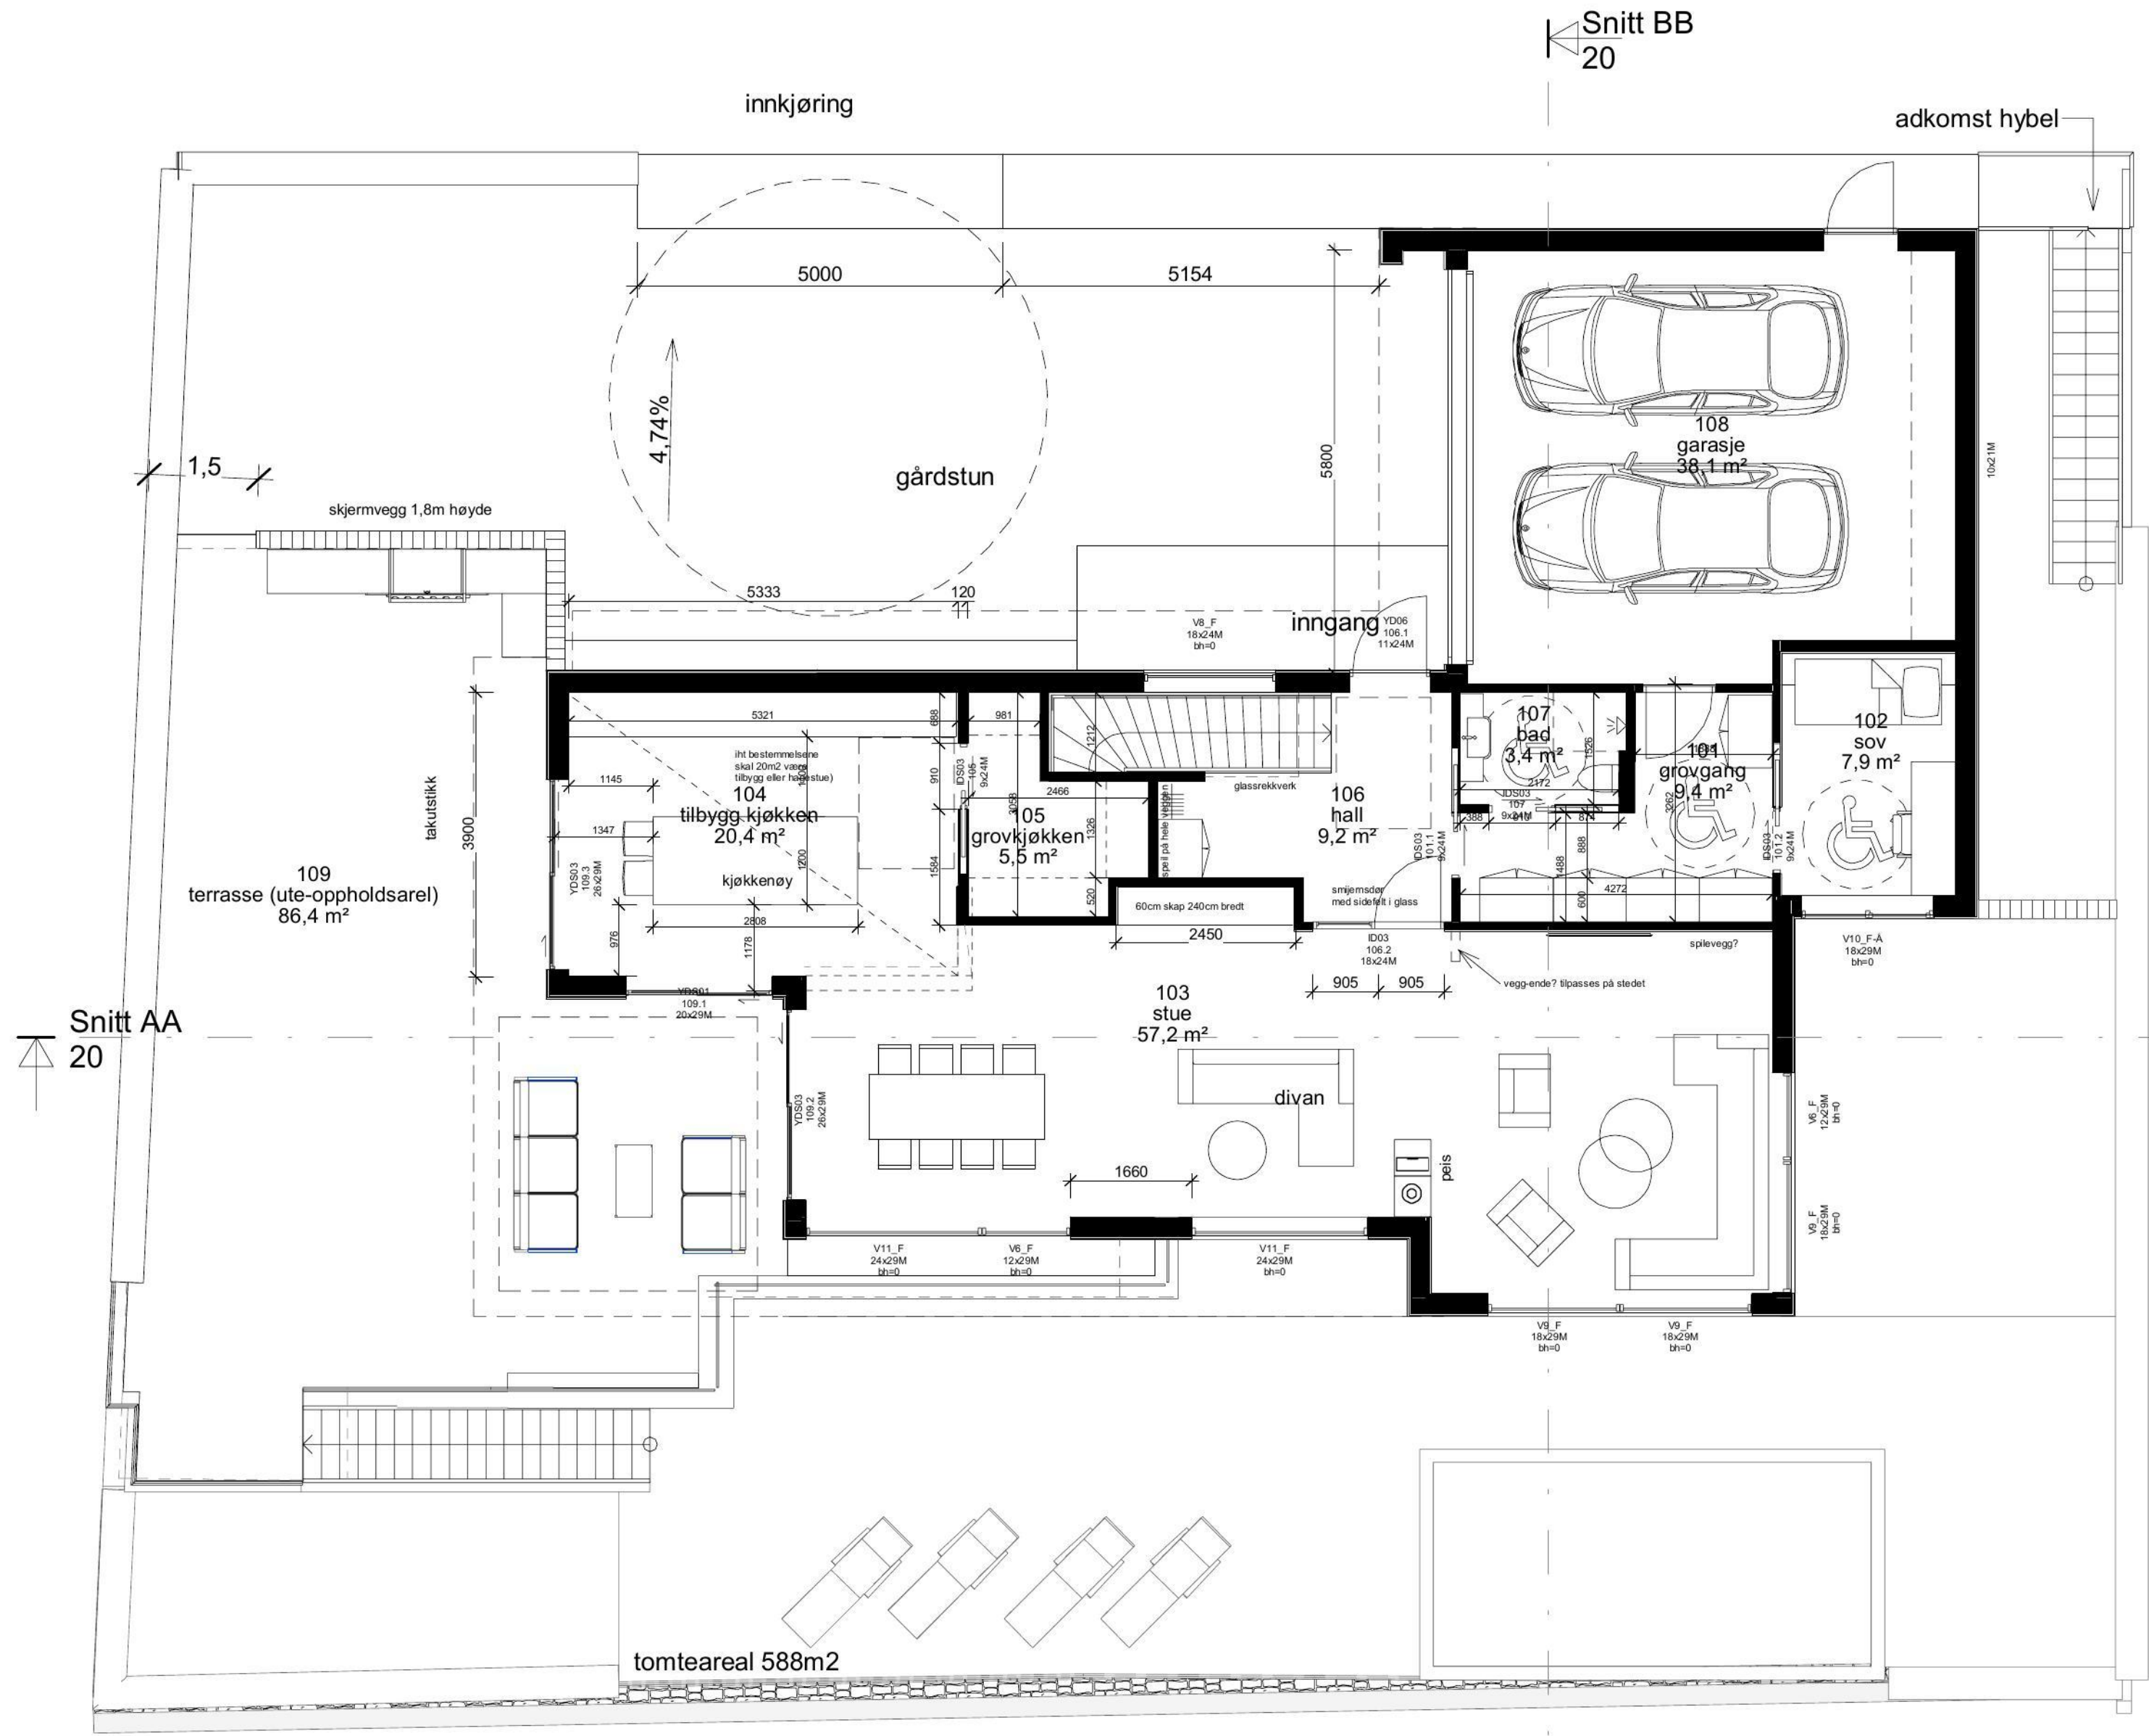

Bebygd areal (BYA)		
Etasje	Navn	Areal

Et. 1	BYA 1.etasje	179 m²
Grand total: 1		

Bruksareal (BRA)		
Etasje	Navn	Areal

Et. 1	BRA 1.etasje	160,5 m²
Et. U f.g	BRA u.etasje	158,9 m²
		319,5 m²

3241

gnr.bnr 37/1179 Spireaveien 62, 4634 Kristiansand S
VILLA SPIREAVEIEN

Plan 1.etasje

11

Tiltakshaver
**Paal Jon Lo og Cathrine
Bratlid**

Prosjektfase
Søknadstegninger

Kontroll dato/sign
KLN

Målestokk
1 : 100 A3

E2
Vedleggsnr.

egøastre