


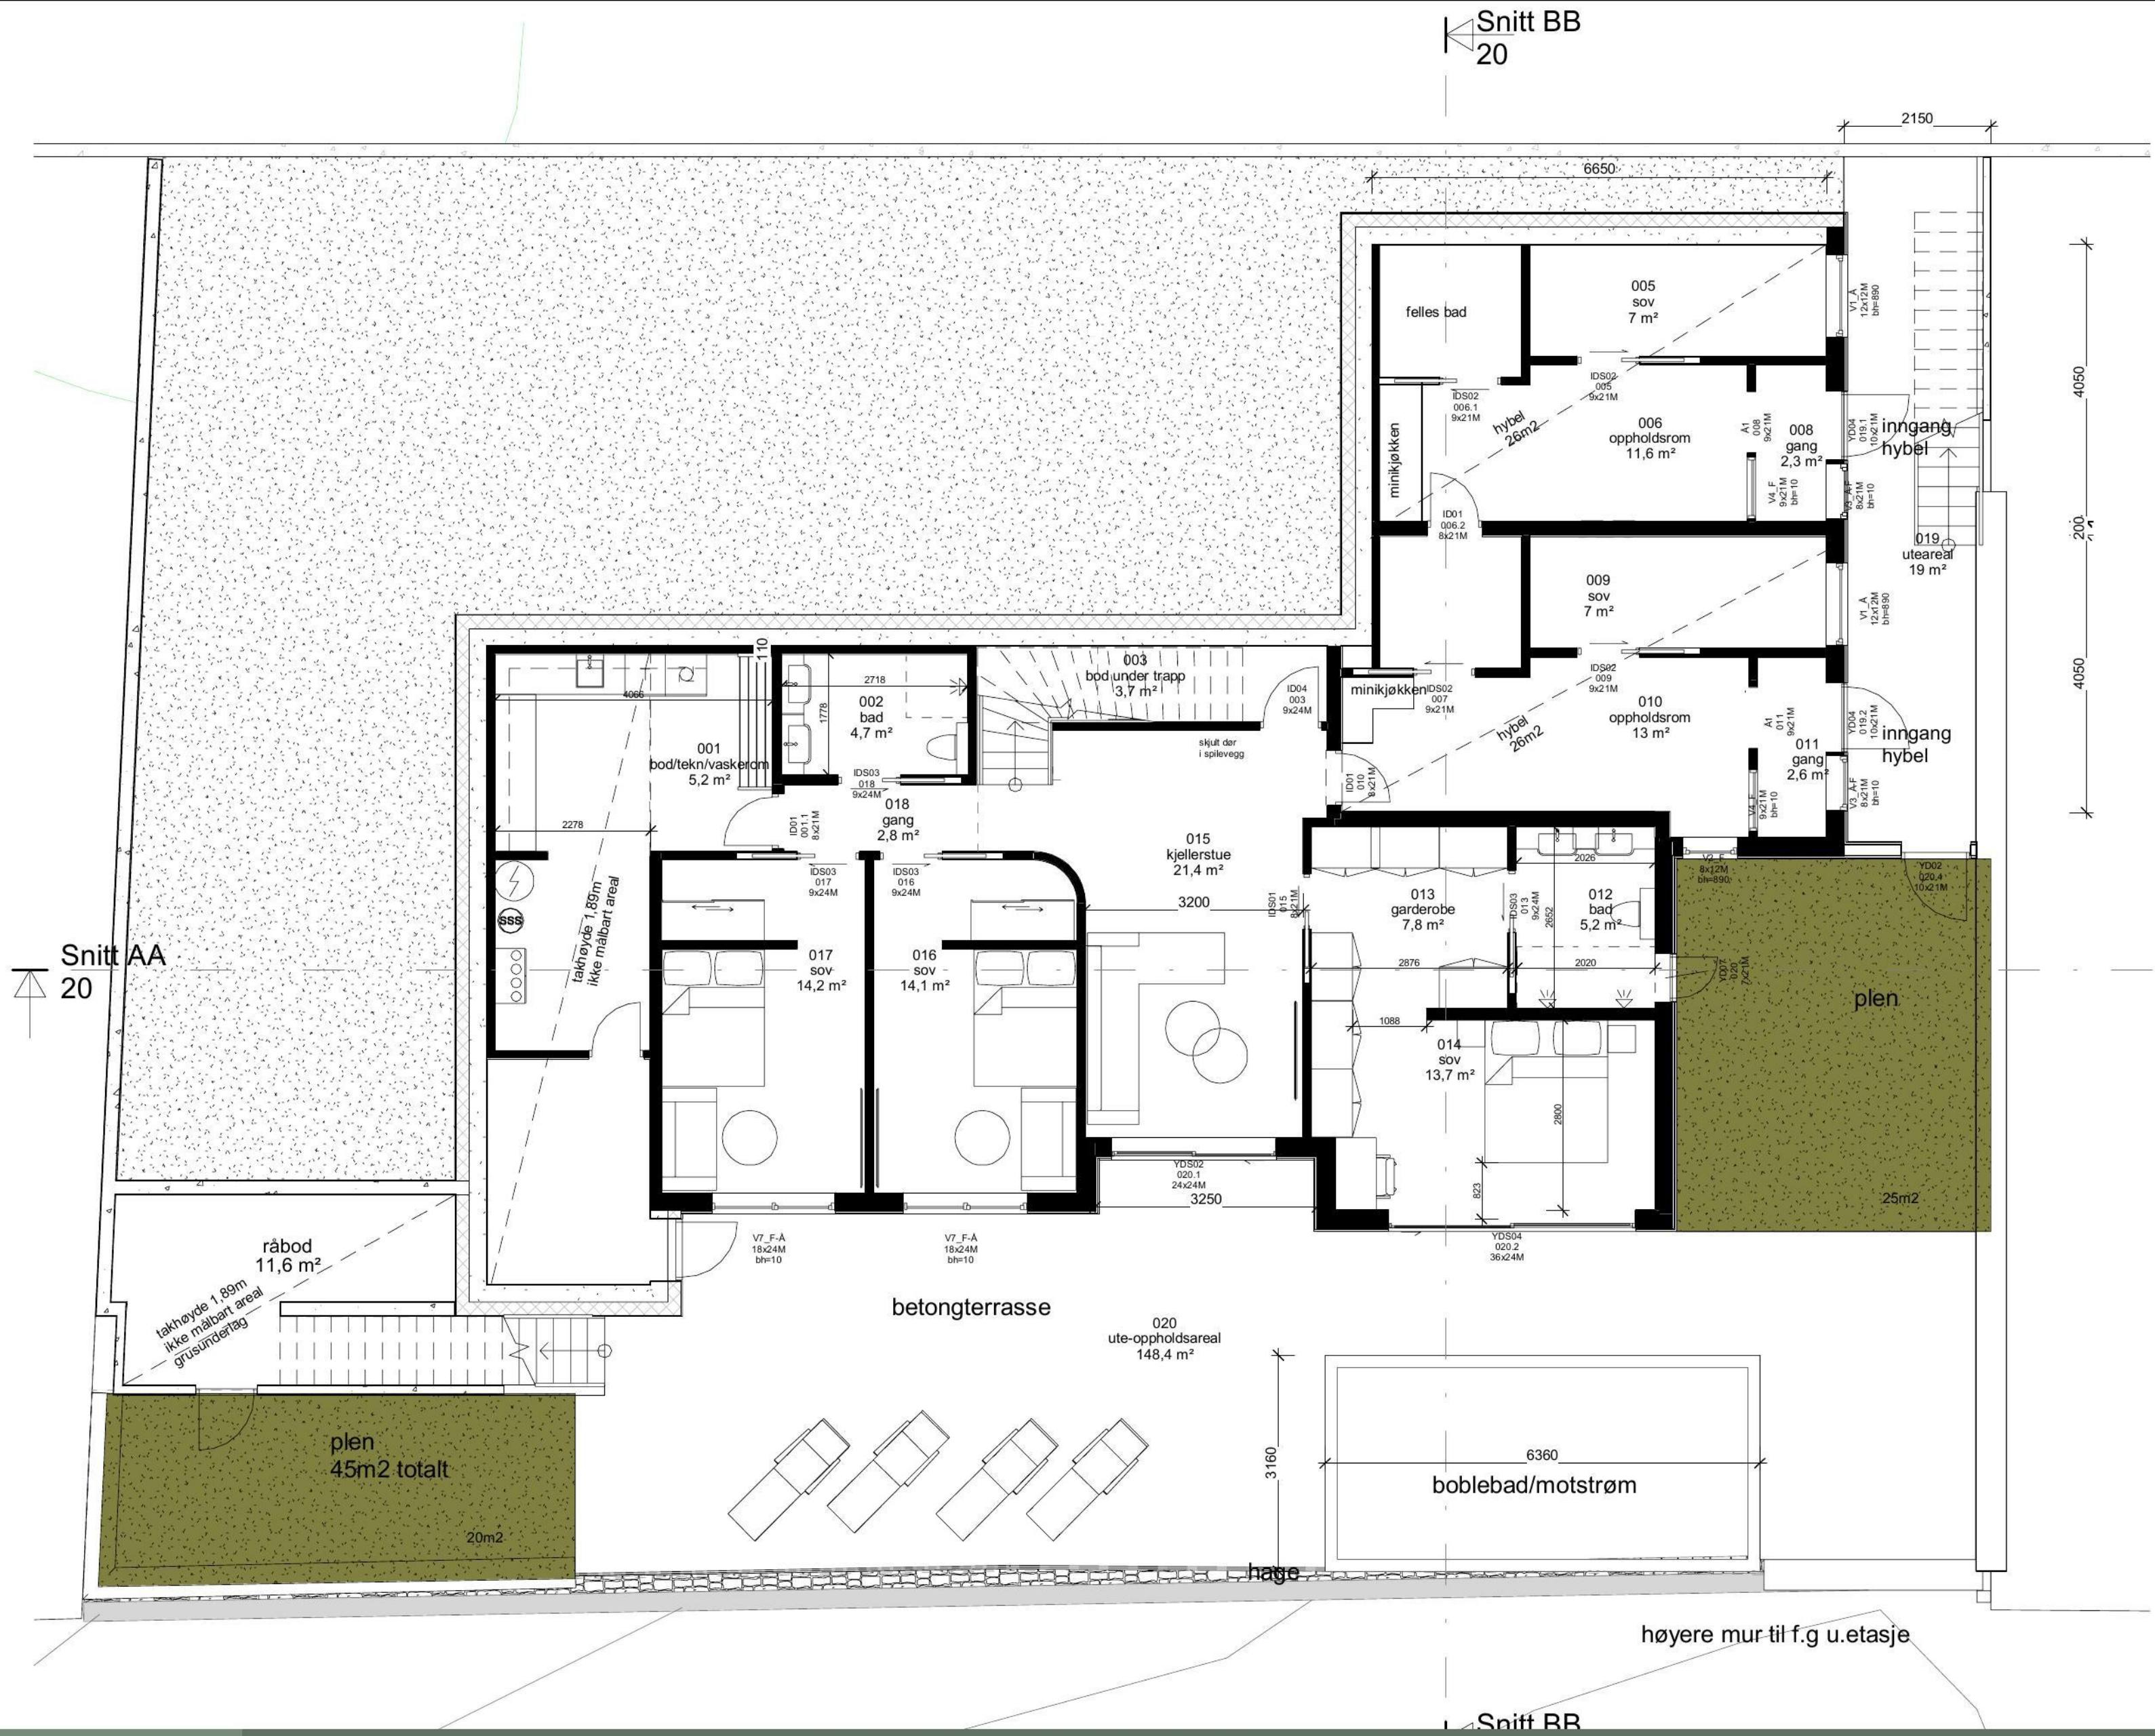

| Bebygd areal (BYA) |      |       |
|--------------------|------|-------|
| Etasje             | Navn | Areal |

|                |              |        |
|----------------|--------------|--------|
| Et. 1          | BYA 1.etasje | 179 m² |
| Grand total: 1 |              |        |

| Bruksareal (BRA) |      |       |
|------------------|------|-------|
| Etasje           | Navn | Areal |

|           |              |          |
|-----------|--------------|----------|
| Et. 1     | BRA 1.etasje | 160,5 m² |
| Et. U f.g | BRA u.etasje | 158,9 m² |
|           |              | 319,5 m² |

Tiltakshaver  
Paal Jon Lo og Cathrine  
Bratlid

Prosjektfase  
Søknadstegninger

Kontroll dato/sign  
KLN

Målestokk  
1 : 100 A3

E1

Vedleggsnr.

Rv Dato Beskrivelse Ut Sgn

3241

Prosjektnr.

gnr.bnr 37/1179 Spireaveien 62, 4634 Kristiansand S

VILLA SPIREAVEIEN

02.10.2023 13:35:53 K:\Prosjekt\3241 Paal Jon Lo - bolig Spireaveien tomt 12\01 Byggesak\06\_Tegninger\02\_Under arbeid\03 Revit\JFC\3241 Villa Spireaveien.rvt

Snitt BB

Plan u.etasje

10

Utarb MB

20.09.23

egøastrek