
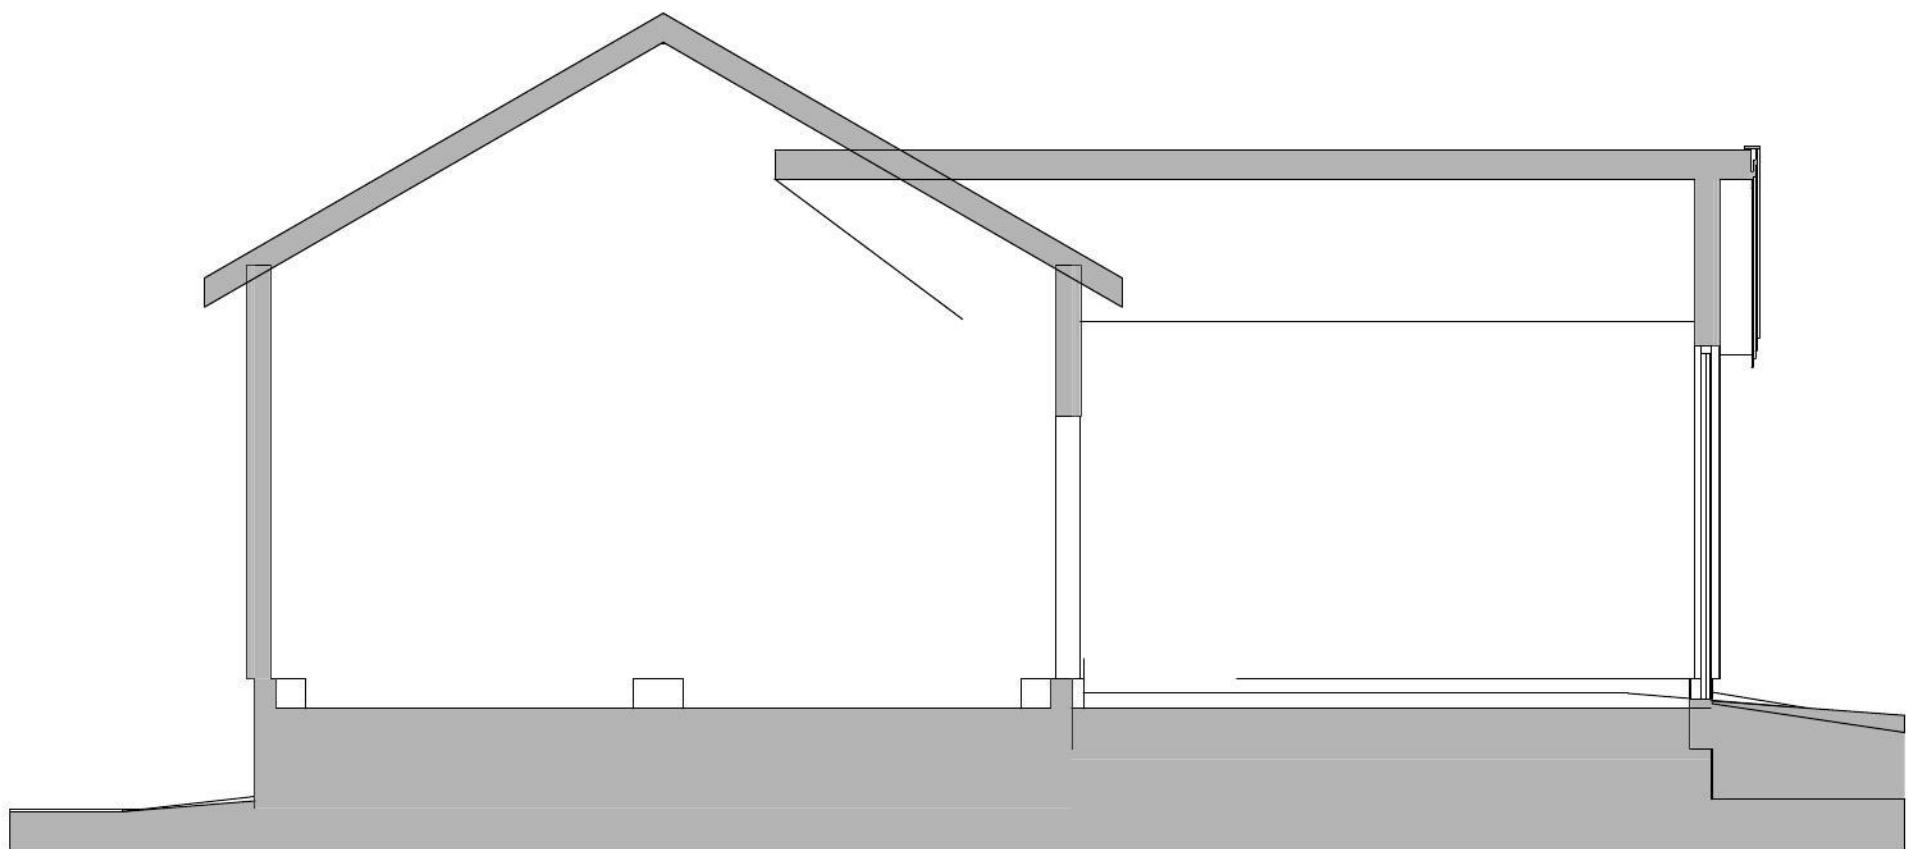


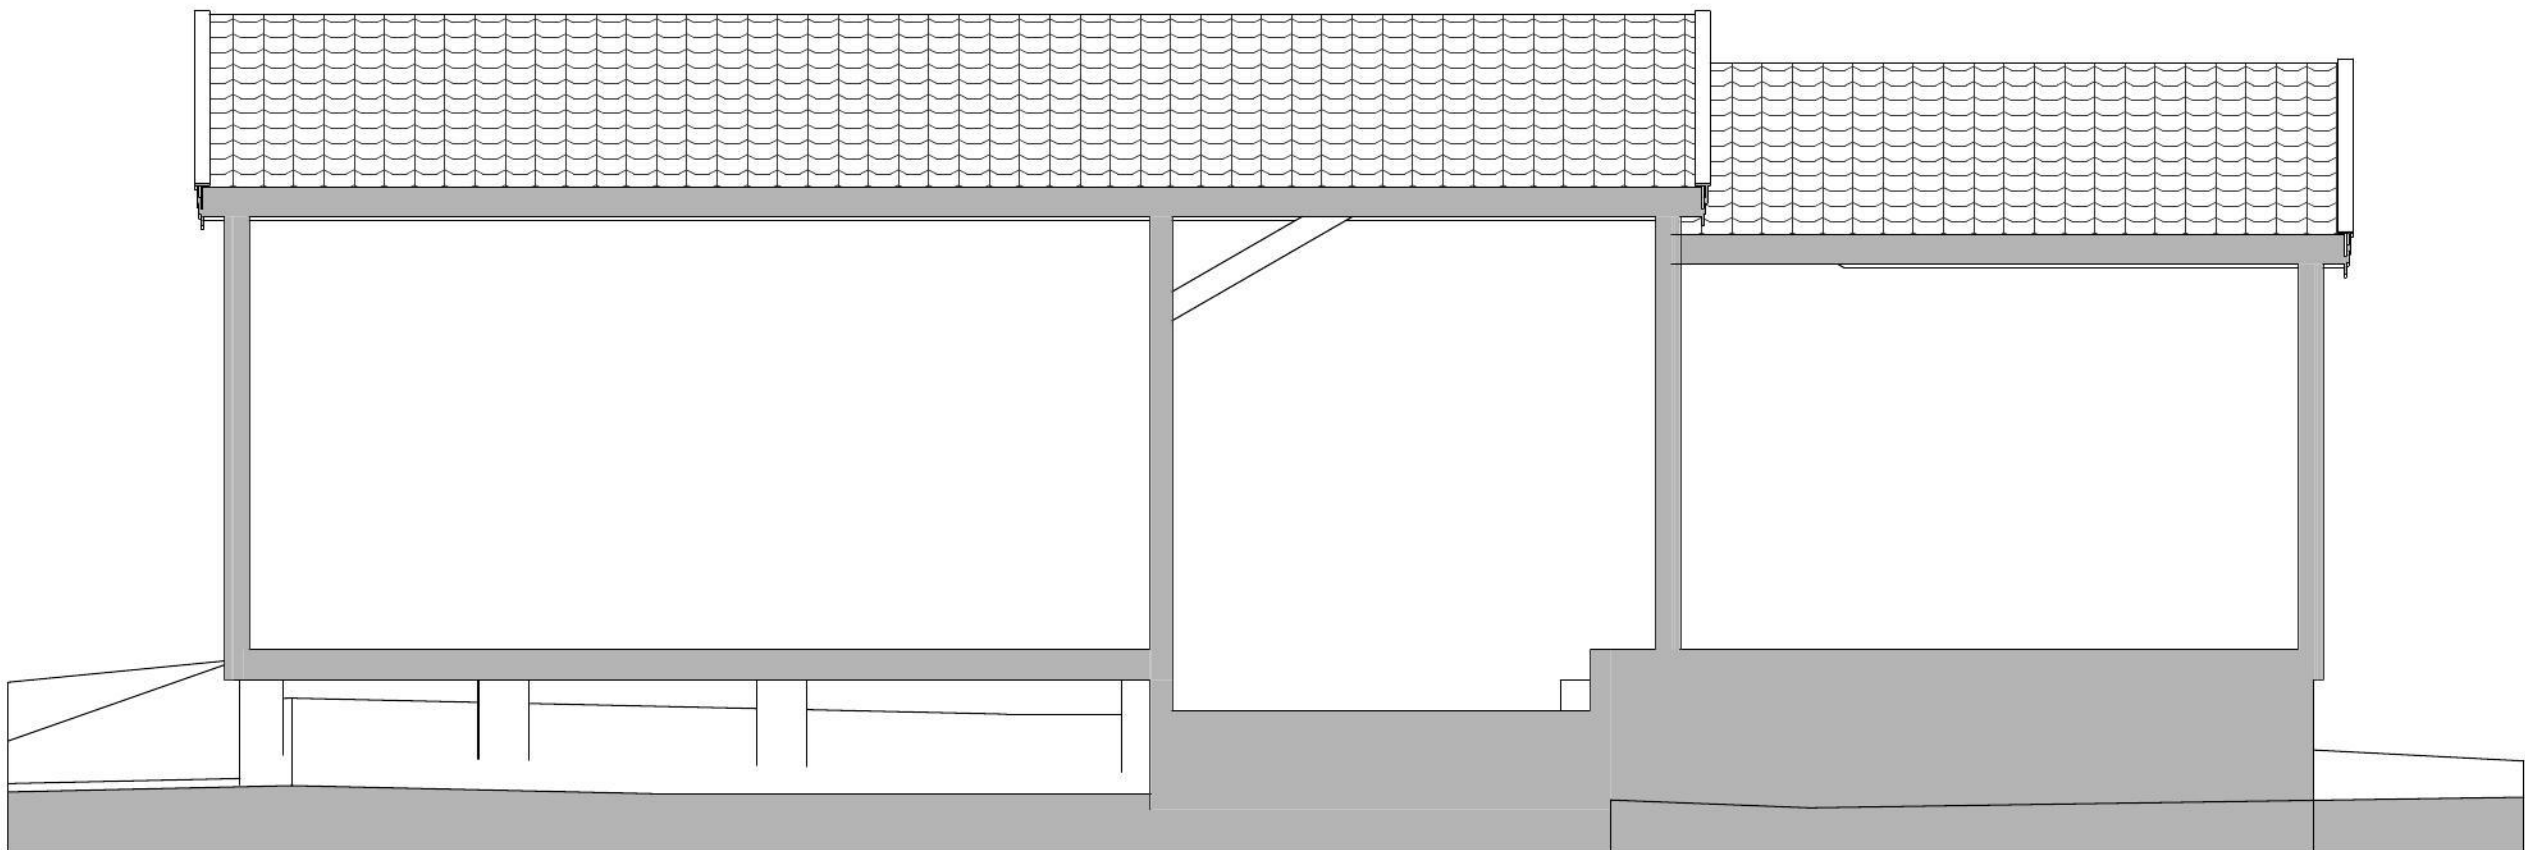

Dato endret:
#

Prosjekt:
Stoltangen 1 låve

Gnr./Bnr.
14/112

Tiltakshaver:
Lasse Ørseng
Stoltangen 1
1747 Skjeberg

Prosjekterende:
Marberg Bygg- og Tegneservice
Svarthalsveien 25
1739 Skjeberg
clas@marberg.no

© Alle rettigheter tilhører Marberg Bygg- og Tegneservice. Kopiering
av disse tegningene er forbudt uten skriftlig samtykke

Dato opprettet:
29.11.2023

Tegning:
Snitt C og D

Målestokk:
1:100

Tegningsnr.:
A30-02