


Romoversikt

- Bad
- Bod
- Entre
- Sov
- Stue/Kjøkken

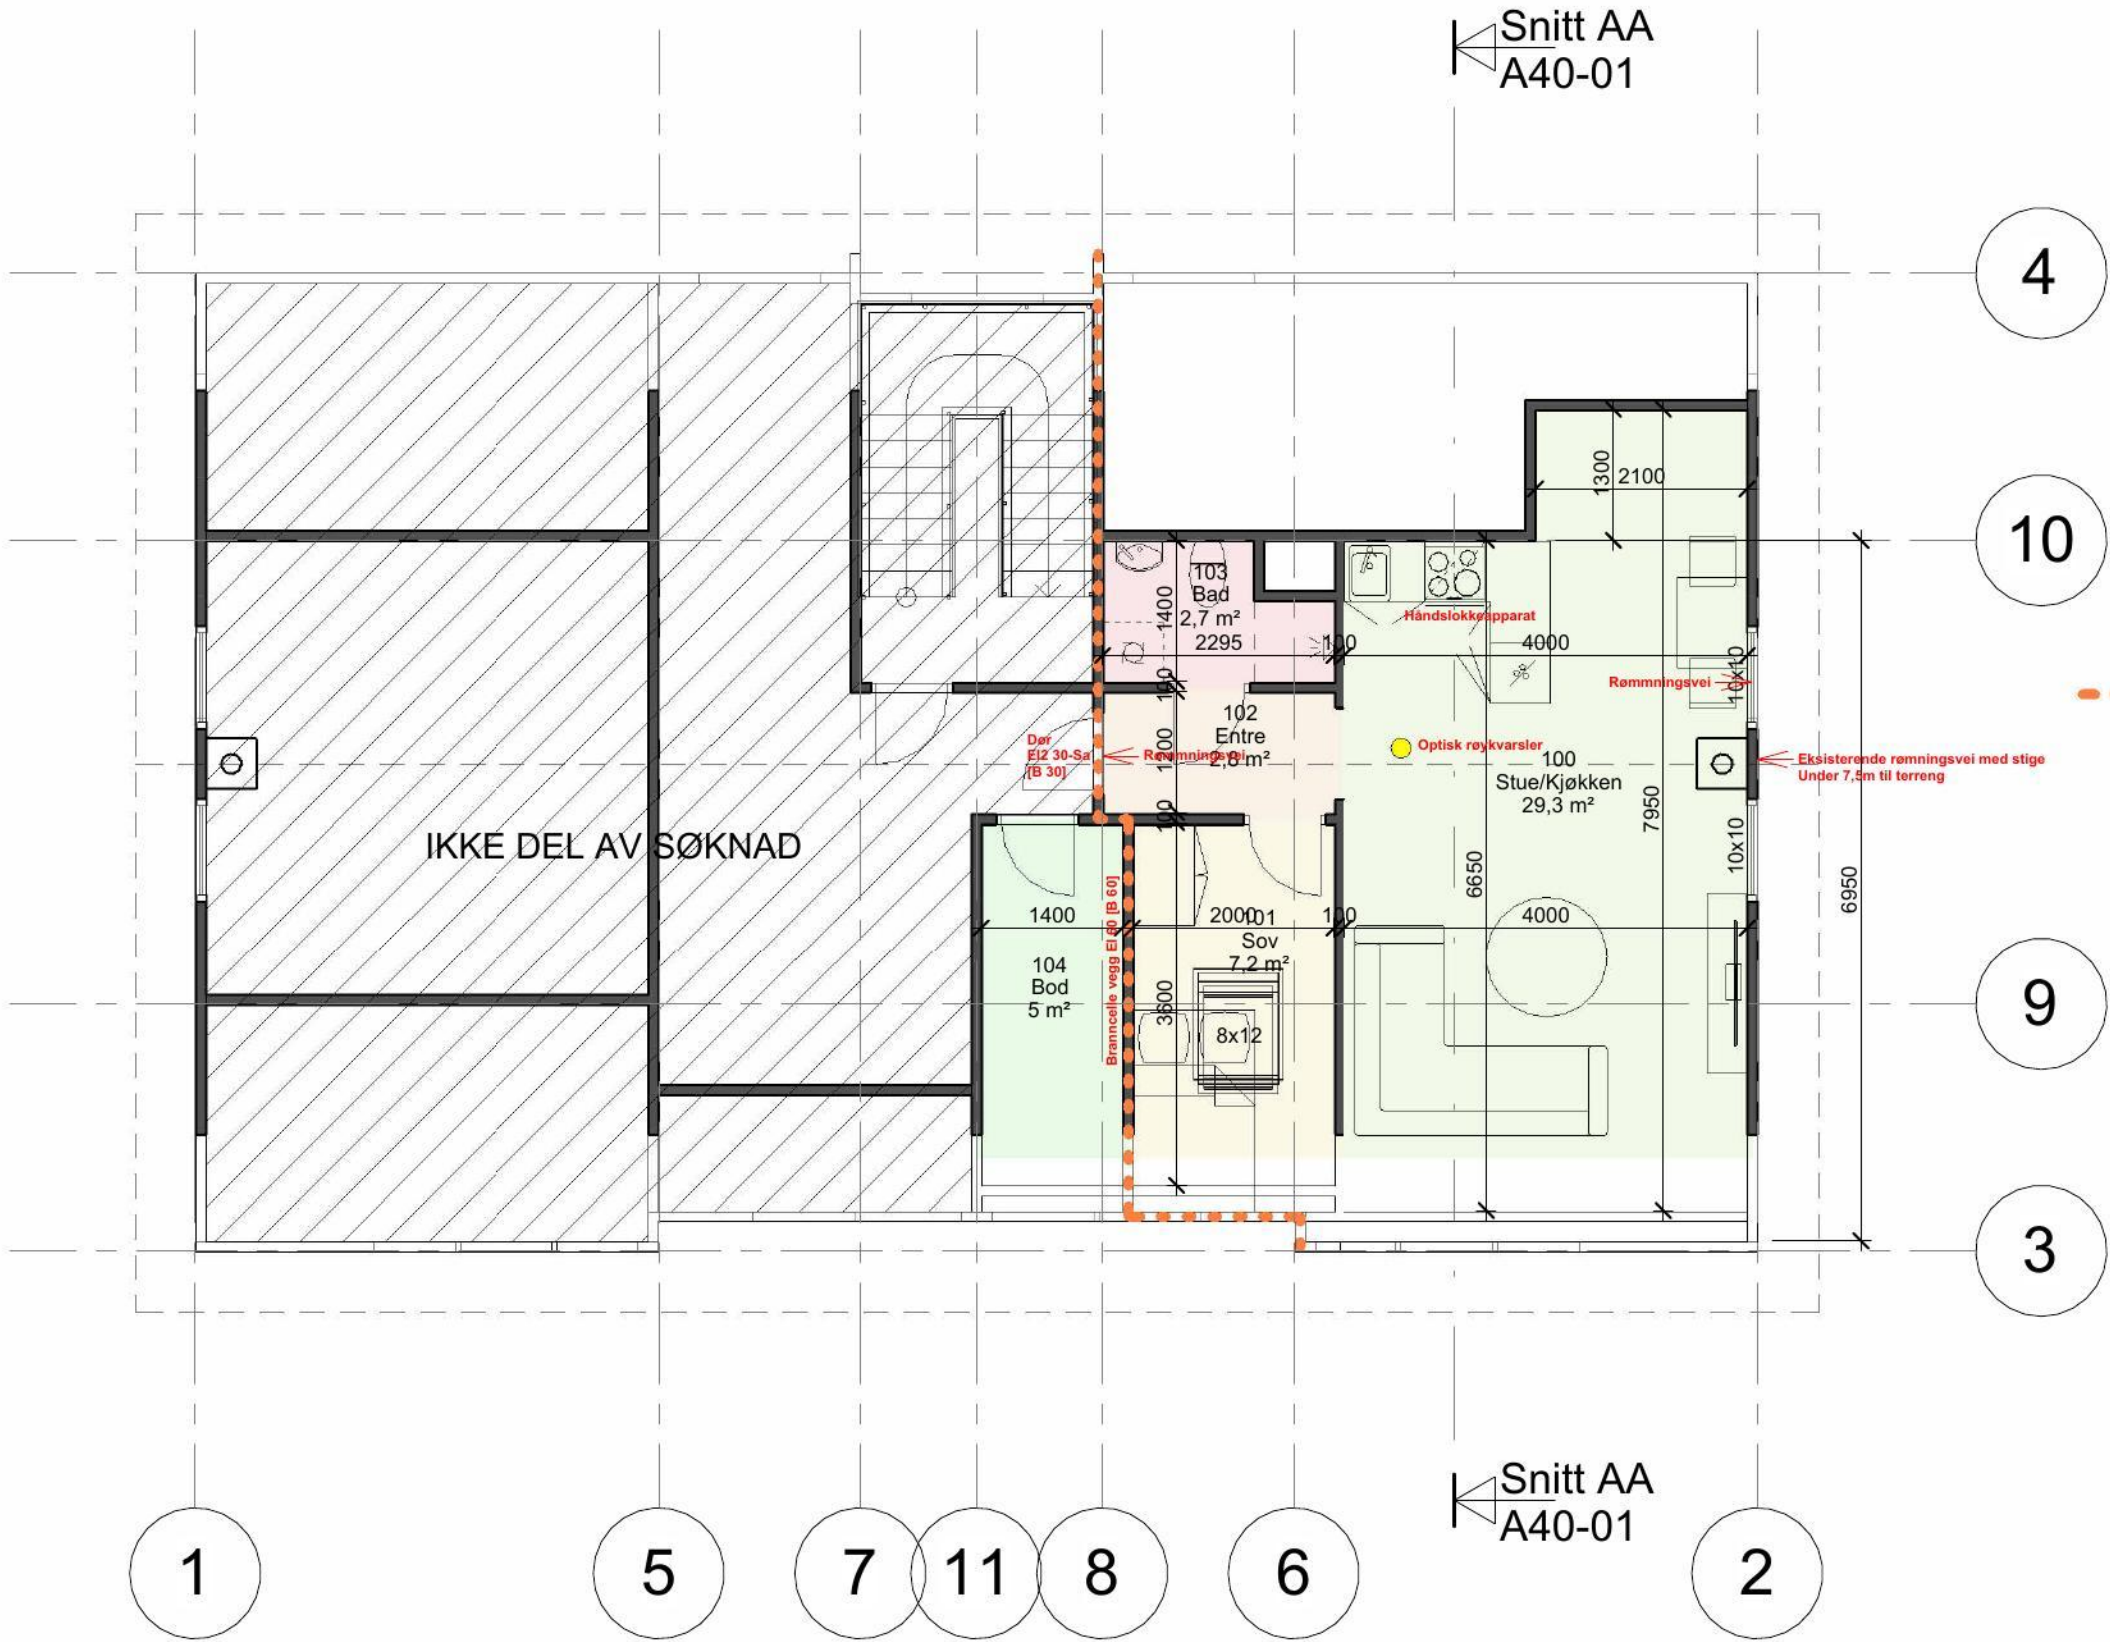

Rev.	Revisjonen gjelder	Utført	Kontr.	Dato	
Sigbjørn Thoresen Agder Allè 20a		Målestokk	Dato	23/08/23	
		1 : 100	Tegnet	SK	
			Kontr.	SK	
Plan Loft Byggemelding		Arkstørrelse	Prosjektnr.	DNK23023	
		Tegningsnr.			Rev.
		A20-04			
DAXARO ARKITEKTUR AS OLAVS GATE 26 3612 KONGSBERG		DAXARO			
DAXARO ARKITEKTUR AS © ALLE RETTIGHETER RESERVERT 2022					

N/S=0

Ø/N=0