


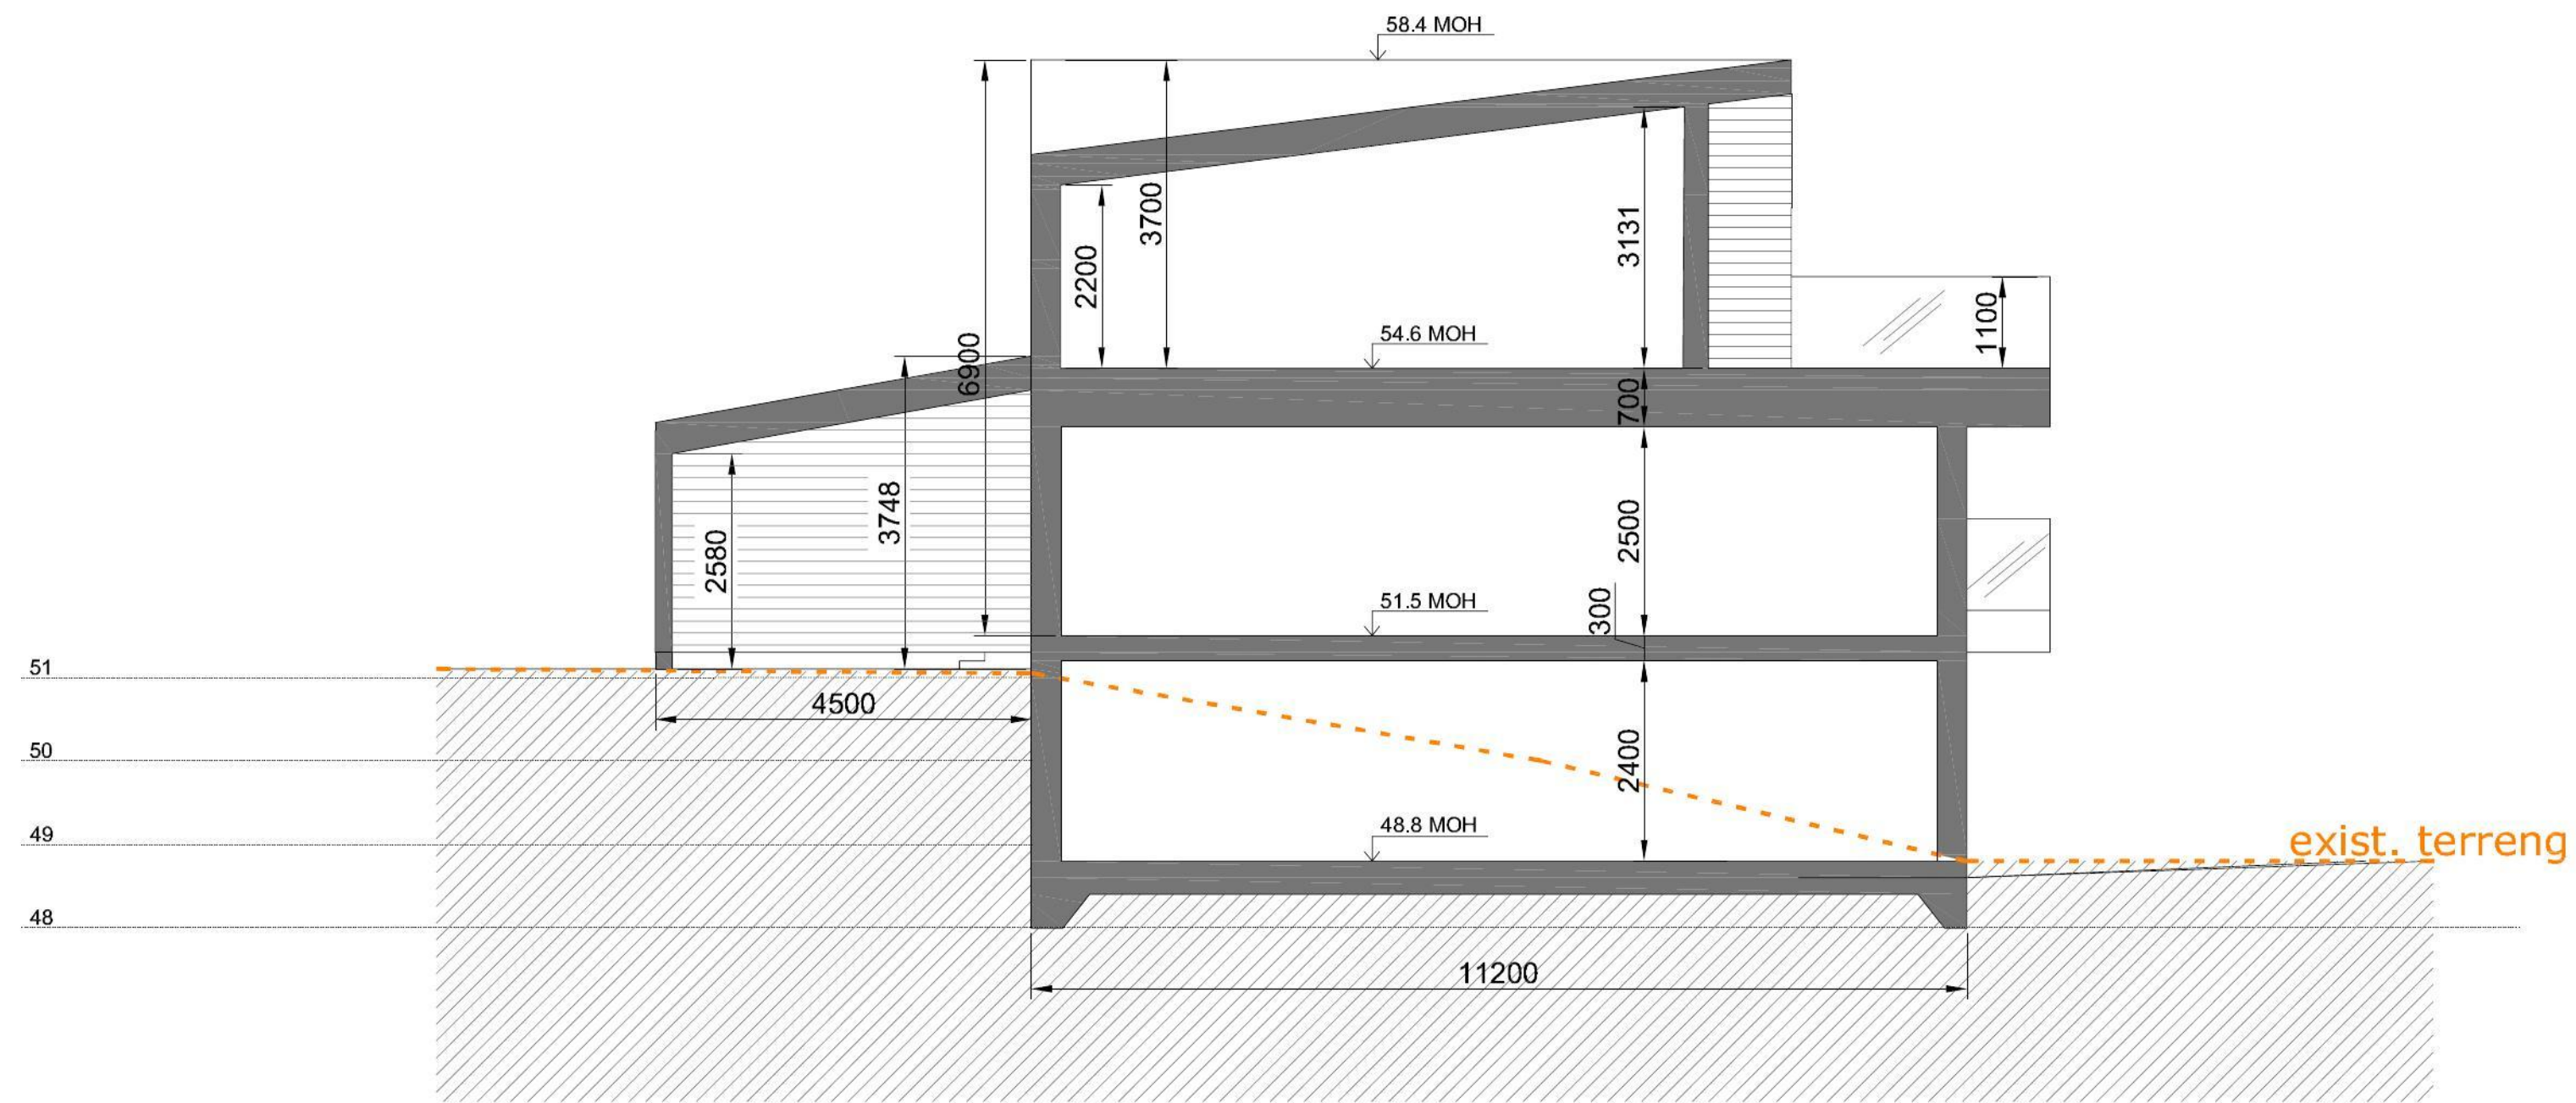

Rev nr 1 15.09.2023		Thor Helge Kvinge	
Tegning av: Snitt 1-1			
Tilltak type: Enebolig			
Byggeplass:	Humleveien 26, Kristiansand	Gnr: 37	Bnr:1166
	Mål: M:100 A3	Tegning nr:	
	Tegnet av: BYGGNOR SOLÅS AS	Erstening for:	
	Godgjett: Priit Avila	Erstattet av:	