

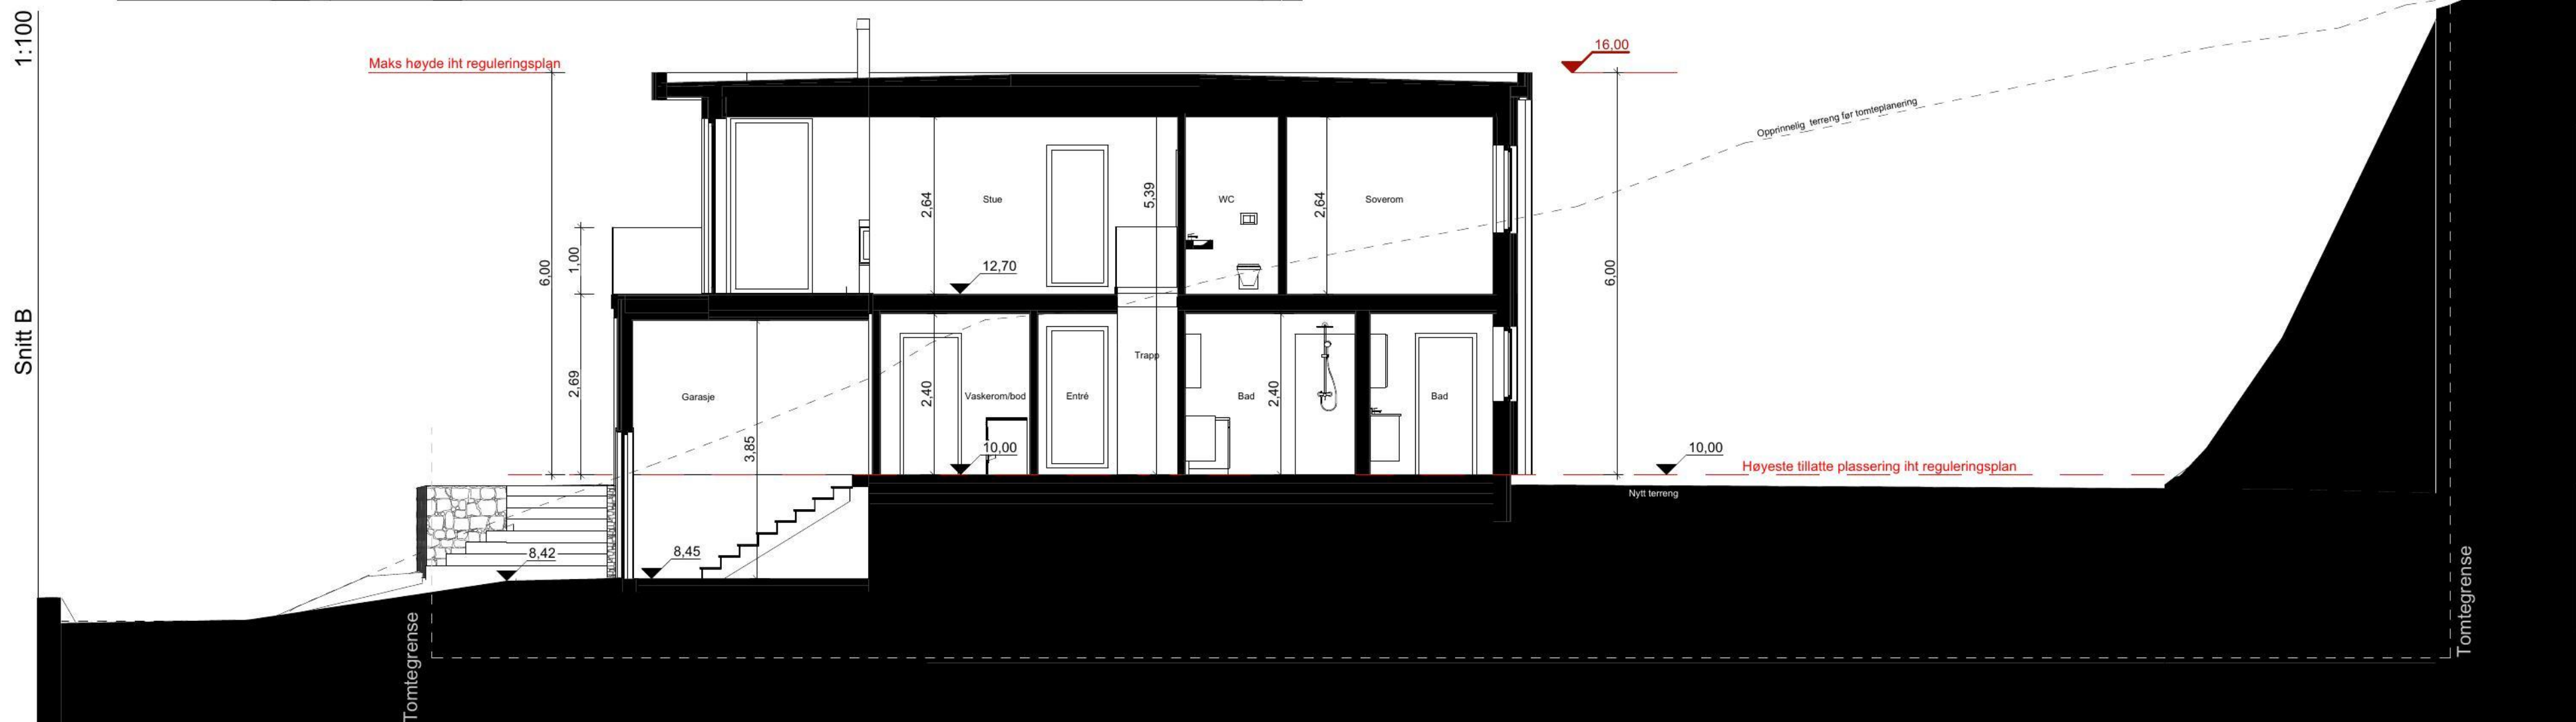


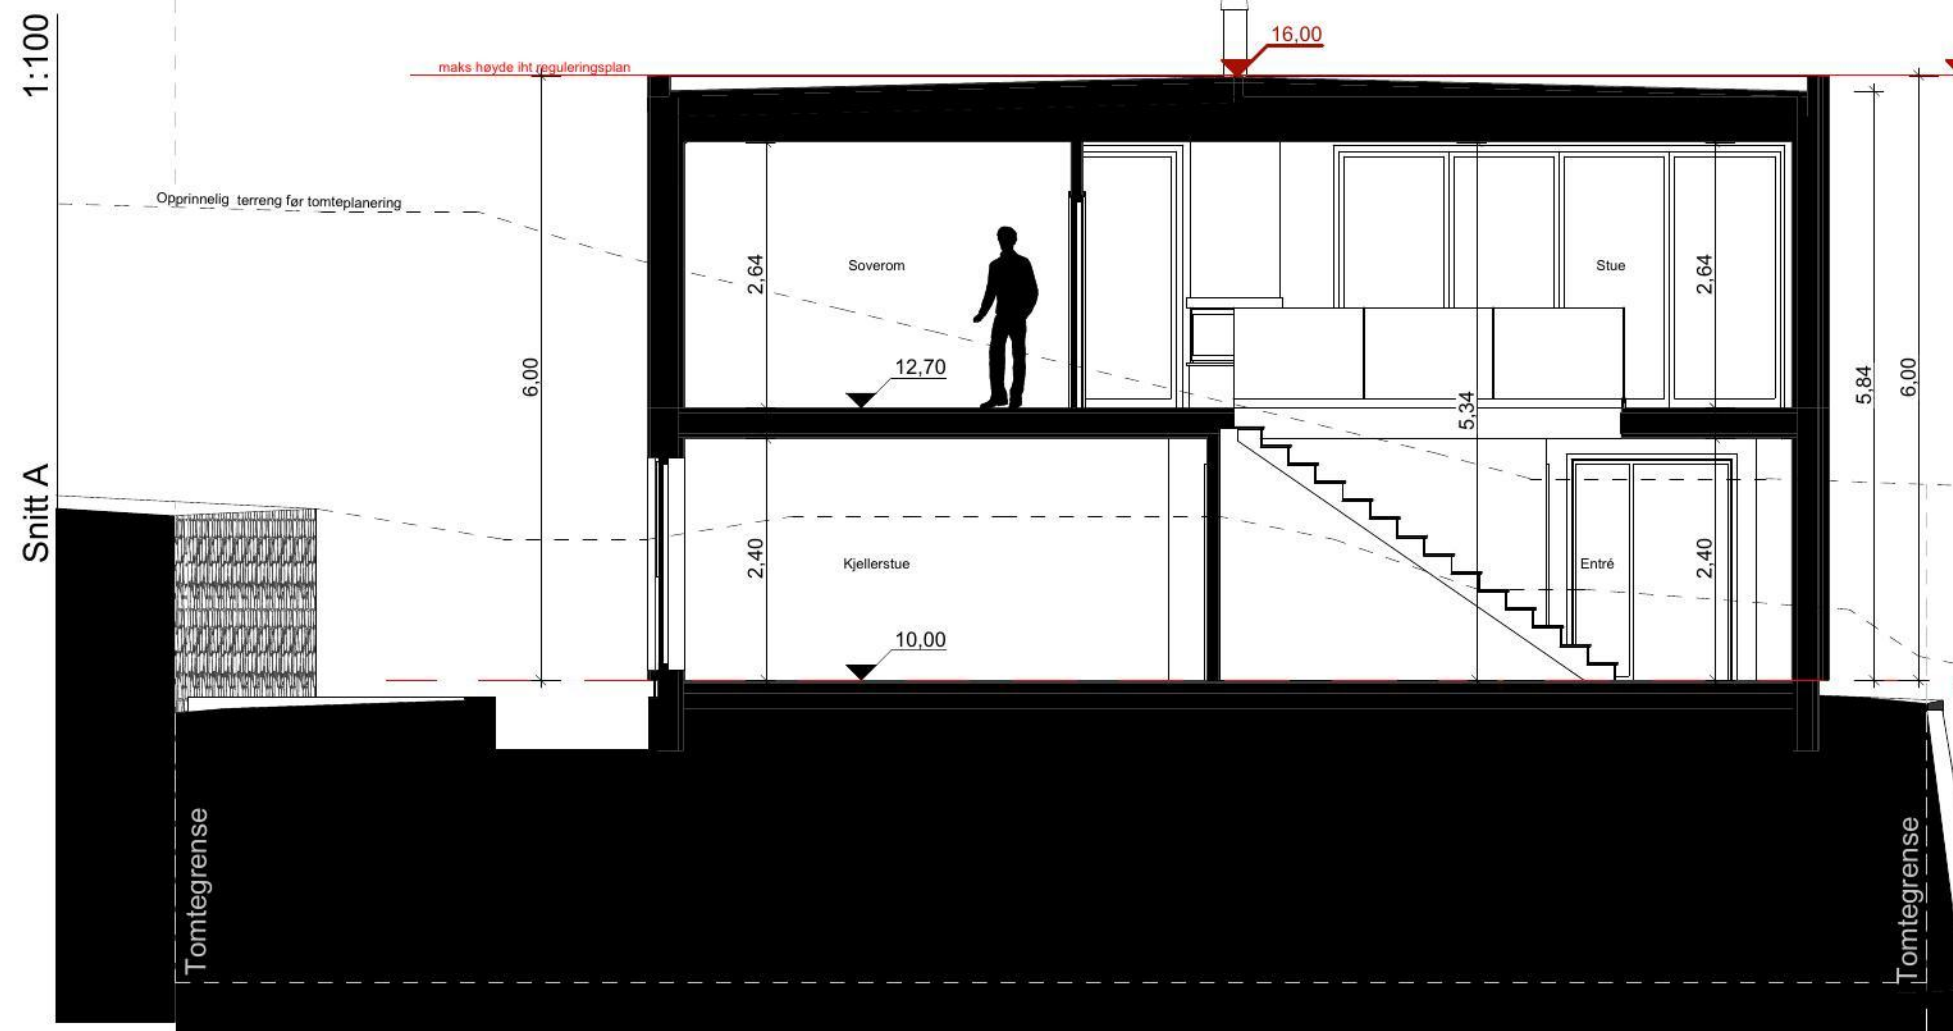

eller bruk av disse tegningene er forbudt uten skriftlig samtykke

Enebolig
Strandåsen 27C
4638 Kristiansand

Gnr./Bnr.:
97/449

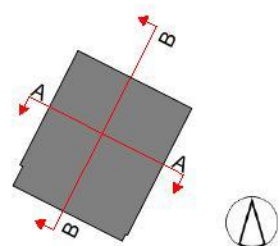

TROLLVEGG

Østre Strandgate 31, 4610 Kristiansand - Org. nr: 991 688 285
MVA - www.trollvegg.no - post@trollvegg.no

Type tegning:
Snitt A og B

Fase:
Søknadstegninger

Målestokk:
1:100

Dato:
06.09.23

Tegner:
ANF/MT

Tiltakshaver:
Knes Eiendom AS

Filnavn: KNES_arbeidstegning_27C_Variant2.pln

Prosjektnr.:

A676

Tegningsnr.:

A30-01