


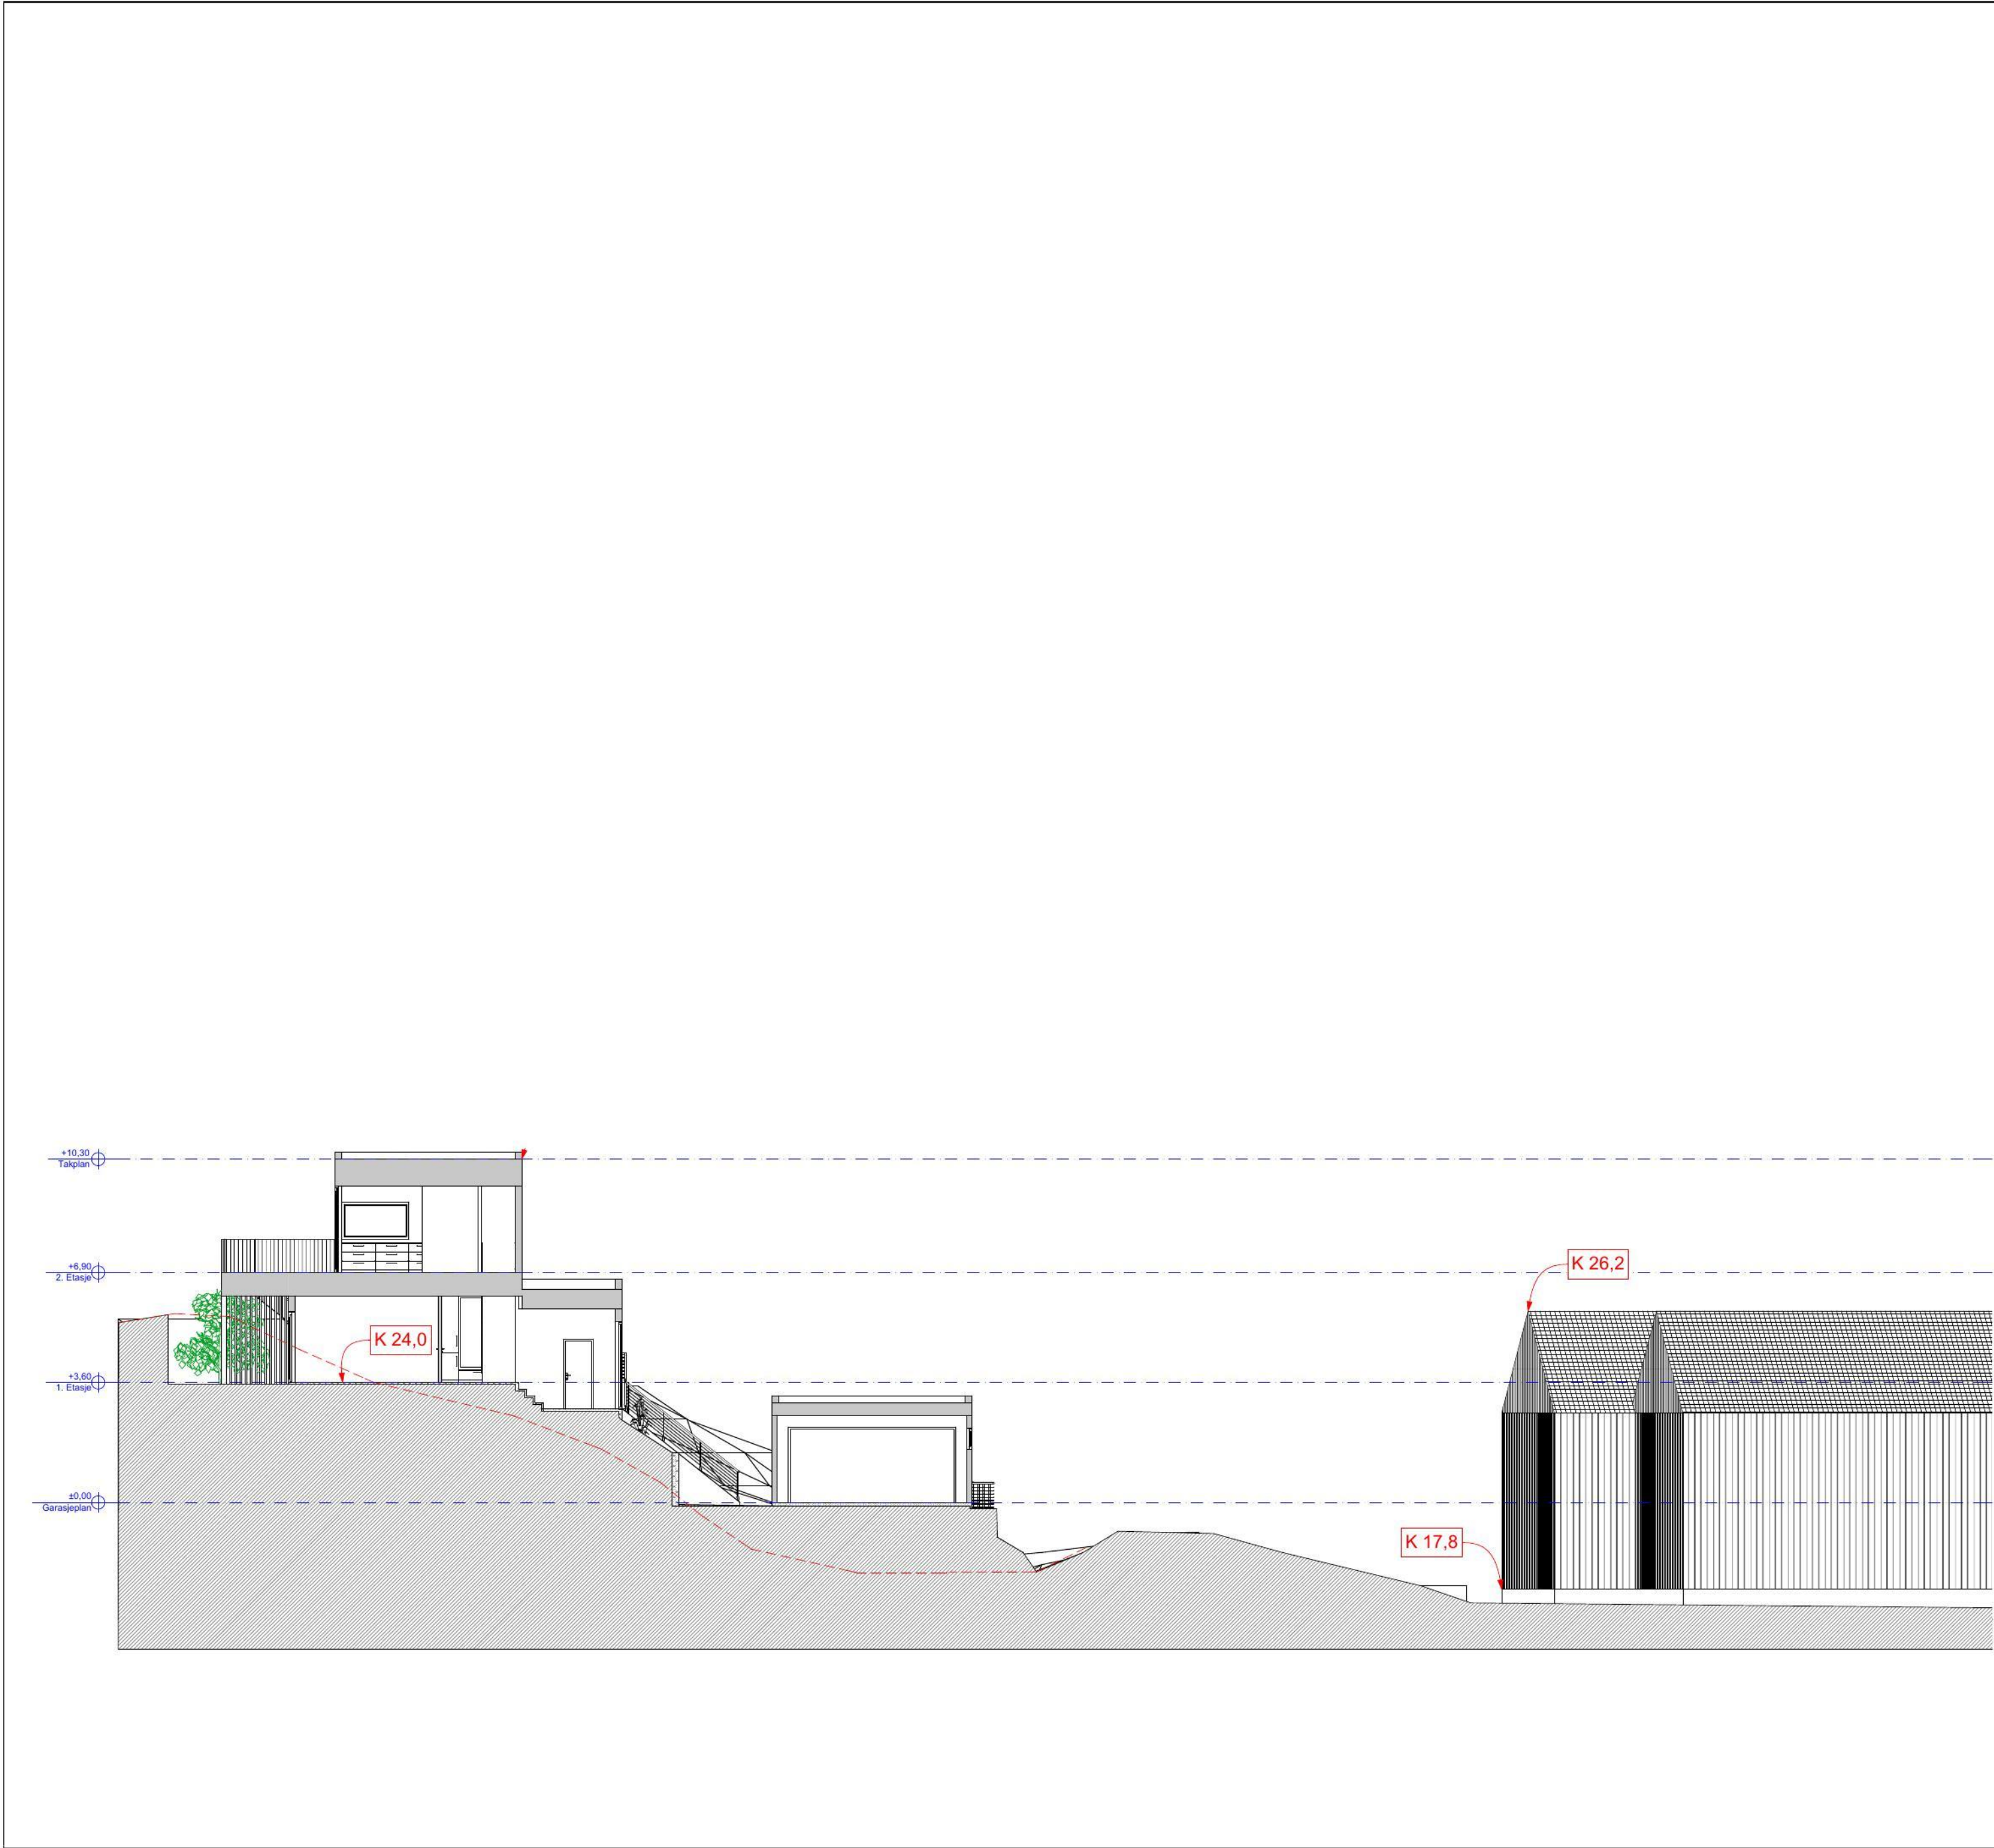

Tegningsnr.: A30-02		Revisjon nr.:	
Type tegning: Snitt 2			
Index	Dato	Beskrivelse	Sign Kontr.
ARKICON AS Arkitekttjeneste, byggrådgivning, prosjektering, byggesøknader, uavhengig kontroll og byggeledelse Besøksadresse: Kjøita 37 Postadr: 4630 Kr.sand Knut Ove Kristiansen Tlf: 916 84 510 Mail: knut.ove@arkiconas.no			
Prosjekteringsgruppen:			
☒	ARK :	Knut Ove Kristiansen	Kjøita 37 Tlf. 916 84 510
☐	RIB :	Rådg. ing. Bygg	veien 0 0000 Stedet Tlf. 00 00 00 00 Fax. 00 00 00 00
☐	RIE :	Rådg. ing. Elektro	veien 0 0000 Stedet Tlf. 00 00 00 00 Fax. 00 00 00 00
☐	RIV :	Rådg. ing. Vent.	veien 0 0000 Stedet Tlf. 00 00 00 00 Fax. 00 00 00 00
Fase: Søknadstegninger			
Gnr: 3 Bnr: 144			
Tittel: Lisa og Knut Ove Kristiansen Enebolig og garasje Østerøya 4625 Flekkerøy		Godkjent:	
		Kontroll prosjekt	
		Sign.:	Kontroll:
		Filnavn: Østerøya v5.pln	
		Dato: 31.03.2023	
Målestokk: 1:200		Kontroll utførende	
Sign.:		Kontroll:	
Prosjektnr.: Prosjektnr.	Tegningsnr.: A30-02	Prosjektnr. for prosjekterende/lev	
Type tegning: Snitt 2			