


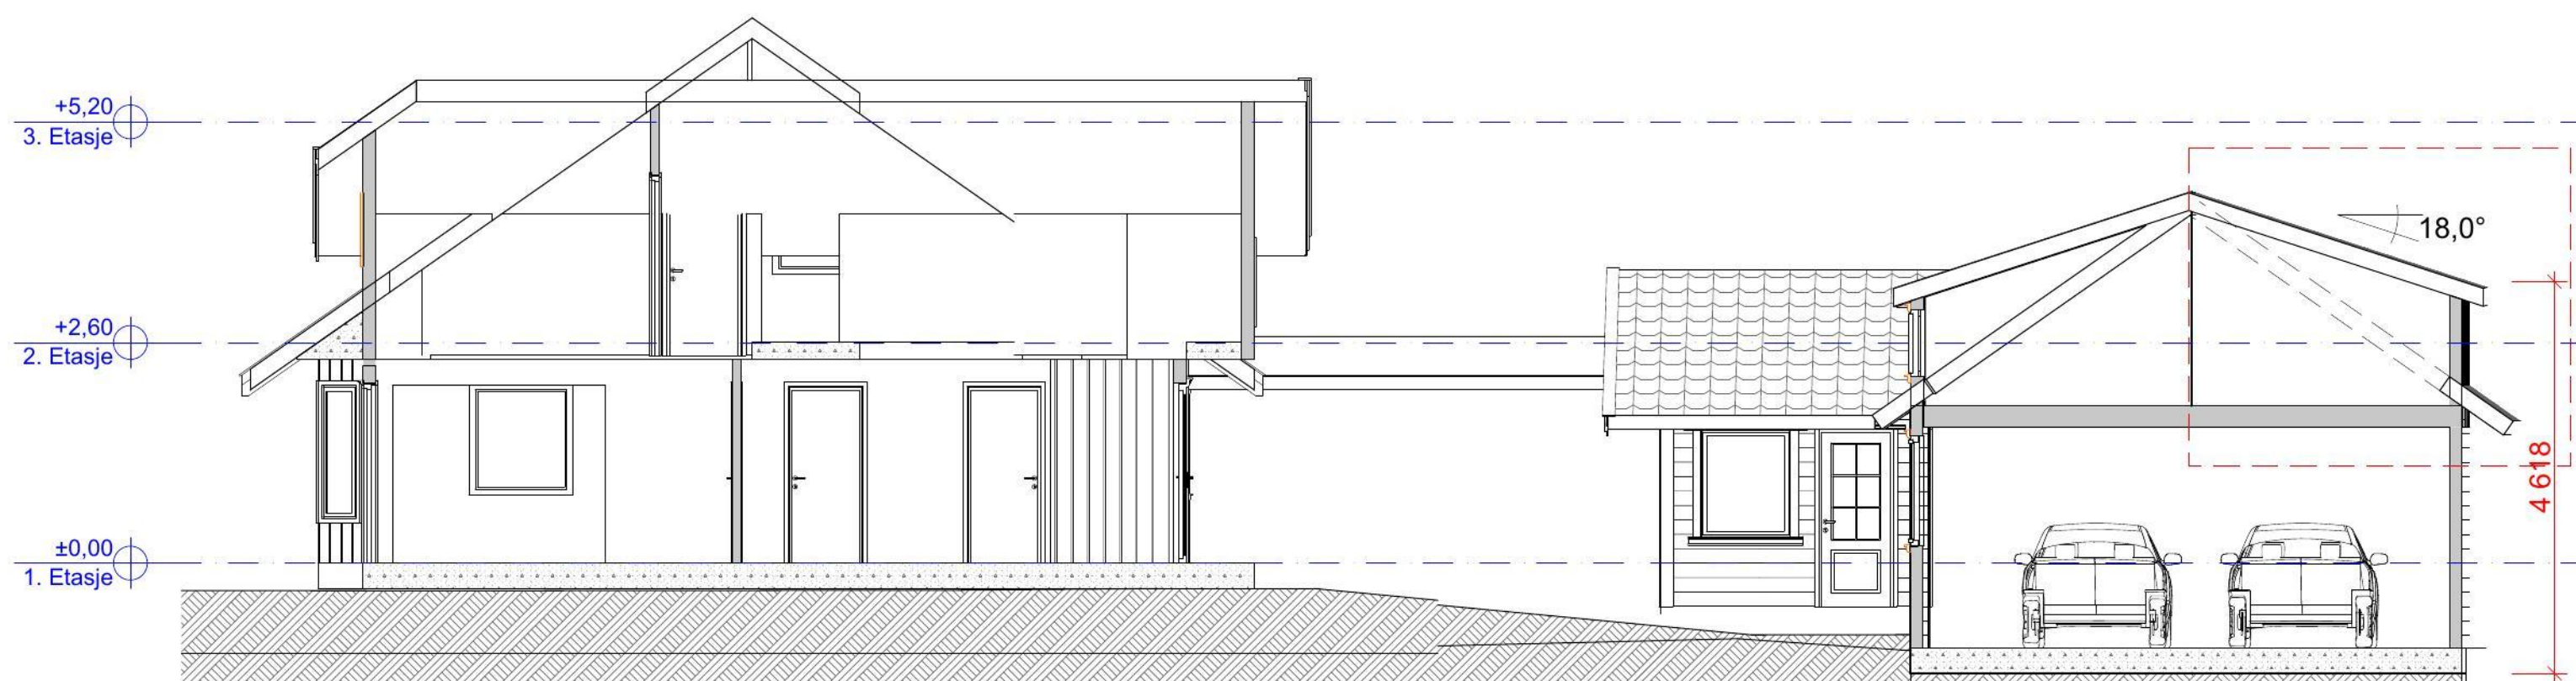

Tegningsnr.: A30-01	Revisjon nr.:									
Type tegning: Snitt										
Index	Dato	Beskrivelse							Sign	Kontr.
ARKICON Arkitekttjenester & Byggrådgivning Besøksadresse: Kjøita 37 (4. etg) Postadr: Kjøita 37 4630 Kristiansand Knut Ove Kristiansen Tlf: 916 84 510 Mail: knut.ove@arkiconas.no										
Prosjekteringsgruppen:										
☒	ARK :	Nancy Eisner	Kjøita 37 (4. etg) 4630 Kristiansand Tlf. 916 84 510							
☐	RIB :	Rådg. ing. Bygg	veienn 0 0000 Stedet Tlf. 00 00 00 00 Fax. 00 00 00 00							
☐	RIE :	Rådg. ing. Elektro	veienn 0 0000 Stedet Tlf. 00 00 00 00 Fax. 00 00 00 00							
☐	RIV :	Rådg. ing. Vent.	veienn 0 0000 Stedet Tlf. 00 00 00 00 Fax. 00 00 00 00							
Fase: Skisse										
Gnr: 96 Bnr: 287										
Tittel:							Goddjent:			
Monica Eikeland Tilbygg, Påbygg og Støttmur Odderhei Platå 58 4639 Kristiansand							Kontroll prosjekt			
							Sign.:		Kontroll:	
							Filnavn: Odderhei platå vs 23.08.2023.pln			
							Dato: 23.08.2023			
							Målestokk: 1:100			
							Kontroll utførende			
							Sign.:		Kontroll:	
Projektnr.: 36/2022							Prosjektnr. for prosjekterende/lev			
Type tegning: Snitt										
Tegningsnr.: A30-01										