Brannsikkerhet - Tegnforklaring:

Branncelle EI 30 (vinduer E 30)

Etasjeskille EI 30

Rømningsdør

Rømningsvindu


Røykvarsler

Brannslange

Slokkeapparat (6 kg)

Slokkevann:
Det legges til grunn at det finnes brannkum/hydrant < 50 meter fra eiendommen
Hvis ikke forutsettes det at brannvesenet kan medbringe tilstrekkelig slokkevann
Eiendommen er ikke i et tett bebygd område og det liten fare for brannspredning

Sikkerhet ved brann (premisser):
Ny boenhet - RKL 4 / BKL 1
Tilbygg eks boenhet - RKL 4 / BKL 1
Tilbygg eks garasje - RKL 1 / BKL 1
Preaksepterte ytelser

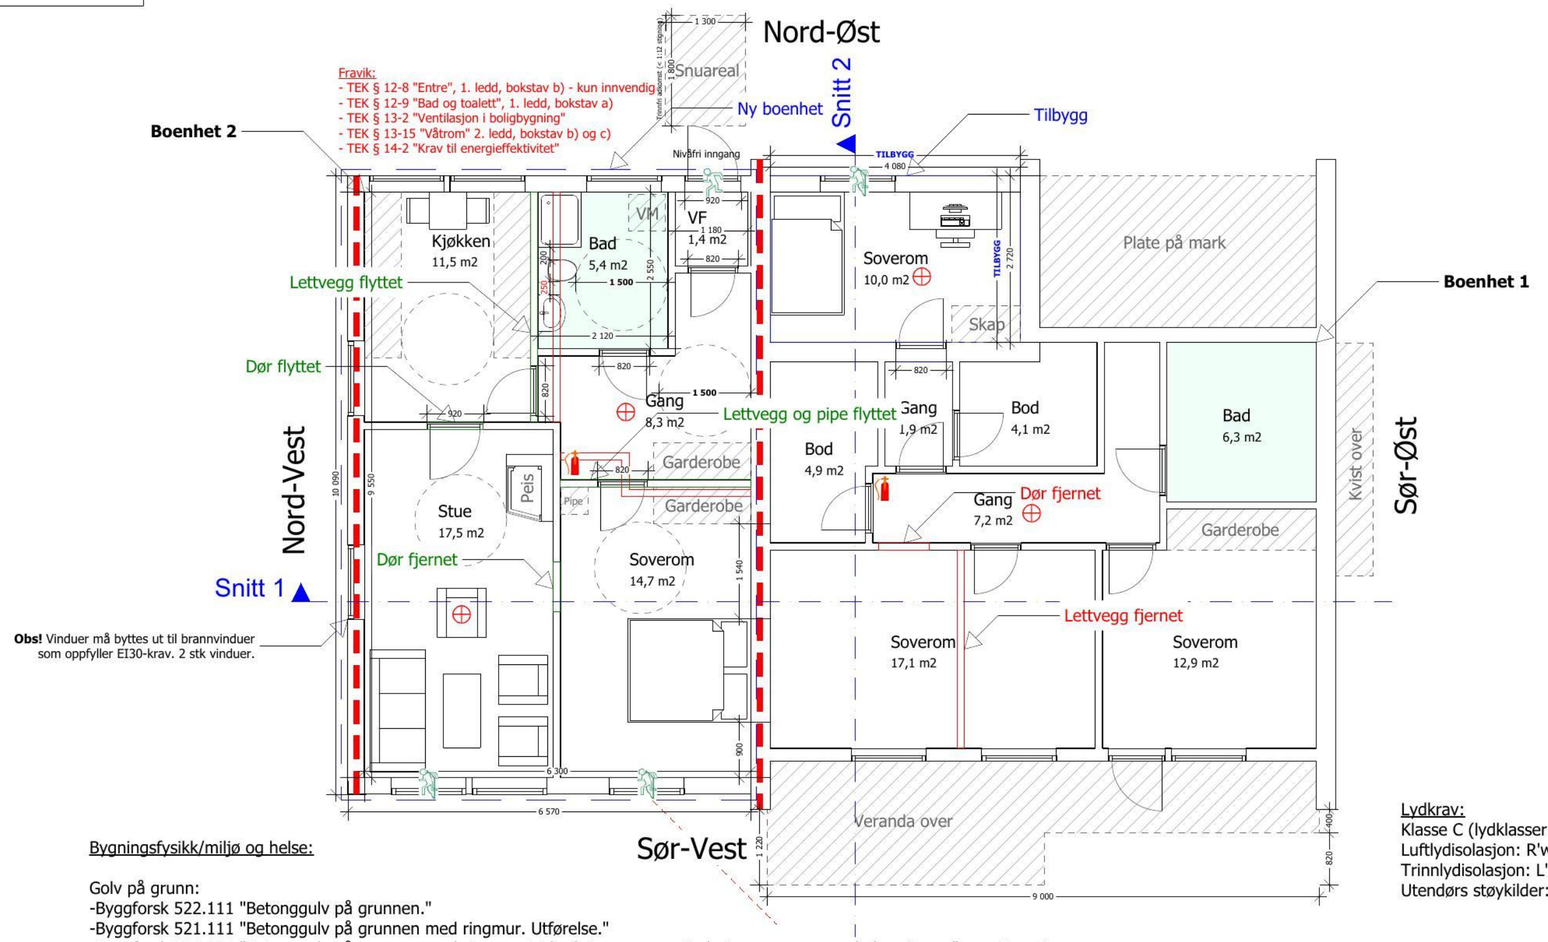

Lydkrav:
Klasse C (lydklasser for boliger)
Luftlydisolasjon: R'w 54 (db)
Trinnlydisolasjon: L'n,w 54 (db)
Utendørs støykilder: Lp,A,24h 30 /db)

Bygningsfysikk/miljø og helse:

Golv på grunn:
-Byggforsk 522.111 "Betonggulv på grunnen."
-Byggforsk 521.111 "Betonggulv på grunnen med ringmur. Utførelse."
-Byggforsk 521.112 "Betonggulv på grunnen med ringmur. Telesikring og varmeisolering av oppvarmede bygninger."

Yttervegg mot friluft:
-Byggforsk 523.251 "Bindingsverk av tre i småhus. Dimensjonering og utførelse."
-Byggforsk 523.701 "Innsetting av vindu i vegger av bindingsverk."
-Byggforsk 523.731 "Trinnfritt inngangsparti for småhus av tre. Tekniske løsninger."

Yttertak (tilbygg eks. boenhet):
-Byggforsk 525.002 "Takformer, taktyper og oppbygning."
-Byggforsk 525.207 "Kompakte tak."

Våtrom:
-Byggforsk 527.204 "Bad og andre våtrom."
-Byggforsk 541.805 "Golv i bad og andre våtrom."

Radon:
Det er ikke mulig å sikre seg mot radon pga. eksisterende utførelse (gjelder ny boenhet og tilbygg i eks. boenhet)
Dermed må det foretas en radonmåling for å påse at grenseverdiene er ivaretatt, før ny boenhet tas i bruk

Energi:
Det legges til grunn at det søkes fravik fra TEK § 14-2 "Krav til energieffektivitet"
Minimumsnivå for energieffektivitet (altså minstekrav til bygningsdeler) skal likevel oppfylles

Utdrag fra TEK § 14-3 "Minimumsnivå for energieffektivitet"

U-verdi yttervegg [W/(m² K)]	*U-verdi tak [W/(m²K)]*	*U-verdi gulv på grunn og mot det fri [W/(m² K)]*	*U-verdi vindu og dør inkludert karm/ramme [W/(m² K)]*	*Lekkasjetall ved 50 Pa trykkforskjell (luftveksling per time)*
≤ 0,22	≤ 0,18	≤ 0,18	≤ 1,2	≤ 1,5

Grunnlag:
Yttervegg: Trestendere min. 150+50 mm iso kl 34 (eller tilsvarende)
Flatt tak (tilbygg): I-bjelker min. 200+50 mm iso kl 34 (eller tilsvarende)
Gulv på grunn: Betongdekke min. 150 mm iso kl 37 (eller tilsvarende)

Grønt = Som-bygget
Rødt = Fjernes
Blått = Nytt

ArchiCAD 24

Tegningsnummer: **A20-1**
Revisjon nummer: **5**

Type tegning: **Plan U. Etasje (bolig)**

karlsen:byggconsult

Kopirett © - Karlsen Byggconsult AS (org.nr.: 931 273 280)

Arkitektur (bygningskunst, så vel tegninger og modeller som selve byggverket) er beskyttet av "Lov om opphavsrett til åndsverk m.v. (åndsverksloven)". Dette innebærer blant annet at arkitekten skal navngis når byggverk presenteres f.eks. i media. Plagiat (kopi) og misbruk av denne opphavsrett kan medføre reaksjoner og sanksjoner fra foretaket, uten at det på forhånd foreligger særskilt avtale.

Prosjekterende:

Alexander Karlsen

karlsen@kbcon.no
+47 97 67 46 27

Fase:

Forprosjekt

Arealregnskap:

Bygd areal (BYA)

Eksisterende bolig: 172,4 m²-BYA (utkragning utgjør 14,3 m²-BYA)
Eksisterende garasje: 36,2 m²-BYA
Tilbygg bolig: 0,0 m²-BYA ("0,0" pga. veranda over)
Tilbygg garasje: 18,9 m²-BYA
Sum: 227,5 m²-BYA

Bruksareal (BRA)

Eksisterende: 286,5 m²-BRA
Tilbygg (bolig): 11,3 m²-BRA
Tilbygg (garasje): 18,2 m²-BRA
Sum: 316,0 m²-BRA
Boenhet 1, bolig: 202,7 m²-BRA (tilbygg utgjør 11,3 m²-BRA)
Boenhet 1, garasje: 25,8 m²-BRA (tilbygg utgjør 9,1 m²-BRA)
Boenhet 2, bolig: 61,7 m²-BRA
Boenhet 2, garasje: 25,8 m²-BRA (tilbygg utgjør 9,1 m²-BRA)
Sum: 316,0 m²-BRA

Utnyttelsesgrad

Underlag: "Plasseringsbestemmelse" med firkant på kartet

Utregning, eksisterende situasjon: 208,6 (areal) / 738,5 (tomt) * 100 = 28,24
Utnyttelse, eksisterende situasjon: 28,24 %-BYA
Utregning, ny situasjon: 227,5 (areal) / 738,5 (tomt) * 100 = 30,80
Utnyttelse, ny situasjon: 30,80 %-BYA

Revisjons liste:

Rev.nr.:	Beskrivelse:	Dato:
rev. 1	Skisse u.etg. basert på sist godkjent tegn	05.07.23
rev. 2	Oppdatert skisse etter mål kunde	06.07.23
rev. 3	Skissere videre, fasadetegninger, snitt	07.07.23
rev. 4	Ajourføring for byggemelding, bygningspr	12.07.23
rev. 5	Branncelle mot nord, vinduer må byttes	18.08.23
rev. 6	-	-
rev. 7	-	-
rev. 8	-	-

Tiltakshaver:

Kai Haugen

Prosjekt:

Ombygging, tilbygg

Villandveien 3, 4623 Kr.sand

Kort beskrivelse:
Ombygging, dvs. ønske om opprettelse av ny boenhet i underetasje.

Tilbygg i u. etg (boenhet 1), og tilbygg i frittliggende garasje (delt på boenhetene)

Dato: **18.08.2023**

Målestokk **1:100**

Signatur: **AK**

Gbnr.: **7/446**

Prosjektnummer: Prosjektnr.

Tegningsnummer: A20-1

Type tegning: Plan U. Etasje (bolig)