

For å unngå en midlertidig forverring av stabilitetsforholdene, utføres utslaking av skråningen med gravemaskin (langgraver) fra skråningstopp og ned til kote +5. Avgravde masser kan mellomlagres i en avstand på minimum 20 m fra skråningstopper.

Fortrinnsvis benyttes langgraver for å unngå tung trafikkering helt ytterst på skråningen. Graveentreprenør må vurdere nødvendig utstyr basert på planlagt sikringstiltak og aktuelle grunnforhold.


Avgravde flater vil i en periode få redusert overflatestabilitet på bakgrunn av manglende topplag, vegetasjon og trær. Vi anbefaler derfor at avgravde flater tildekkes med ca. 10 cm sand- og grusmasser (f.eks. 0/32 eller tilsvarende) for beskyttelse. Dette laget skal være inkludert i avlastningslinja på 1:1,65 fra kote +5.

Videre anbefaler vi å plante vegetasjon med god rotvekst, fortrinnsvis buskvekster (hassel eller tilsvarende) som belaster skråningen marginalt.

Sikringstiltaket bør overordnet utføres i en tørr periode med lite nedbør. For å unngå at avgravde flater står ubeskyttet over lengre perioder, anbefaler vi at utslaking og tildekking med sand/grus utføres seksjonsvis (f.eks. 10 m bredde).

Tildekking av avgravde flater med presenning i perioder med mye nedbør kan bli aktuelt.

Figuren nedenfor viser utklipp fra tegning LS03, med skissering av planlagt avlastning. Tegningen er mottatt av Feste Sør AS den 09.05.2023.

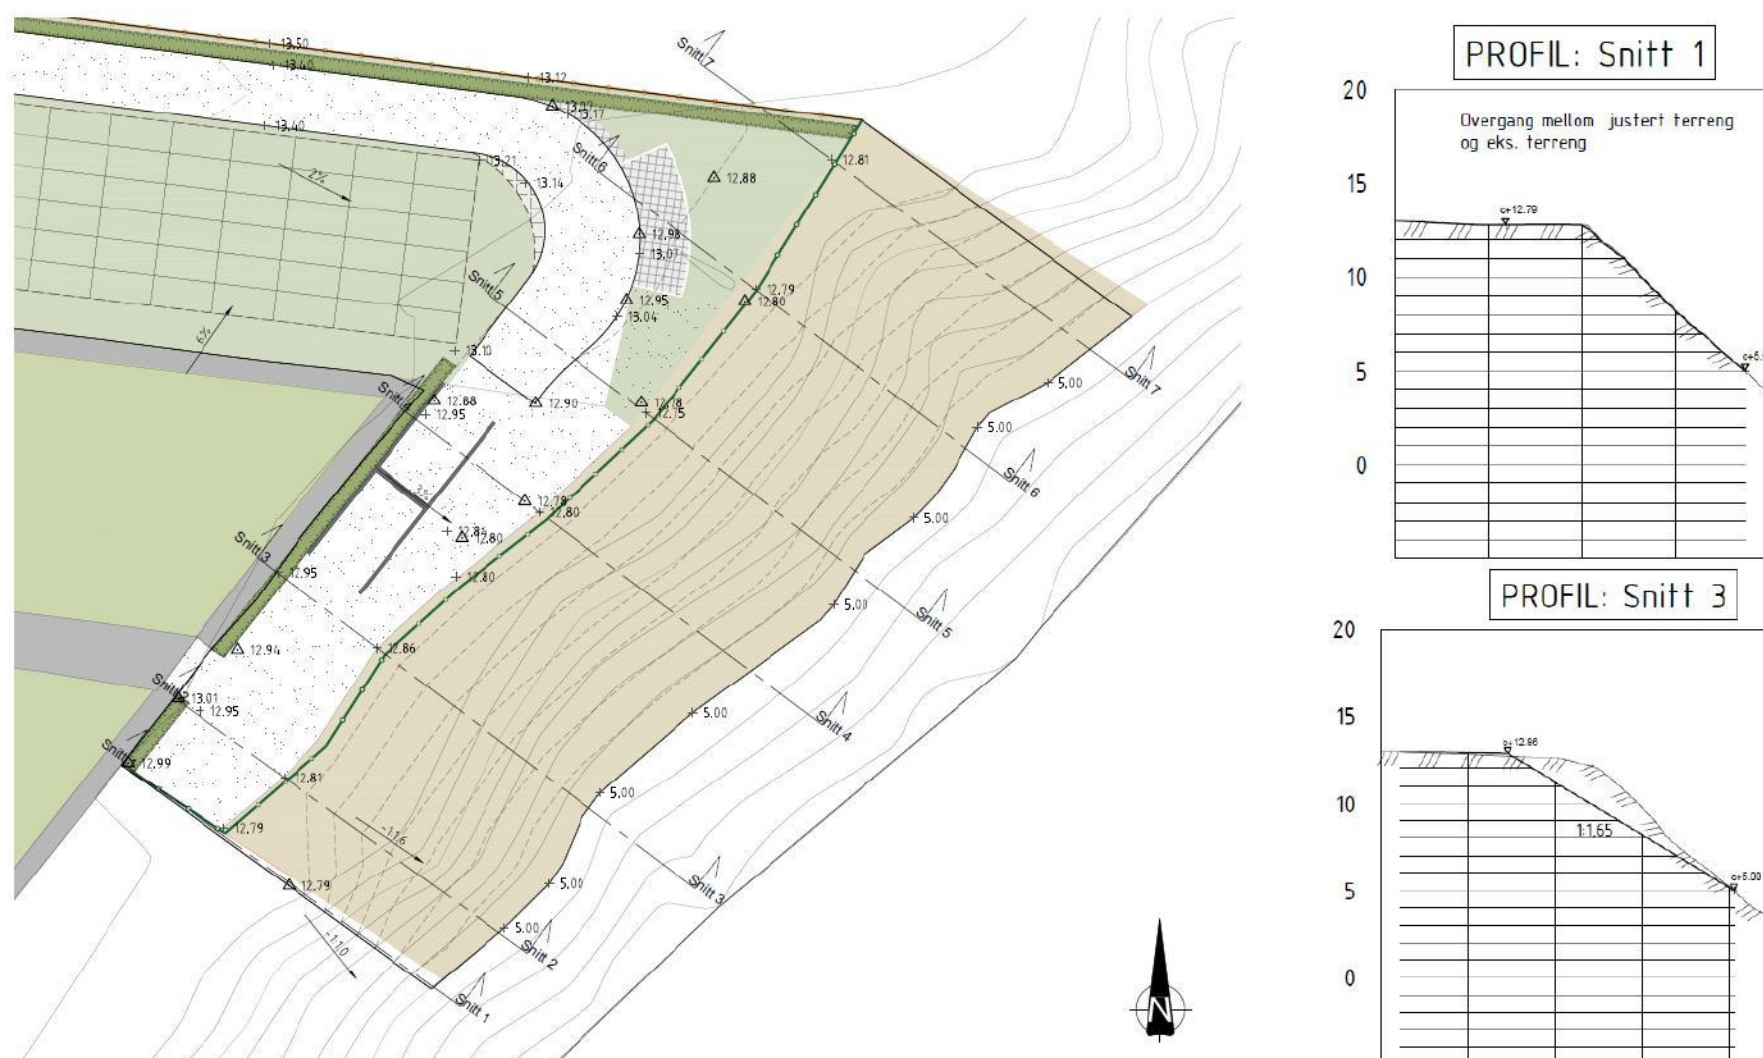

Figur 6. Utklipp fra tegning LS03, som ble mottatt av Feste Sør AS den 09.05.2023.

Merk at sikringstiltaket er avgrenset mot tomtegrensa i sørvest og mot løsmasserygg i nordøst. Skråningsstabiliteten utenfor planlagt avlastningsområde har ikke tilfredsstillende sikkerhet iht.