



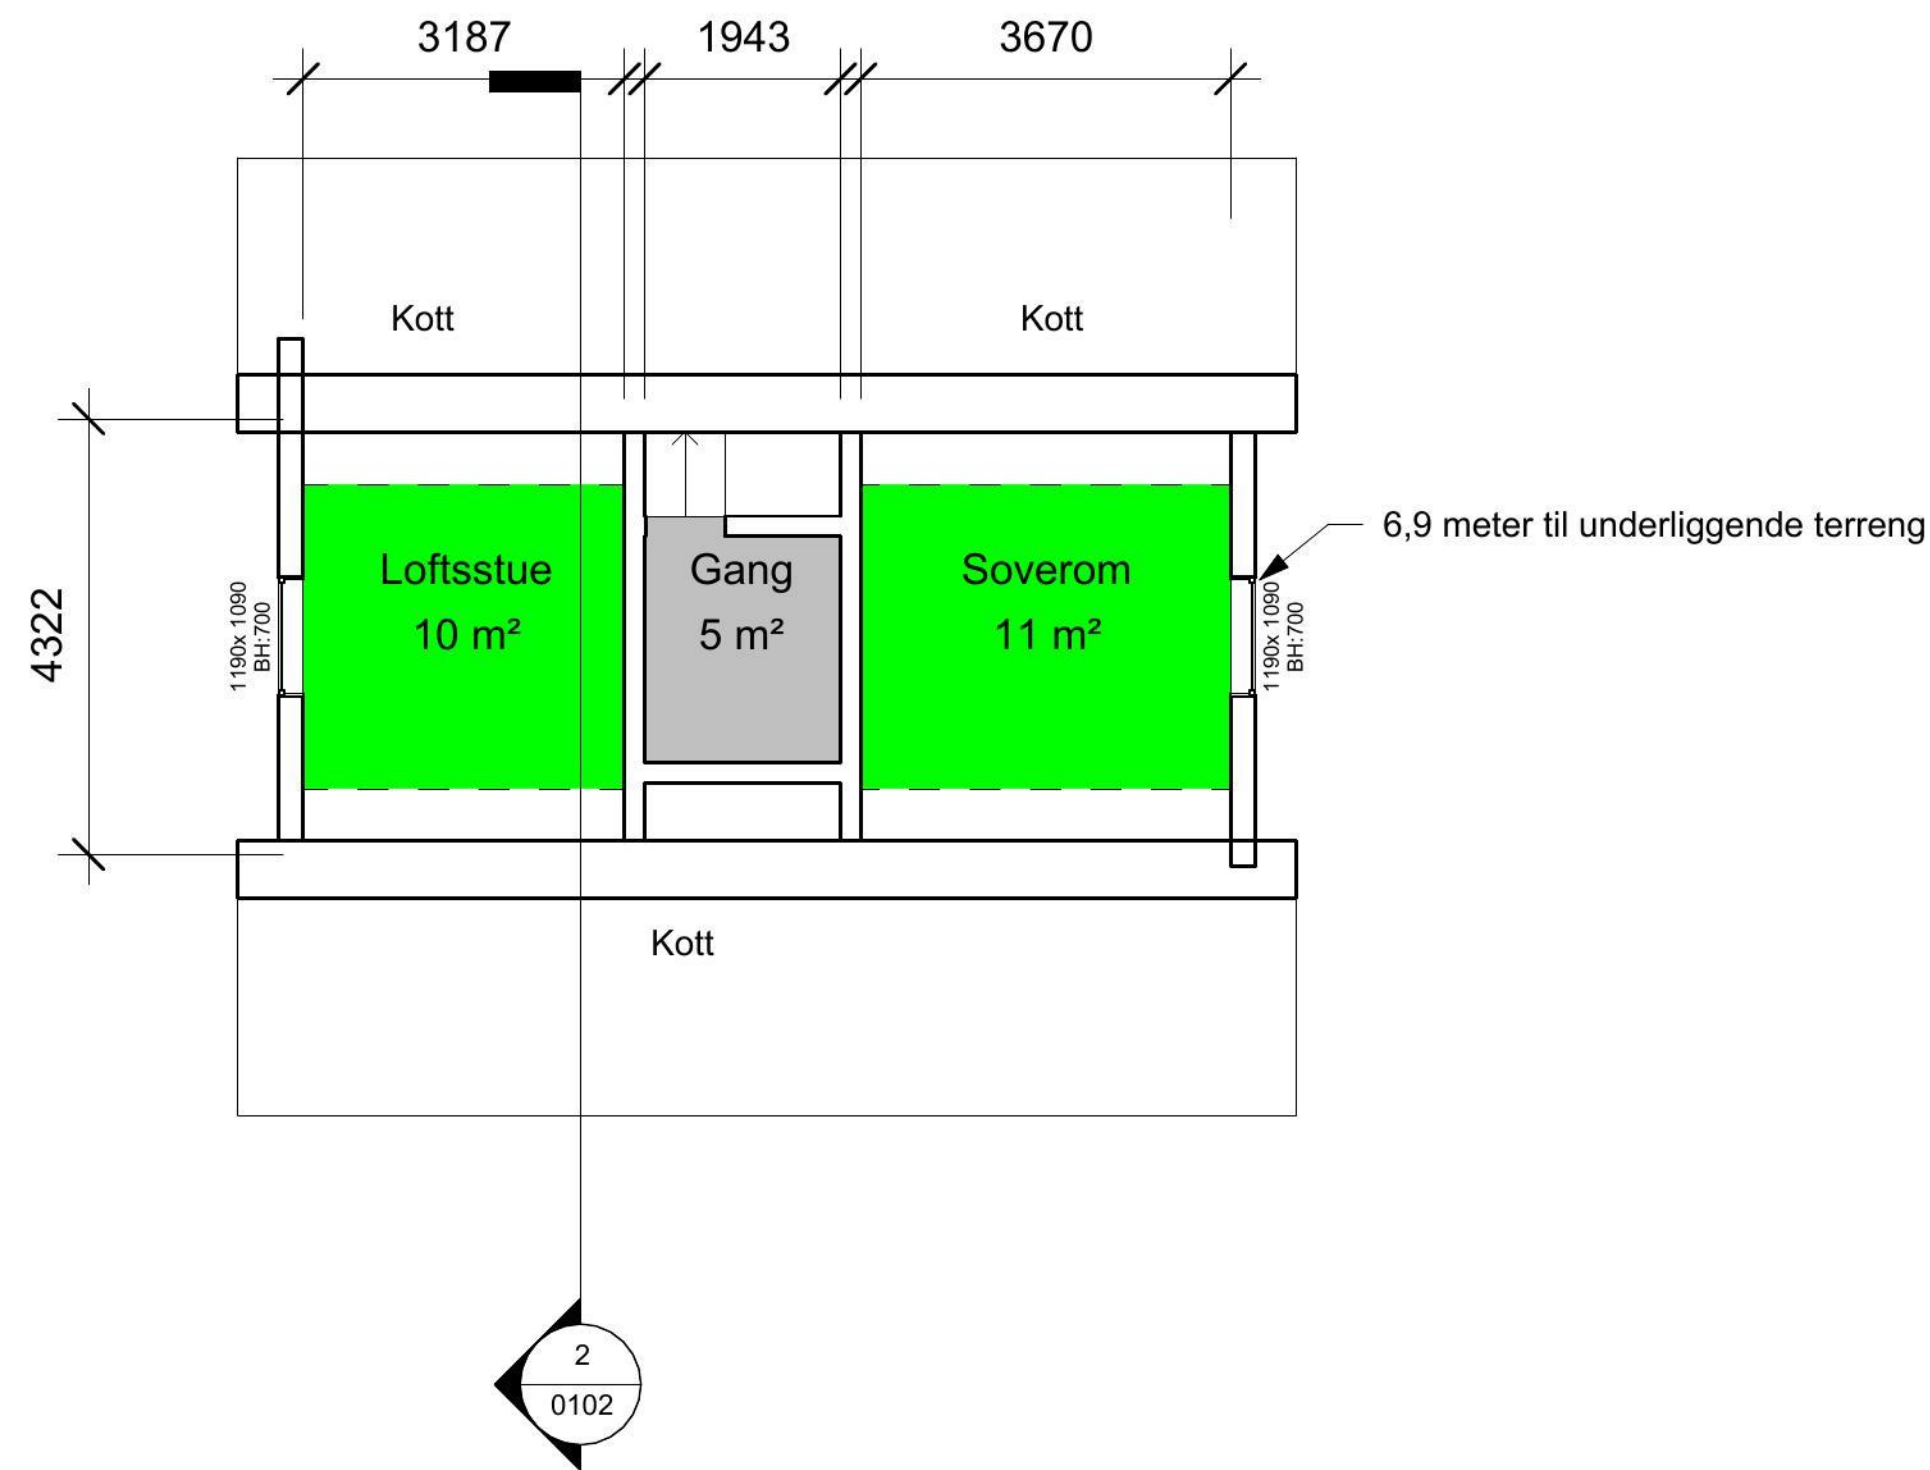


1 3. etasje
1 : 100

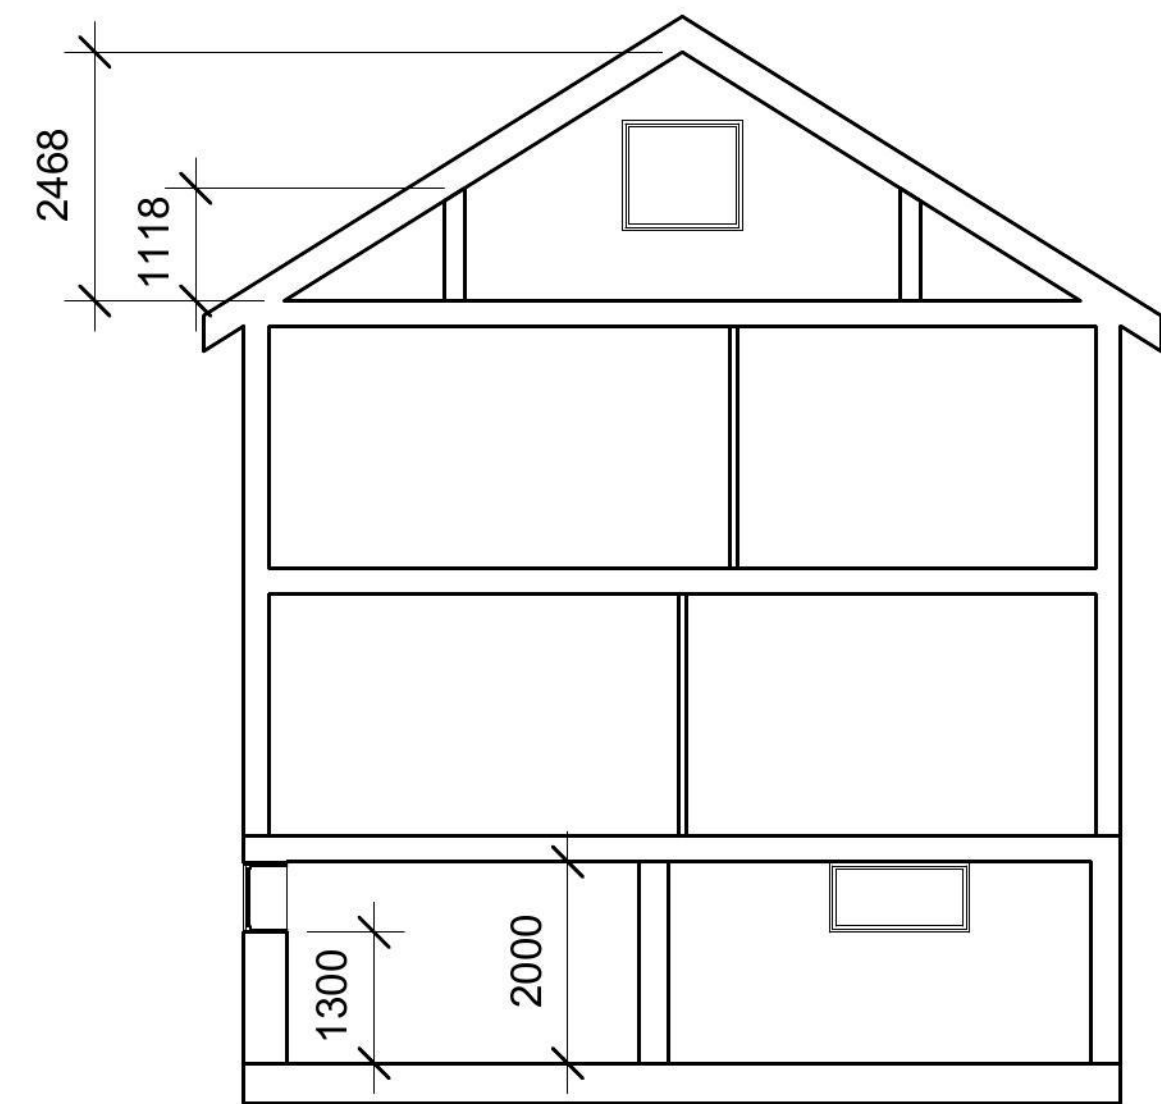

2 Snitt A
1 : 100

© Alle rettigheter tilhører Mentor Prosjektering AS, kopiering eller bruk av disse tegningene er forbudt uten skriftlig samtykke

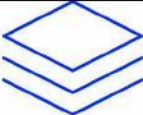Tiltakshaver Morten Ramm	 MENTOR PROSJEKTERING AS Din mentor, ditt prosjekt Grenseveien 21, 4313 Sandnes NO 992 866 233	Rev.	Beskrivelse	Dato	Tronesgeilen 4 Plan loft + snitt Tegningsdato: 28.12.2023 13:17:02 Målestokk: 1 : 100 Format: A3 Tegnet av: Raymond Raugstad	 PRINT REDUCTION BAR A3 SHEET Pro-nr / Tegnings-nr. 23144 - 0102 Revisjon 