
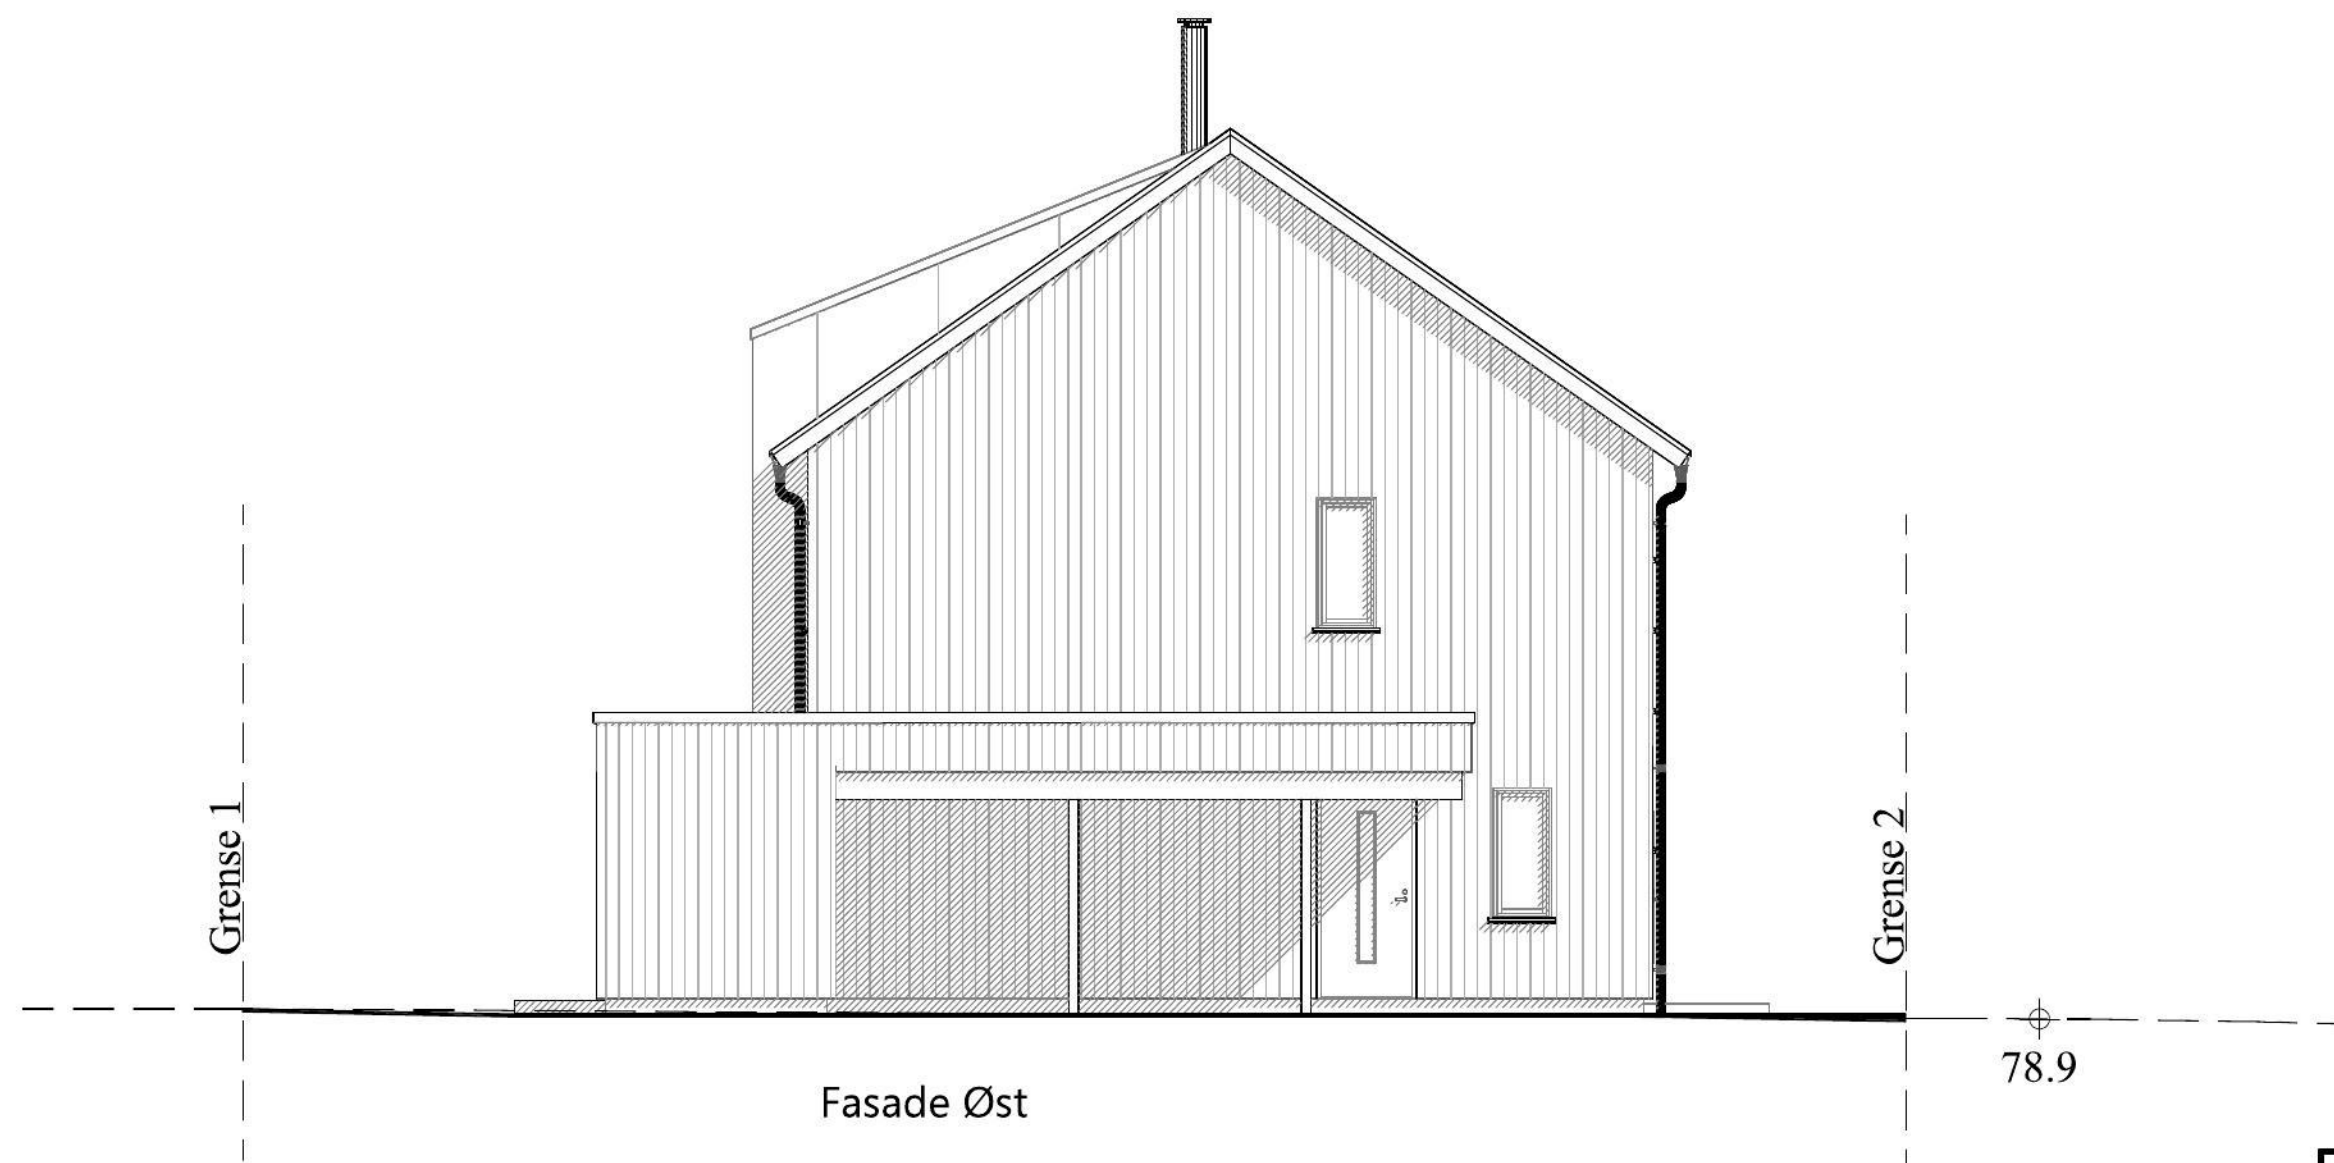


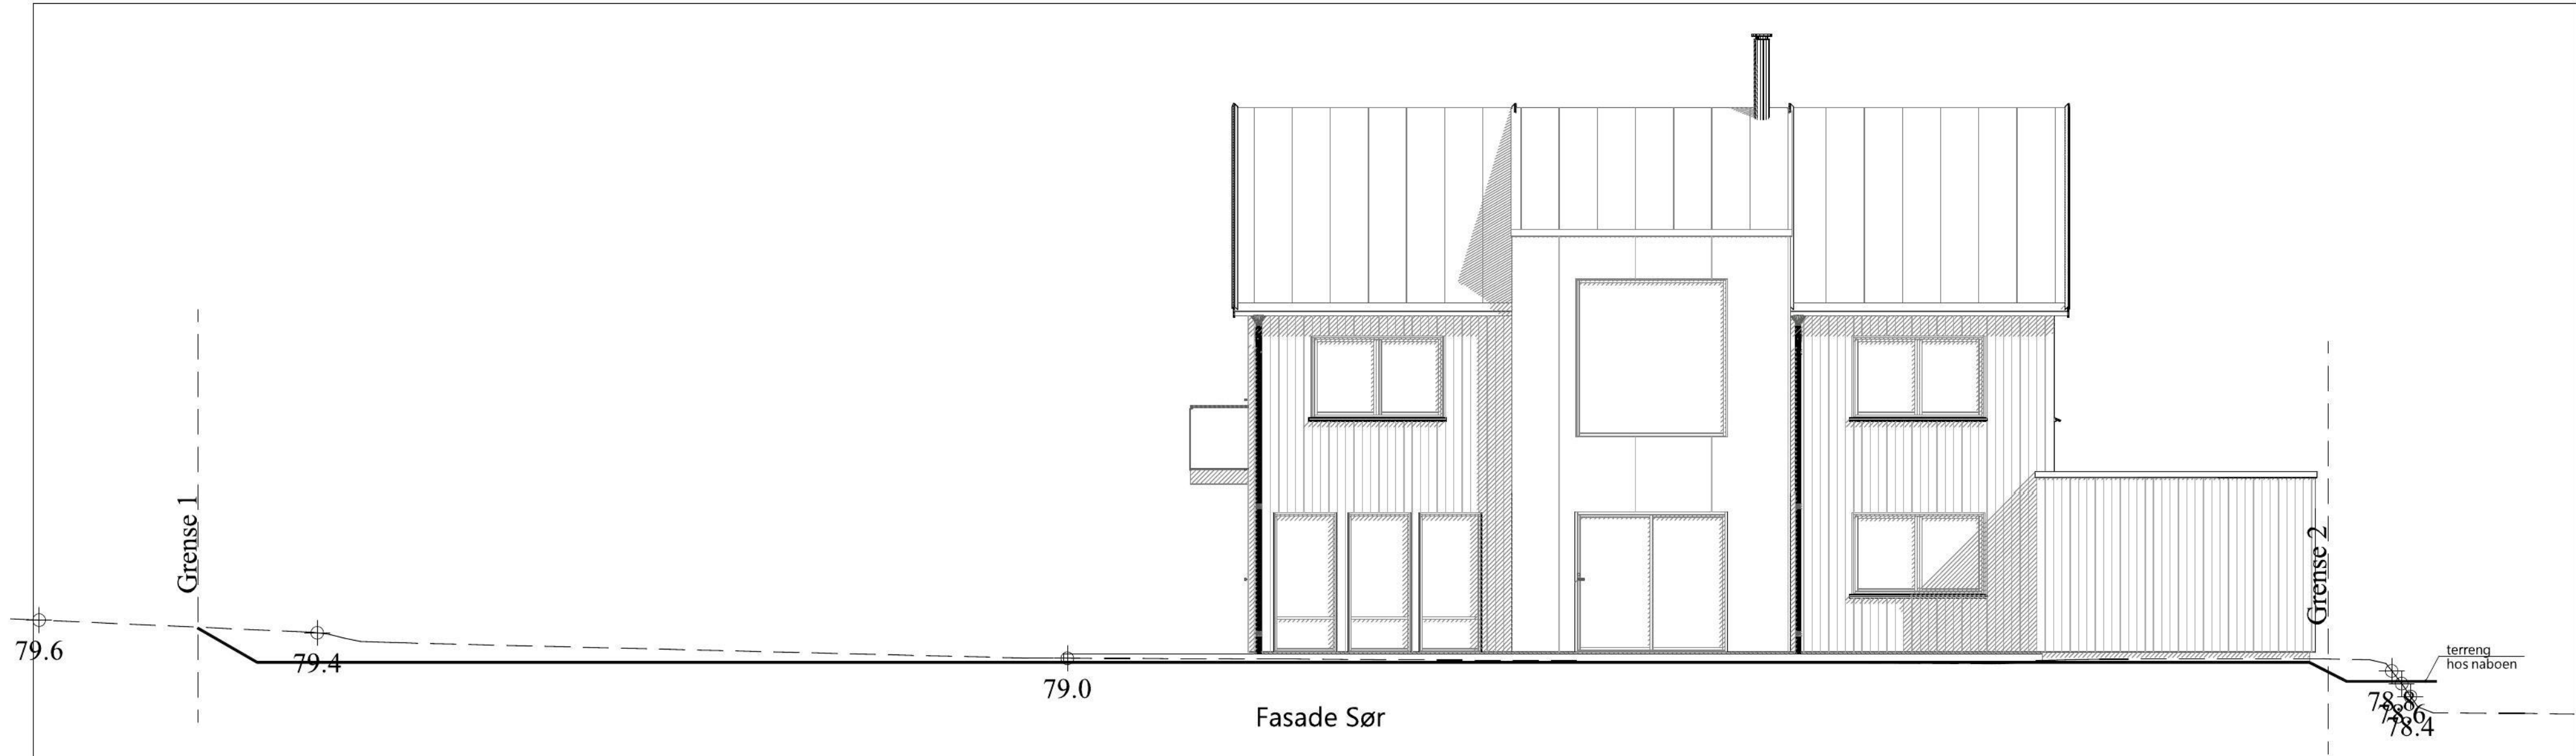

Arealberegninger i hht. NS 3940	Bruksareal BRA kvm			
	Pr etasje	Utvendig bod/garasje	Åpent over- bygg areal og carport	Sum BRA
1. etasje	96.3	7.9	24.7	128.9
2. etasje	96.3	0.0	0.0	96.3
SUM :	192.6	7.9	24.7	225.2
BYA :	112.4	0.0	36.2	148.6

— PLANERT TERRENG
- - - - - EKSISTERENDE TERRENG

B A		BM + tatt bort sport vegg v/trapp, garasjebod	REM REM	30.11.23 21.11.23
Rev.		Revisjonen gjelder:	Utført:	Kontr.
Tiltakshaver: Kristin Teigen og Mikal Klungvedt		Målestokk: 1: 100	Tegn: AG	Dato: 22.09.23
Byggeplass: Turkisveien 82			Trac:	Dato:
Kommune: Sandnes		Gnr/Bnr 61 /48	Format: A3	Sak: Fasader Sør og Øst
BYGGEFIRMA:		ARKITEKT:	Tegn.nr: 82tu1510	
 Systemhus Prosjekt hjørn siden 1967			Prosj.nr: 5130	
 Tomteutvikling AS			© Tegningen er beskyttet (iht. lov om opphavsrett).	
		 ARKITEKTON		