
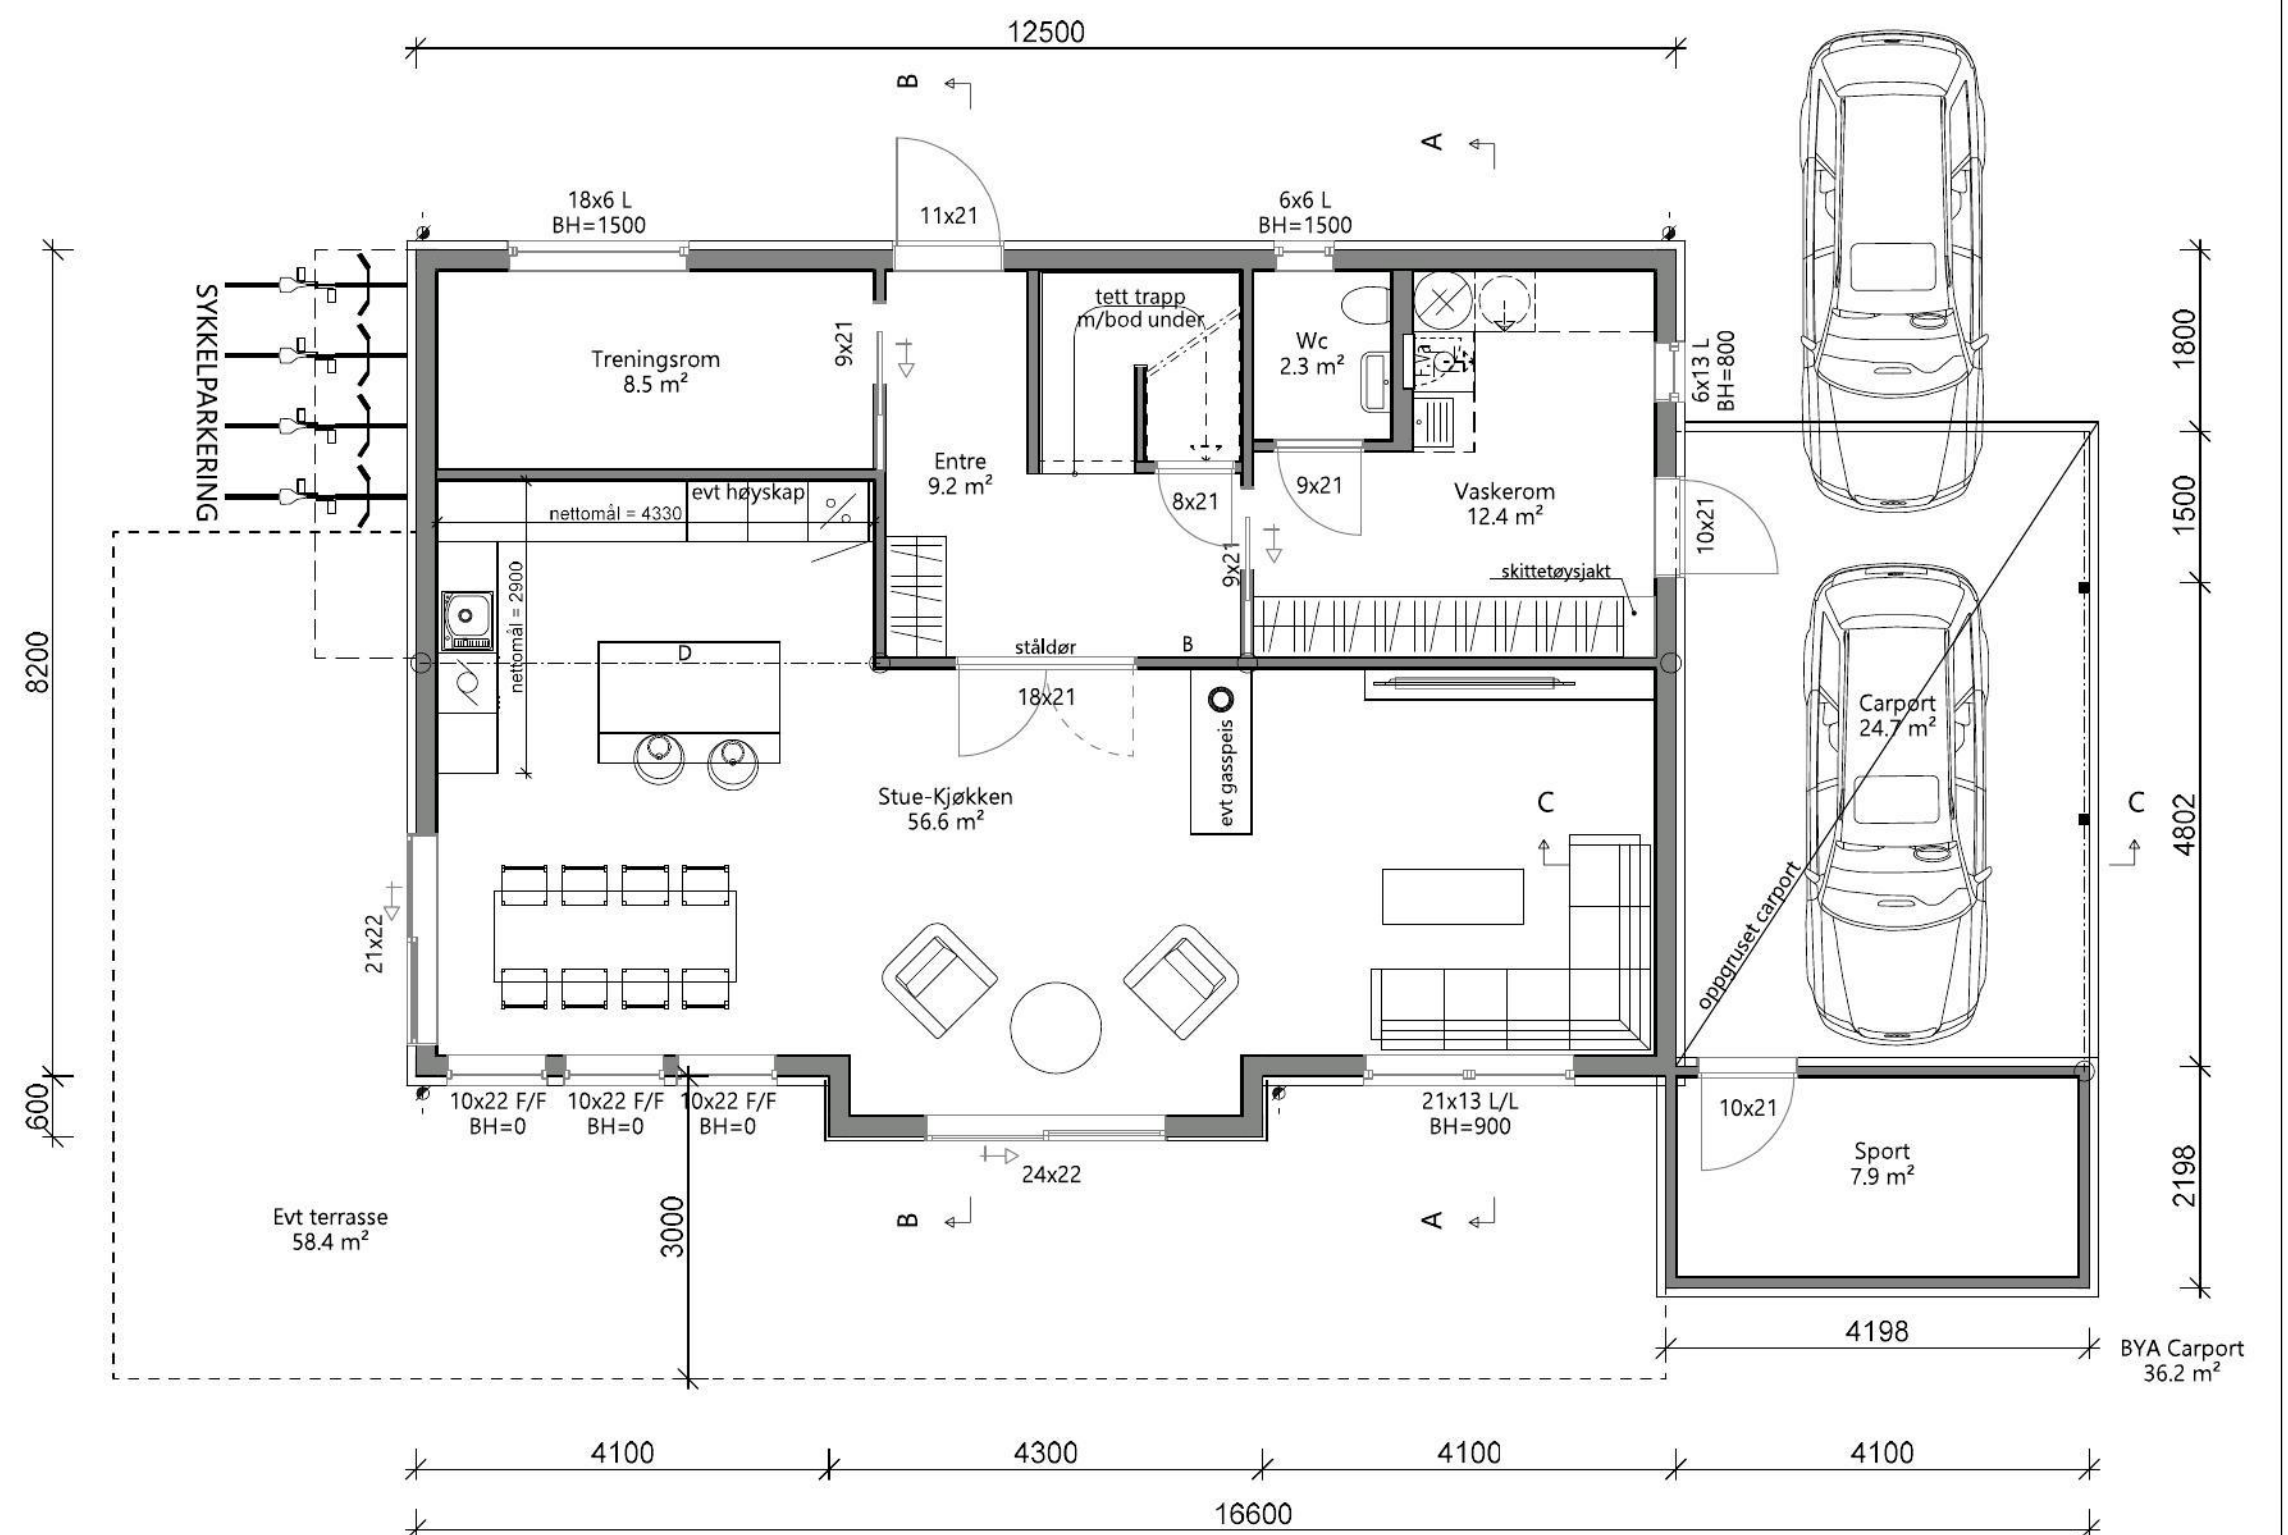


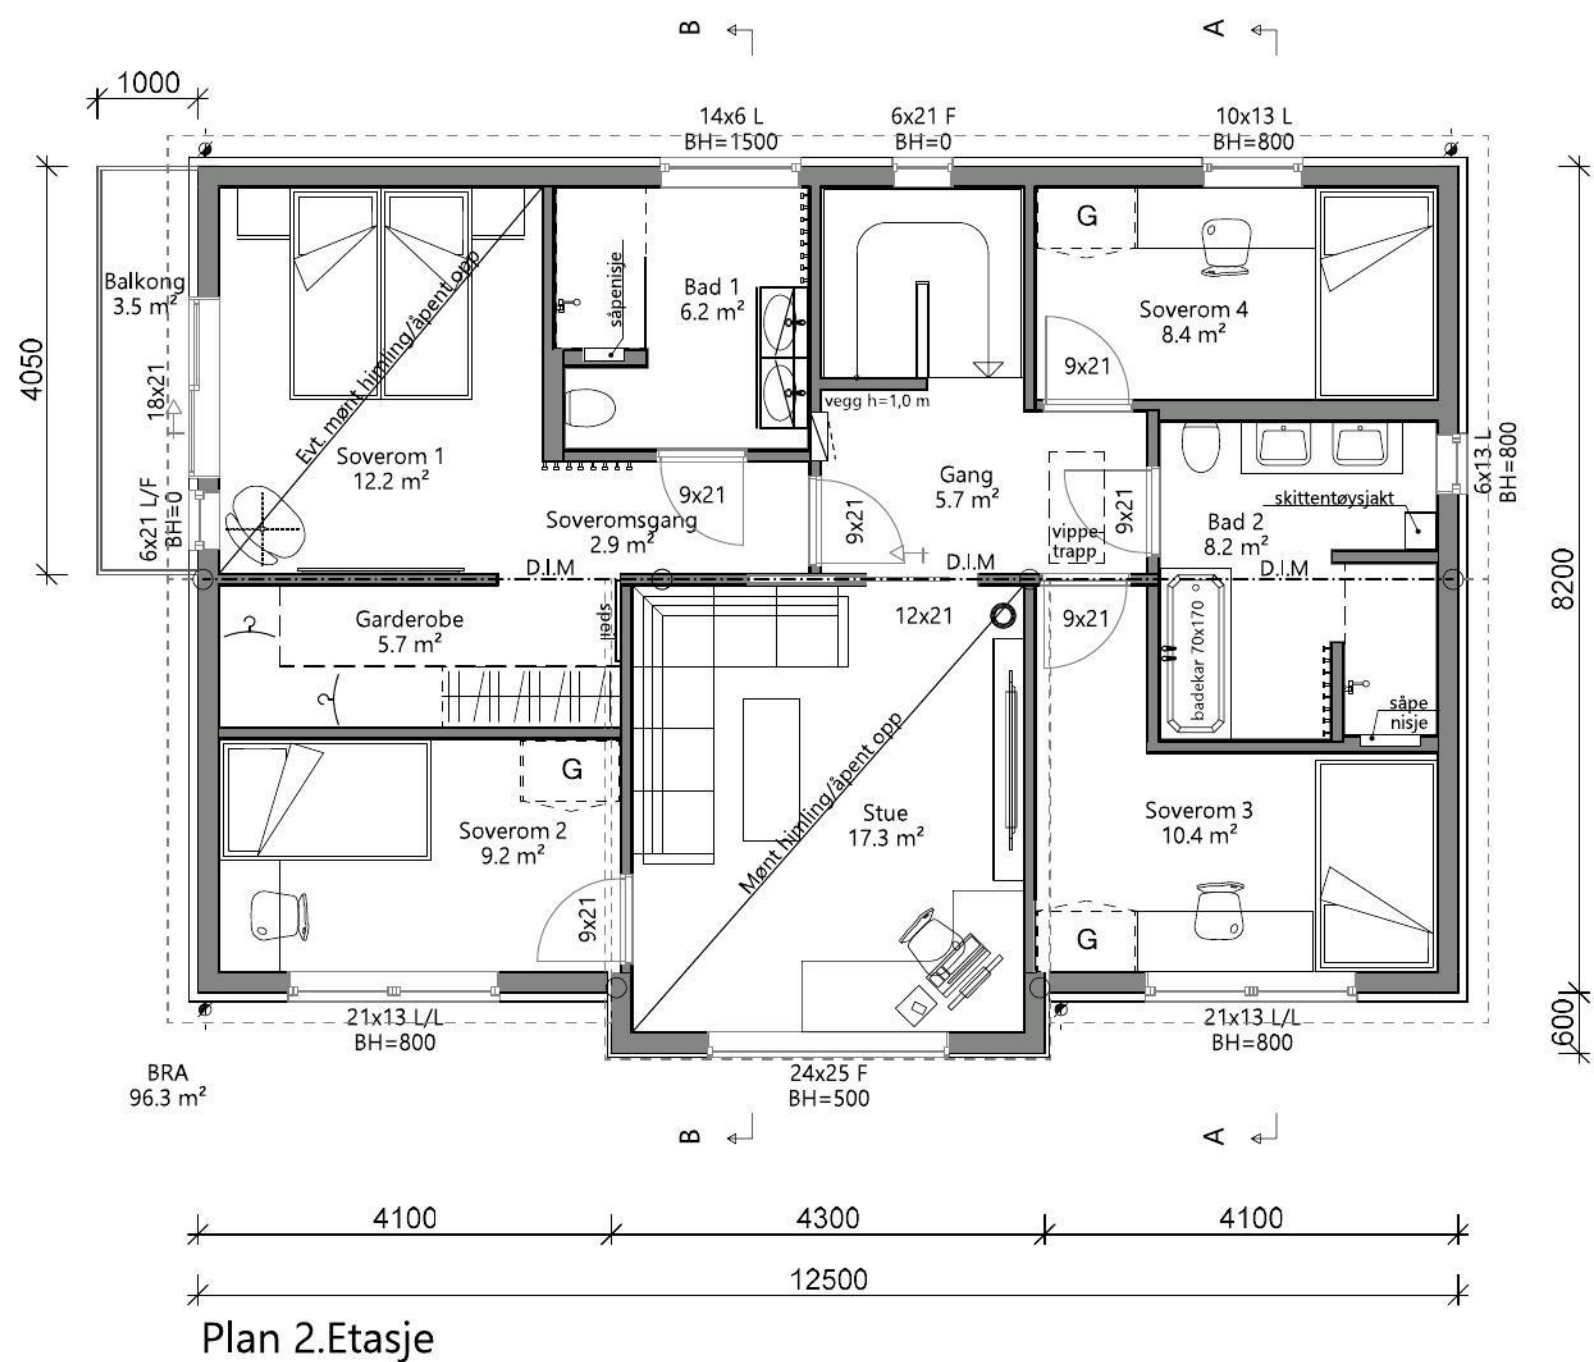

Plan 1. Etasje

BYA Bolig 112.4 m²
BRA Bolig 96.3 m²

B BM + tatt bort sport
A vegg v/trapp, garasjebod
Rev. Revisjonen gjelder: 30.11.23
REM 21.11.23
Utført: Kontr. Dato:

Tiltakshaver: Kristin Teigen og Mikal Klungvedt	Målestokk: 1:100	Tegn: AG	Dato: 22.09.23
Byggeplass: Turkisveien 82	Format: A3	Trac:	Dato:
Kommune: Sandnes	Gnr/Bnr 61 / 48	Sak: Plan 1.og 2.Etasje	
BYGGEFIRMA: Tomteutvikling AS	ARKITEKT: ARKITEKTON	Tegn.nr: 82tu1501	Prosj.nr: 5130