


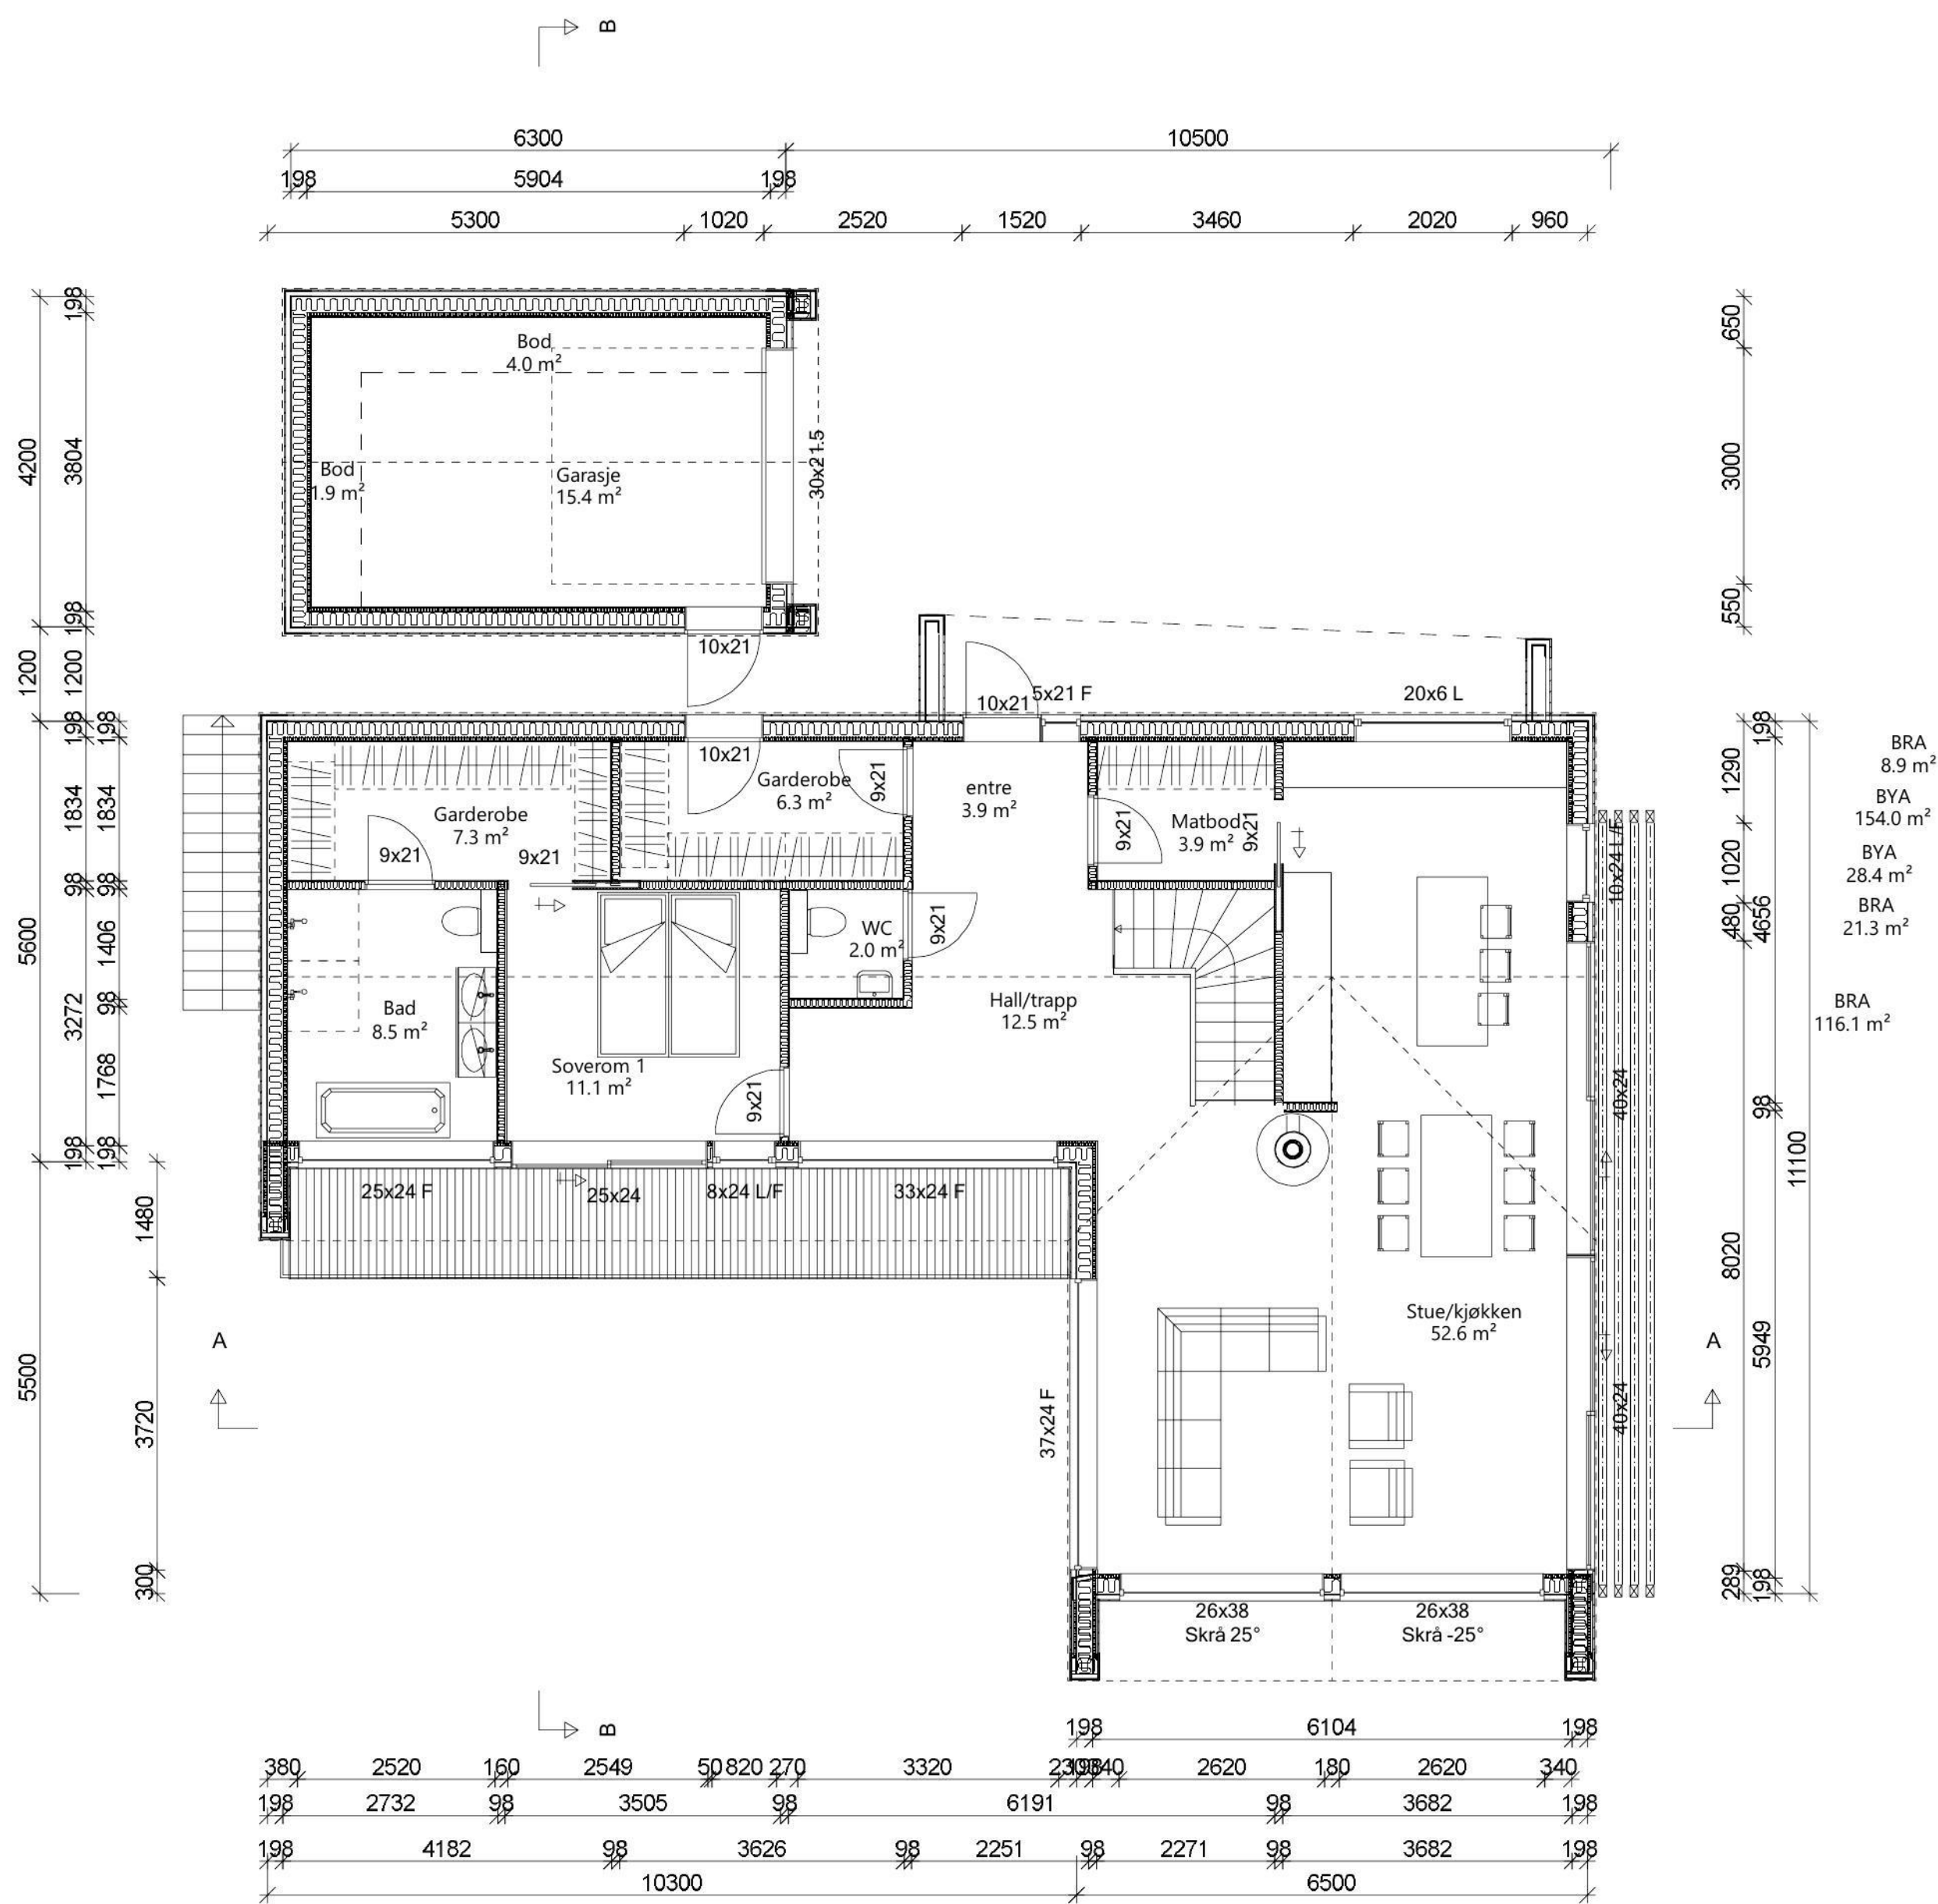

Arealberegninger i hht. NS 3940	Bruksareal BRA kvm			Sum BRA
	Pr etasje	Utvendig bod/garasje	Åpent over- bygd areal og carport	
Underetasje	110.0	0.0	0.0	110.0
1. etasje	116.0	21.3	8.9	146.2
SUM :	226.0	21.3	8.9	256.2
BYA :	154.0	28.4	0.0	182.4

A		vinduer/målseting	Gosia	20.10.23
REV.	ANT.	REVIDERINGEN GJELDER	SIGN.	DATO

DATA DESIGN SYSTEM

Vardåsveien 145		Kenneth Lomeland		G.NR. 56		B.NR. 299	
1. etasje				KOMMUNE:			
 Flatnes Bygg Consult				TEGN. Gosia		PROSJ.NR. 2562	
				GODKJ.			
				MÅL 1 : 100		TEGN. NR. 501	
				DATO 20.09.23			
TEGNINGEN MÅ HVERKEN HELT ELLER DELVIS KOPIERES ELLER BENYTTES TIL UTFØRELSE AV ARBEID SOM FLATNES BYGG CONSULT AS IKKE MEDVIRKER I							