


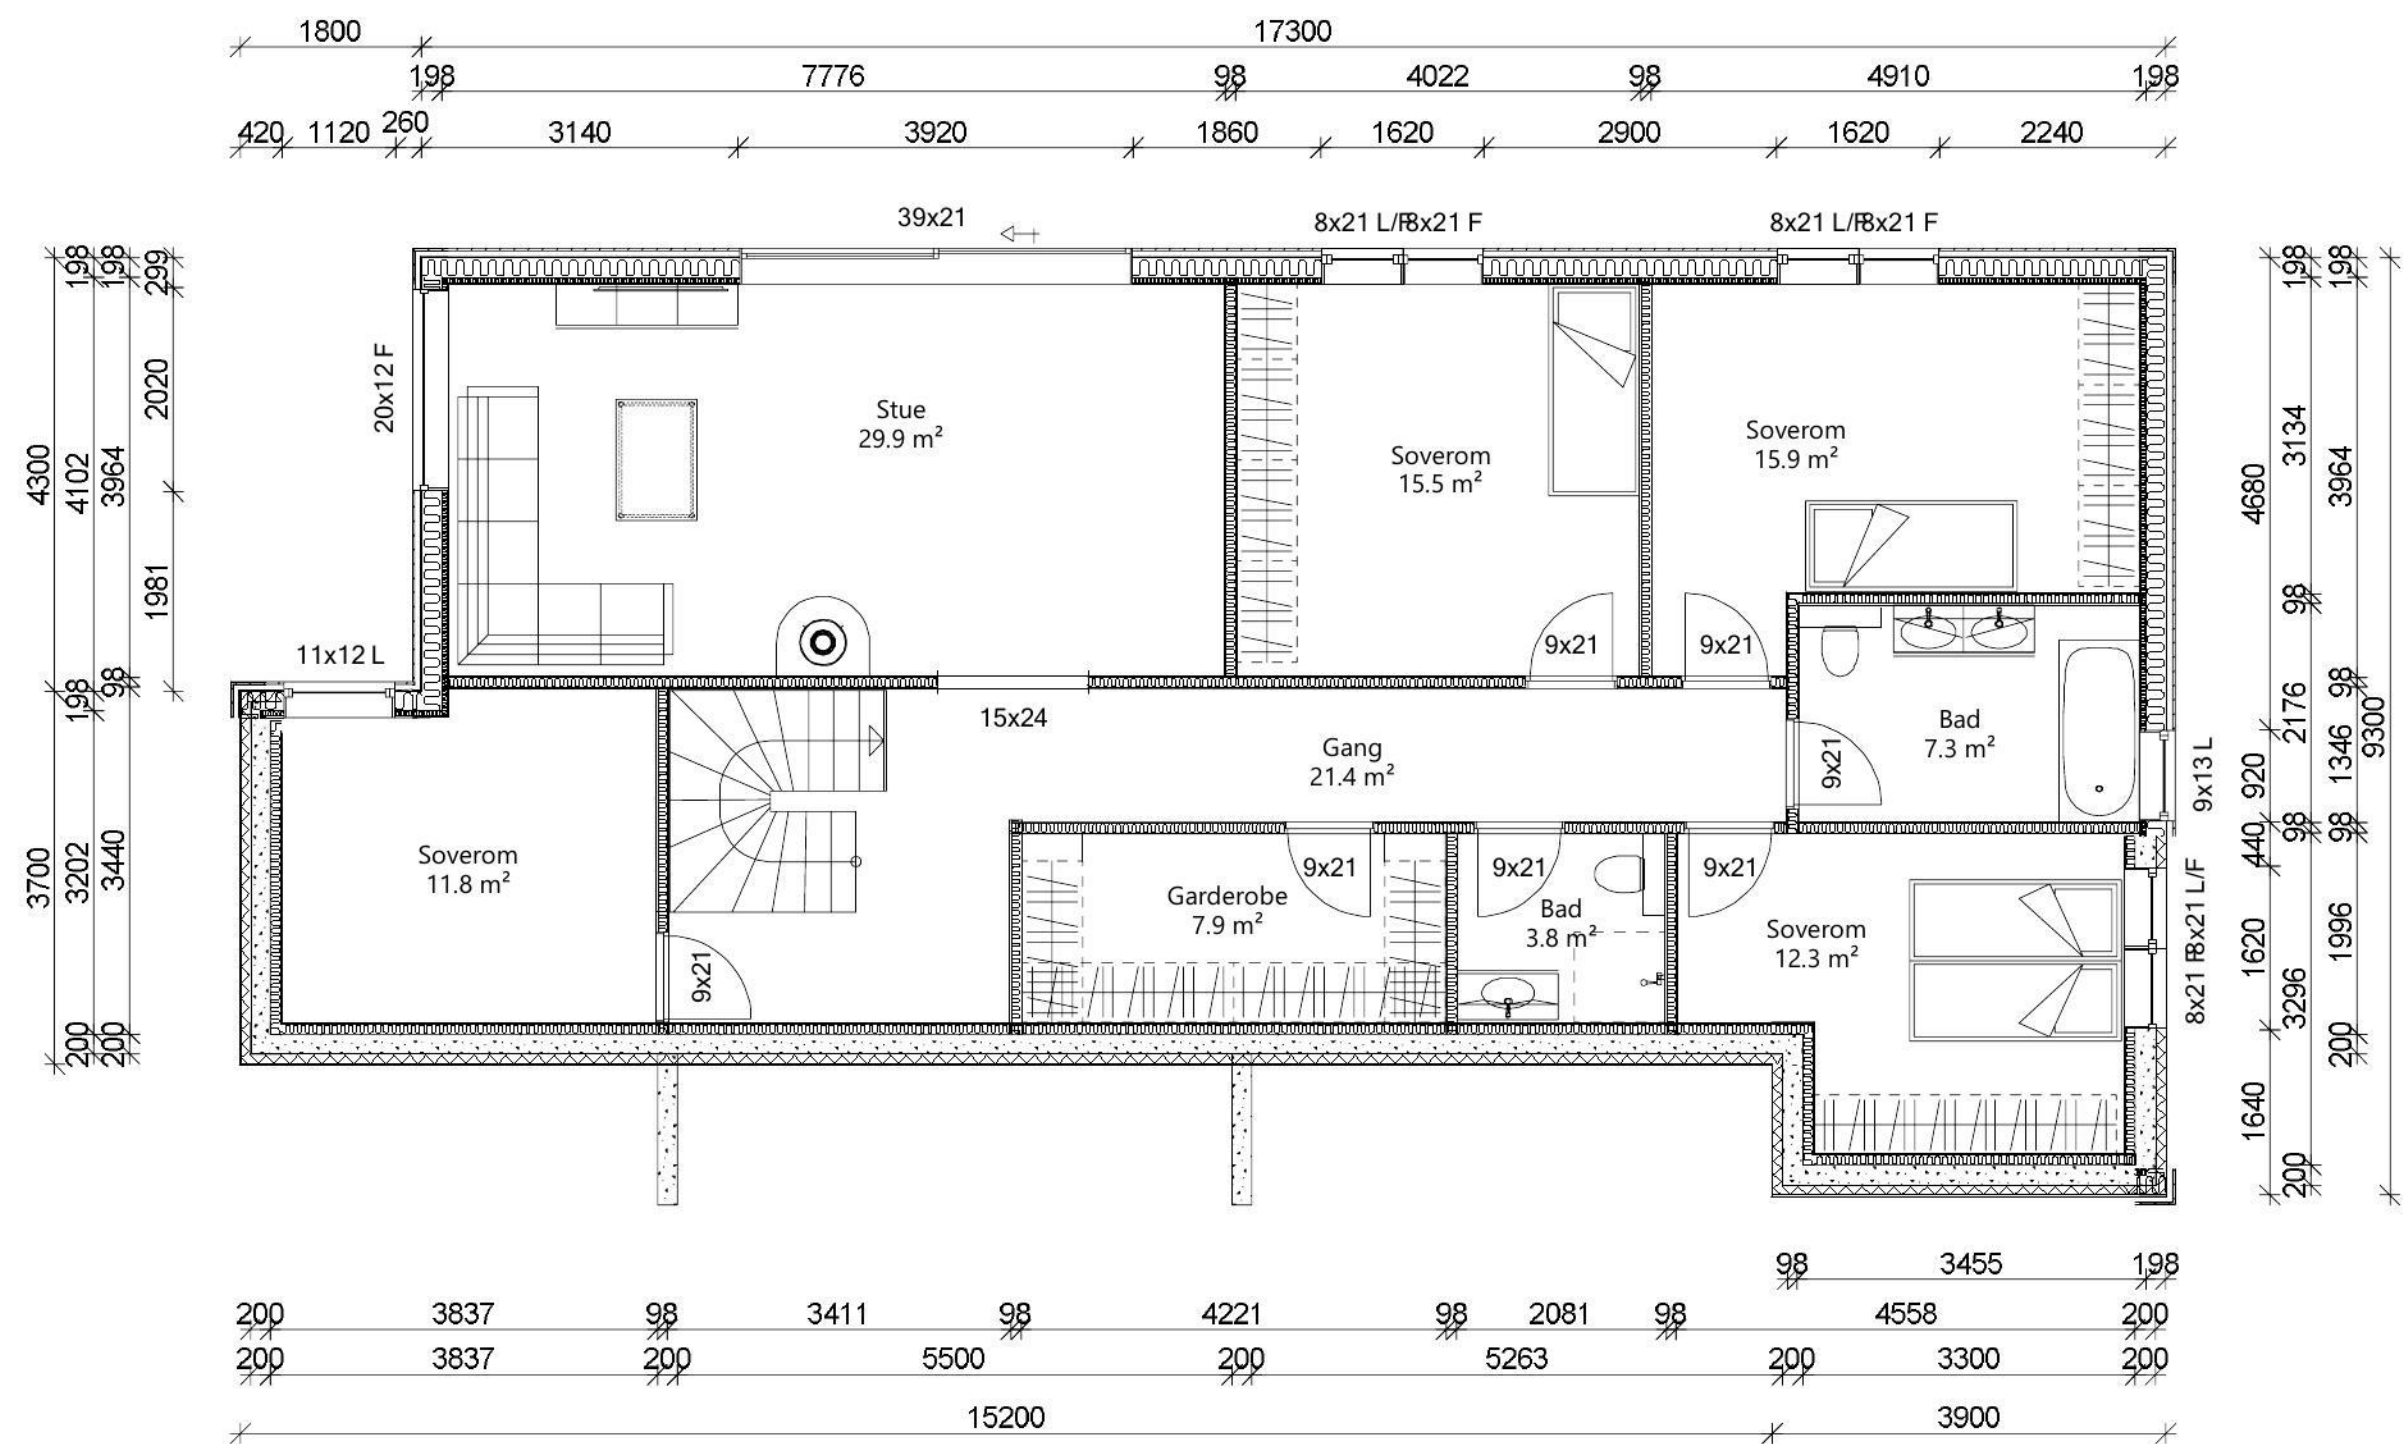

B	vinduer	Gosia	02.10.23
A	diverse	Gosia	02.08.23
REV.	ANT.	REVIDERINGEN GJELDER	SIGN. DATO

DATA DESIGN SYSTEM

Malwina Ciula-Poltorak og Piotr Poltorak

G.NR. 47
B.NR. 675

Under etasje

Vedderheia 175

KOMMUNE: Kristiansand



Flatnes Bygg Consult

TEGN. Gosia

GODKJ.

MÅL 1 : 100

DATO 05.06.23

PROSJ.NR.

2553

TEGN. NR.

500

TEGNINGEN MÅ HVERKEN HELT ELLER DELVIS KOPIERES ELLER BENYTTES TIL ANDRE UTFØRELSE AV ARBEID SOM FLATNES BYGG CONSULT AS IKKE MEDVIRKER I