


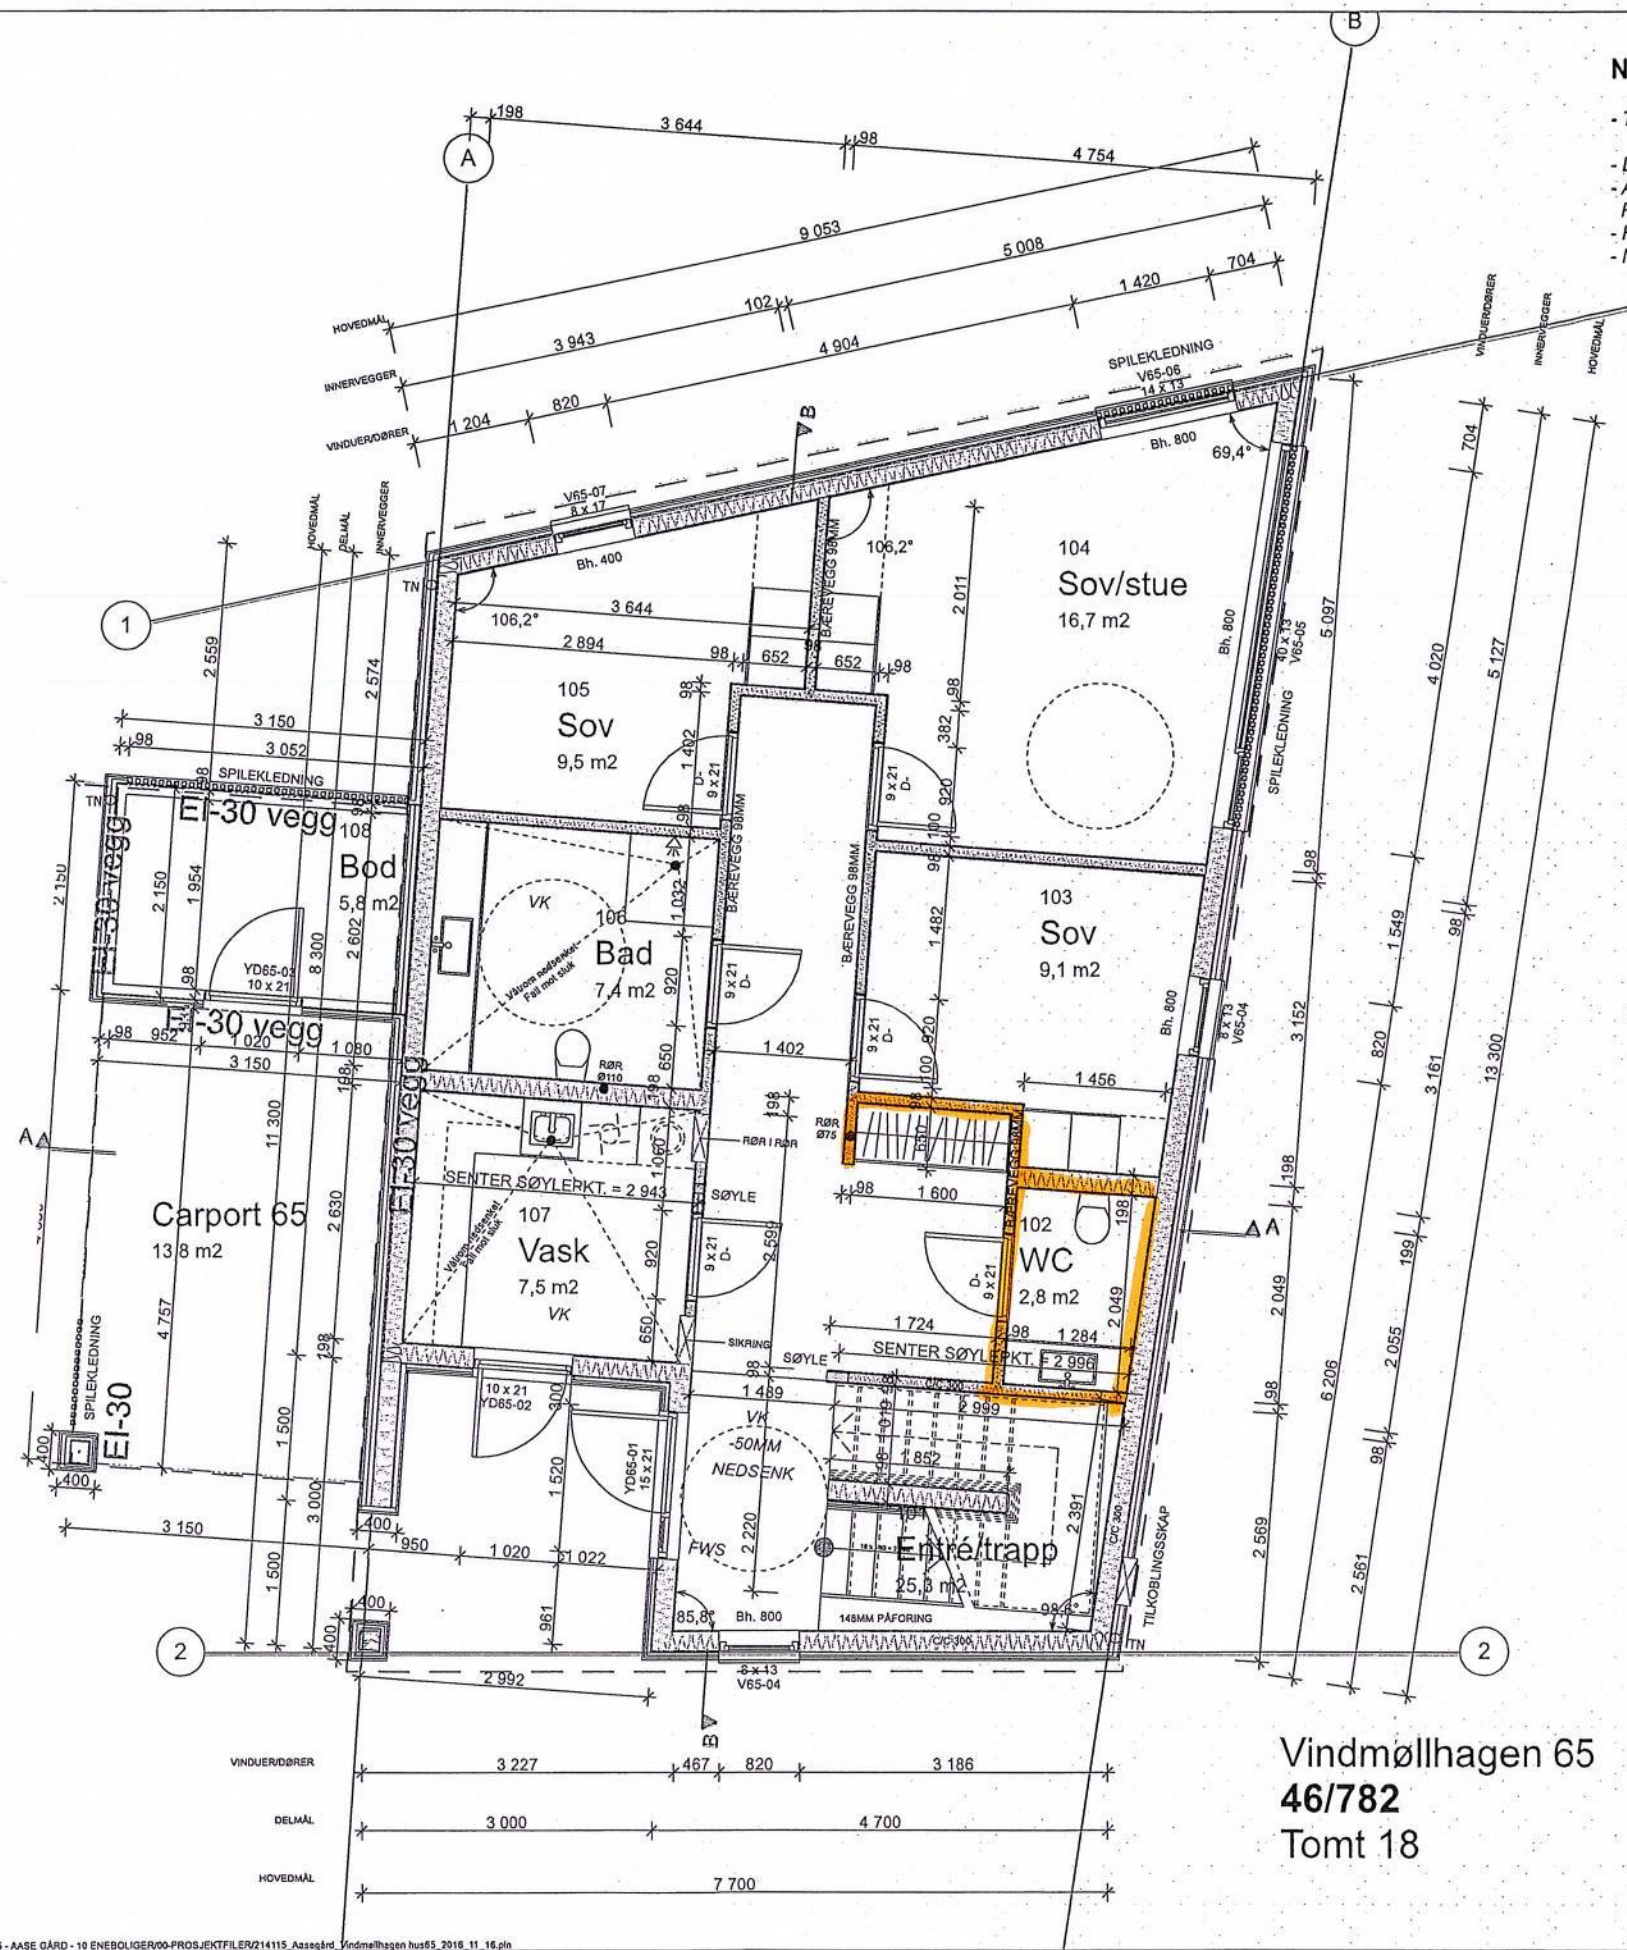

NB!

- TILGJENGELIG BOLIG

- DET HENVISES TIL STATISKE BEREGNINGER FRA OPTIMERA
- ALLE TRAPPER MÅ HA BREDDE 2150MM OG C/C 300 RUNDT REPOS
- HIMLING I BAD 2.ETG: 2400MM
- NEDSENKET GULV I VÅTROM M/ FALL

Vindmøllhagen 65
46/782
Tomt 18

0	16.11.2016	Arbeidstegning	NK	
Index	Dato	Beskrivelse	Sign	Kontr.
Marknadert nordpil				
				
ARKVEST AS		Storgt. 48 4304 Sandnes TELEFON: 51 68 12 40 E-post: post@arkvest.no www.arkvest.no		
Fase: Arbeidstegning		Arkitekt: K.D. Tegnet av: K.O.J.E.F.N.K. ###		
Prosjekt: Stolt Prosjekt AS Aase Gård Vindmøllhagen 65, GNR46/BNR782				
Tittel: Plan 1. Etasje				
Mål:	Dato:	Saksnr:	Tegningsnr:	Rev:
1:50	16.11.16	214115	A22-1093	0
Alle rettigheter forbeholdt. Arkitekt AS, tegning eller bruk av disse tegningene er forbudt uten skriftlig samtykke.				
				A2