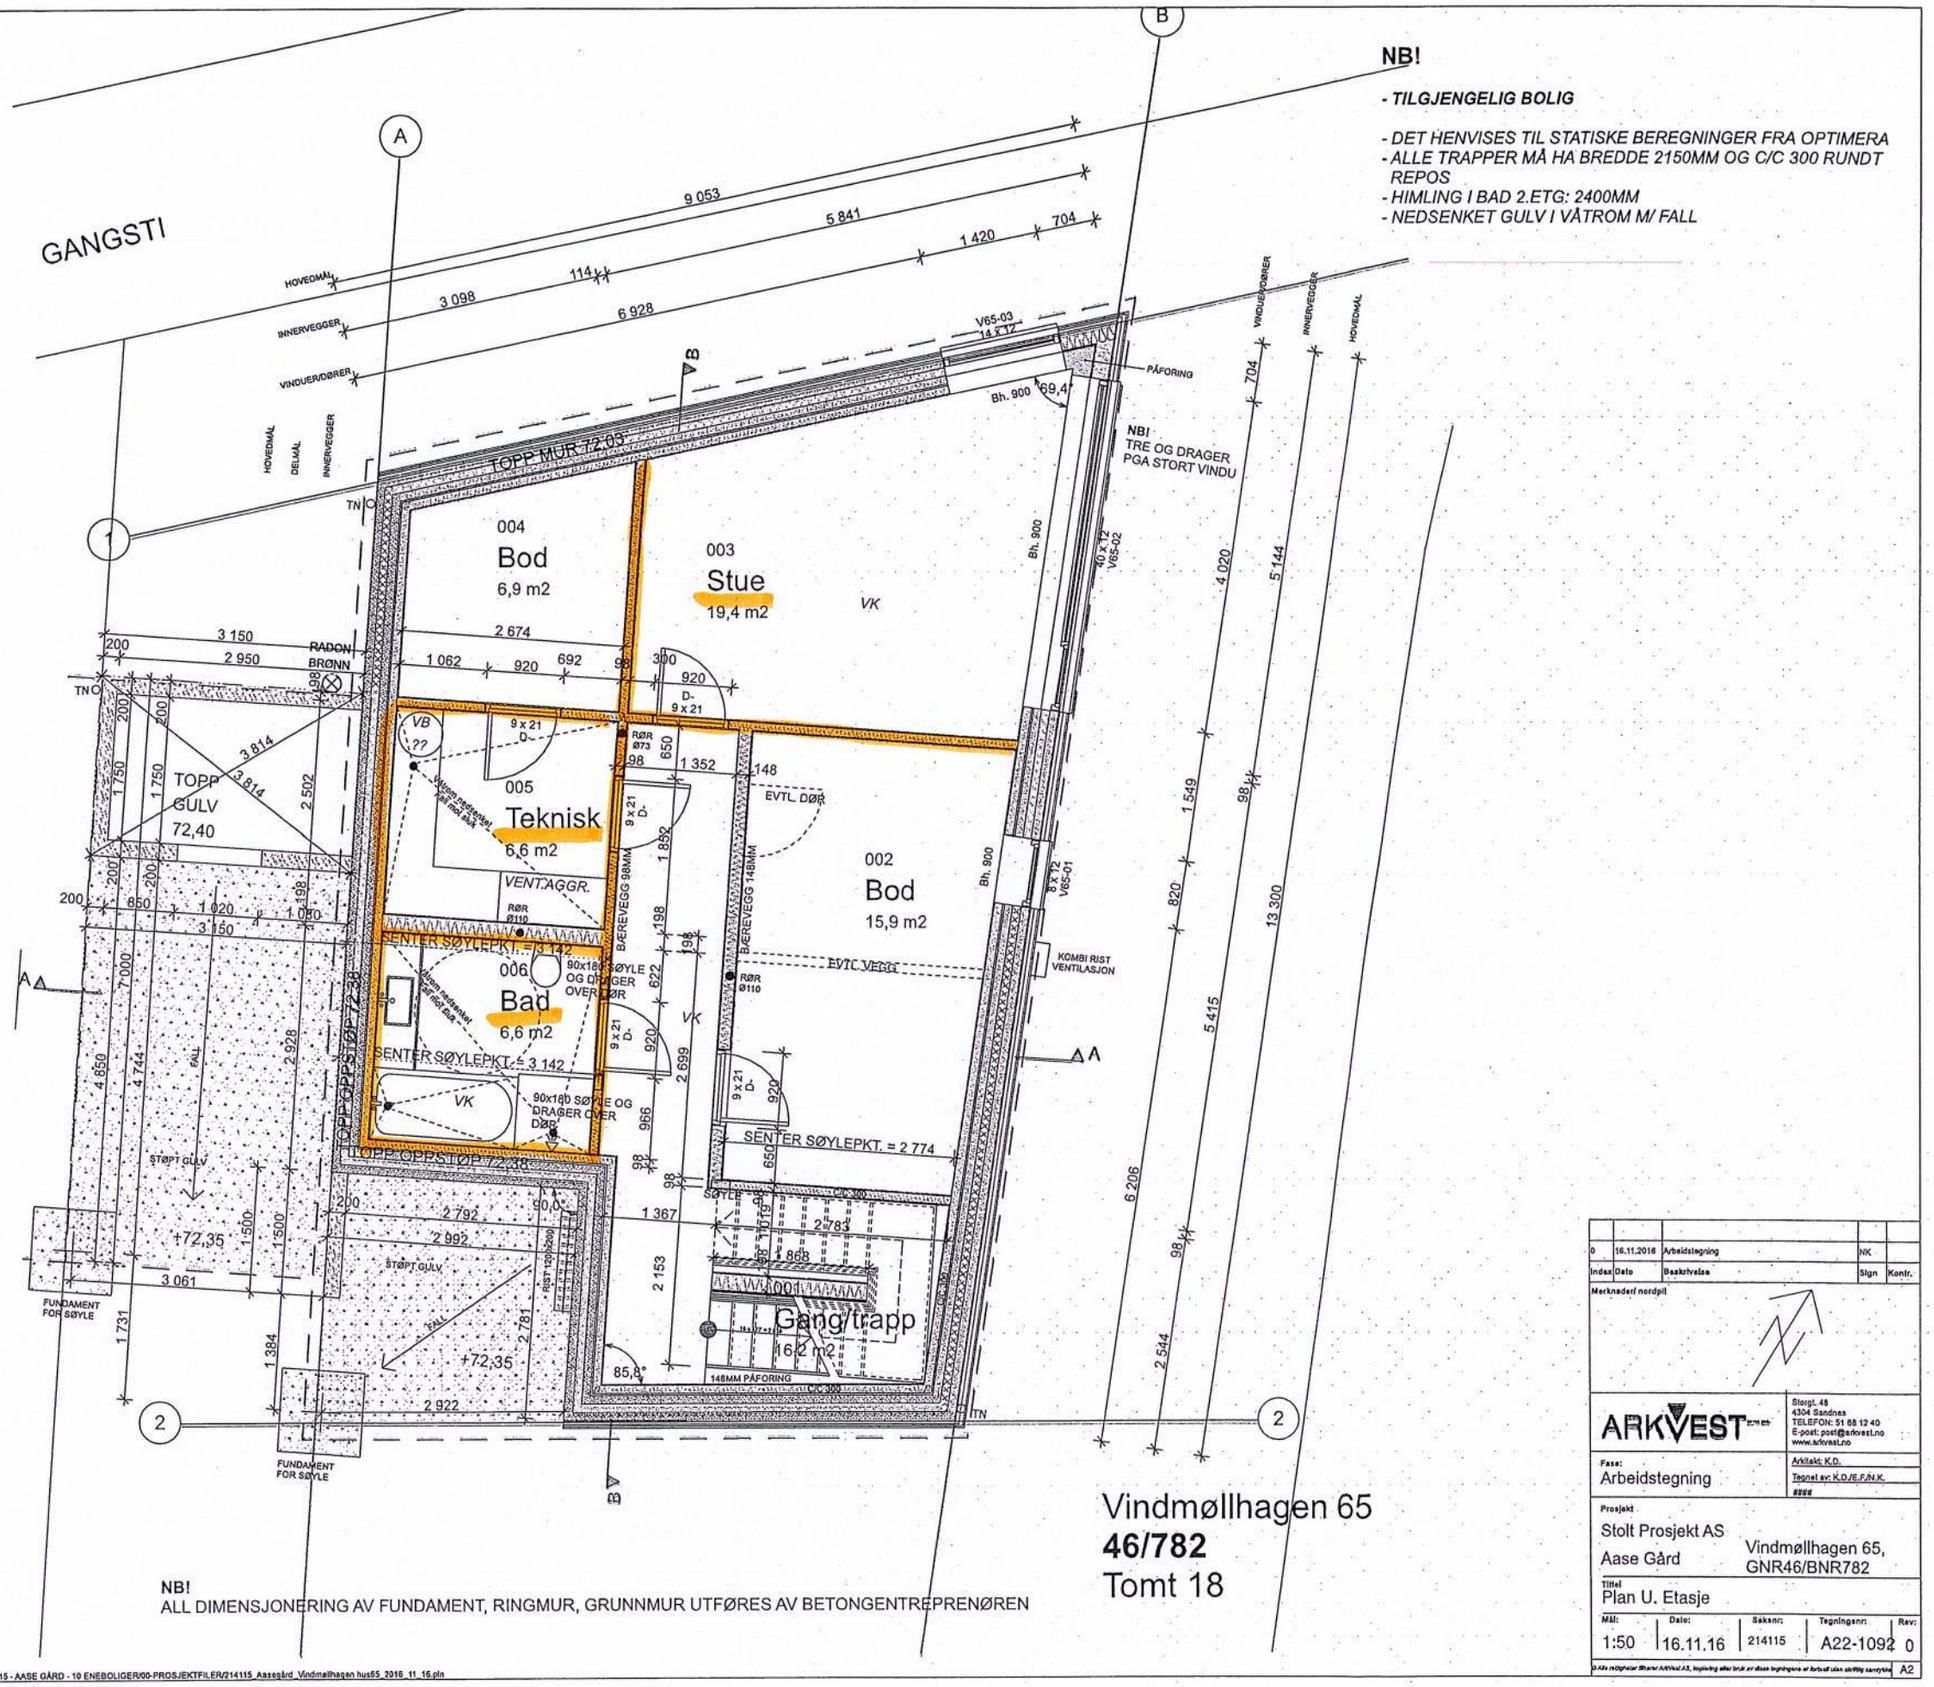


Index	Dato	Beskrivelse	Sign	Kontr.
0	16.11.2016	Arbeidstegning	NK	

Merknader/ nordpil

ARKVEST
Storgt. 48
4304 Sandnes
TELEFON: 51 68 12 40
E-post: post@arkvest.no
www.arkvest.no

Fase: Arbeidstegning

Arkitekt: K.D.
Tegnet av: K.D./E.F./N.K.

Prosjekt:
Stolt Prosjekt AS
Aase Gård
Vindmøllhagen 65, GNR46/BNR782

Tittel
Plan U. Etasje

Mål:	Dato:	Saksnr:	Tegningsnr:	Rev:
1:50	16.11.16	214115	A22-1092	0

© Alle rettigheter tilhører ArkVest AS, kopiering eller bruk av disse tegningene er forbudt uten skriftlig samtykke

A2

BIM model ArchiCAD 16 NOR Filplassering: /Volumes/ArkVestBryna/05 DIV. PROSJEKTER/214115 - AASE GÅRD - 10 ENEBOLIGER/00-PROSJEKTFILER/214115_Aasegård_Vindmøllhagen hus65_2016_11_16.pln