


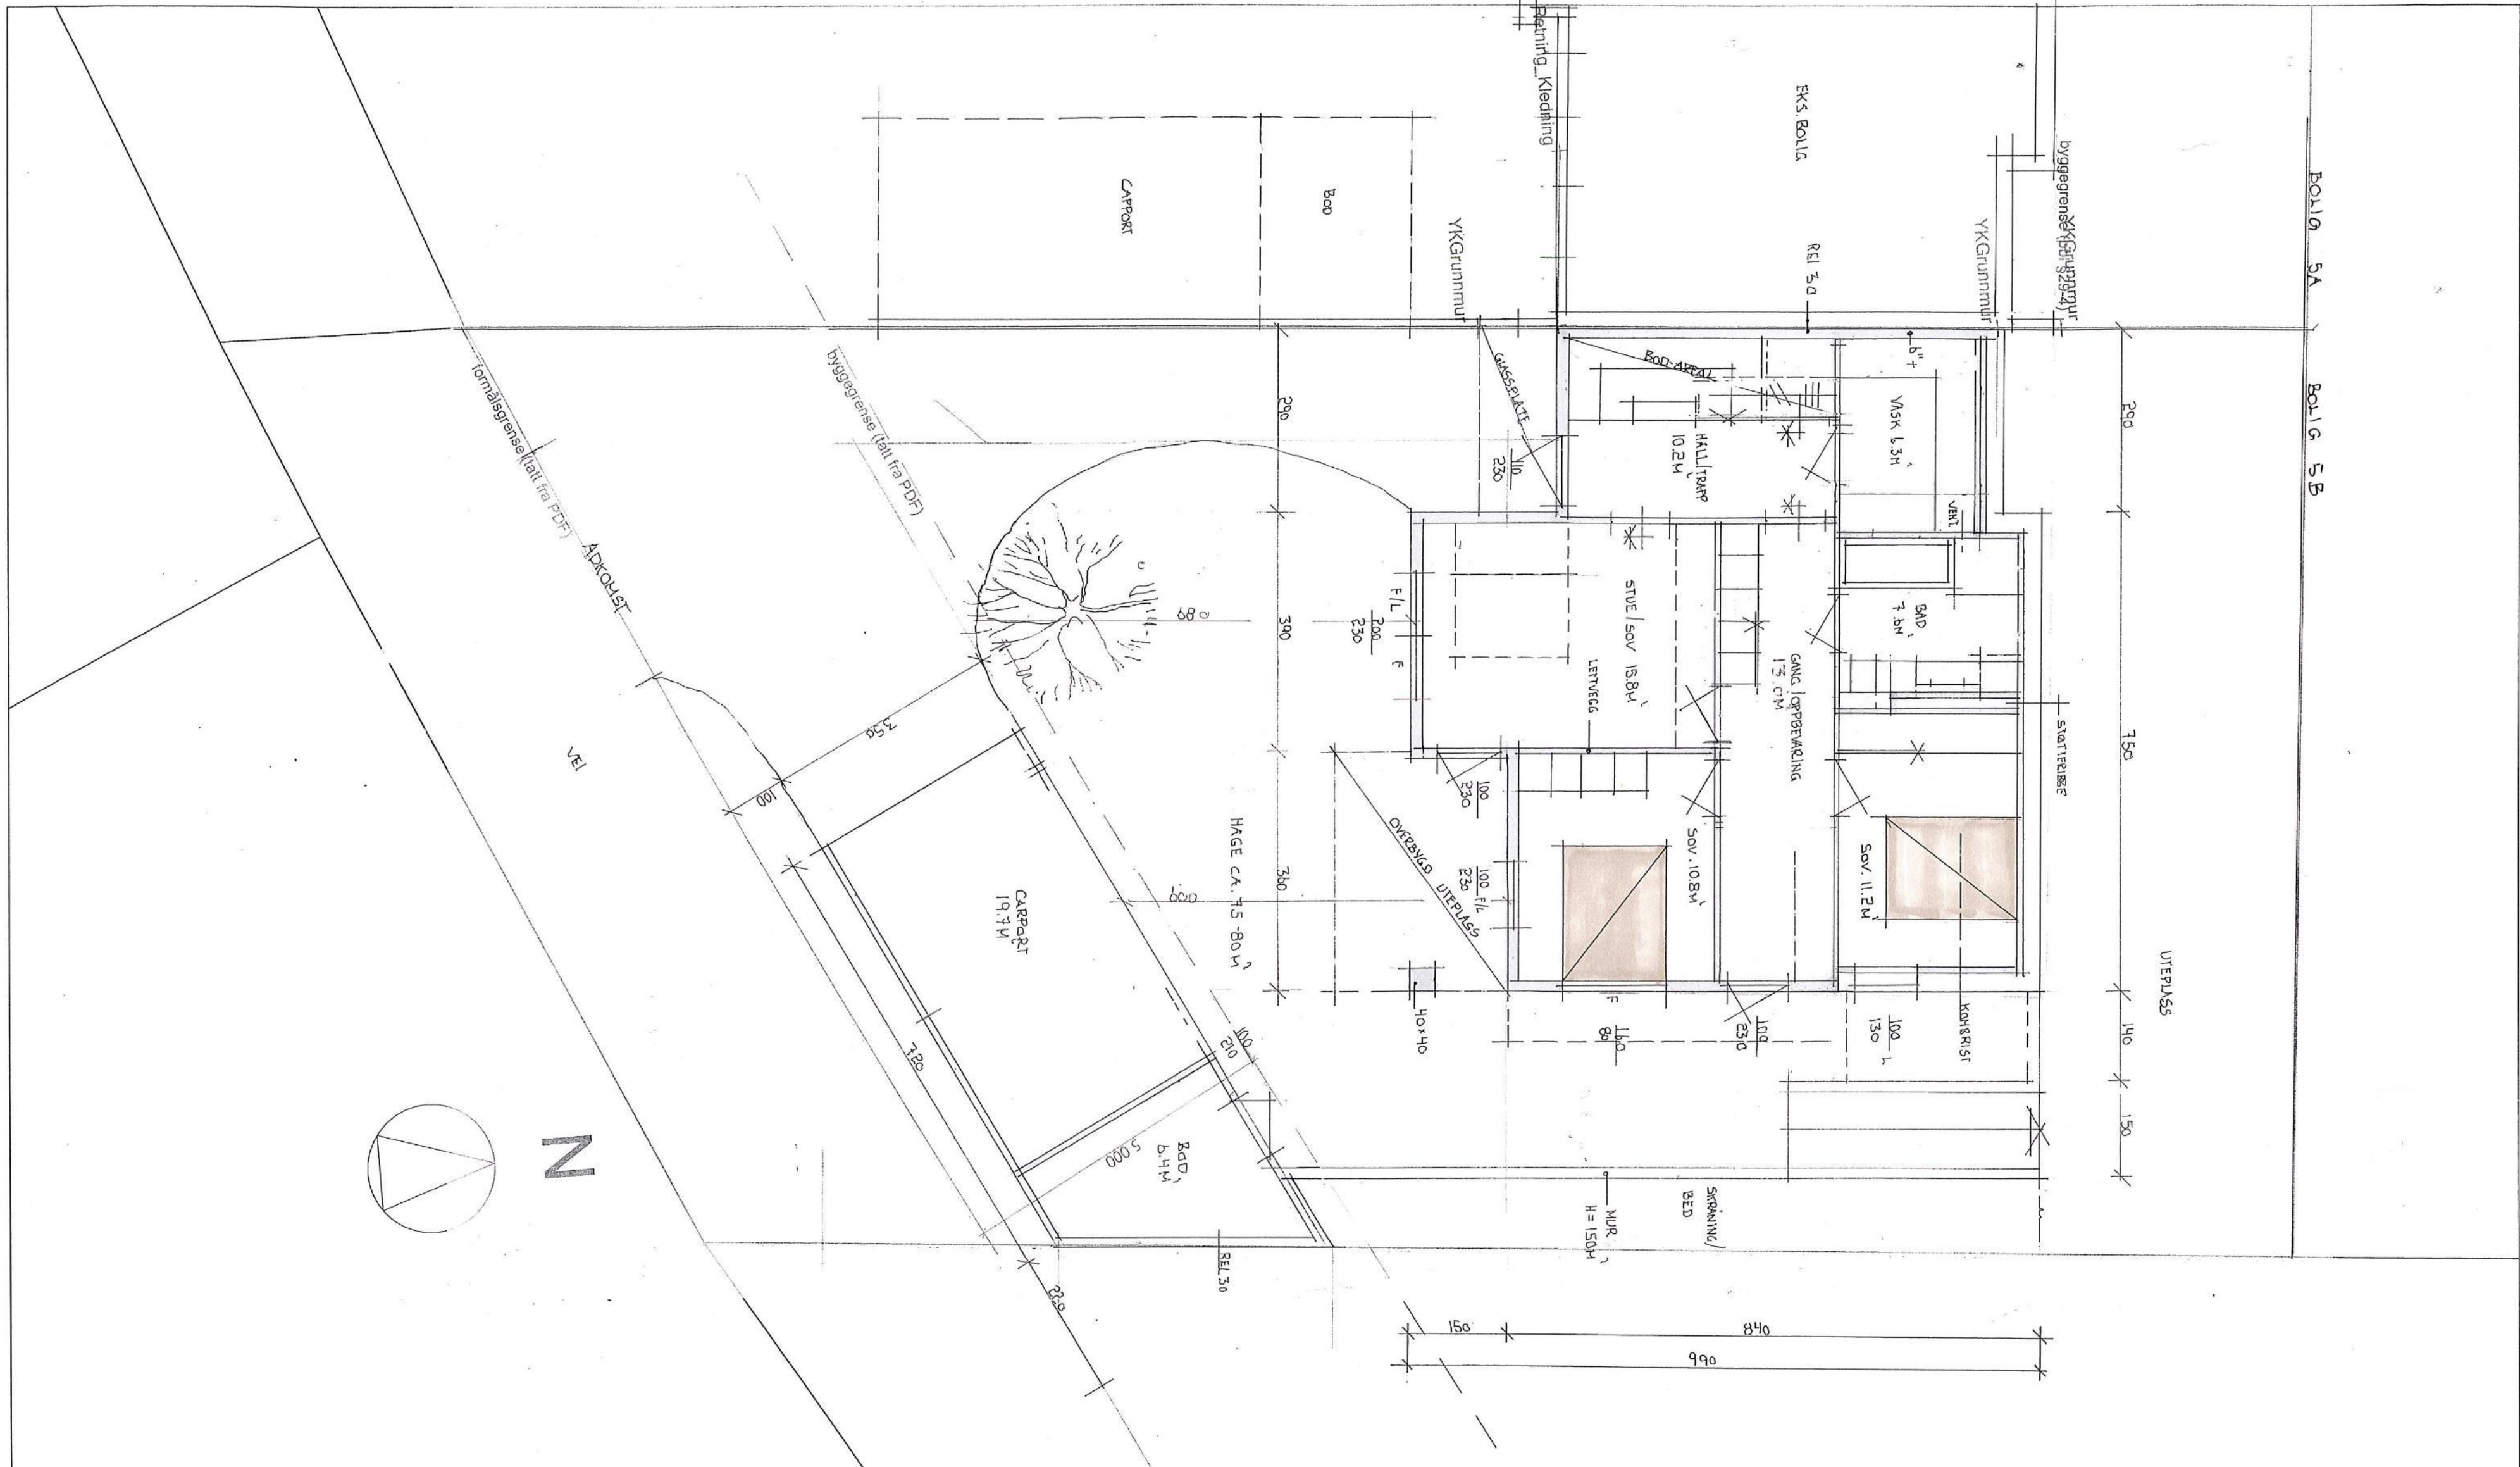

DET VIL BLI SENDT INN SØKNAD PÅ BOLIG SA PÅ ET SENERE TIDSPUNKT.
REF. SAMTALE MED KRISTIAN HÅRESDAD 22.01.24

Areal (BYA)		Areal (BRA)	
eks. bolig rives (26,5 % BYA)	95 m ²	U.etasje + 1. etasje	167,1 m ²
ny bolig	101,4 m ²		
SUM (BYA)	101,4 m ²	SUM (BRA)	167,1 m ²
% BYA (maks 20 %)	28,3 %		
ny carport/bod (maks 30 m ²)	30,0 m ²	carport / bod	26,4 m ²
netto tomt (brutto = 417 m ²)	359,0 m ²		

FJOGSTAD
Etablert 1903
HUS

Byggherre:			
JANE KR. OG ARNE BAKKEN			
Byggplass:			
VIPEVEIEN 5 B			
Ark:	B.nr.:	B.nr.:	
KVT			
Tegner:	Prosjekt nr.:		
Målestokk:	Tegning:		
1:100			
Dato:	Tegningsnummer:		Rev.:
22.11.23			