


Situasjonskart

Eiendom: 47/308
Adresse: Vipeveien 5B
Dato: 07.11.2023
Målestokk: 1:500



UTM-32

Sandnes kommune

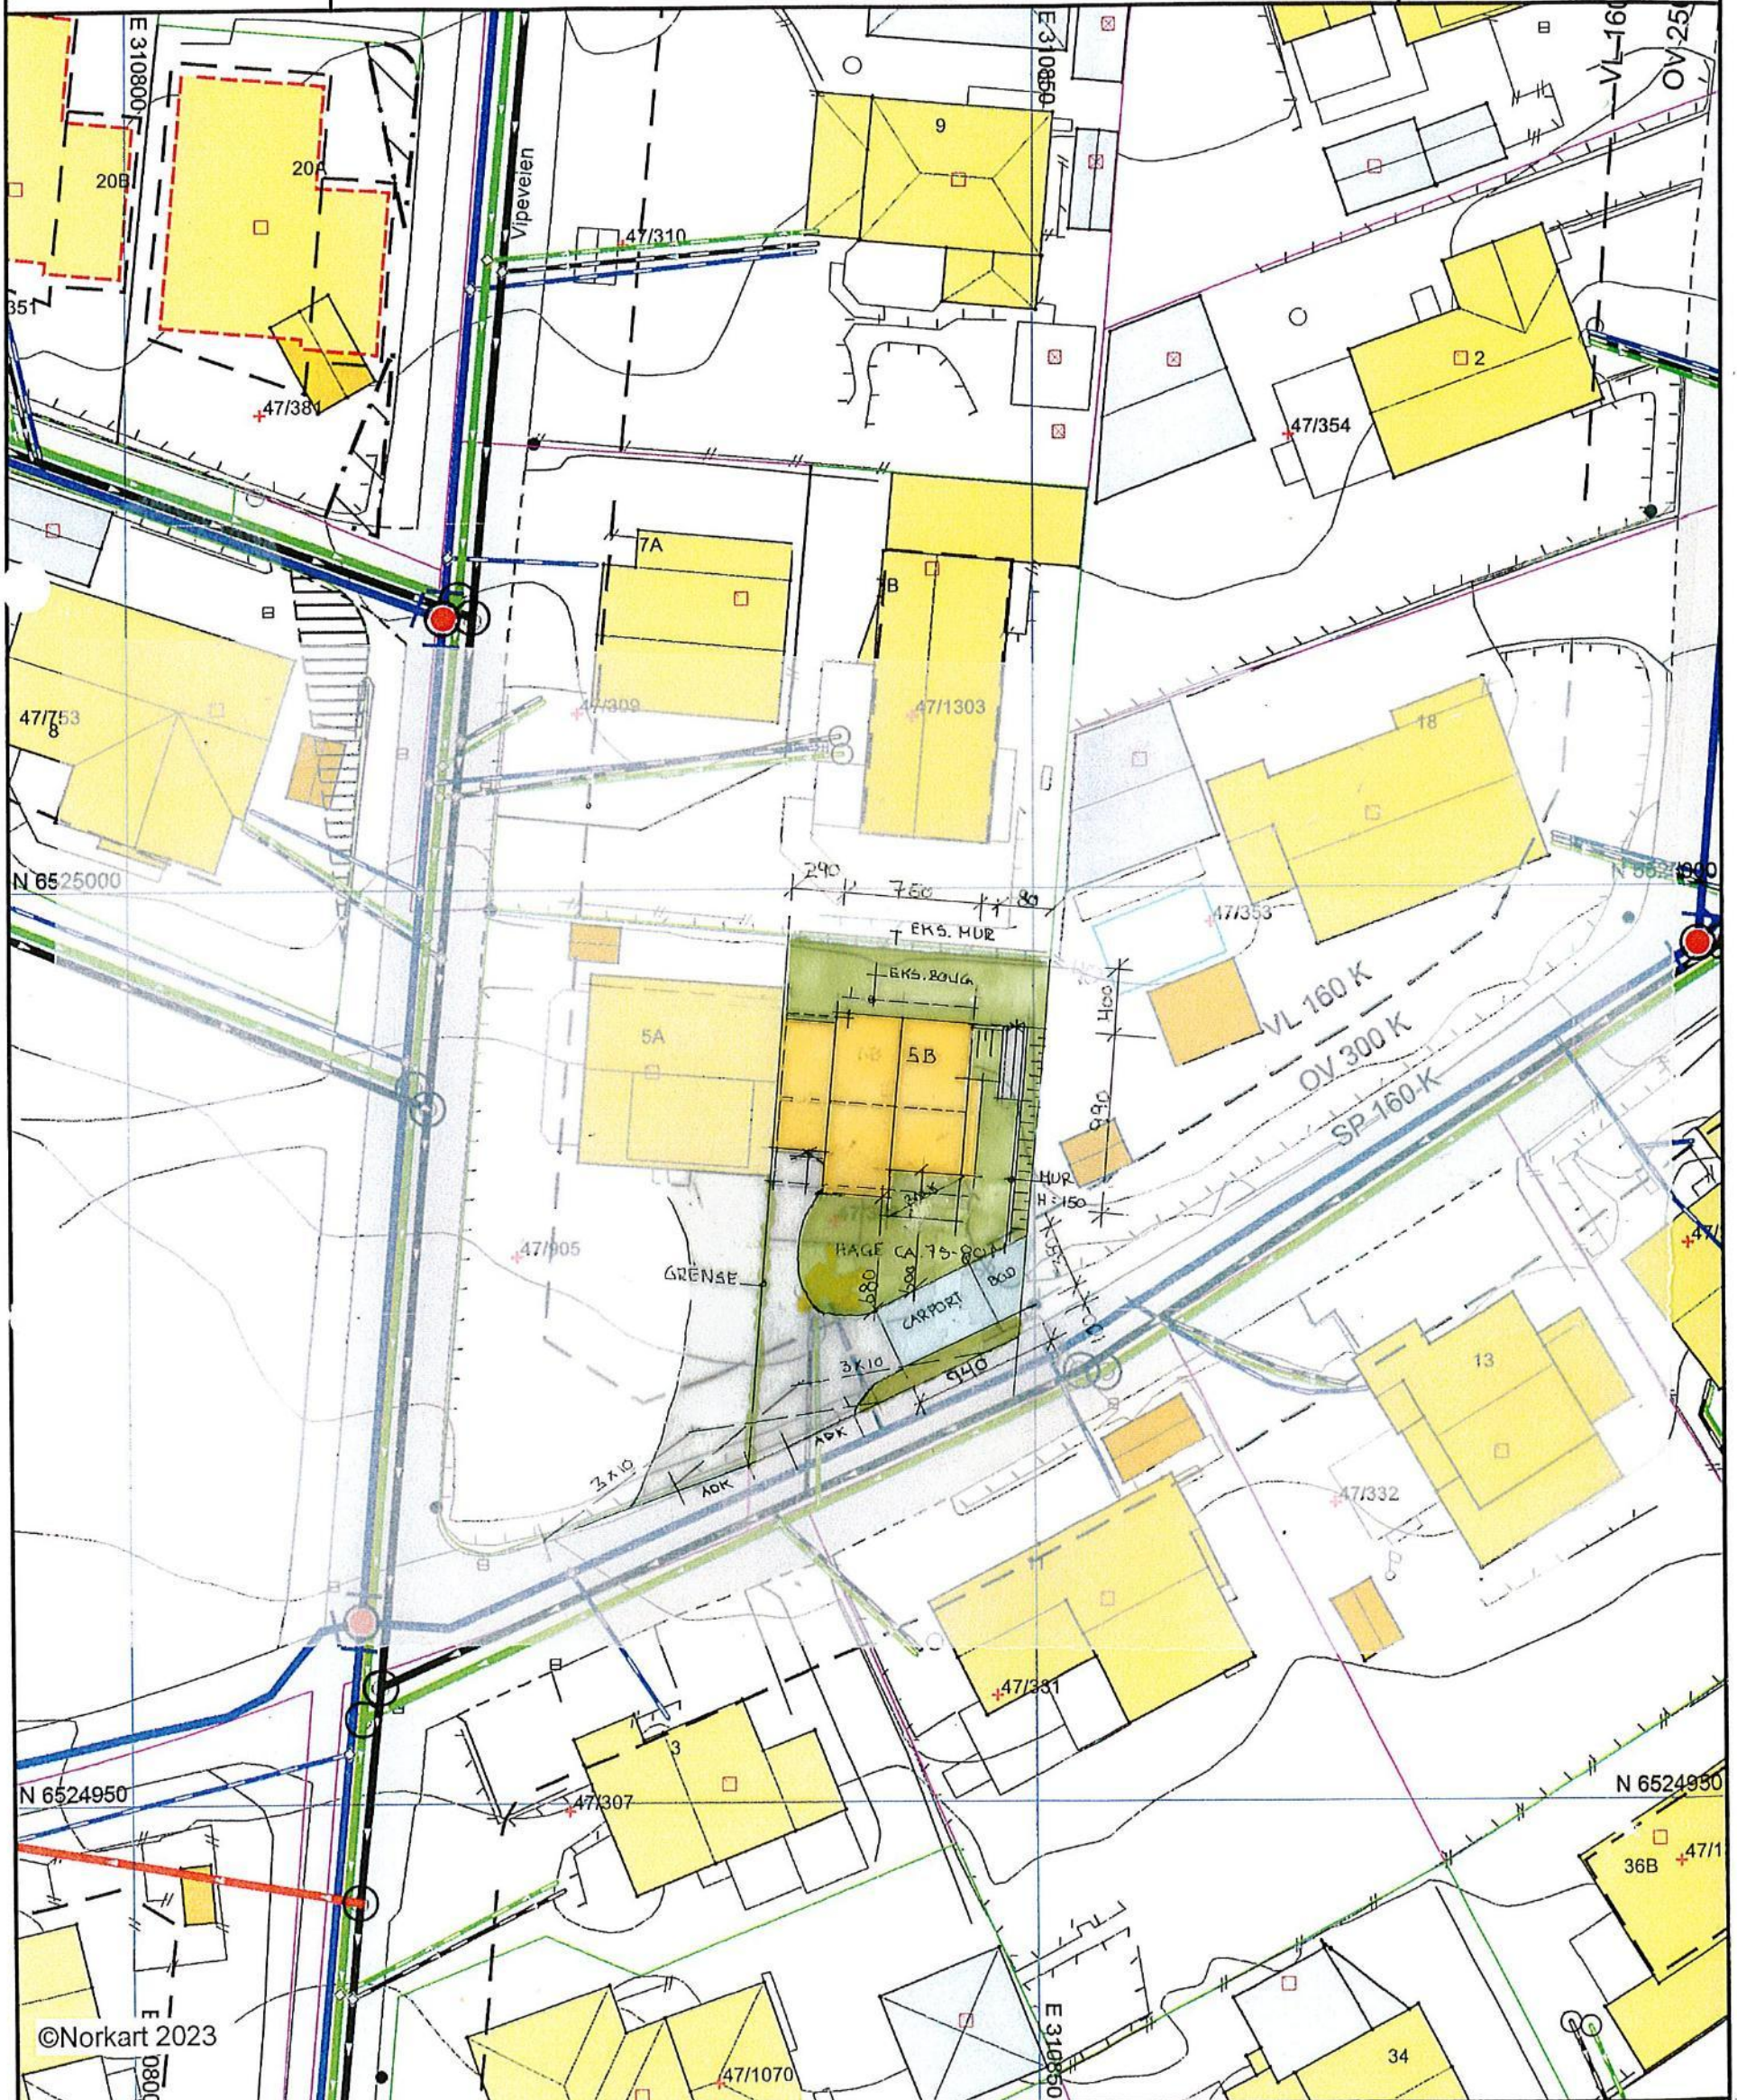

©Norkart 2023

- 1) Det tas forbehold om feil i kartgrunnlaget
2) Ved utskrift fra PDF-fil kan målestokken bli unøyaktig