


Situasjonskart

Eiendom: 62/504
Adresse: Wergelands vei 13
Dato: 24.10.2023
Målestokk: 1:500

$$A_{\text{real}} = 1288 \text{ m}^2$$


UTM-32

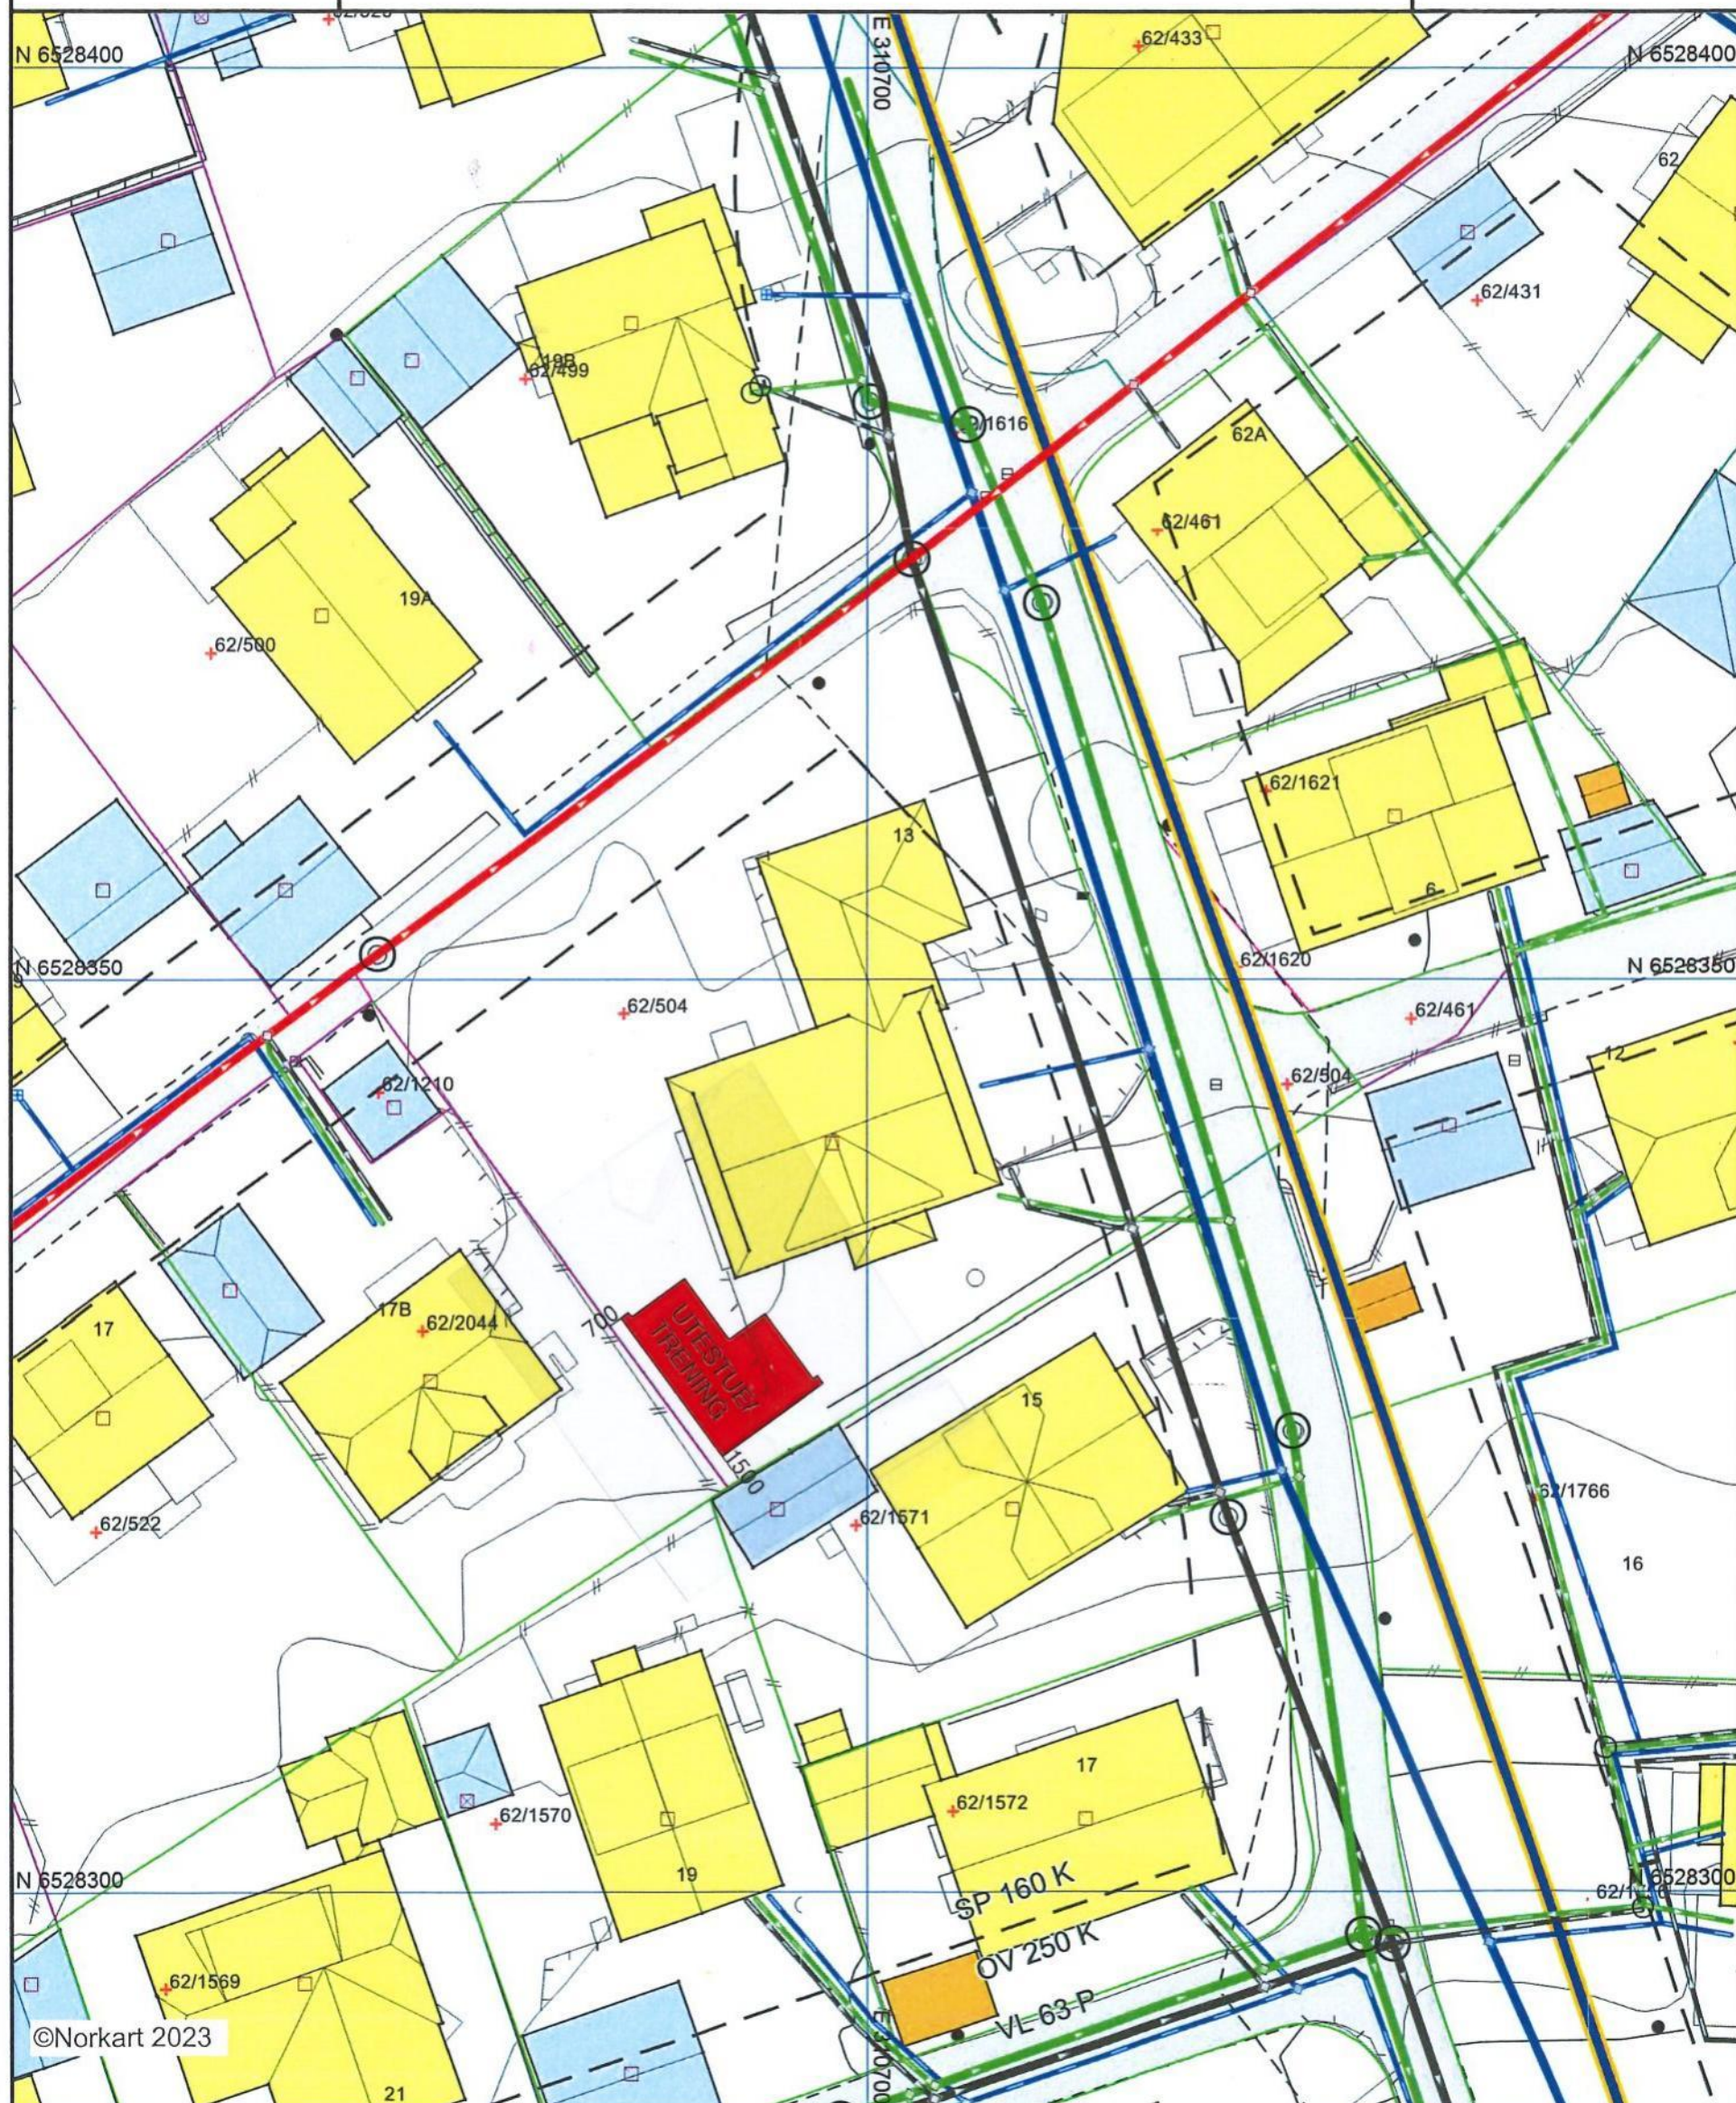

©Norkart 2023

- 1) Det tas forbehold om feil i kartgrunnlaget
2) Ved utskrift fra PDF-fil kan målestokken bli unøyaktig