



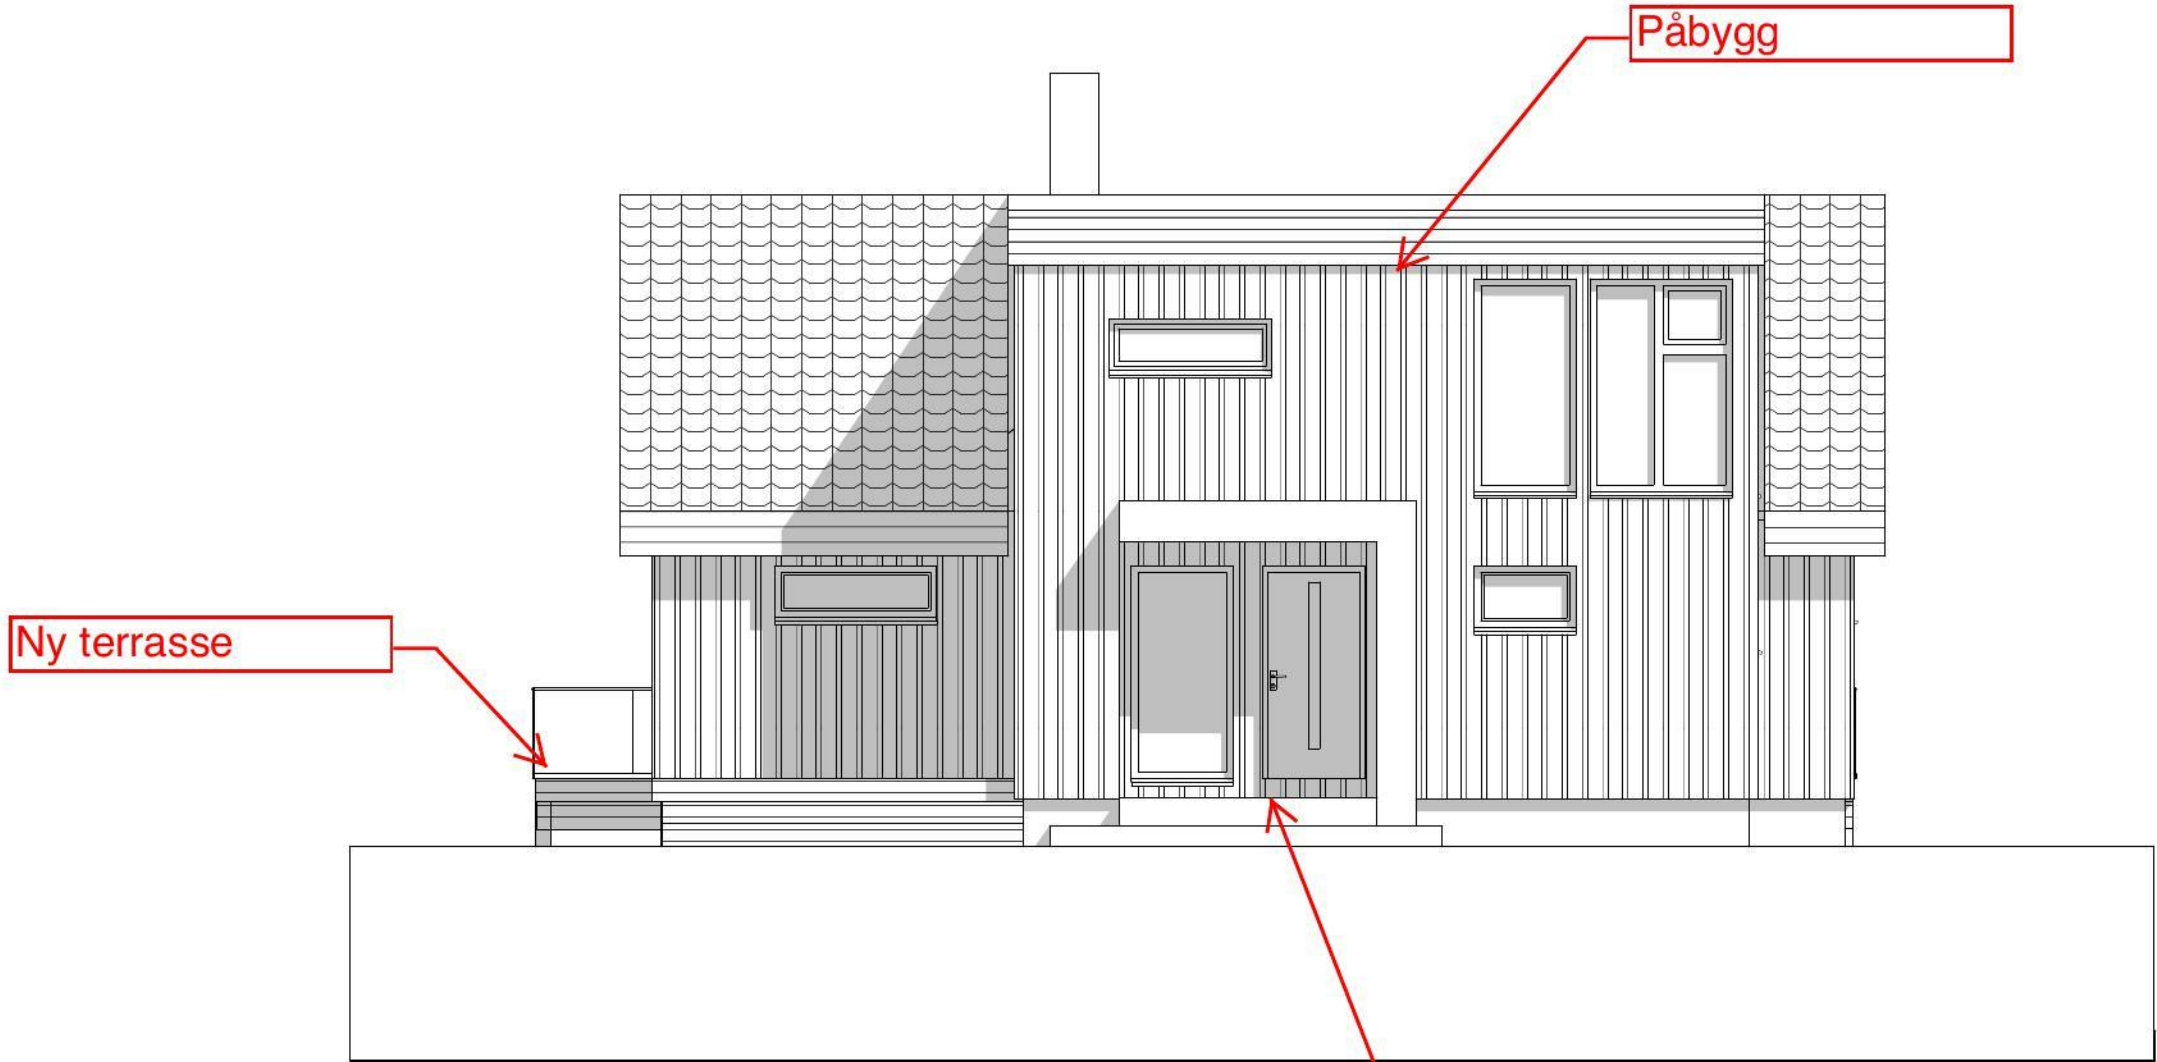

1:100 Fasade Øst

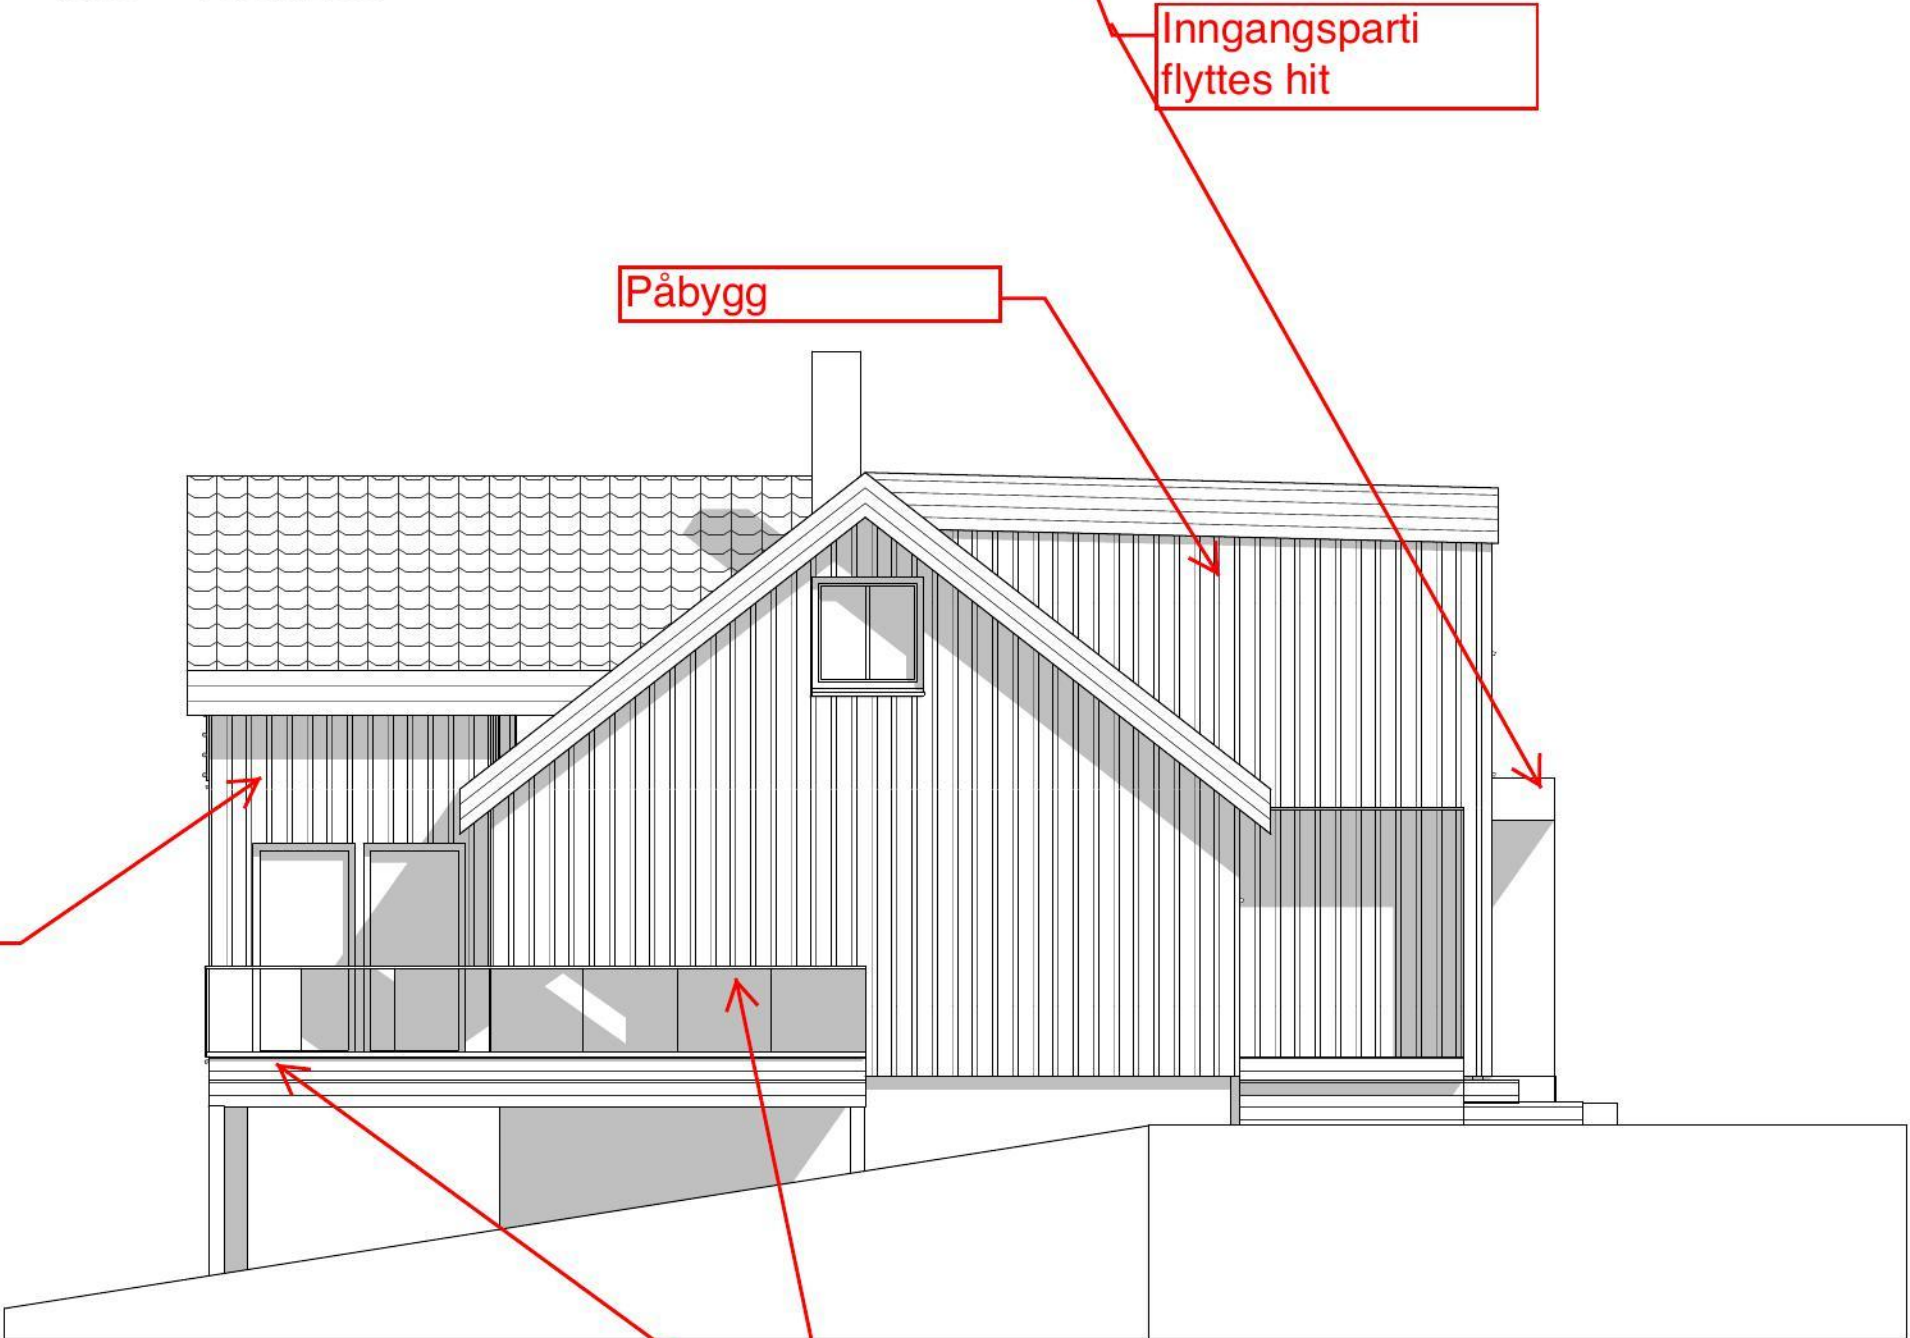

1:100 Fasade Sør

Ny terrasse

Tegningsnr. A40-2		Revisjon nr.	
Type tegning Fasade Sør og Øst	
<table><tr><td></td><td>Revidert</td><td>07.07.2022</td><td></td></tr><tr><td></td><td>Revidert</td><td>02.01.2023</td><td></td></tr><tr><td></td><td>Revidert</td><td>vindusliste</td><td>09.01.2023</td></tr><tr><td></td><td></td><td></td><td></td></tr><tr><td></td><td></td><td></td><td></td></tr><tr><td></td><td></td><td></td><td></td></tr><tr><td></td><td></td><td></td><td></td></tr><tr><td></td><td></td><td></td><td></td></tr><tr><td></td><td></td><td></td><td></td></tr><tr><td></td><td></td><td></td><td></td></tr></table>					Revidert	07.07.2022			Revidert	02.01.2023			Revidert	vindusliste	09.01.2023																												
	Revidert	07.07.2022	
	Revidert	02.01.2023	
	Revidert	vindusliste	09.01.2023	
Rev	Nr	Beskrivelse	Dato	Sign	Kontr																																						
Lokalisering:	
Prosjekteringsgruppen	
●	ARK :	Skjærgårdsbygg a/s	Østerøya 240 4625 Flekkerøy Tlf.: 90522750 steinar@skjaergardsbygg.no	
●	RIB :	Rådg. ing. Bygg	RIBveien18 0000 RIBbyen Tlf: 000 00 000 rib@ribfirma.no	
●	RIE :	Rådg. ing. Elektro	RIEveien18 0000 RIEbyen Tlf: 000 00 000 rie@riefirma.no	
●	RIV :	Rådg. ing. VVS	RIVveien18 0000 RIVbyen Tlf: 000 00 000 riv@rivfirma.no	
Fase	
Fase	
Tiltakshaver				Godkjent																																							
Mia og Sivert	
Prosjekt				Kontroll prosjekt.																																							
				Sign.	Kontroll																																						
Filnavn				Sivert og Mia.pln,lck.pln																																							
Dato				20.04.2022																																							
Målestokk				1:100																																							
Kontroll utførende	
Gnr./Bnr./Festenr.:				Sign.	Kontroll																																						
Gnr/Bnr/Festenr	
Prosjektnr.:		Tegningsnr.:		Prosjektnr. for																																							
Prosjektnr.		A40-2		prosjekterende/lev.																																							
Type tegning:	
Fasade Sør og Øst	