



FASADE NORDVEST

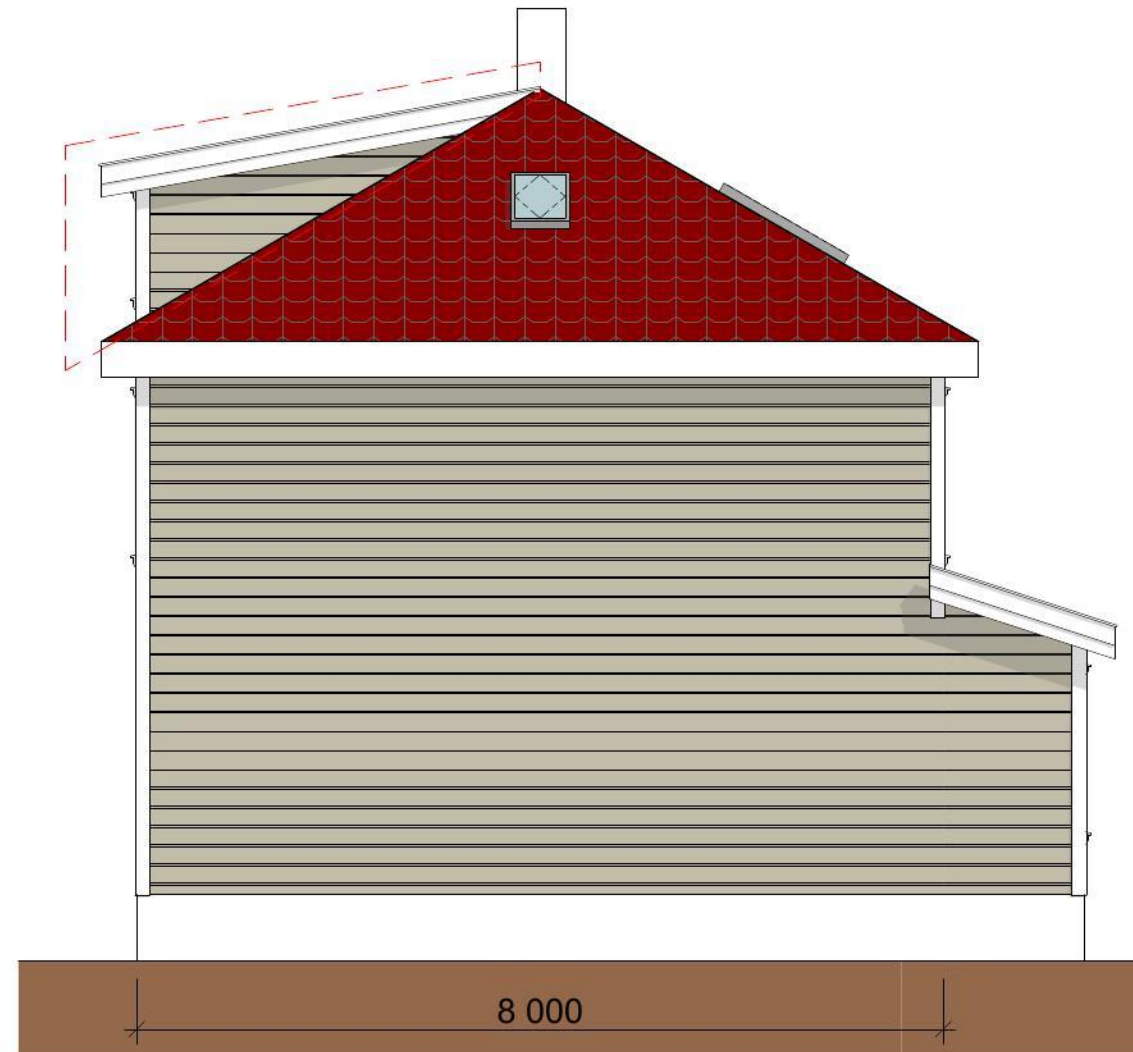

FASADE SØRVEST



FASADE SØRØST

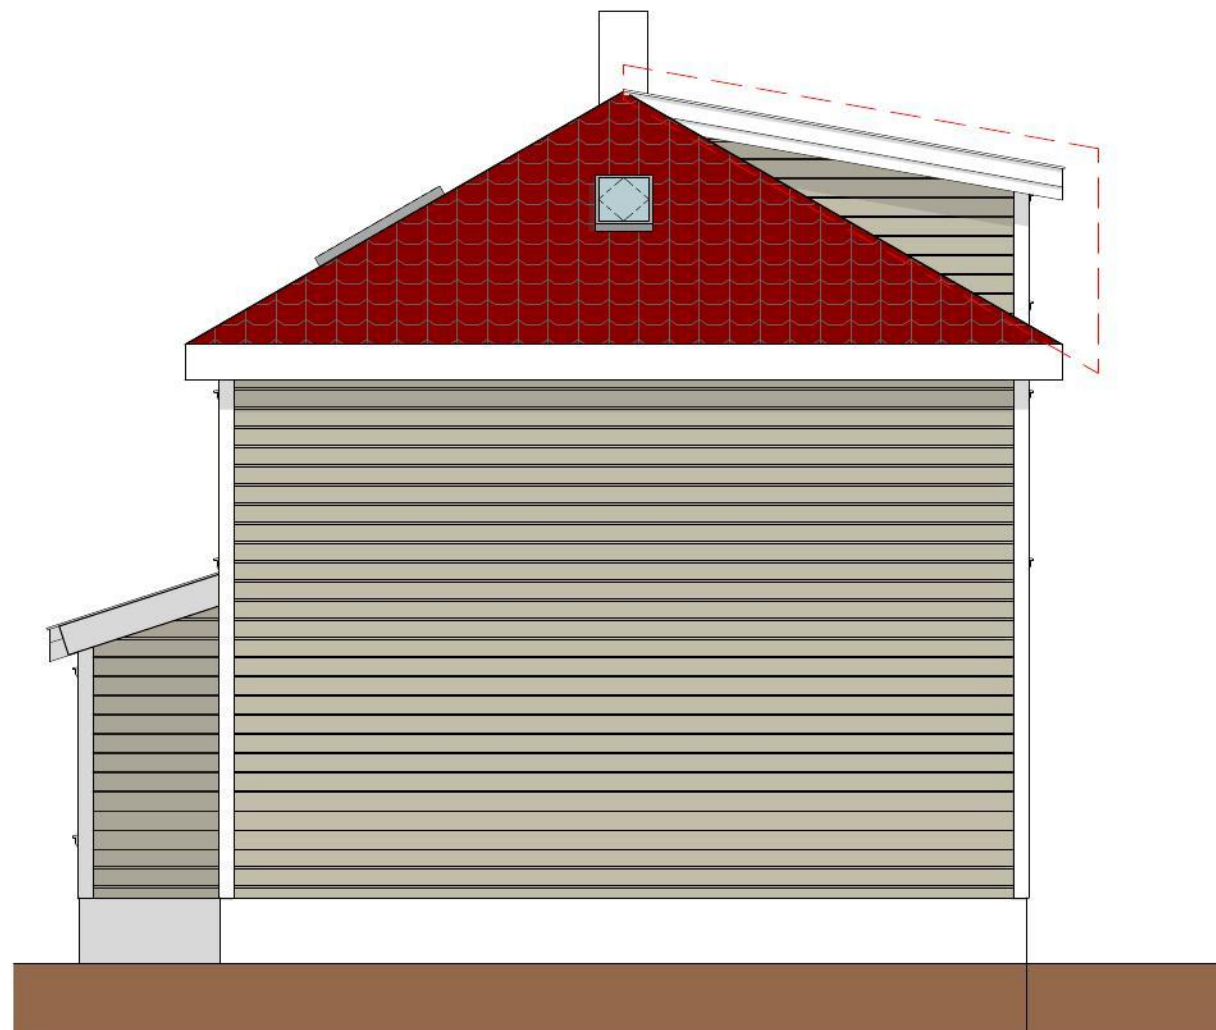

FASADE NORDØST



Tegningsnr.: A40-01	Revisjon nr.:
------------------------	---------------

Revisjon nr.:

Type tegning:
Fasader 1

Index	Dato	Beskrivelse	Sign.	Kontr.



Besøksadresse: Kjøita 37 (4. etg)
Postadr: Kjøita 37 4630 Kristiansand

Knut Ove Kristiansen Tlf: 916 84 510 Mail: knut.ove@arkiconas.no

Prosjekteringsgruppen:

- ☒ **ARK :** Nancy Eisner
- ☐ **RIB :** Rådg. ing. Bygg
- ☐ **RIE :** Rådg. ing. Elektro
- ☐ **RIV :** Rådg. ing. Vent.

Kjøita 37 (4. etg)
4630 Kristiansand
Tlf. 940 19 420
nancy@arkiconas.no

.....veien 0
0000 Stedet
Tlf. 00 00 00 00
Fax. 00 00 00 00

.....veien 0
0000 Stedet
Tlf. 00 00 00 00
Fax. 00 00 00 00

.....veien 0
0000 Stedet
Tlf. 00 00 00 00
Fax. 00 00 00 00

Fase:
Søknadstegning

Gnr: 151 Bnr: 384

Tittel:

Tone Lise
Haraldseid
**Bruksendring Loft
Kvist**
Dalaneveien 10
4617 Kristiansand

Godkjent:

Kontroll prosjekt	
Sign.:	Kontroll:

Filnavn:
Dalaneveien 10 vs
22.12.2021.pln

Dato:
22.12.2021

Målestokk:
1:100

Kontroll utførende	
Sign.:	Kontroll:

Prosjektnr.:
55/2021

Tegningsnr.:
A40-01

Prosjektnr. for prosjekterende/lev	

Type tegning:
Fasader 1