



Stavanger kommune

Situasjonskart

Eiendom: 125/95


Utskriftsdato: 08.03.2022

Adresse: Øvre Hauskjeneset

Målestokk: 1:500



UTM-32

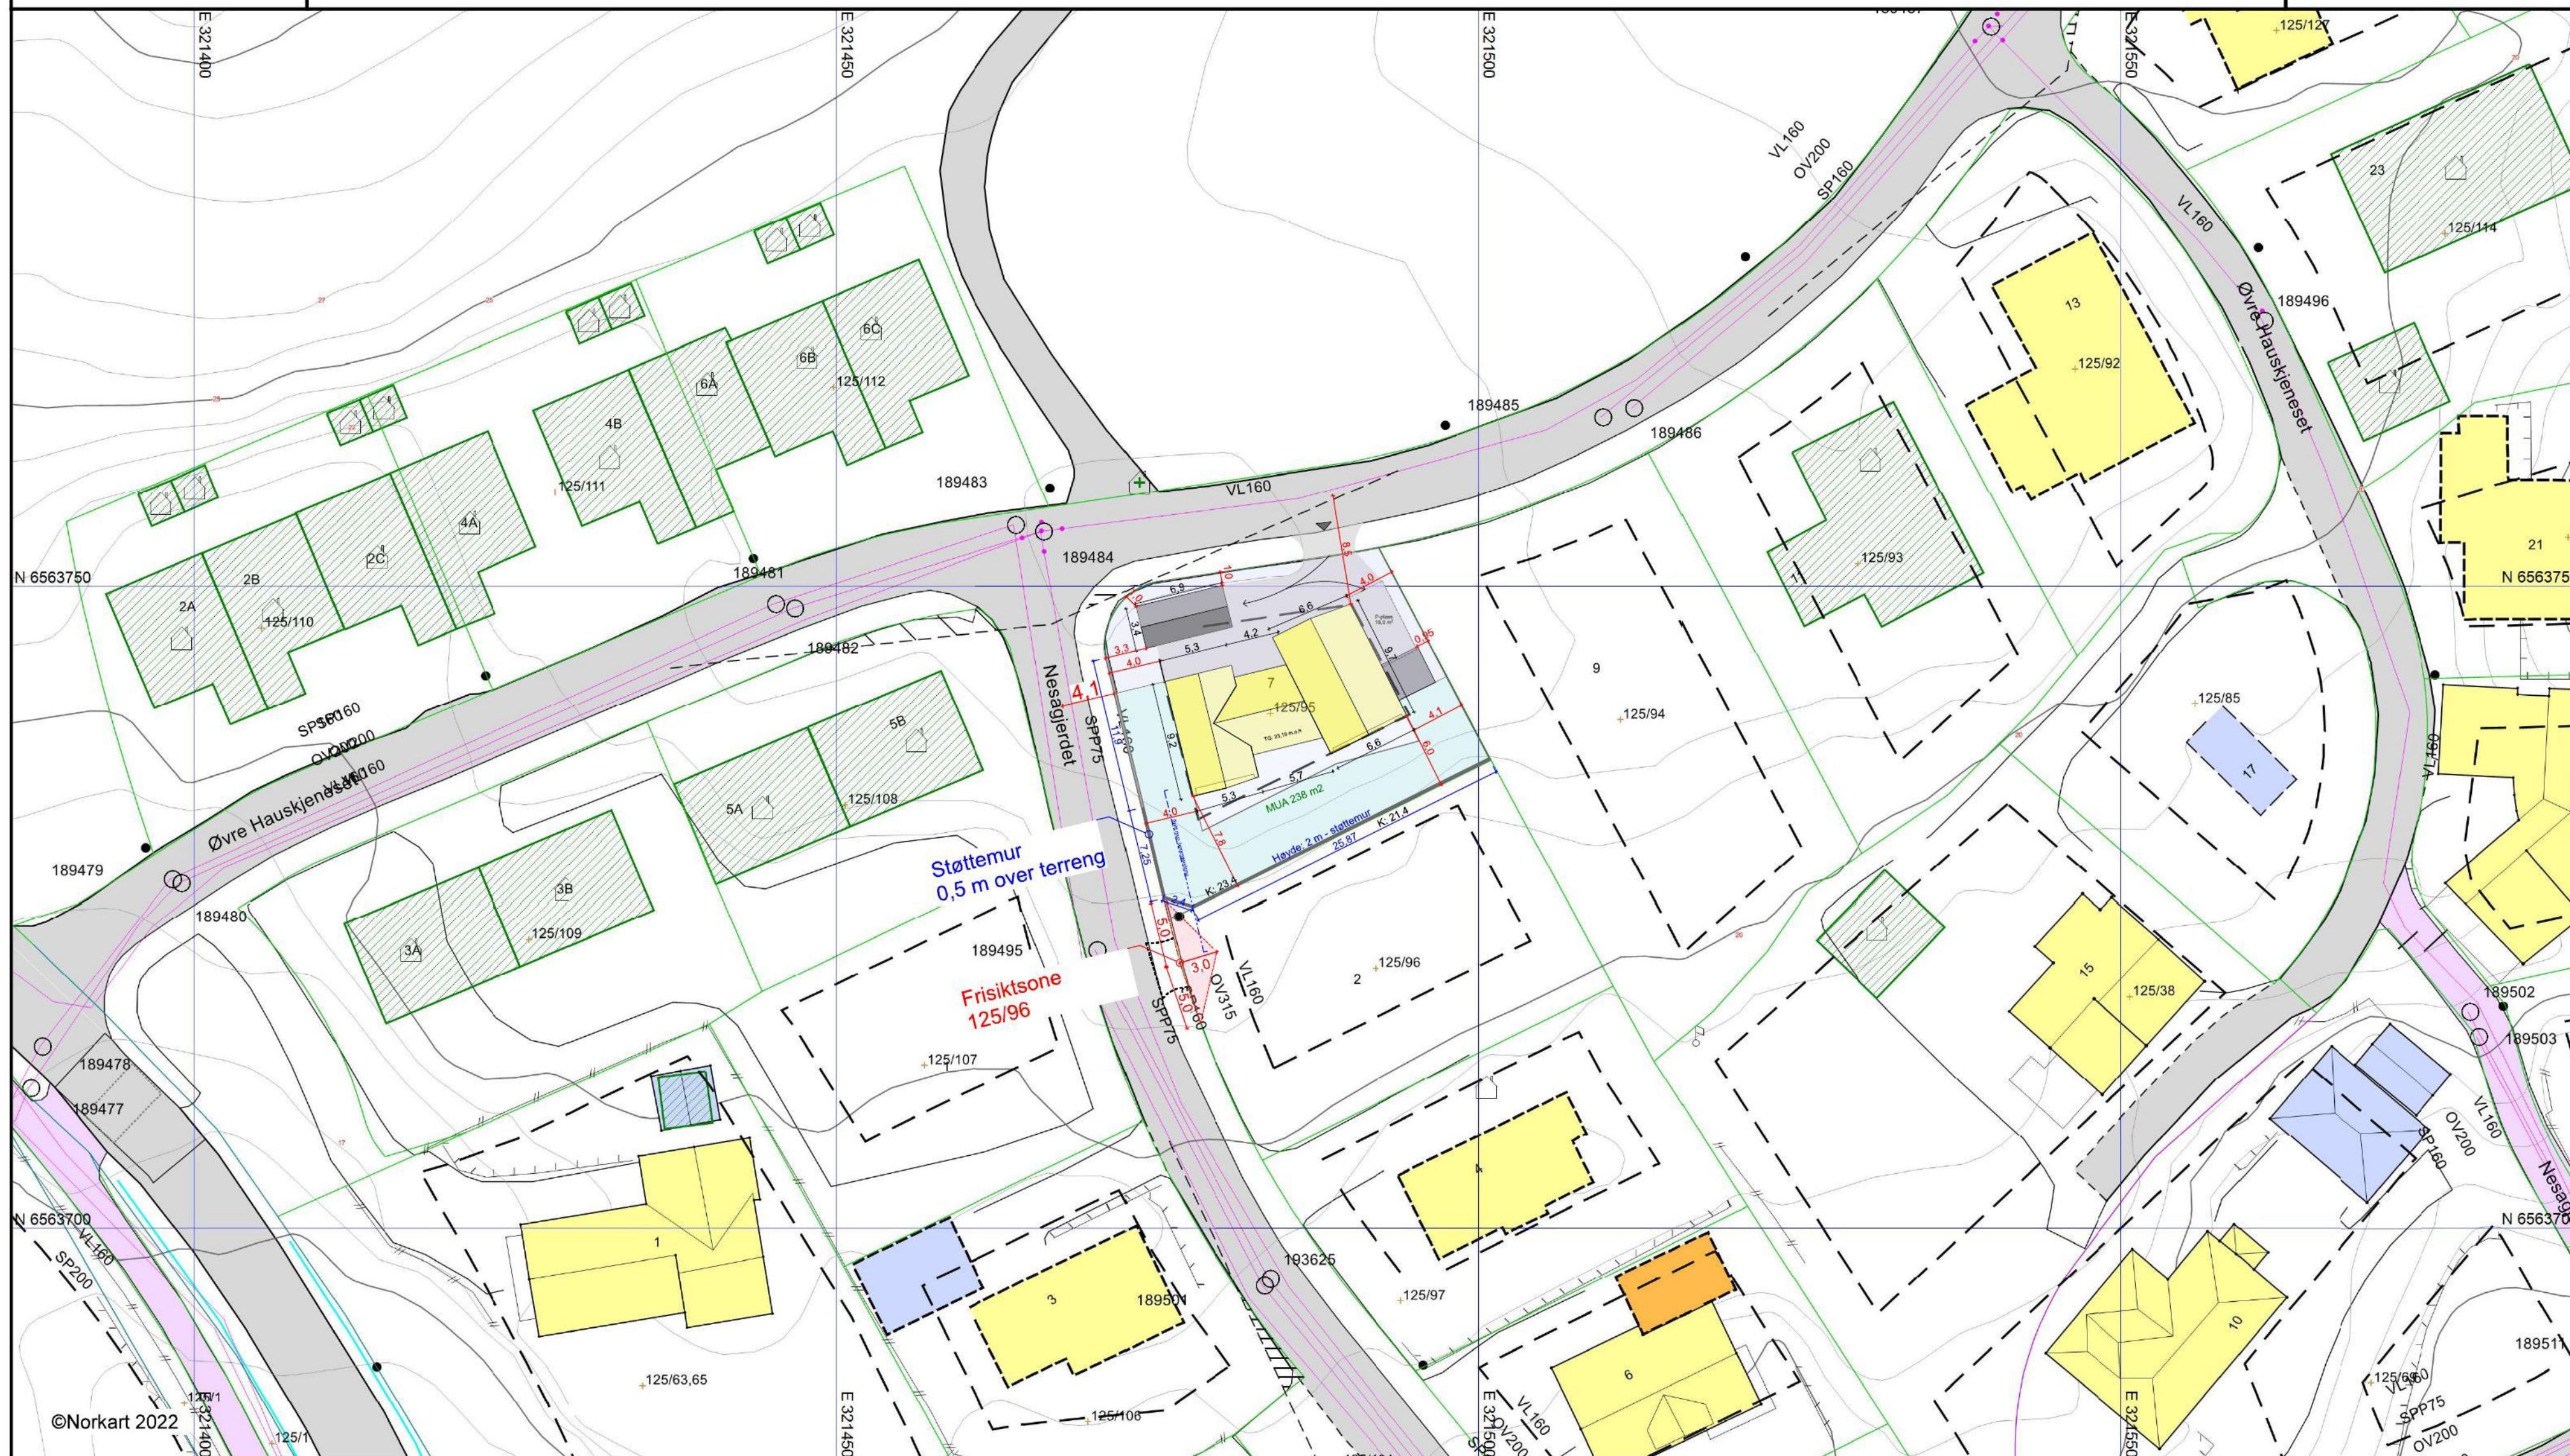

1) Det tas forbehold om feil i kartgrunnlaget. 2) Ved utskrift fra PDF-fil kan målestokken bli unøyaktig.