


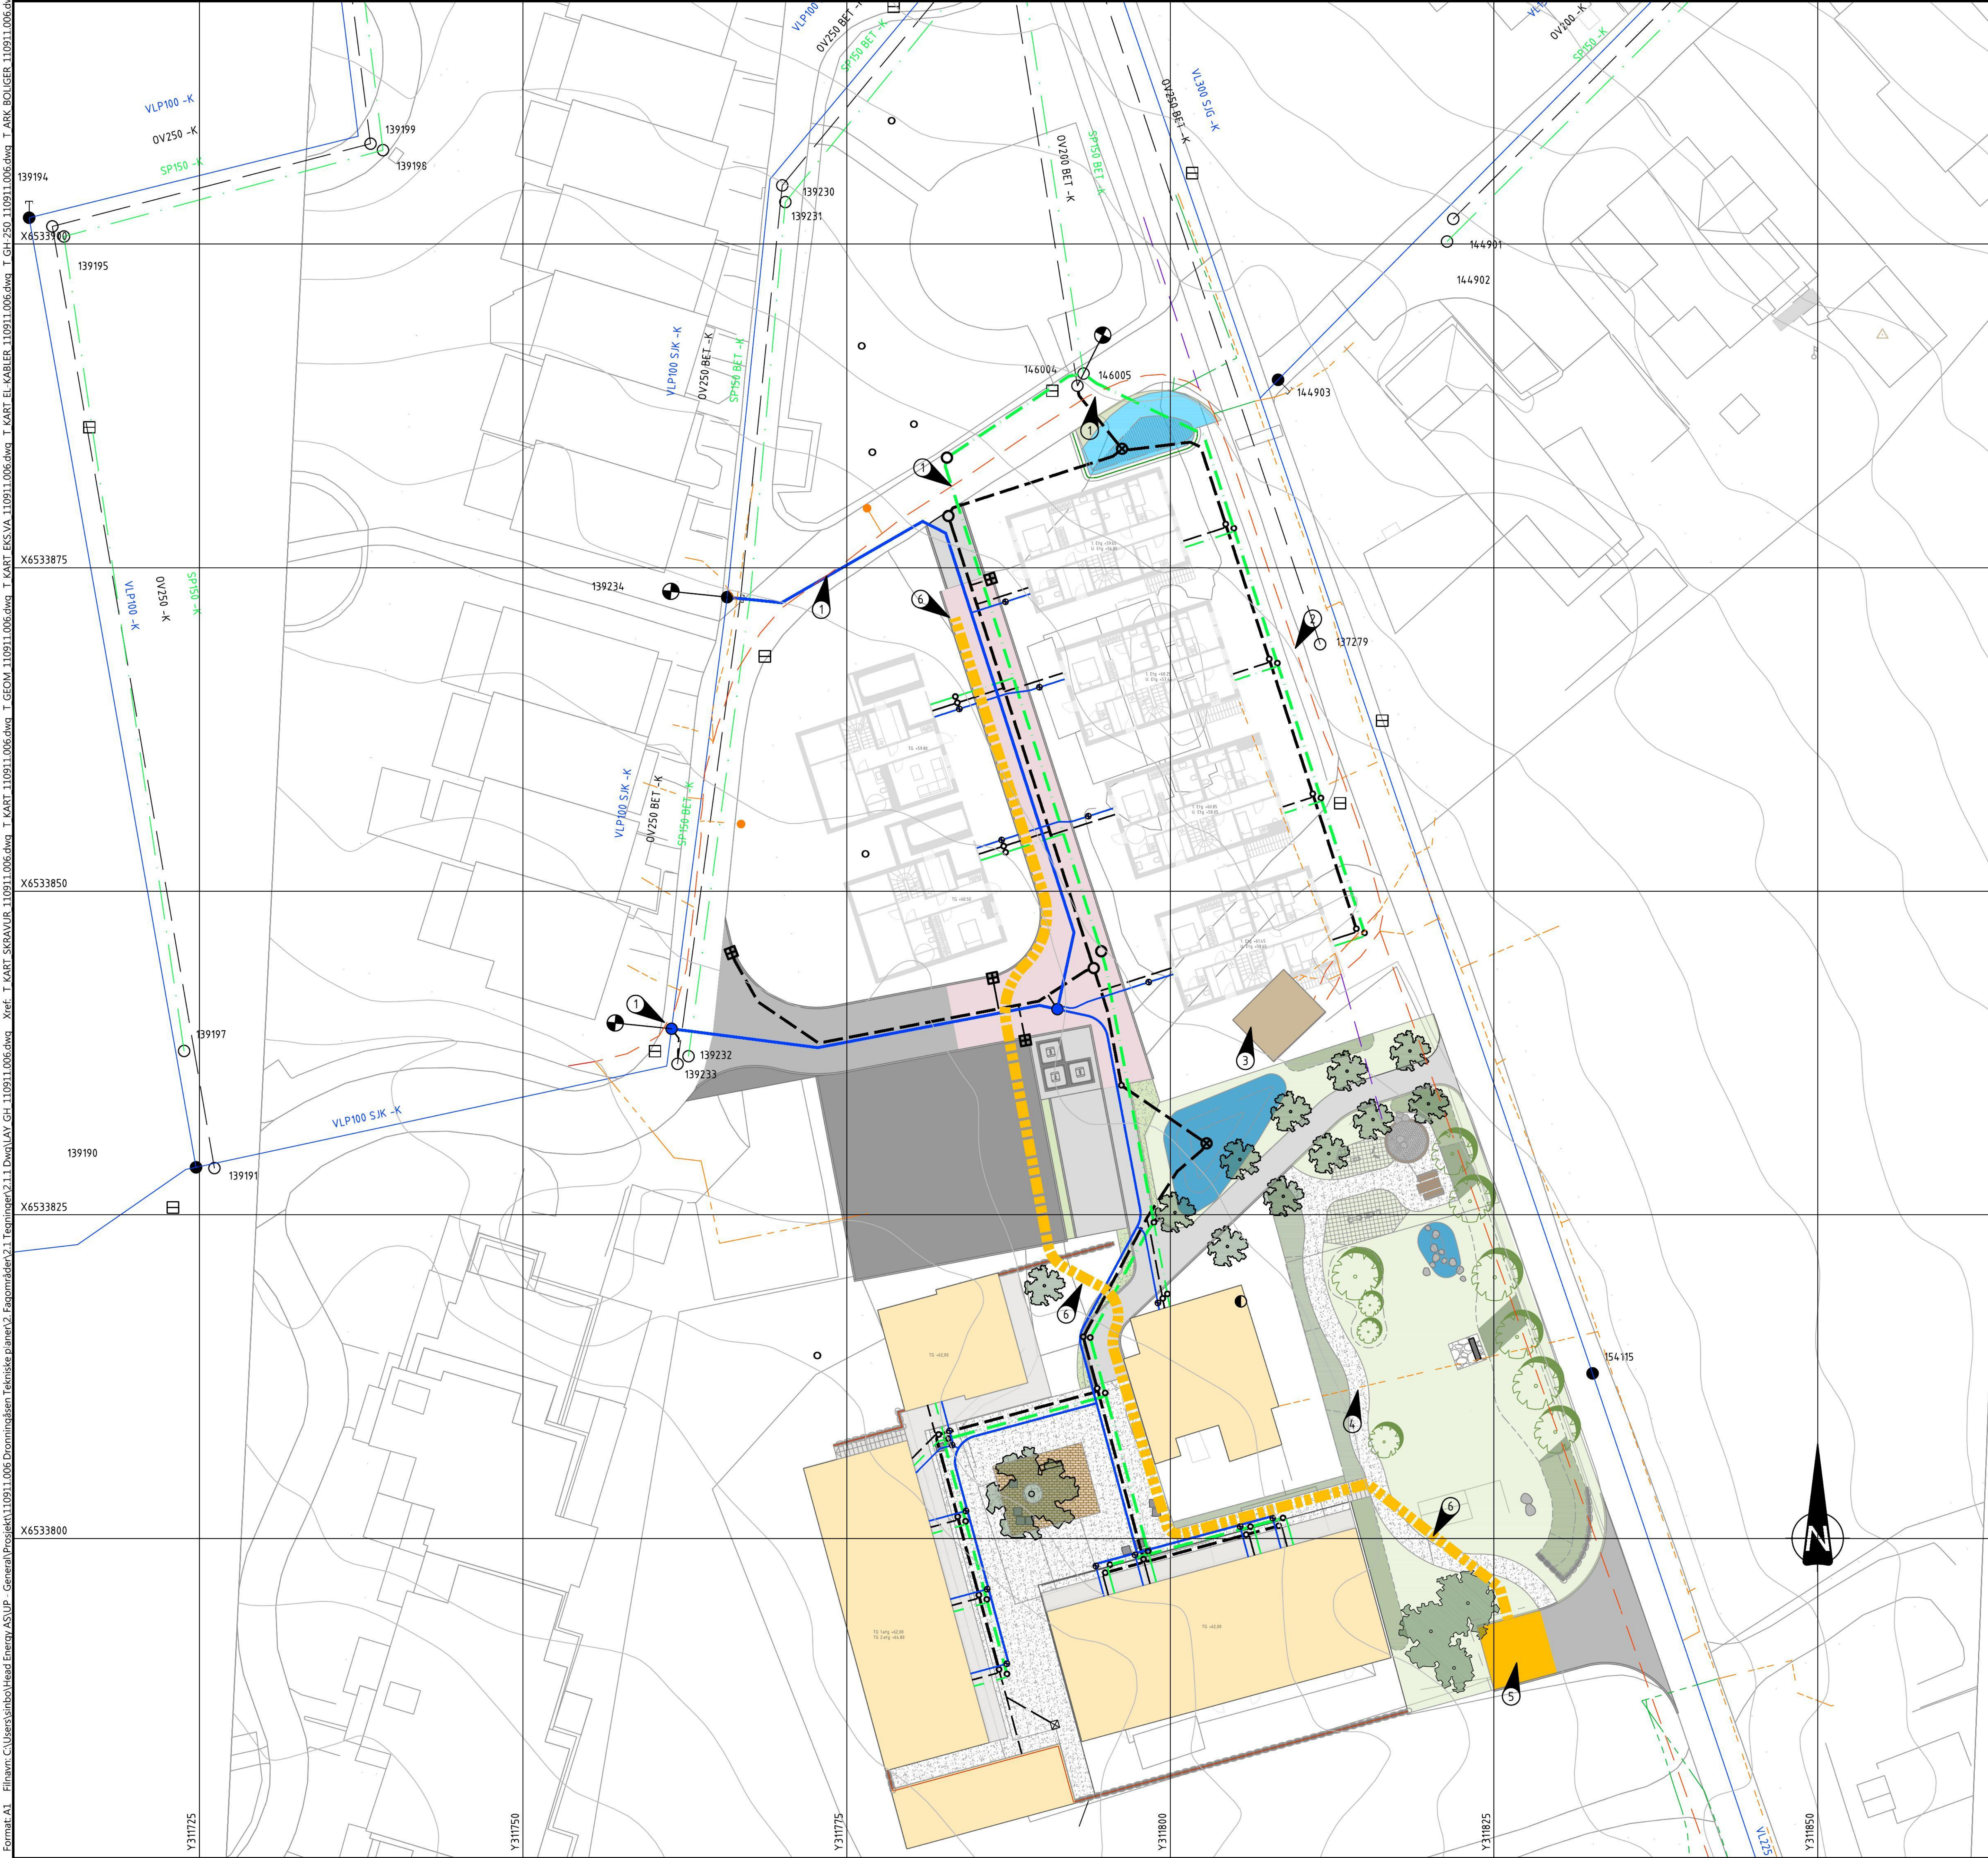

MERKNADER

- VA-anlegget er basert på følgende underlag:
 - * FKB Kart, mottatt 04.05.2020
 - * VA Kart, mottatt 26.10.2023
 - * Innmålinger eks. VA, datert 02.01.2024
- Det tas forbehold om unøyaktighet i opplysninger om eks. anlegg. Entreprenør er ansvarlig for gravemelding og påvisning av kabler og eksisterende VA-anlegg.
- Punkter for tilknytning til eks. ledninger må frigraves og kontrolleres mot prosjektert underlag før utførelse. Ved avvik må planene revideres.

MERKNADSPILER

- 1 OBS! Eks. langsgående/-kryssende HSP kabel ift. PRO. VA.
- 2 OBS! Eks. Langsgående HSP ift. PRO VA (Private stikkledn.)
- 3 Eks. trafo rives/-flyttes og kabler omlegges.
- 4 OBS. Eks. LSP - abonnement kabel til eks. bolig. Overdekning ved senking av terreng kontrolleres.
- 5 Ny trafoplassering.
- 6 Foreslått ny kabeltrase gjennom boligområdet.

TEGNFORKLARING EKS. KABLER FORSLAG TRASE

Jordkabel HSP	---	
Jordkabel LSP	---	
Jordkabel GTL	---	
Jordkabel tele/fiber	---	
Vraket kabel	---	
Forslag kabeltraseer		---

TEGNFORKLARING EKS. VA PRO. VA

Vannledning	---	---
Vannledning utgår	---	---
Spillvannsledning	---	---
Spillvannsledning, utgår	---	---
Overvannsledning	---	---
Overvannsledning, utgår	---	---
Drensledning	---	---
Kum/utviser/lufteventil	○	○
Slamavskiller	●	●
Kum m/brannventil	●	●
Stoppekran	○	○
Sandfang/kuppel	⊞	⊞
Sluk	⊞	⊞
Entrepisegrense	---	---

1	TIL GODKJENNING	19.01.24	RONHO	AGAMA	SINBO
Rev.	Revideringen gjelder	Dato	Tegnet	Kontroll	Godkj.
Dronningåsen AS		Prosjektnr. 110911.006	Fag	VA	
Dronningåsen Tekniske Planer		Målestokk A1	Tegnet	RONHO	
Stavanger Kommune		1:250	Kontrollert	AGAMA	
VA-ANLEGG OVERSIKTSTEGNING MASTERPLAN (VA & KABEL)		Koordinatsystem EUREF89-32N NN2000	Dato	19.01.2024	
HEAD ENERGY		HEAD ENERGY UP AS Org.nr: 925 044 329 www.headenergy.no T: +47 992 04 323	Kontor: Vassbotnen 118, 4313 Sandnes Lønningsvegen 47, 5258 Blomsterdalen	Status TIL GODKJENNING	
		Tegningsnr. GH002		Rev.	1