



Format: A1 - Filnavn: C:\Users\thale\OneDrive\Head Energy\AS\UP - General\Prosjekt\110911.006\Drømminnåsen\Tekniske planer\2. Fagområder\2.1 Tegninger\2.1.1 Dwg\LAV D. 110911.006.dwg - Xref: T. KART. KOTER: 110911.006.dwg T. KART. BEGNOM: 110911.006.dwg T. GEOM: 110911.006.dwg T. KART. SKRAVUR: 110911.006.dwg T. CL: 110911.006.dwg A. LPL: 110911.004.dwg T. SKI: 110911.006.dwg

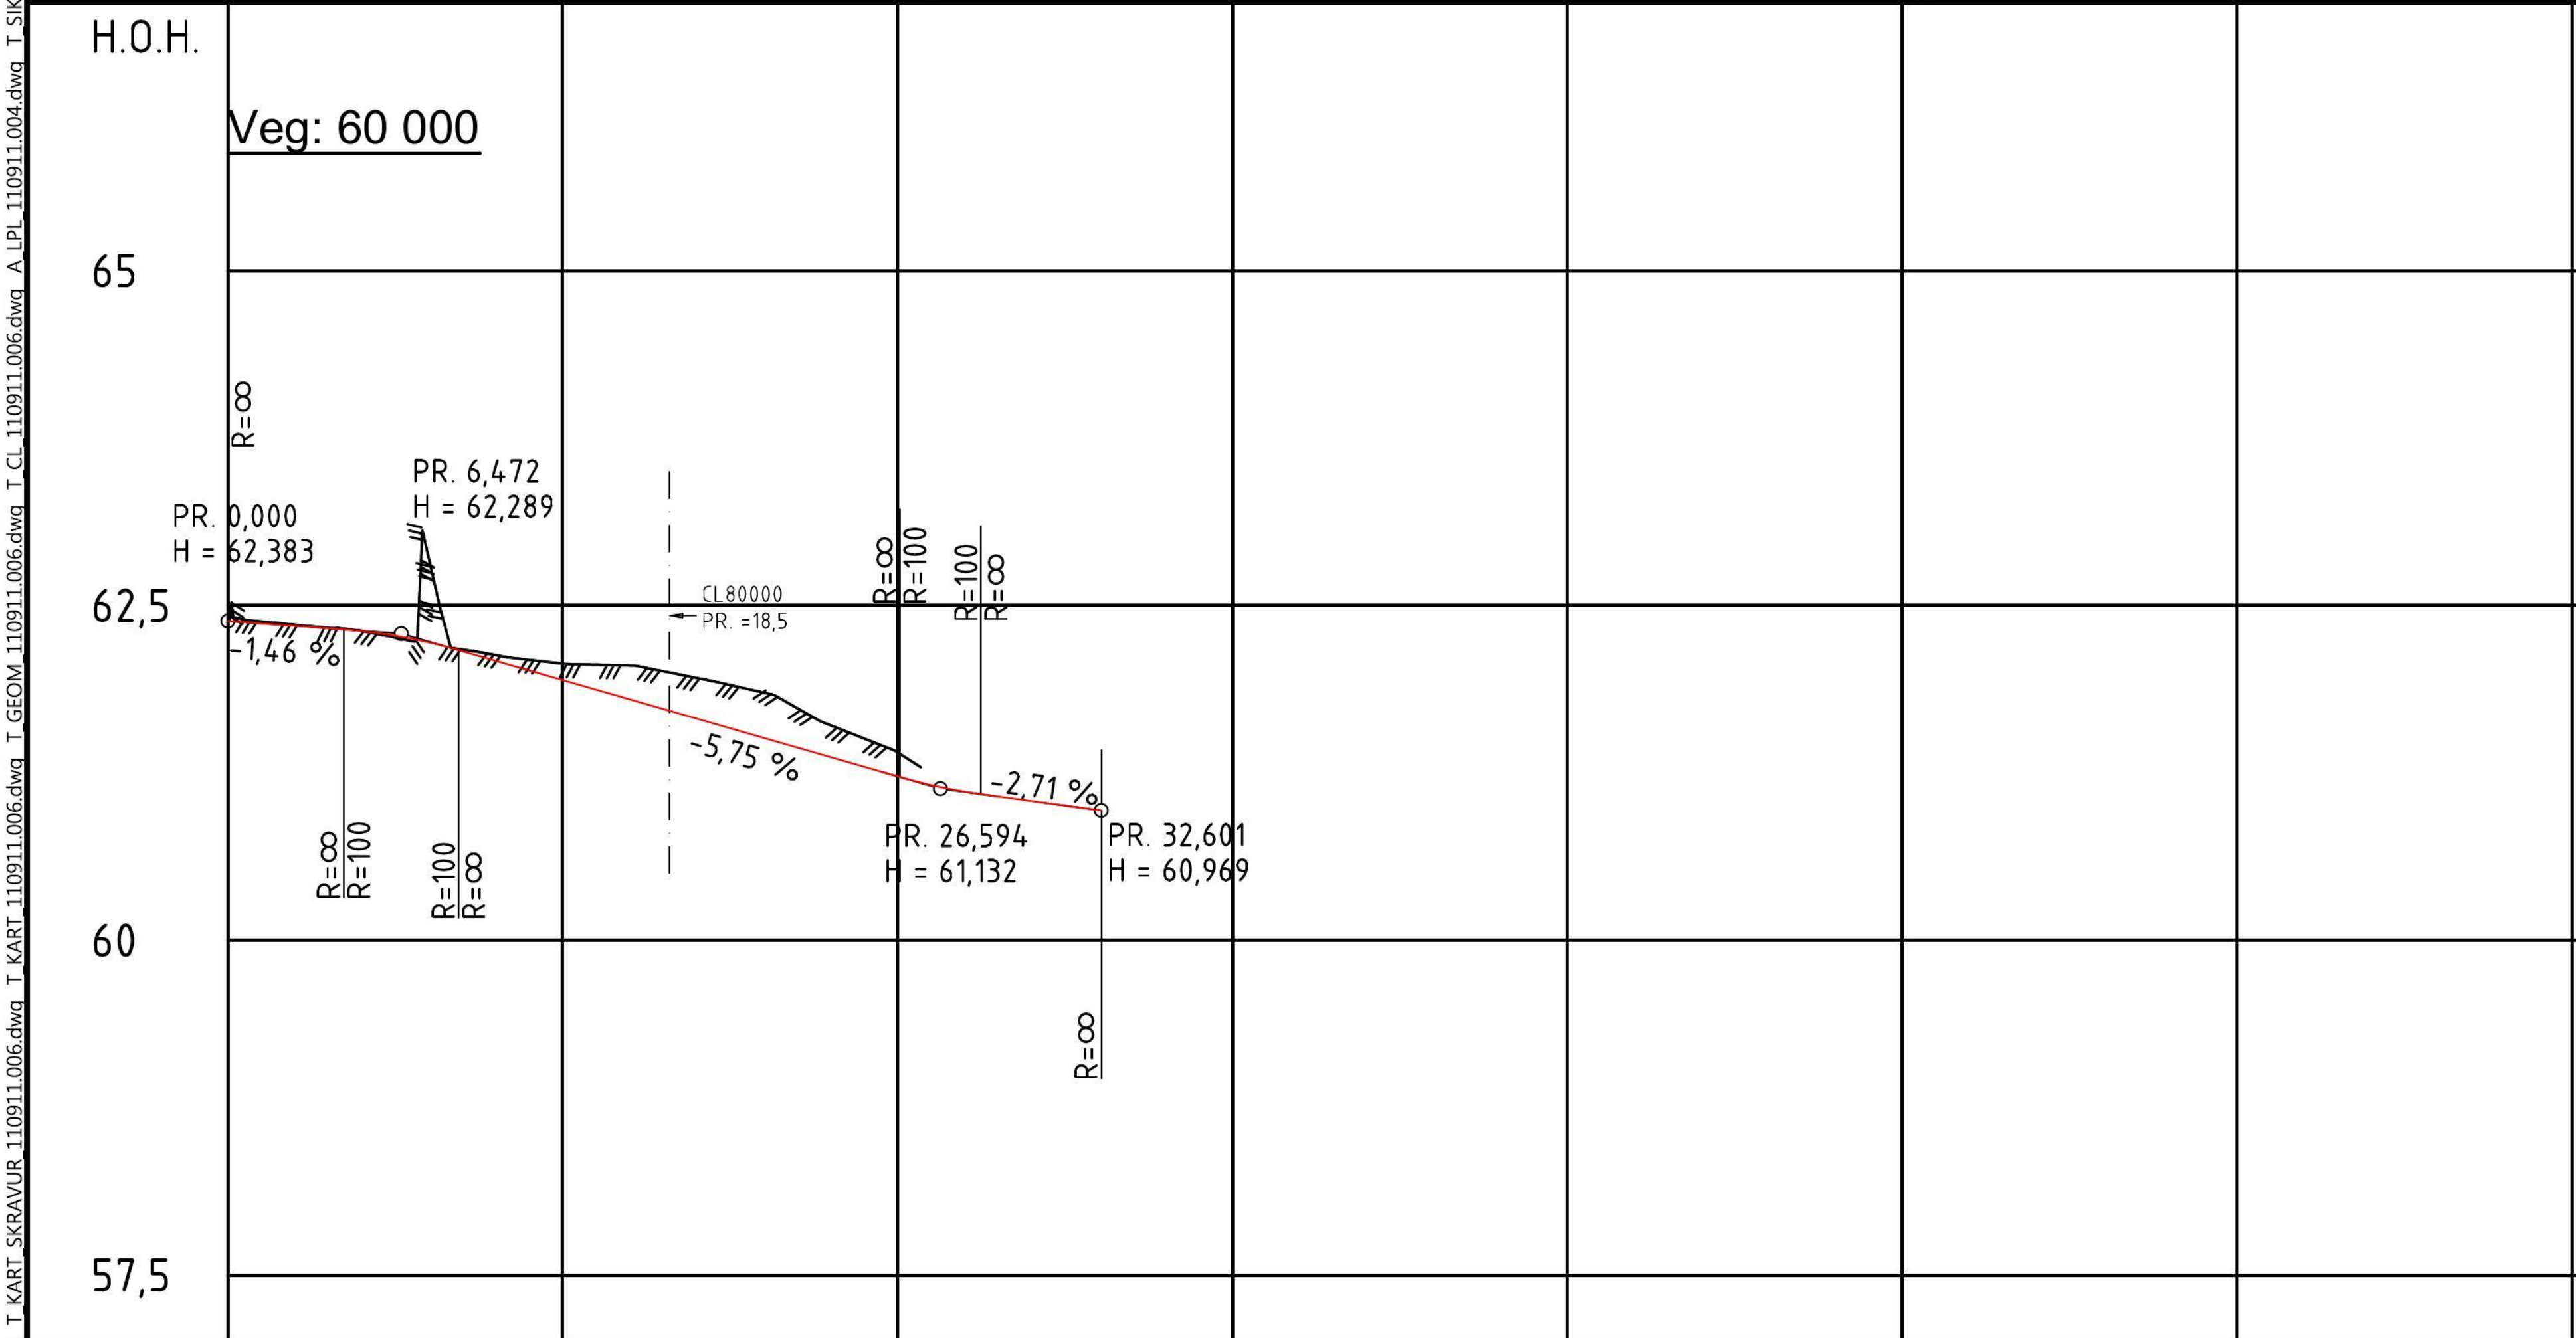

PROFIL NR.	0	12,5	25	37,5	50	62,5	75	87,5
HOR.KURV.	R=∞	R=9,5	R=∞					
BREDDEUTV.								
TVERRFALL	7,0%							
H.kj.b.k.	3,0%		3,0%	4,0%				
V.kj.b.k.	8,0%							
PROFIL H.	62,38	62,31	62,22	62,09	61,94	61,80	61,65	61,51
TERRENG H.	62,38	62,31	62,22	62,09	61,94	61,80	61,65	61,51
OVERBYGN.T.		48CM						

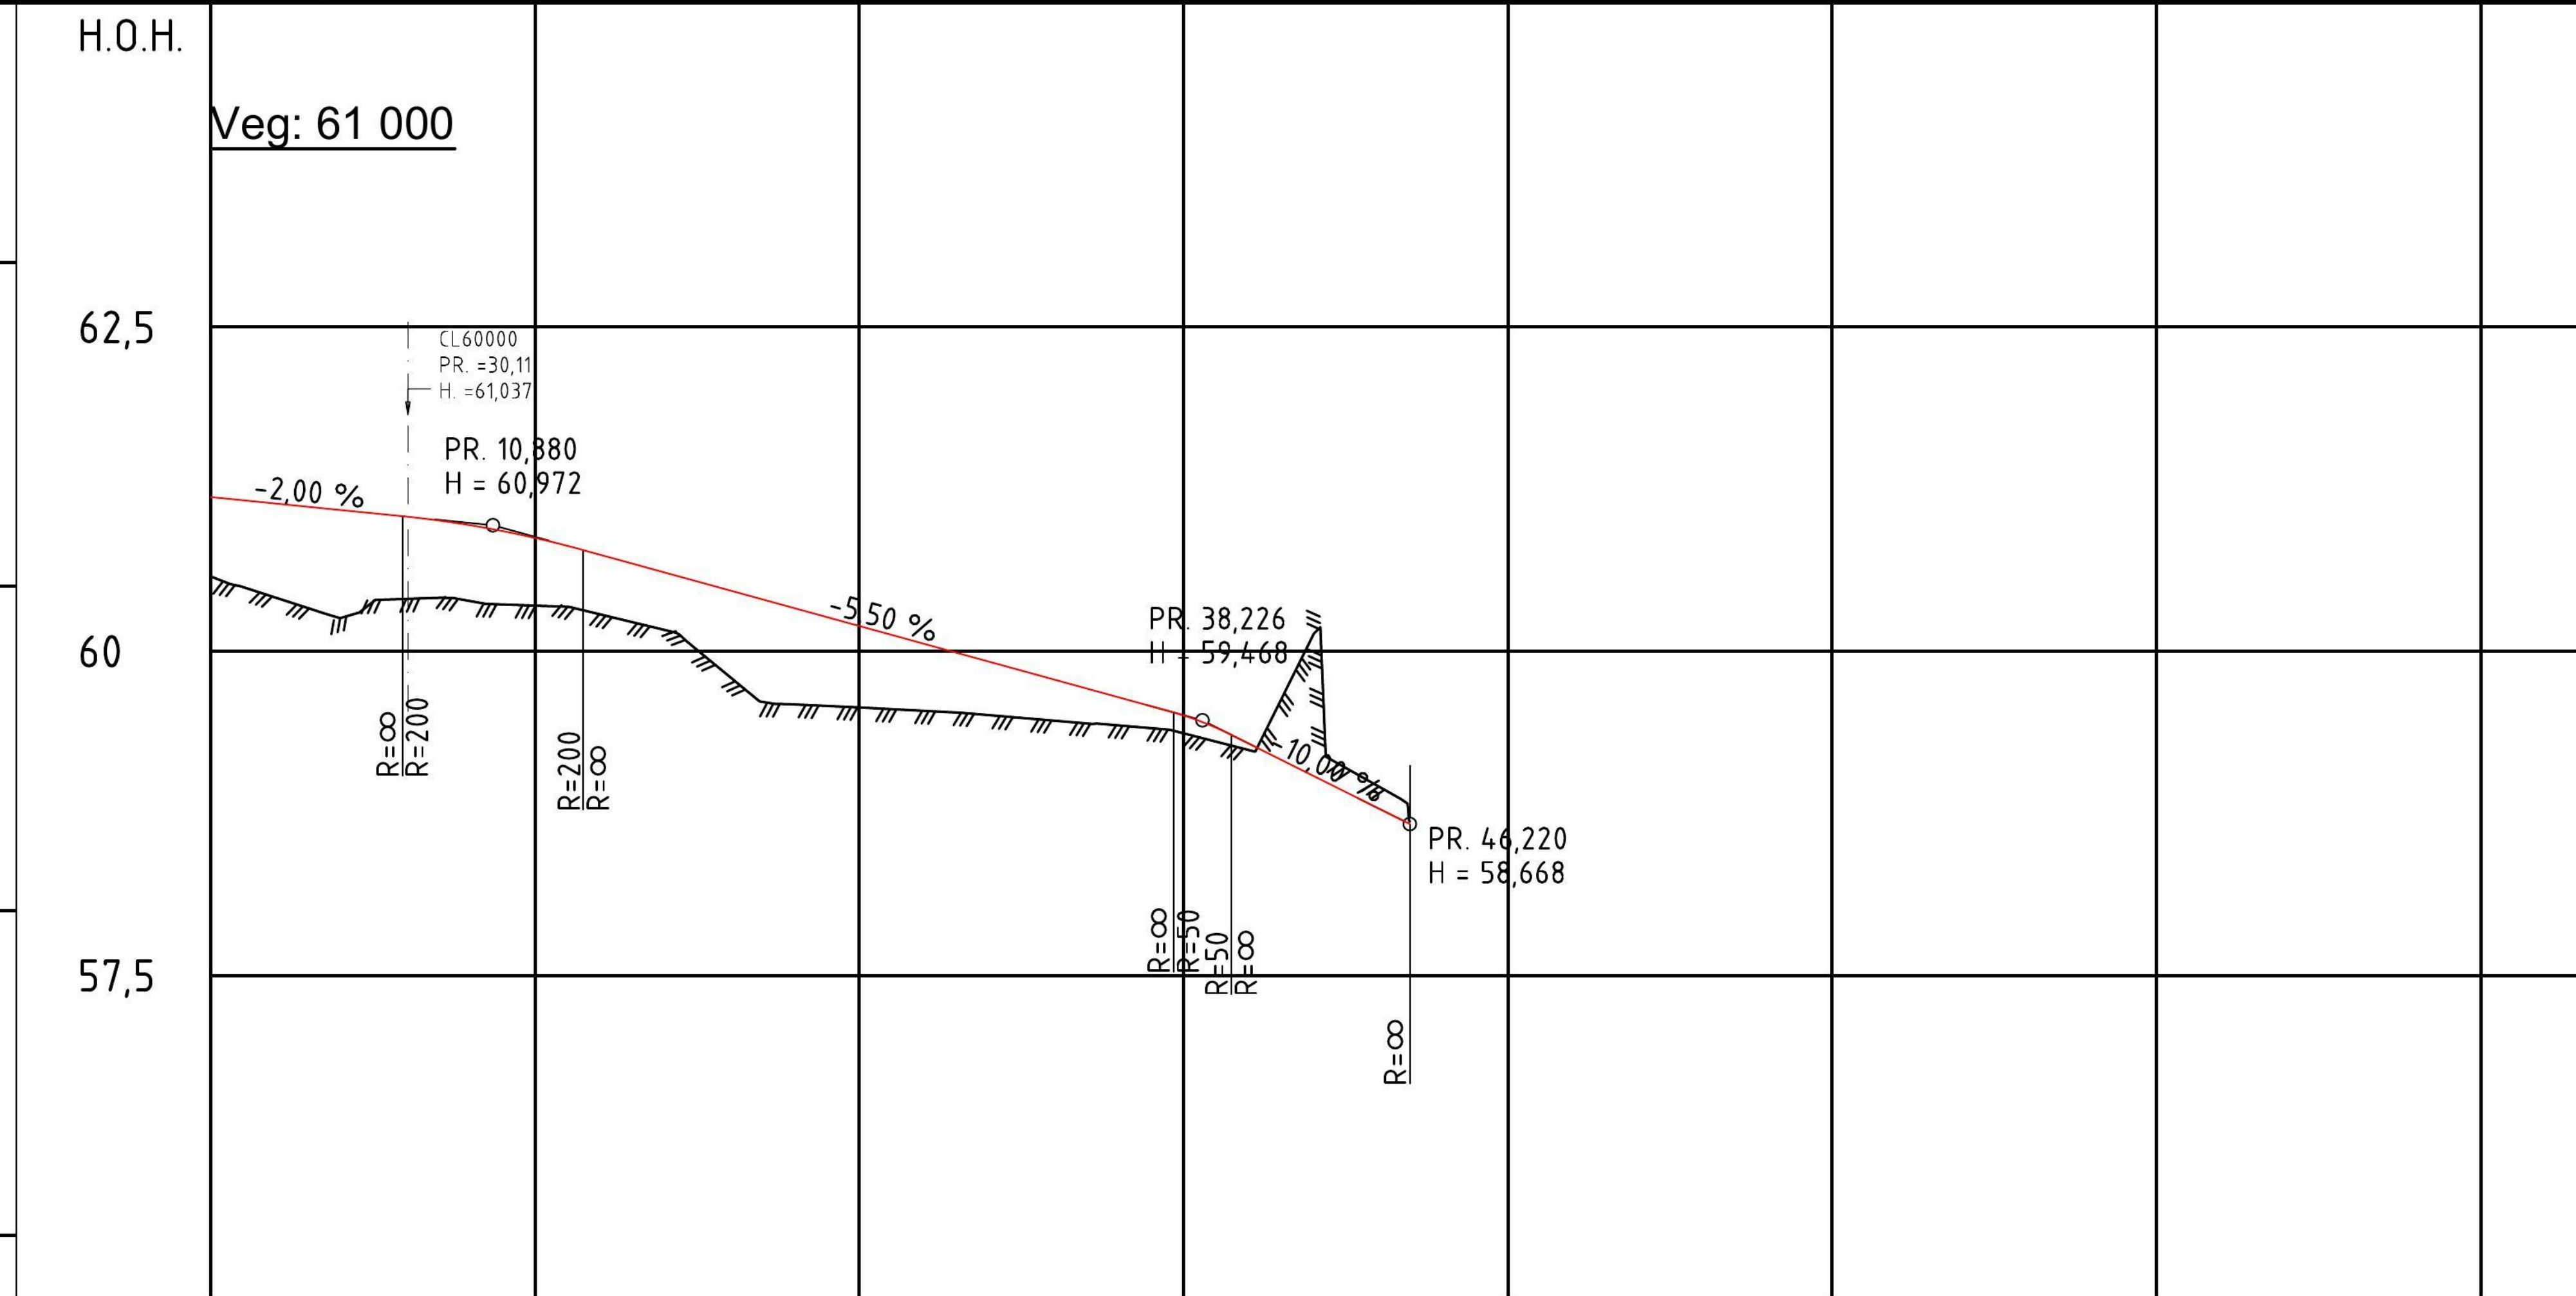

PROFIL NR.	0	12,5	25	37,5	50	62,5	75	87,5
HOR.KURV.			R=∞					
BREDDEUTV.								
TVERRFALL								
H.kj.b.k.								
V.kj.b.k.								
PROFIL H.	61,19	61,14	61,09	61,04	60,97	60,87	60,75	60,61
TERRENG H.	61,19	61,14	61,09	61,04	60,97	60,87	60,75	60,61
OVERBYGN.T.			48CM					



Tegnforklaring

- Prosjektet
- Veg
 - Fortau/ogs-veg
 - Kantsteins rom
 - Parkering
 - Drenerende asfalt
 - Henvisning vegmodell

- Breddeutvidelse
- Grusarmert gress
- Energianlegg, Trafo

Koordinatsystem: EUREF 89 UTM Sone 32 - Høydegrunnlag: NN2000



Head Energy UP AS
Org.nr: 925 044 299
T: +47 592 04 323
E: info@headenergy.no
www.headenergy.no

Kontor:
Nordåsdaalen 27, N-5235 Rådal
Vassbotnen 118, 4313 Sandnes

1	TIL GODKJENNING	19.01.24	THABI	KJAGI	SINBO
Rev.	Revideringen gjelder	Dato	Tegnet	Kontroll	Godkj.
	Prosjektnr.: 110911.006		Fag	VEG	
	Målestokk A1: 1:250/1:50		Tegnet	THABI	
	Koordinatsystem: EUREF89-UTM32N NN2000		Kontrollert	KJAGI	
	Dato: 19.01.2024		Godkjent	SINBO	
	Status: TIL GODKJENNING		Tegningsnr.: D001		Rev.: 1