



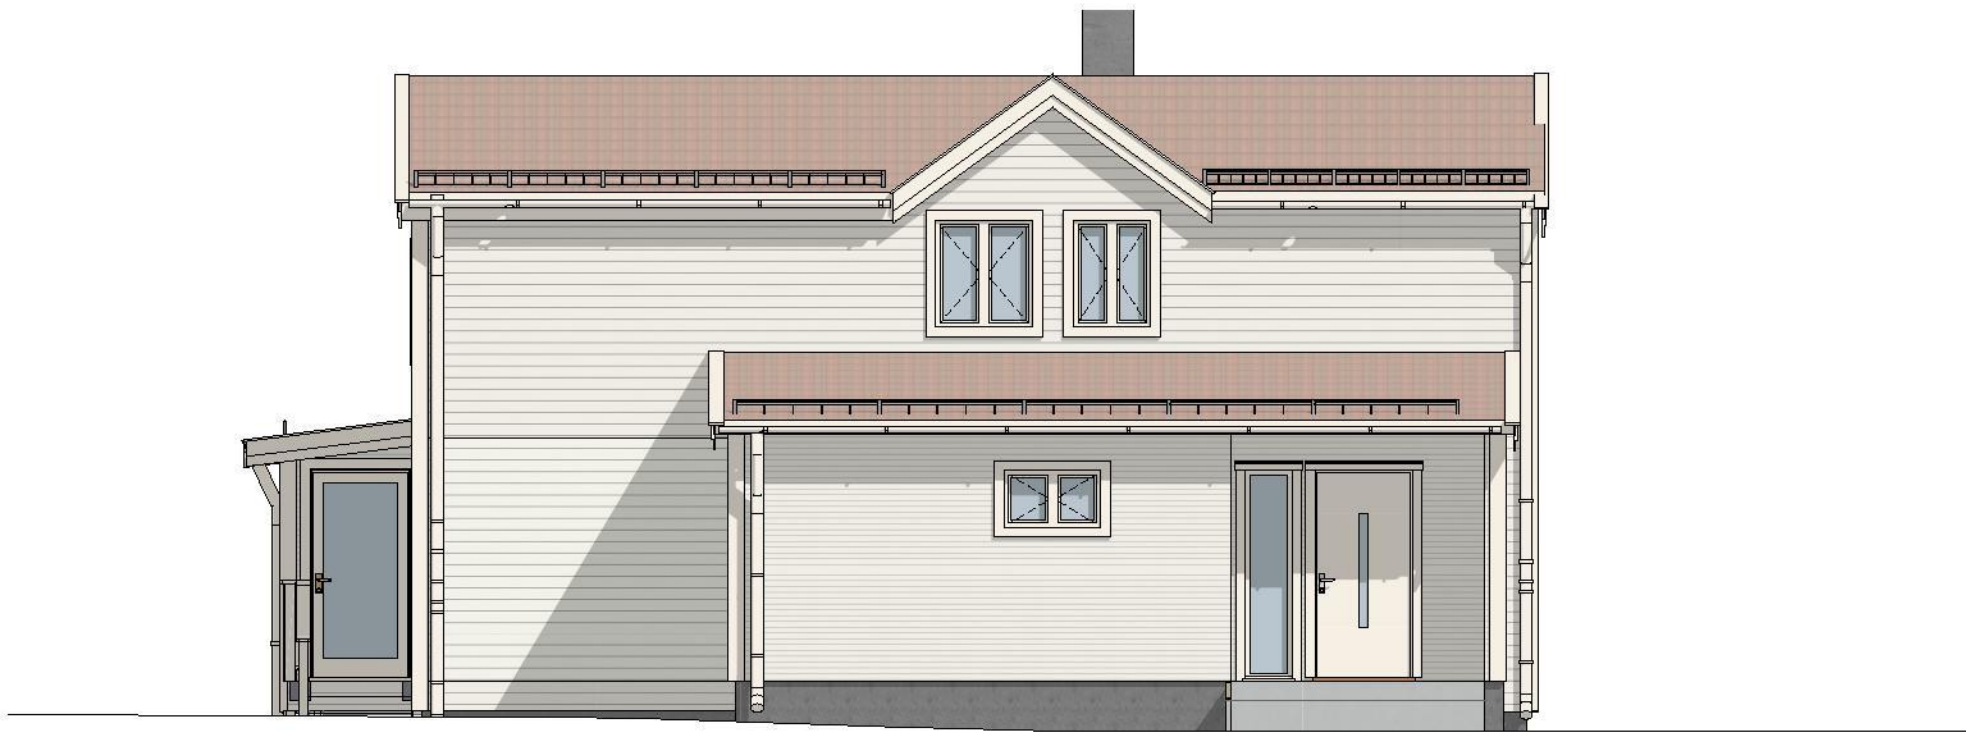

Fasade Nord

1:100

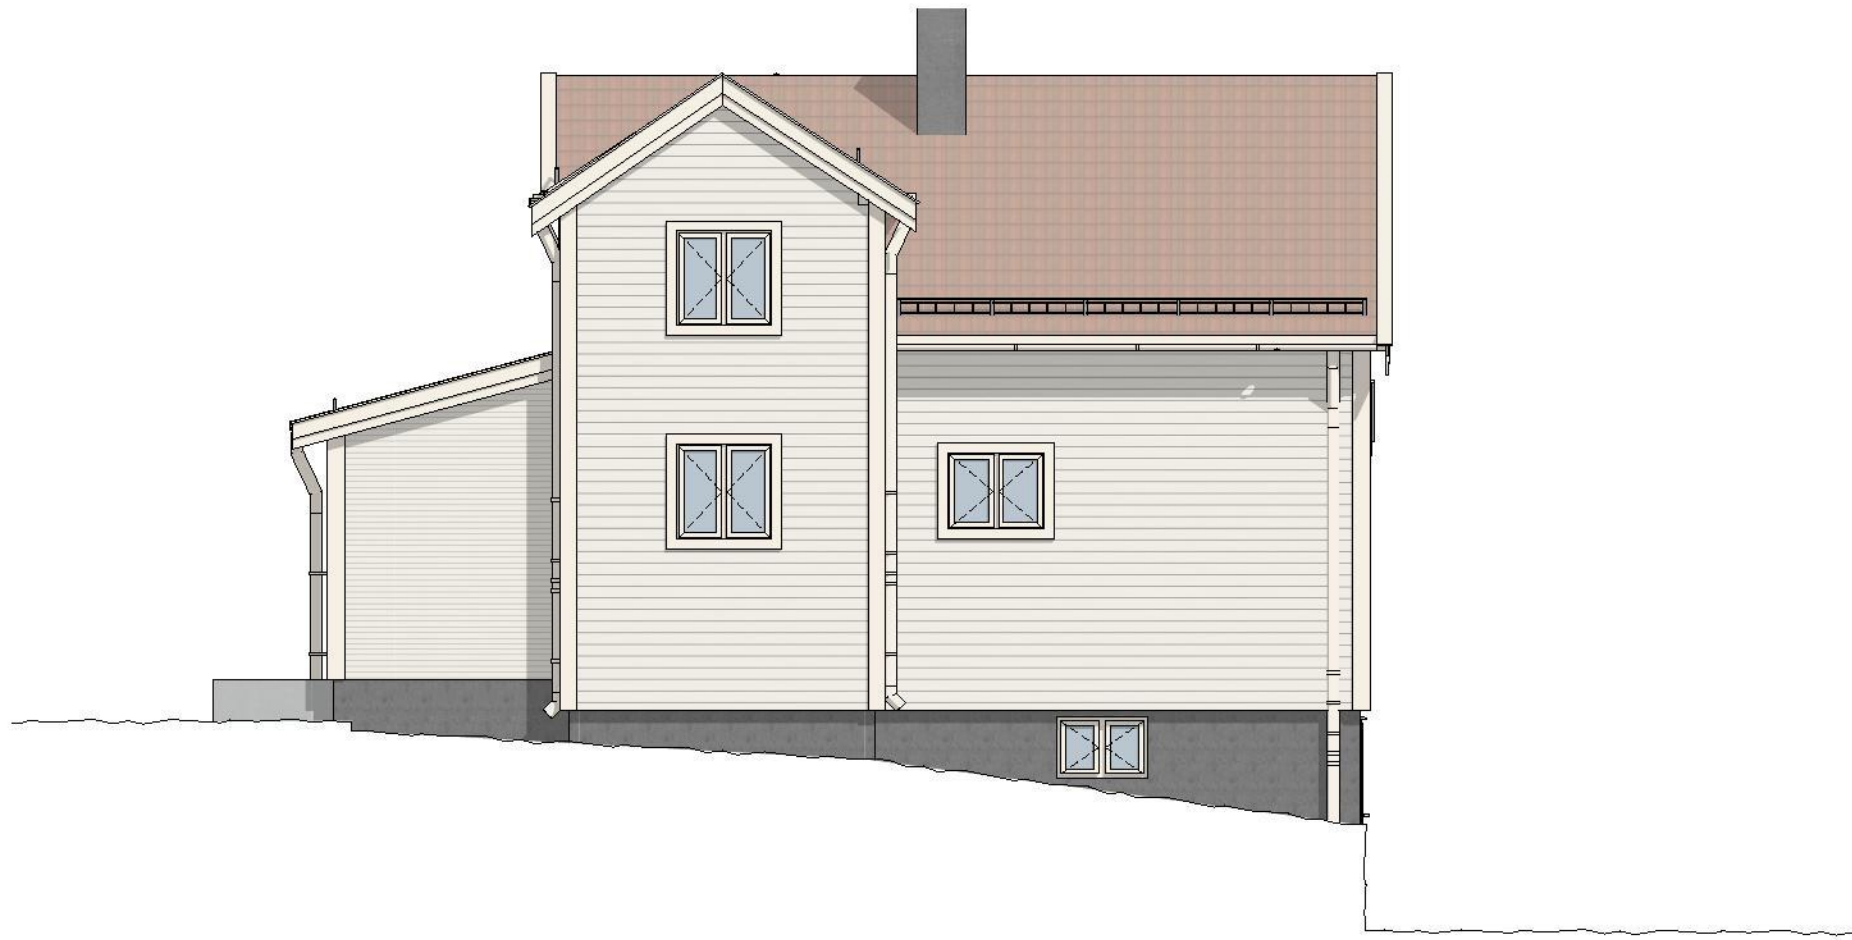

Fasade Vest

1:100

MERKNADER:

Forbehold: Det tas forbehold om mulig nedforet himling pga. tekniske føringer. Arealer er beregnet ut fra tegning og er oppgitt iht. NS3940. Tekniske forhold i bygningsmessig utførelse kan påvirke arealer i mindre grad.

Boenhet i småhus skal oppføres med skorstein. Kravet gjelder ikke dersom boenheten oppføres med vannbåren varme. Unntak for skorstein forutsetter at vannbåren varme dekker minimum behov for romoppvarming i stue eller tilsvarende rom. Det kan benyttes annen oppvarming på baderom, soverom eller rom som skal holde lavere innetemperatur. Det er ikke krav til vannbårent varmebatteri for ventilasjonen, og det omfatter heller ikke oppvarming av varmt tappevann.

Det er beregnet sikkerhetsglass på alle vinduer/balkongdører med brystningshøyde mindre enn 0,8 m på bakkeplan, samt der det er angitt verandaer/uteplasser i andre etasjer. Dette kan fravike fra perspektiver i huskatalogen og det kommer fram av dør- og vindusskjema hvilke vinduer/balkongdører dette gjelder.

Sikkerhetsglass leveres ihht. Plan og bygningsloven og glassbransjens anbefalinger.

Prosjektering iht TEK 17.

NB! Før bestilling av kapitalvarer som vindu, precut, takstoler etc. vil det være behov for en arbeidstegning slik at underlaget er gjennomprosjektert for best mulig sikkerhet i forhold til riktige leveranser. Norgeshus AS kan ikke ta ansvar for evt. feil som kan oppstå hvis bestillinger blir gjort på et underlag som ikke er detaljprosjektert.

NB! Inntegnet terreng er veiledende, og kan avvike fra ferdig opparbeidet tomt.				
A	19.12.23	Justering badersvegg	AH	AH
Index	Dato	Beskrivelse	Sign	Kontr.

Oppvarmet BRA:	BYA:	VOLUM:	Koordinatsystem:
167,1 m ²	102,8 m ²	m ³	UTM-XX
BRA U01 + H01 + H02 + Vinterhage:		BRA TOTALT:	Høydesystem:
40,5 + 74,1 + 52,5 + 14,6 m ²		181,7 m ²	NNXXX
		Utnyttelse %BYA:	MUA:
		%	200 m ²

BYGGKommune:	GNR/BNR:	POSTNR:	POSTSTED:
Stavanger	164/16	4170	Sjernerøy
ADRESSE:			MOH:
Norheimsbergveien 93			moh

TEGNET AV:	KONTROLLERT AV:	DATO:	FORMAT:
AH	BW	15.12.23	A3

PROSJEKT:	PROSJEKTNR.:
Oppgradering av enebolig	23-0617
TEGNINGEN VISER:	TEGNING NR.:
Fasade Nord og Vest	ARK-2-3-01
STATUS:	MÅLESTOKK:
Byggemelding	1:100

TILTAKSHAVER:
Tone Karin Viken

BYGGEFIRMA:


INGENIØR- OG ARKITEKTKONTORET NORGESHUS AS, PB 161, 7223 MELHUS, TLF: 72 85 69 00	
TEGNINGEN ER BESKYTTET ETTER LOV OM OPPHAVSRETT OG EIES AV NORGESHUS AS. TEGNINGER SKAL IKKE BENYTTES UTEN VÅR TILLATELSE. TEGNINGEN GJELDER IKKE SOM ARBEIDSTEGNING.	REV. A