


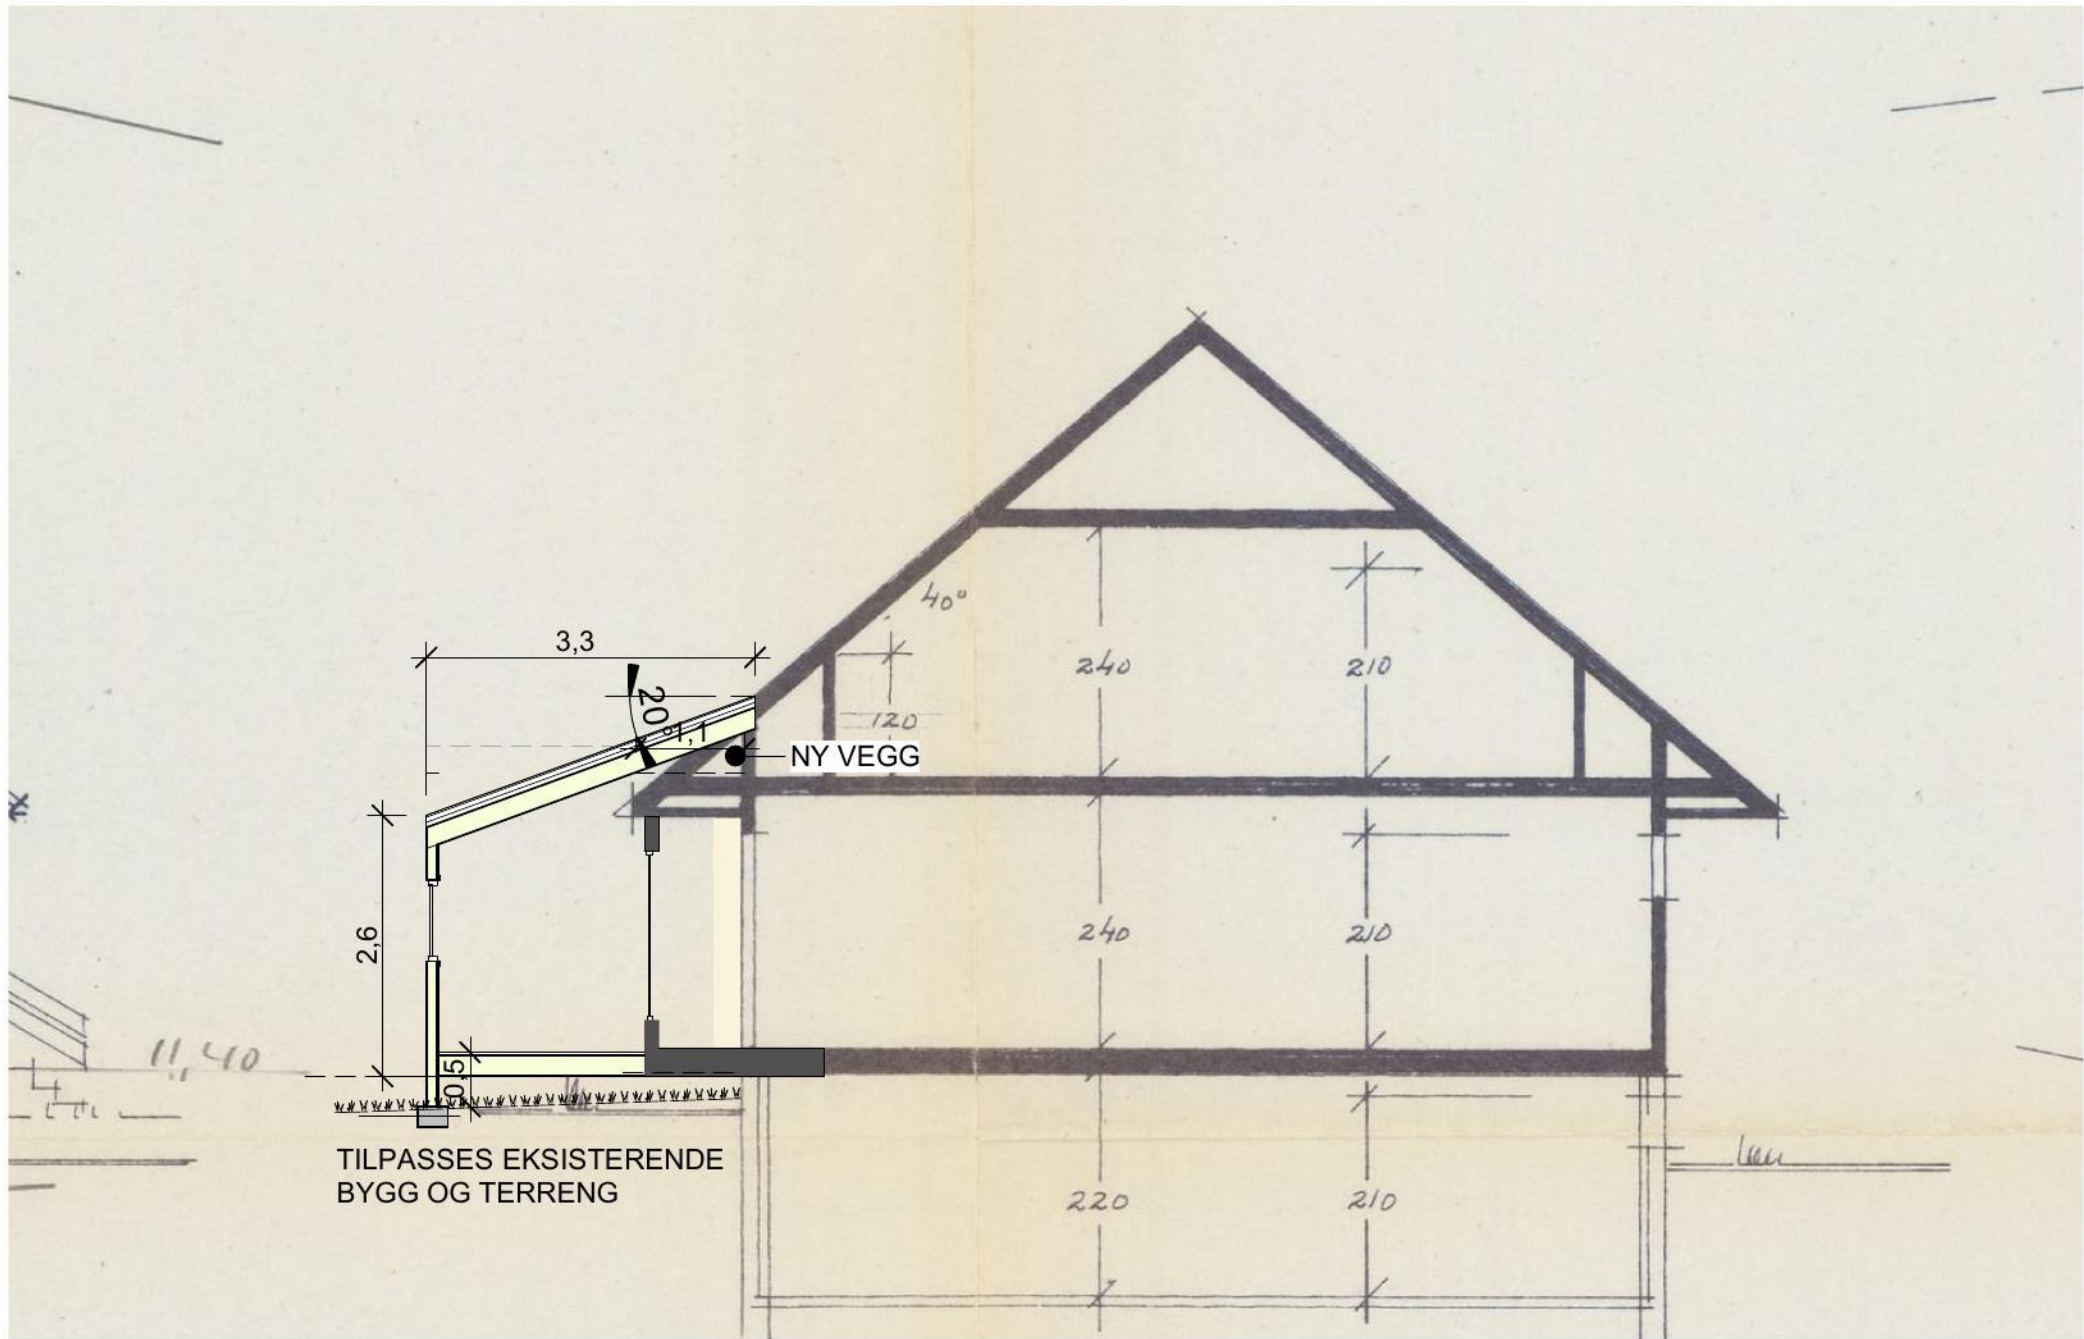

MERKNADER: Vi står ikke ansvarlig for de oppgitte mål og BYA på eksisterende konstruksjoner Ny konstruksjon må tilpasses eksisterende. Faktisk terreng og koter må kontrolleres.	FASE:		Rev. Revisjonen gjelder ROGALAND FYLKESKOMMUNE HINNAVÅGEN 56 SNITT Autodesk Revit	Utført		Kontr.	Dato
	FORELØPIG	X		Målestokk	Dato	12.01.24	
	BYGGESAKSTEGNING			1 : 100	Tegnet	AMA	
	ARBEIDSTEGNING				Kontr.	SL	
	SOM BYGGET			Arkstørrelse A3	Prosjektnr.	10944	
				Tegningsnr.	A102		Rev.