

\\SVGDC\N\Prosjekt\02\7\27169\7\27169-03\ARBEDSOmråde\03_Tegninger\1_Lark_gamleieven_33.dwg - Layout: 100%

BESKRIVELSE

Port
Mellom terrasse og inngangsparti skal det være en port i samme høyde som rekkverk.

Vindu
Alle vinduer på sørsiden blir skiftet ut. Stuevindu på østside, blir skiftet ut og tilpasset nytt inngangsparti.


Inngang
Ny dør med kodelås eller avtrykk- lås. Produkt avklares med grunneier.

Rekkverk
Støyskjem, terrasse, balkong og trapp skal ha lik utførelse med liggende spiler


Fasaden er tegnet opp på grunnlag av innmålinger. Avvik fra eksisterende forhold må likevel påregnes. Det forutsettes kontrollmålinger og tilpasninger på stedet.

Nødvendig prosjektering i forbindelse med utsparinger for vinduer og endring av fasaden utføres av entreprenør


Fasade
Utomhus
M 1:50 (A1)

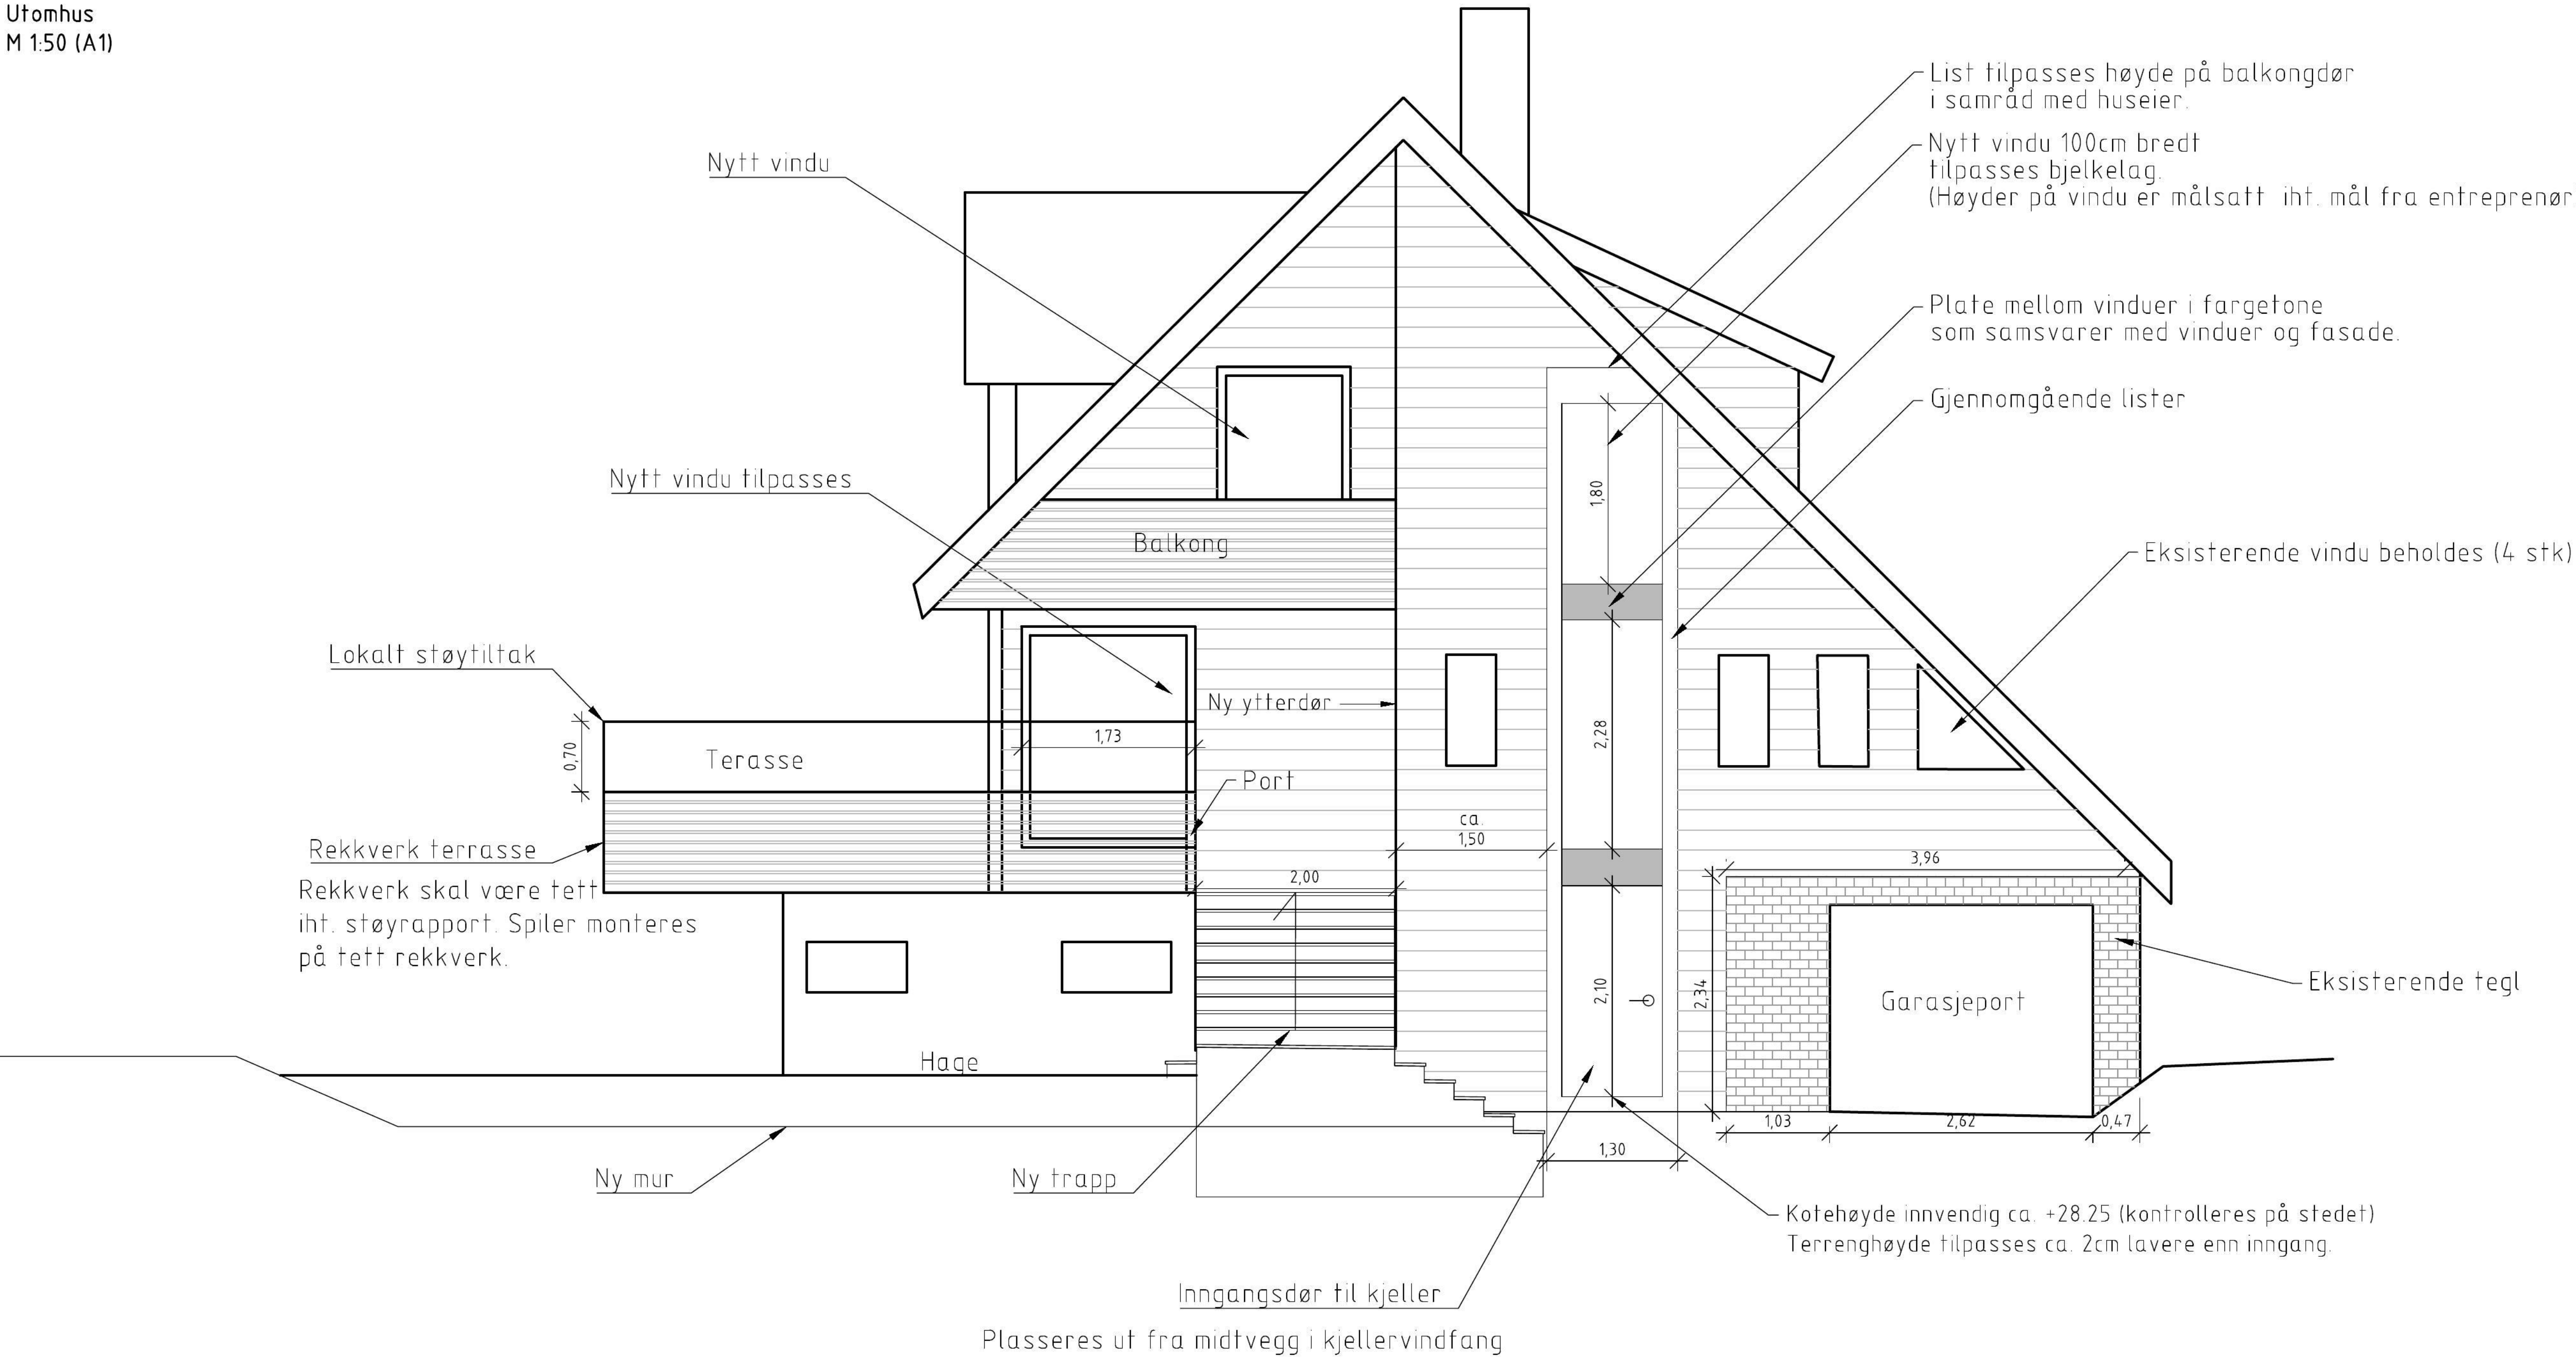

Fasade rekkverk
M 1:50 (A1)

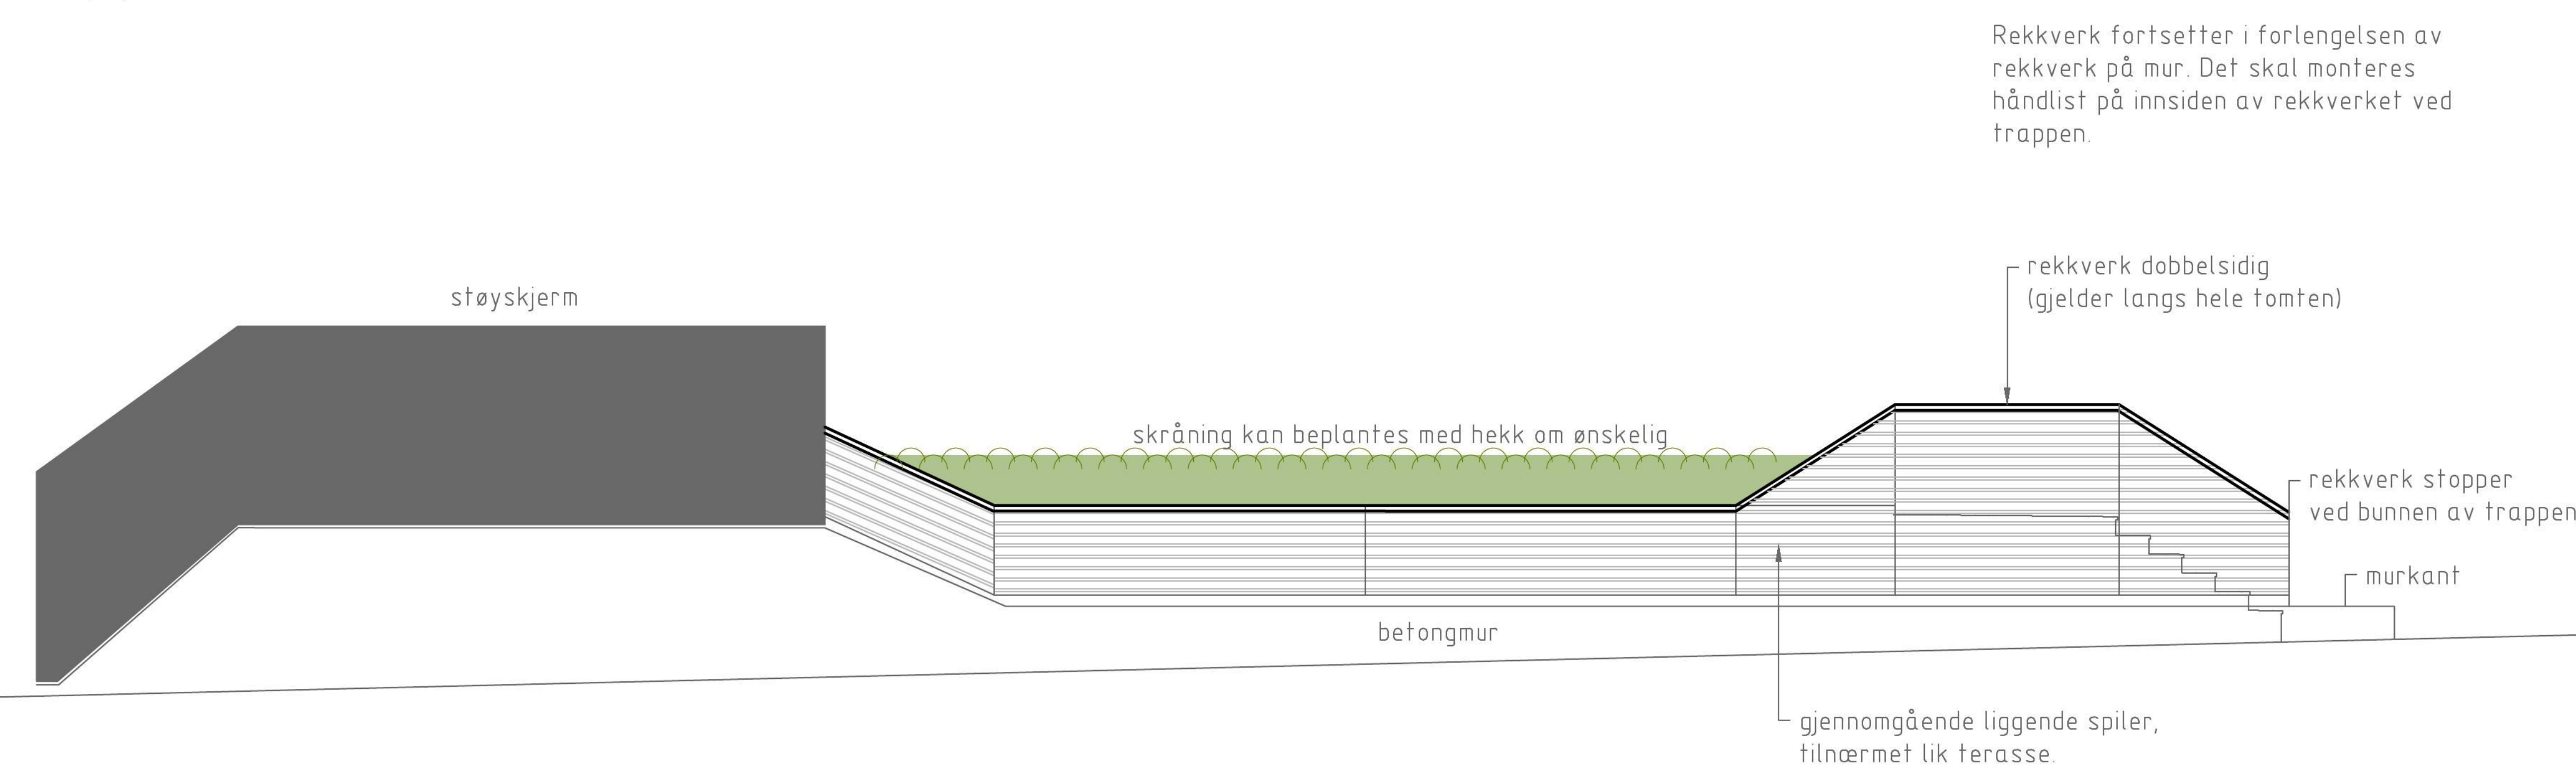

Plansituasjon hage
M 1:50 (A1)

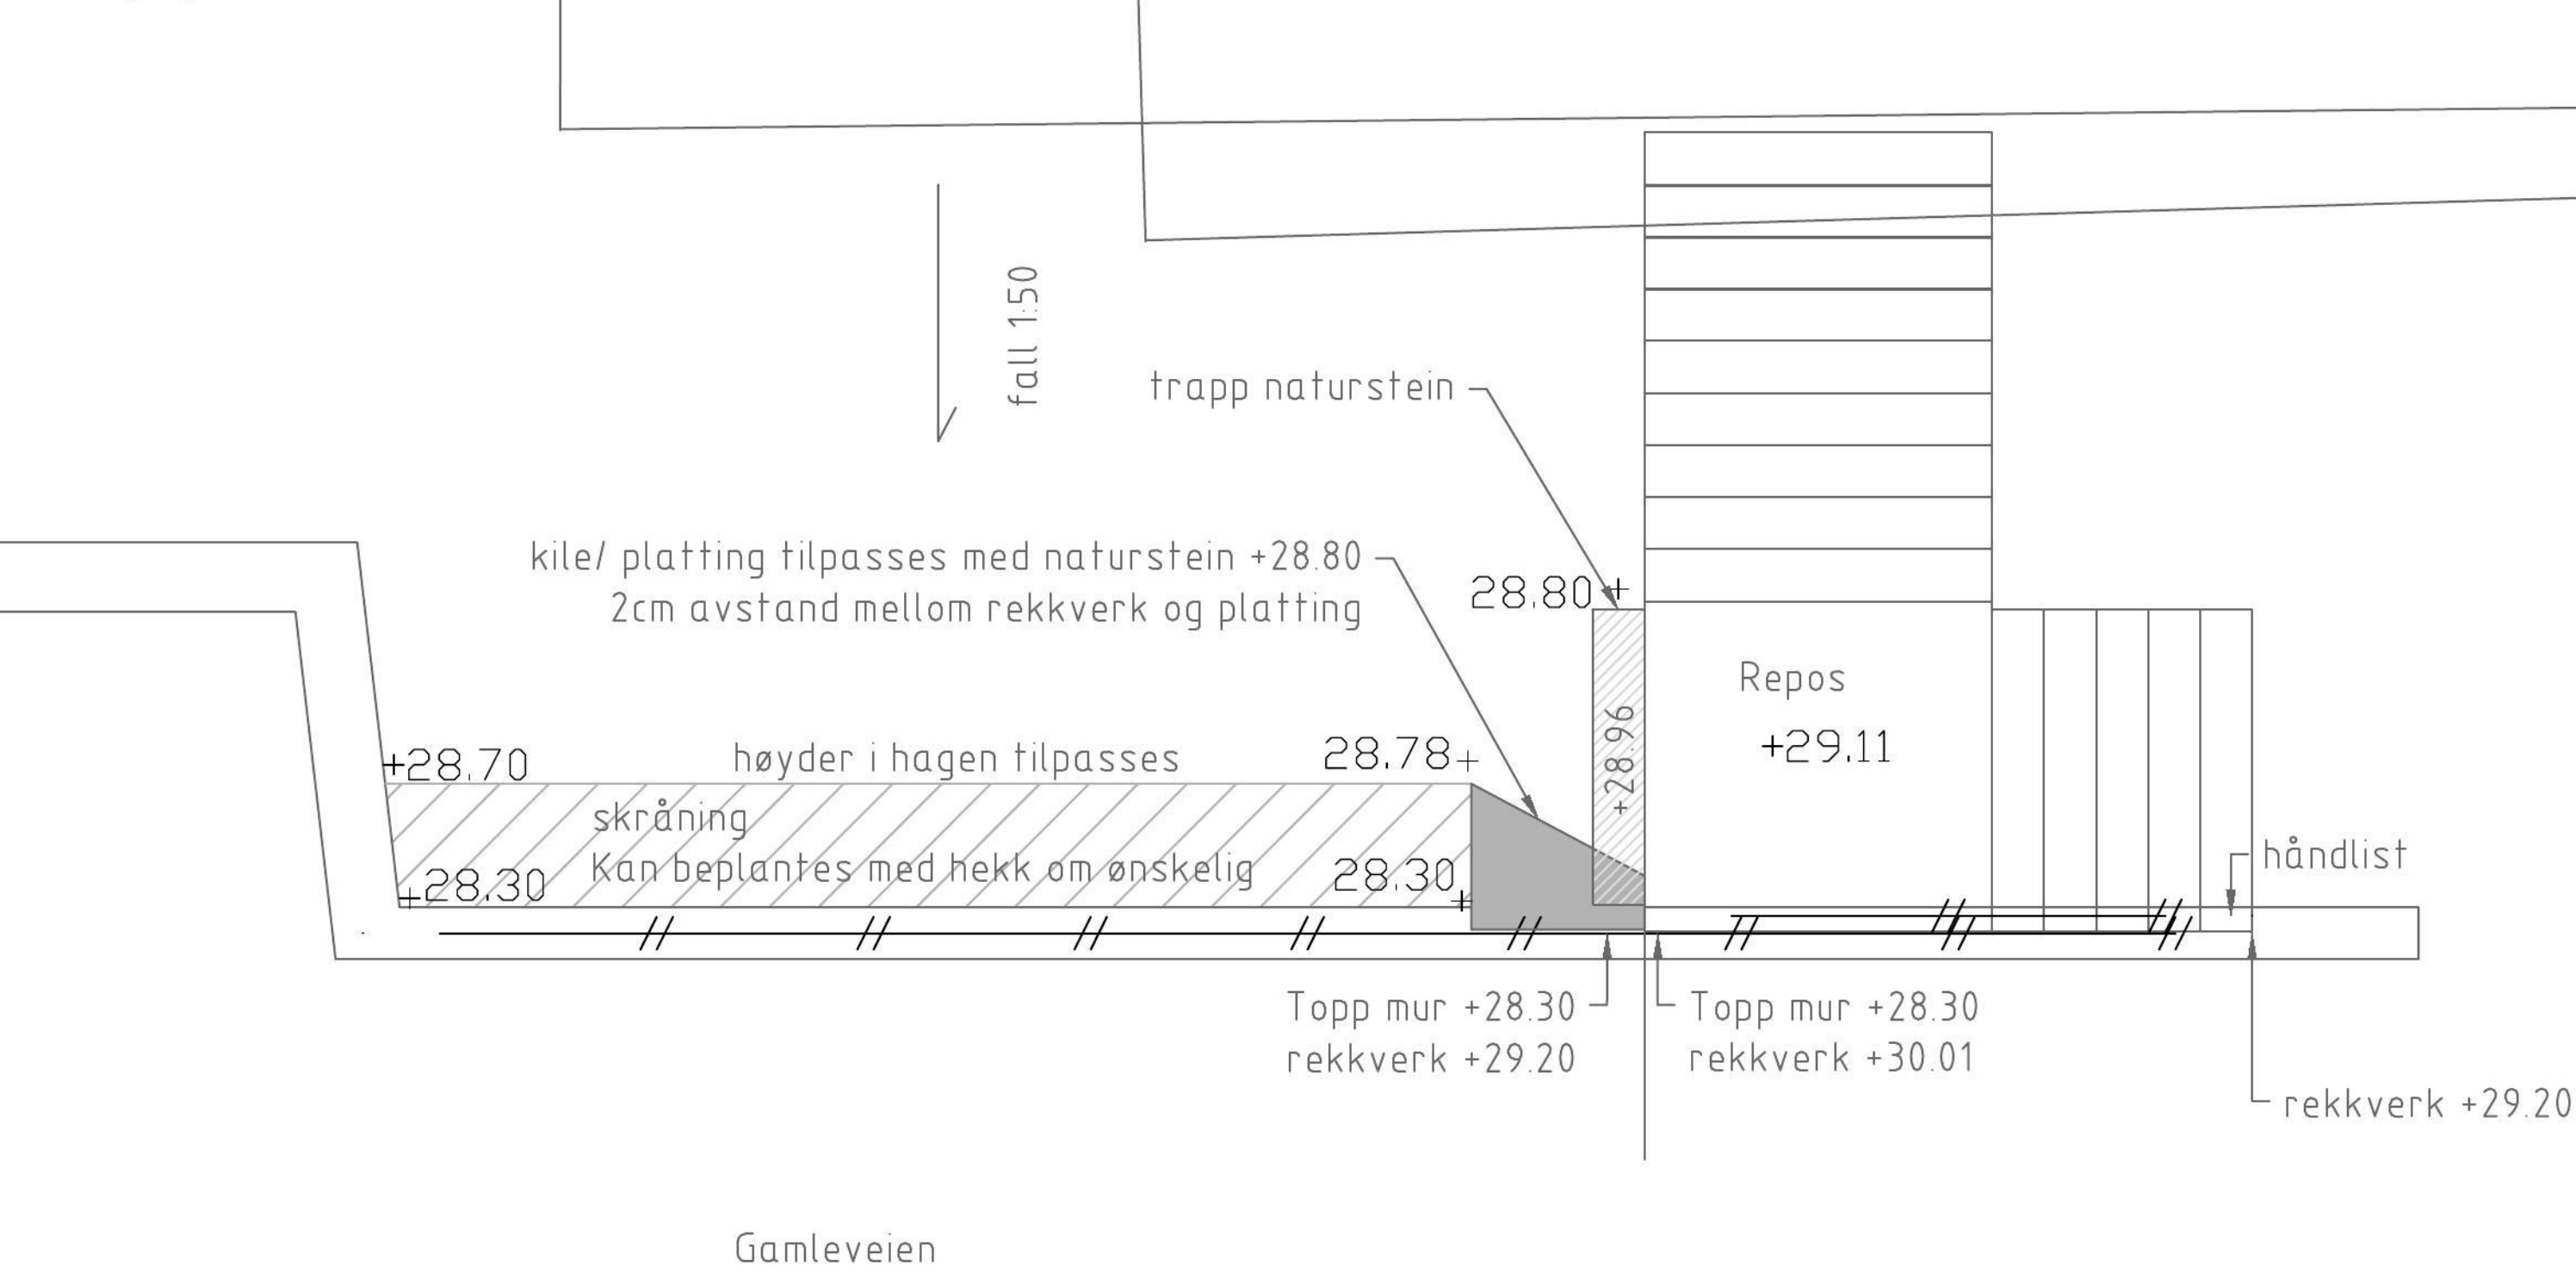


Akustikk

Nye vindu i soverom i tetg. kan påvirke støysituasjonen.
Viktige momenter:
- Det anbefales at triangulærevinduet til høyre flyttes til tak ($R_w+C_{tr} \geq 38$ dB).
- Stort vindu er ok med forutsetning av at man benytter $R_w+C_{tr}=38$, og det trekantede vinduet blir flyttet til taket.
Det er tatt utgangspunkt i at nytt takvindu får et areal på ca 1m² og at det nye gulv-tak-vinduet får et areal på ca 3,6 m².
Dersom dette avviker vesentlig fra planen kreves en ny beregning.

se forøvrig. Konstruksjonstegning

Snitt rekkverk
M 1:50 (A1)

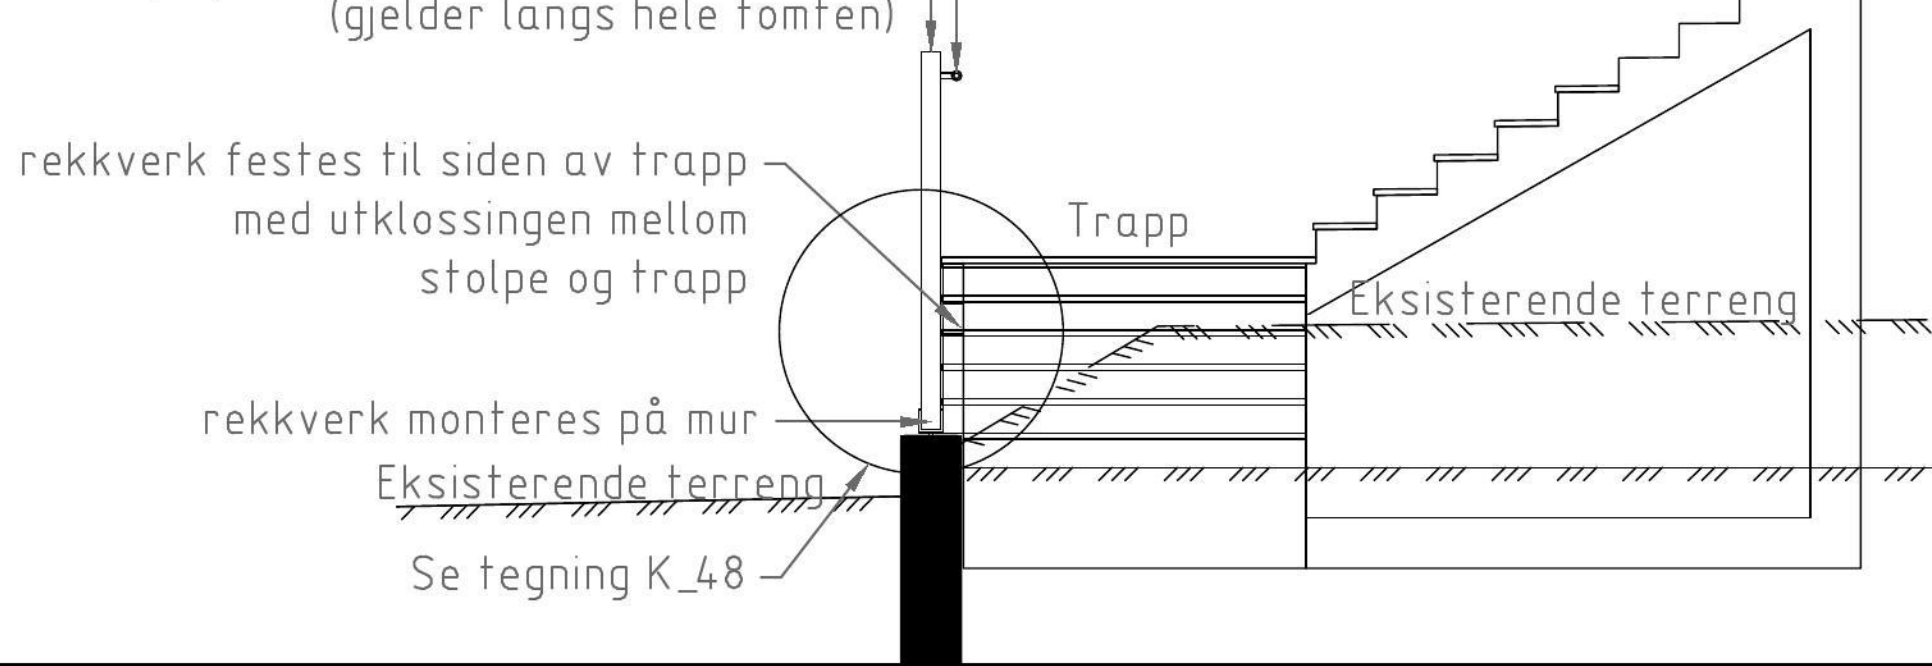

F	Justering av vindu	25.06.2018	GNS
E	Uiforming rekkverk	07.06.2018	GNS
D	Plansituasjon mur og gjerde tatt bort etter avtale med Stavanger kommune	08.05.2018	GNS
REV.	ENDRING	DATO	SIGN.
 STAVANGER KOMMUNE Bymiljø og utbygging Plan og Anlegg		REG PLAN	
		TEGNER	GNS
		KONTR.	HTB, AB, CB,
		SKALA	1:50 (A1)
PROSJEKT: GAMLEIEVEN		KONSULENT MULTIKONSULT	HB SYSTEM
OMRÅDE: HINNA		TEGNINGSNUMMER	TYPE
ANLEGGSTYPE: VVA		391476523	J50
TEMA: Fasade gamleieven 33		REV.	F