



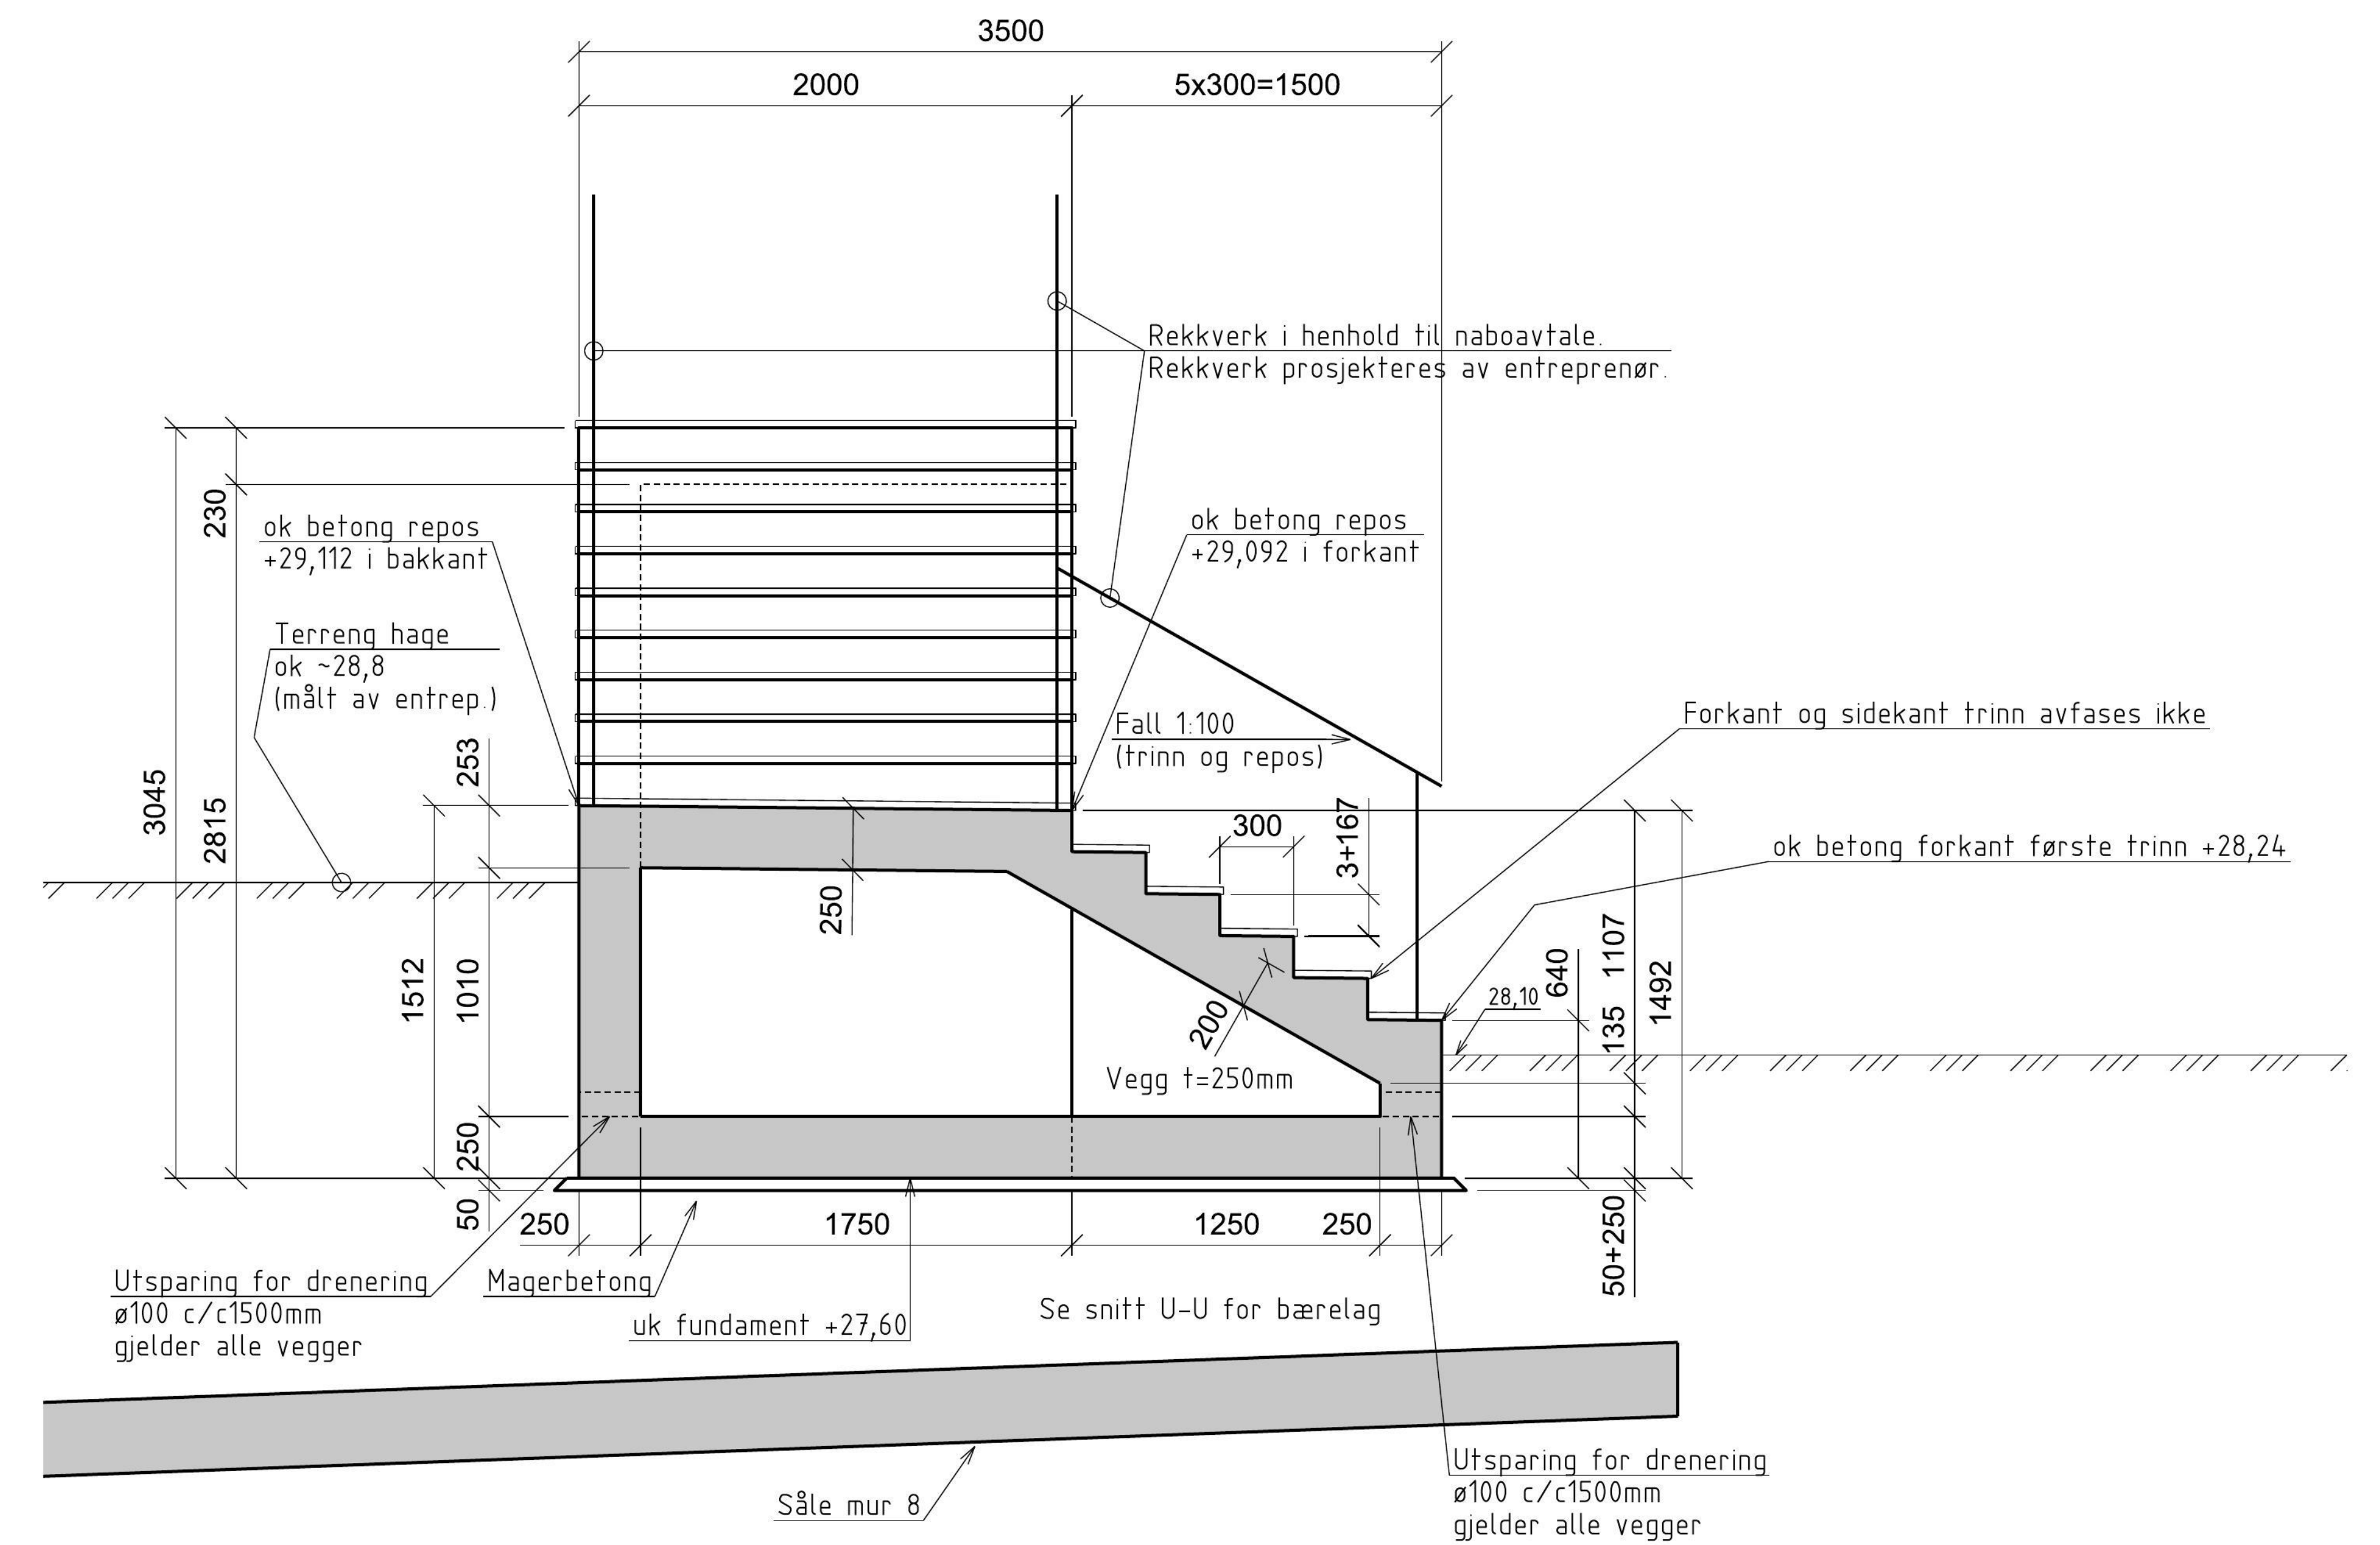

SNITT U-U
1:25

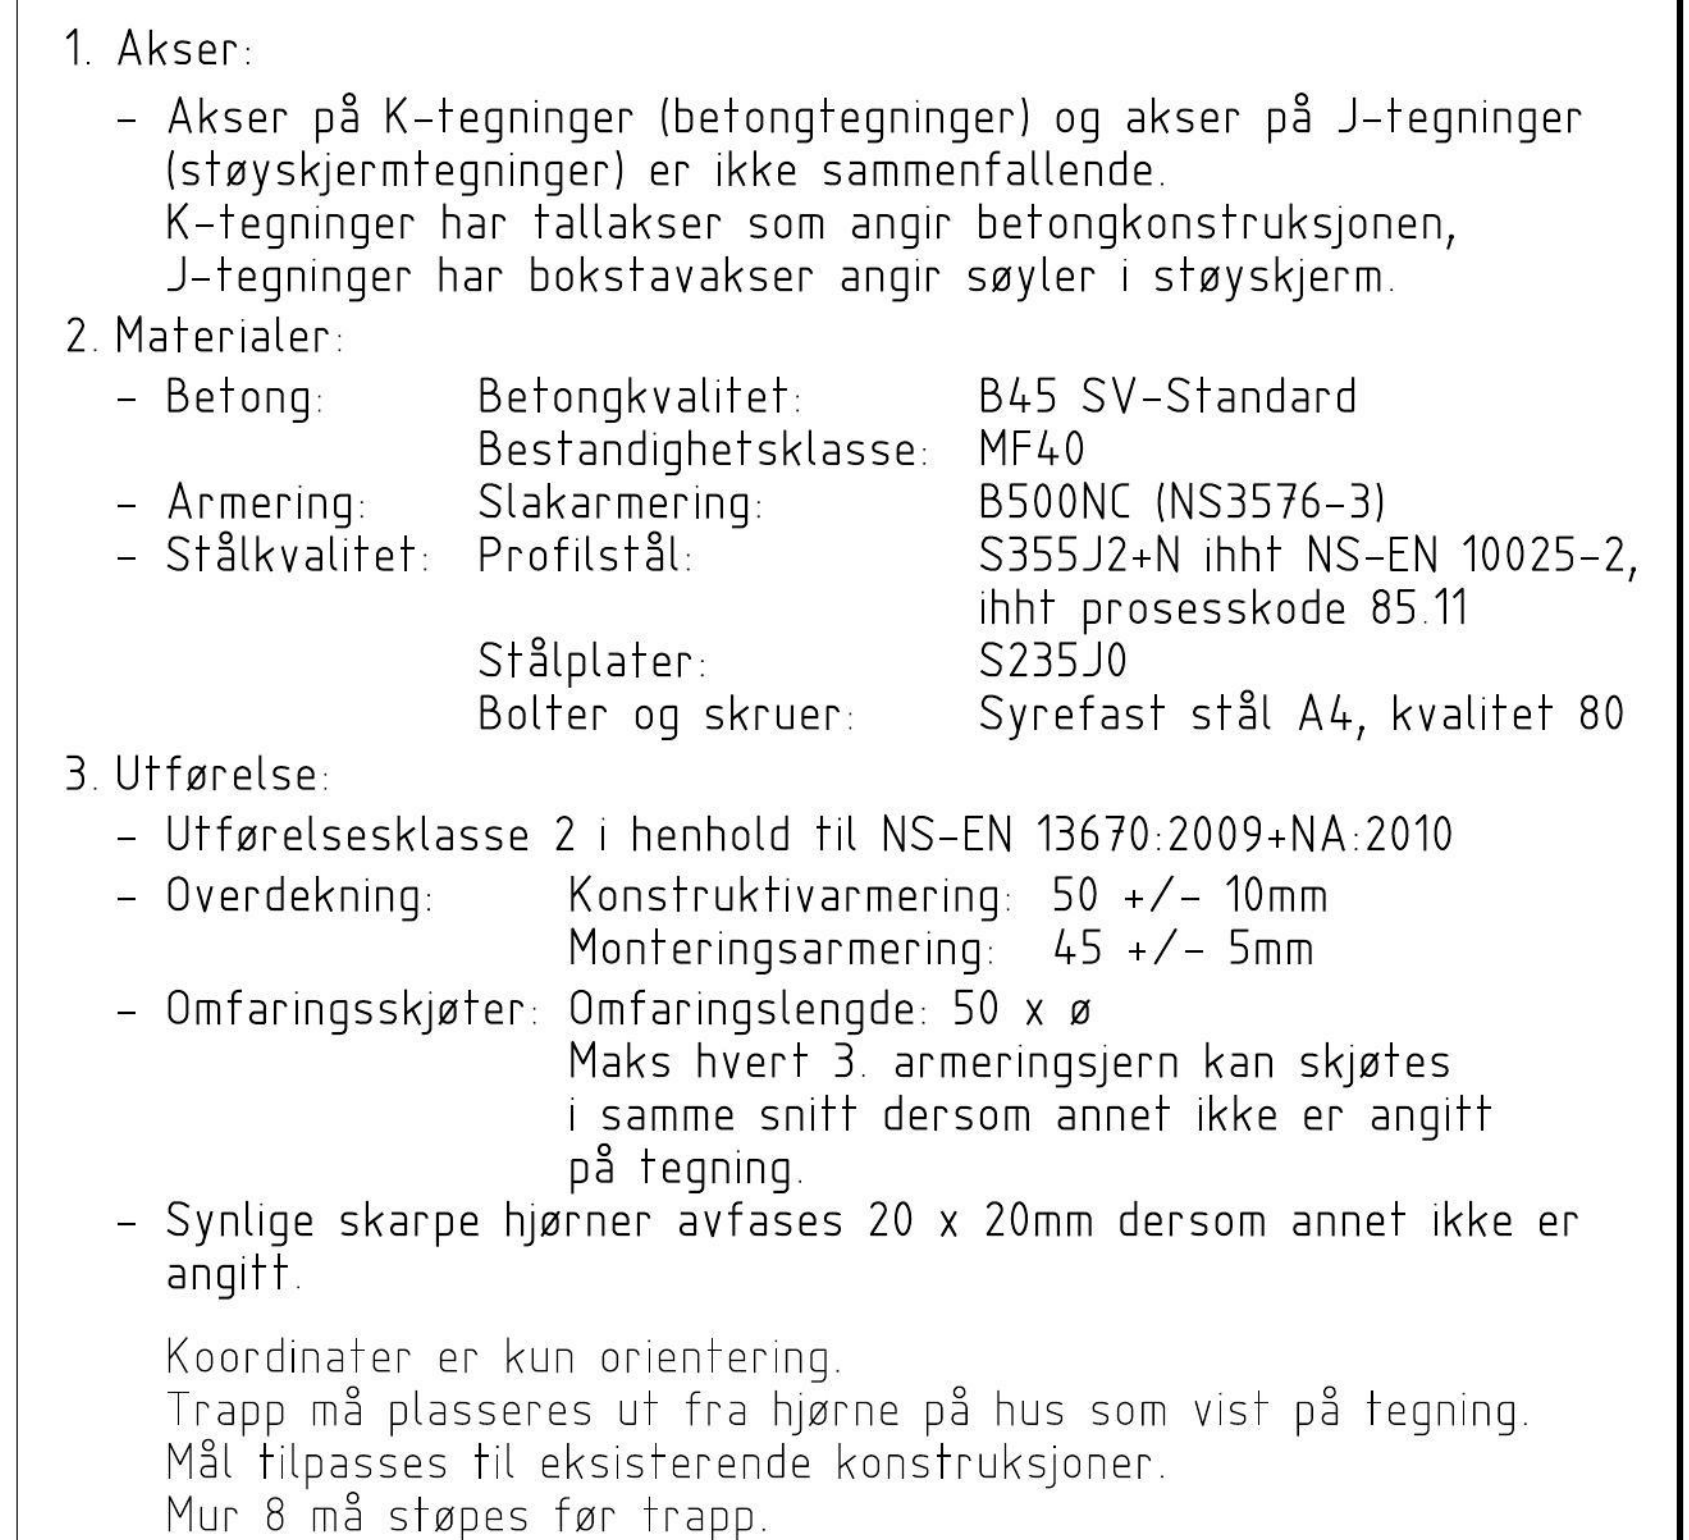

Z	Son bygget		25-03-2019	CNB	
REV	ENDRING		DATO	SIGN	
 STAVANGER KOMMUNE Bymiljø og utbygging Plan og Anlegg		REG.PLAN	2004		
		TEGNER	CNB		
		KONTR.	AIS		
		SKALA	1:20/25:100		
		HØRSYSTEM	NN2000		
PROSJEKT: GAMLEVEIEN		KONSULENT			
OMRÅDE: HINNA		Multiconsult			
ANLEGGSTYPE: Konstruksjon		TEGNINGSNUMMER			
TEMA: Trapp 1 Plan, oppriss og snitt T-T og U-U		391476523	TYPE	Z	
			REV.		