


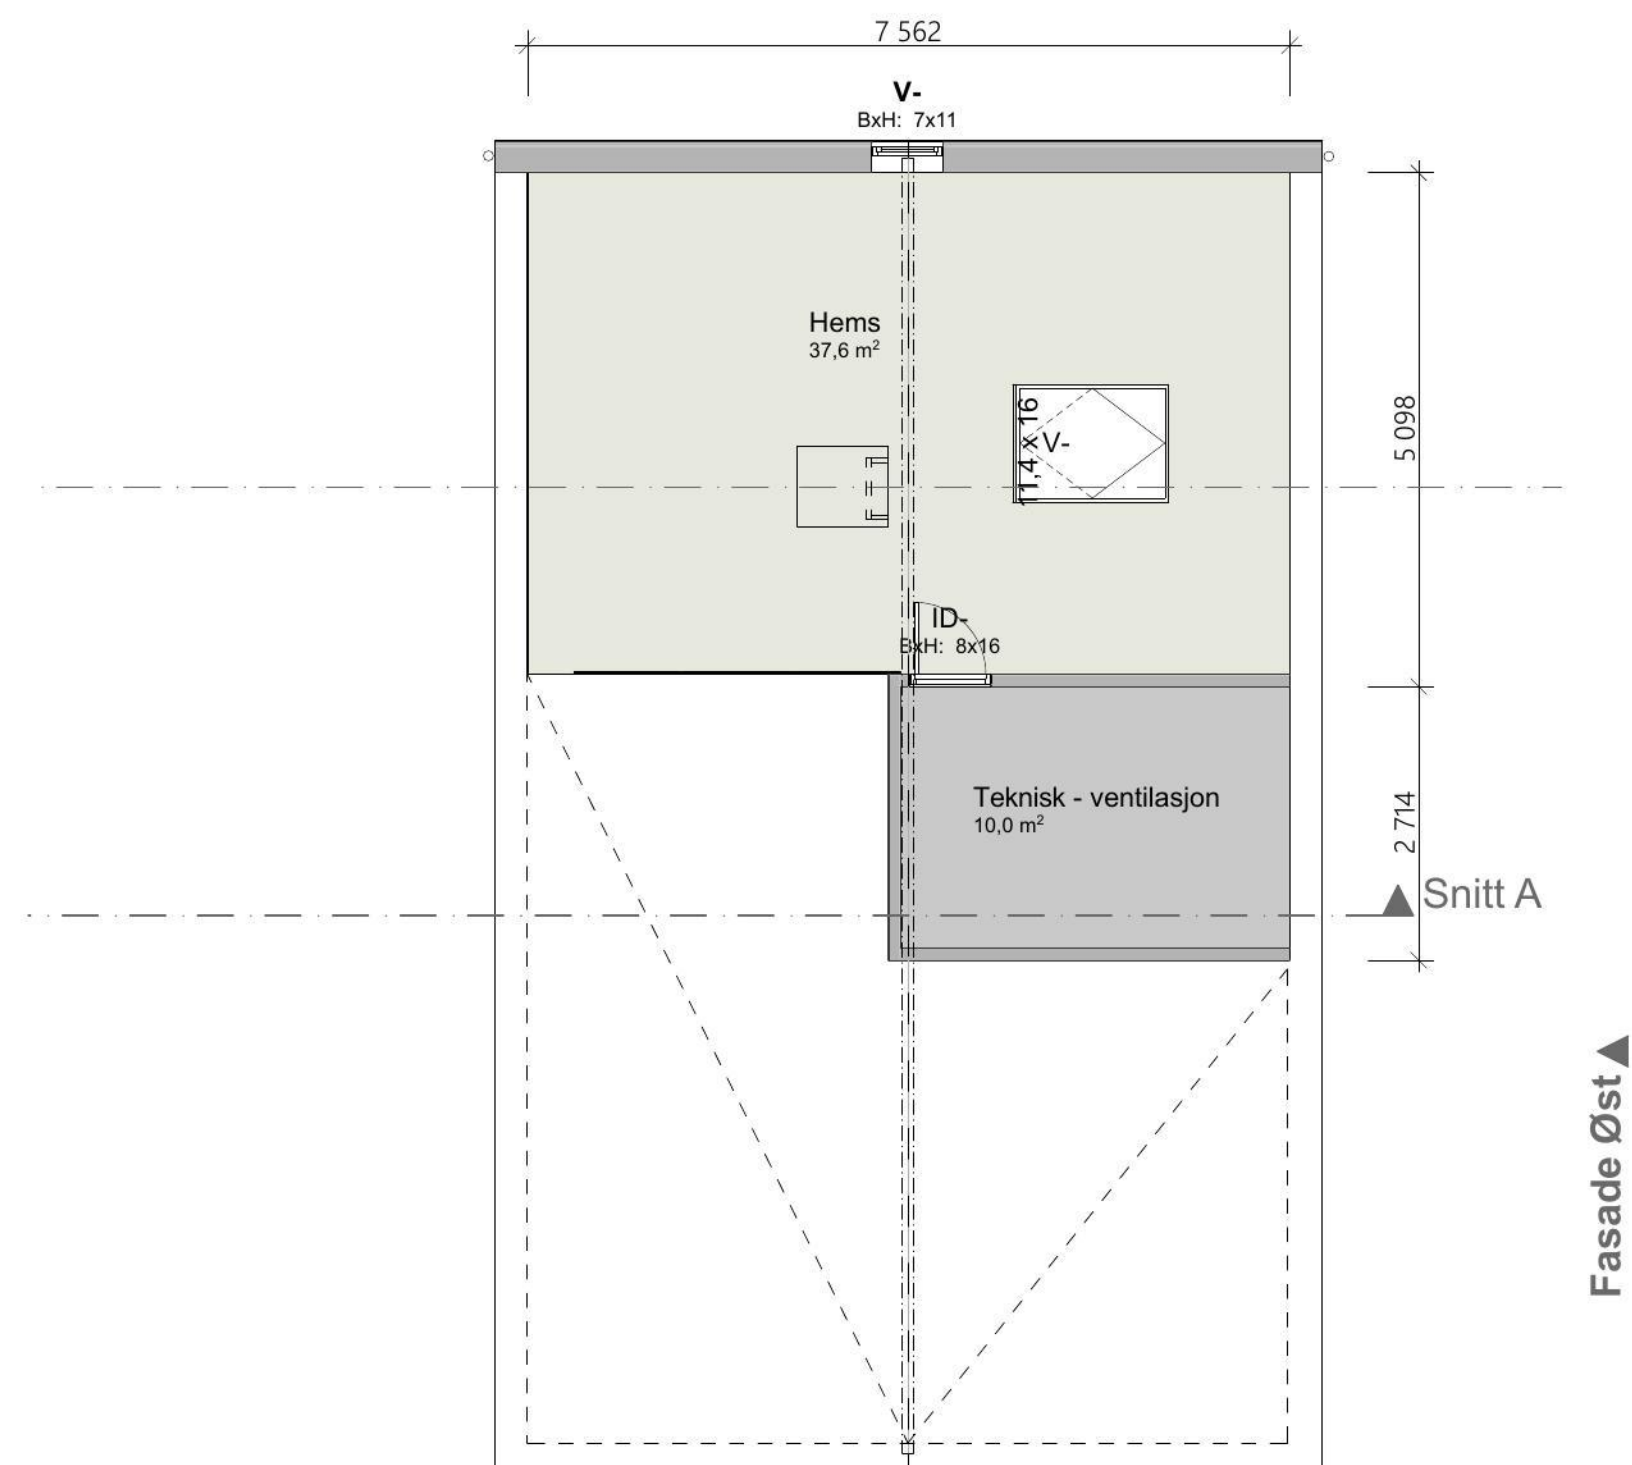

Tegninger kun utarbeidet for rammesøknad/deling. I forbindelse med søknad om IG, må det tas kontrollmåling, før utarbeidelse av prosjekterings/arbeidstegninger.

Rev.:16.12.23	
Rev.:03.03.23	
Rev.:19.10.22	
Rev.:06.10.22	
Prosjekt: Enebolig, carport og bod	Kontroll prosjekt:
	Sign.: t.th Kontroll: t.th.
Adresse: Buflåtveien 4 4018 Stavanger	Gnr/Bnr. 17/835 A:1002 m2
Arkitektur: Botakst as Gretebakken 12 4355 Kvernaland	 bygg og taksttjenester www.botakst.no
© Alle rettigheter tilhører utførende for arkitektur, kopiering eller bruk av disse tegningene er forbudt uten skriftlig samtykke	Dato: 01.09.2022
Tegning: Plan hems	Målestokk: 1:100
	Tegningsnr.: E3