



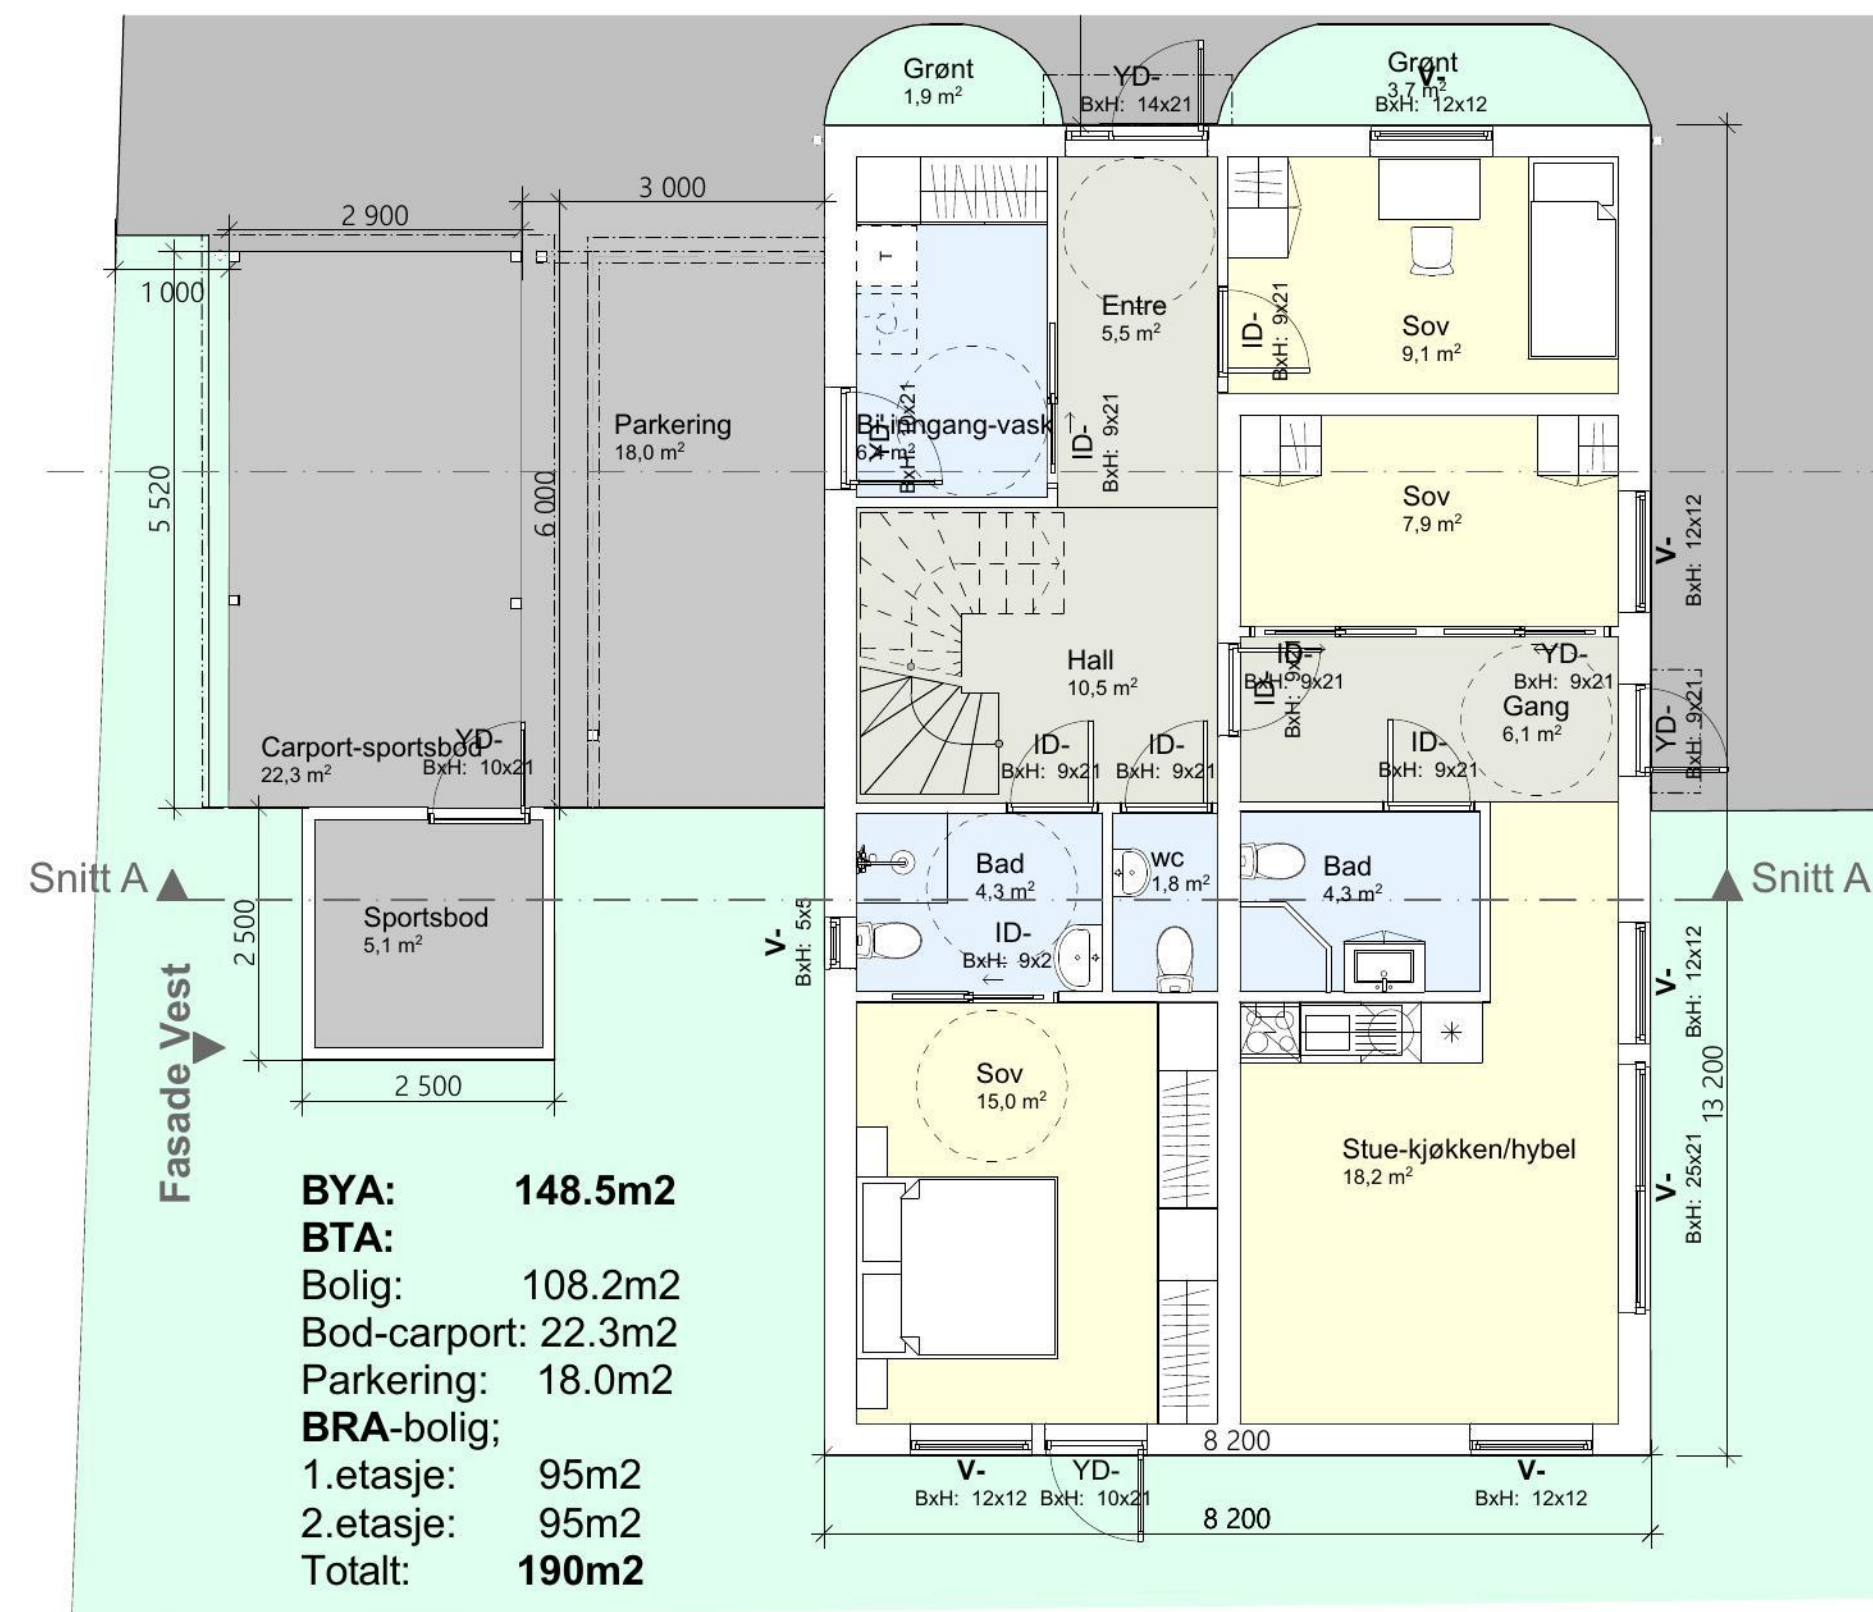

1.etasje

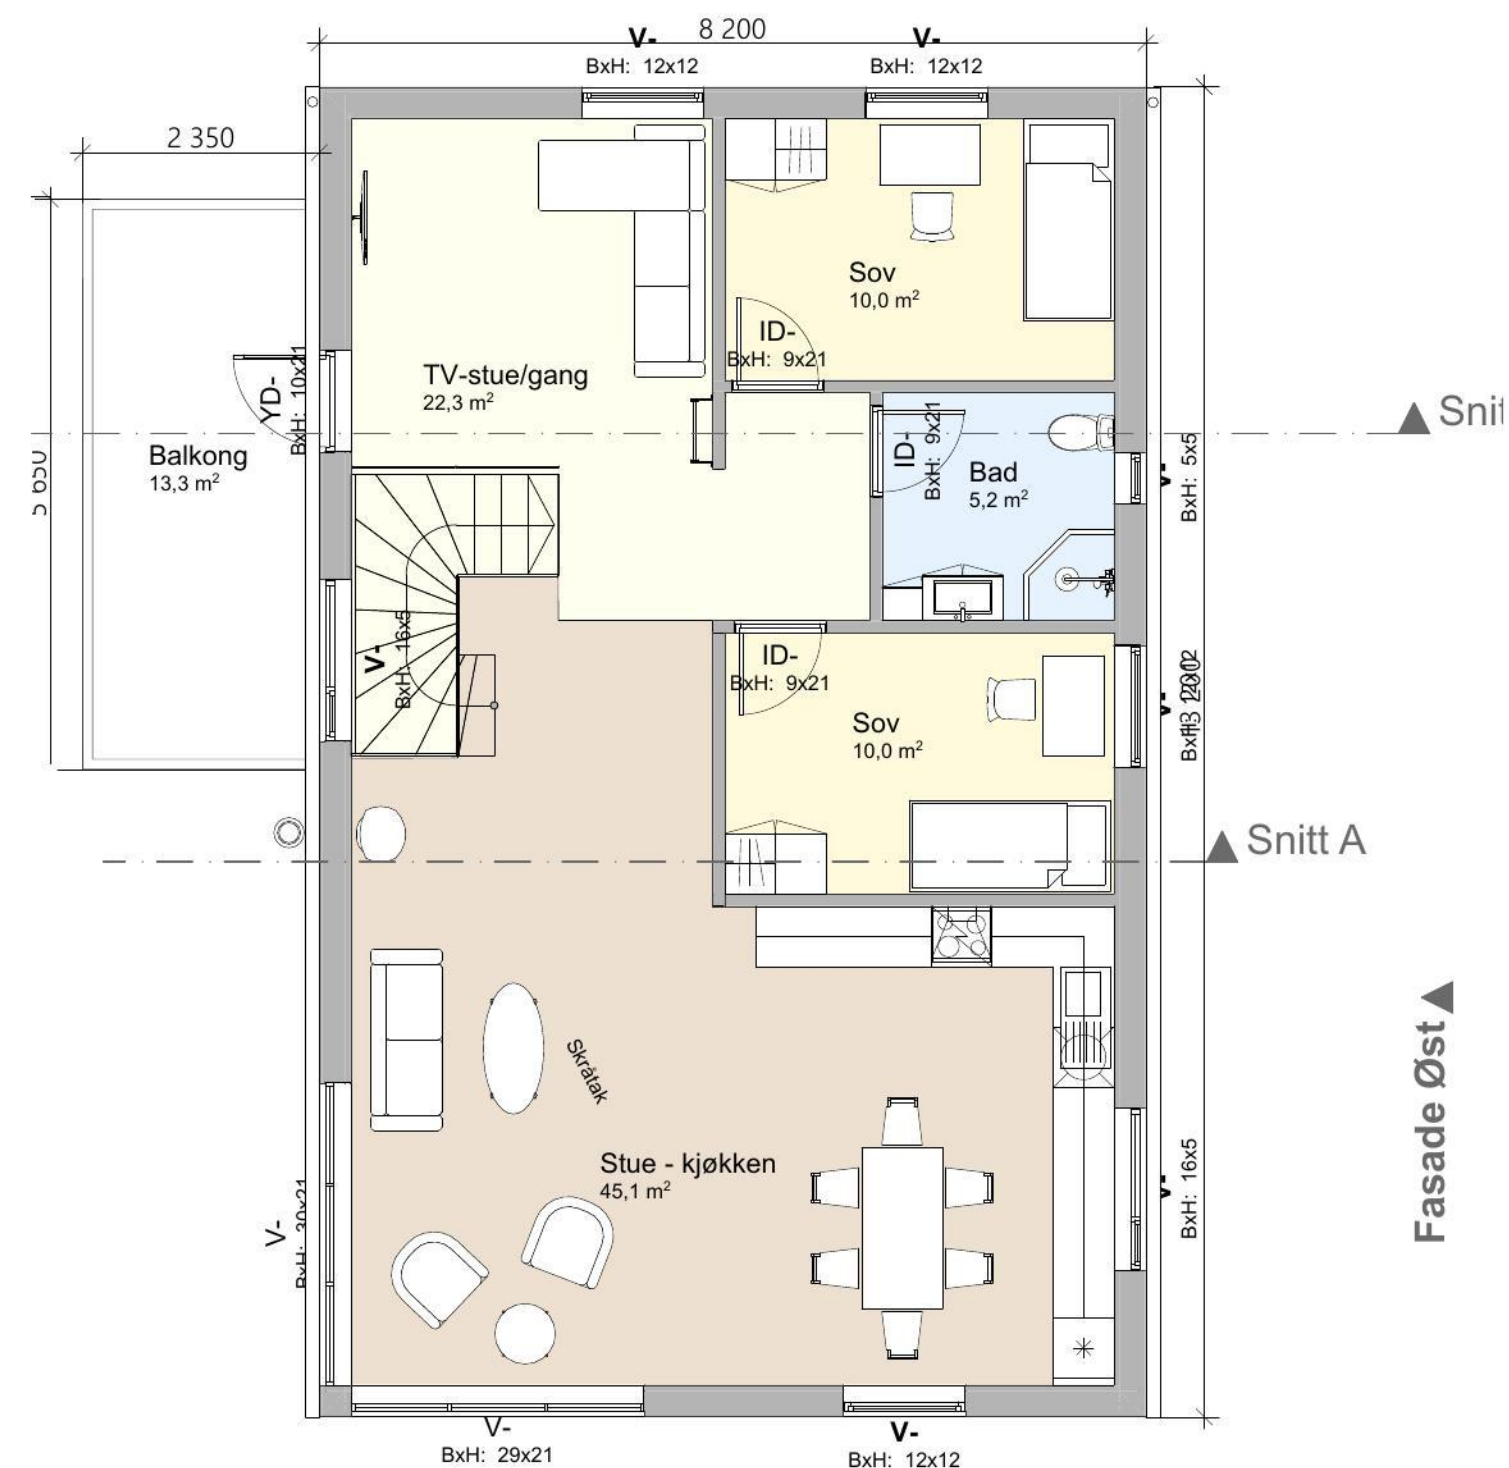

2.etasje

Tegninger kun utarbeidet for rammesøknad/deling. I forbindelse med søknad om IG, må det tas kontrollmåling, før utarbeidelse av prosjekterings/arbeidstegninger.

Rev.:16.12.23
Rev.:03.03.23
Rev.:19.10.22
Rev.:06.10.22

Prosjekt: Enebolig, carport og bod	Kontroll prosjekt:	
	Sign.: t.th	Kontroll: t.th.
Adresse: Buflåtveien 4 4018 Stavanger	Gnr/Bnr. 17/835 A:1002 m2	
Arkitektur: Botakst as Gretebakken 12 4355 Kvernaland	 bygg og taksttjenester www.botakst.no	
© Alle rettigheter tilhører utførende for arkitektur, kopiering eller bruk av disse tegningene er forbudt uten skriftlig samtykke		Dato: 01.09.2022
Tegning: Plan 1.etasje og 2.etasje		Målestokk: 1:100
		Tegningsnr.: E1