

Arealtabell (BRA) Åpent			
Etasje:	Beskrivelse:	Type:	Areal (m²)
Plan 01	Overbygget areal	Åpent	5,5
Plan 01	Overbygget areal	Åpent	7,2
Plan 01	Overbygget areal	Åpent	7,7
			20,4
Totalt Areal:			20,4

Fasade 3

MERKNADER:


- For isolasjonsmengder, U-verdier og energiforsyning, se energidokumentasjon.
- Arealer oppgitt i tabeller iht. NS3940
- BYA er beregnet til utside kledning / underliggende søyle. Bygningsdeler mindre enn 5m over terreng, utkraget mer enn 1 meter tas med i sin helhet.
- Arealer angitt i de enkelte rom er oppgitt som faktiske gulvareal.
- Romhøyde er 2,4m dersom annet ikke er spesifisert.
- I rom under skrå himling kan deler av dette areal ha lavere takhøyde enn 2,4m.
- Målsetting på utside mur / stenderverk, utv. søyler til senter.
- Gesims og mønehøyde er målt fra gjennomsnittlig planert terreng, plassert 0,35m under ferdig støpt plate.
- Statiske beregninger for konstruksjonen er ikke utført. Forbehold om endringer av dimensjoner og plasseringer ved detaljprosjektering.
- Innredninger og sanitærutstyr vist på tegning kun inkludert hvis angitt i kontrakt.
- Evt. snøfangere monteres iht. Sintef bfs detaljblad 525.931
- For bolig hvor sportsbod ikke prosjekteres tilknyttet bolig, forutsettes sportsbod (5m²) iht. TEK17, frittliggende eller i uthus/garasje, oppført samtidig med bolig.

Ved tilgjengelig bolig:

- Trinnfri adkomst til sportsbod.
- Vridere (dører, vinduer etc.) plasseres mellom 0,8 – 1,2 m i fra gulv.

Fasade 4

Fasade 2

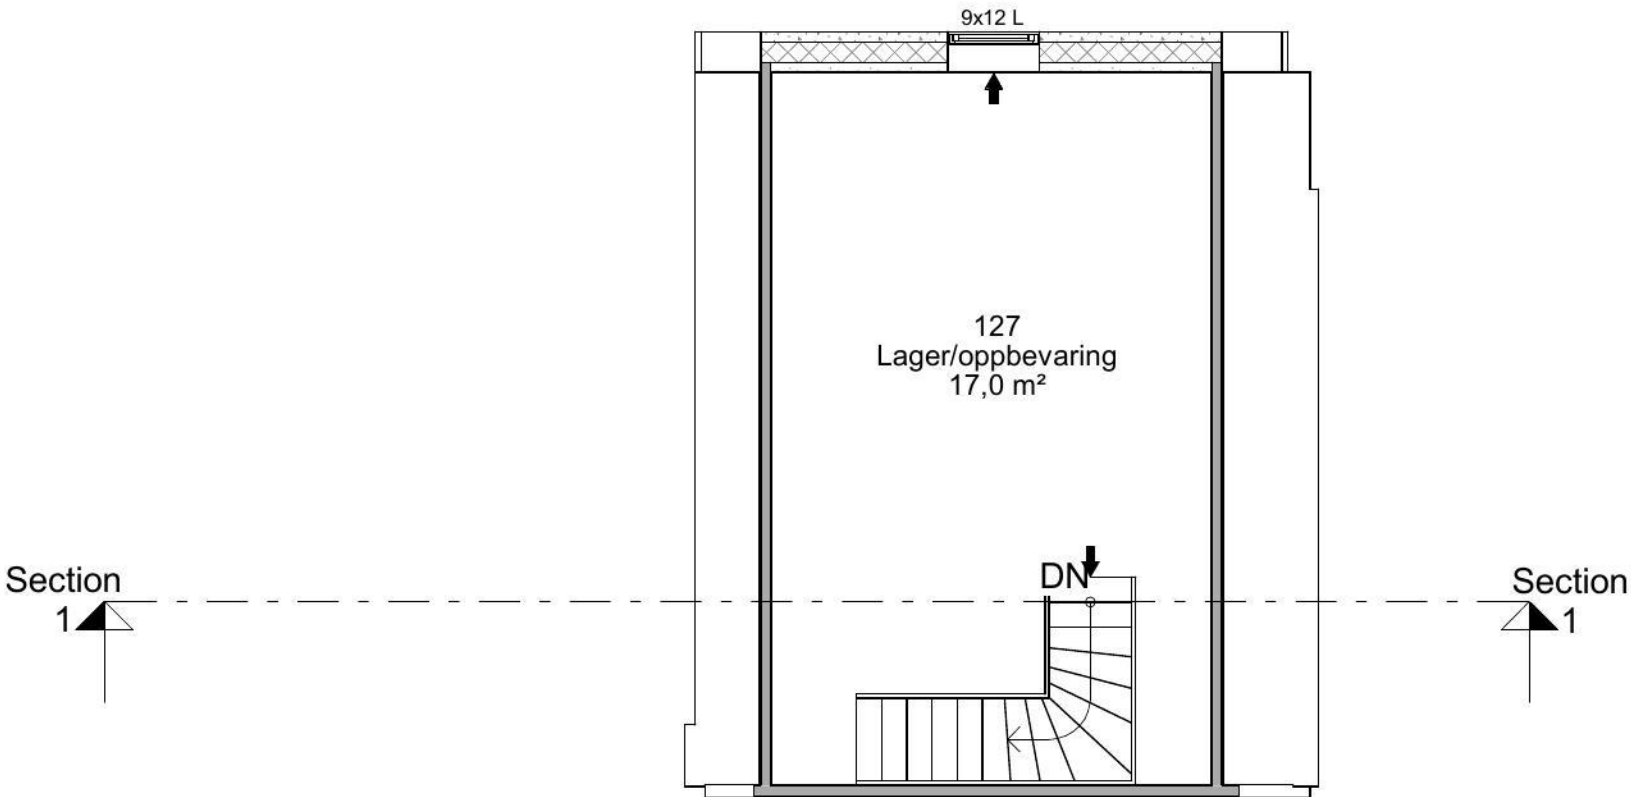

Fasade 1

BYGGEMELDINGSTEGNING

Symbolforklaring:

- ▼ = Adkomst Hovedinngang
- ➔ = Rømningsvei
- BV = Bærevegg
- D = Drager
- S = Synlig innv. søyle
- SD = Synlig Drager
- DM = Drager i møne
- SG = Sikkerhetsglass

Overbygget areal (BYA)			
Beskrivelse		Areal netto	Areal (m²)
Overbygget areal		7,9	8
Overbygget areal		7,7	8
Overbygget areal		Arealtabell (BRA) 11,6	12
27,2			
Etasje:	Beskrivelse:	Type:	Areal (m²)
Plan 01	Eksisterende bolig		49,1
Plan 01	Tilbygg		122,8
Plan 02	Tilbygg 2.etg		17,0
Totalt Areal:			188,9



TILTAKSHAVER:
Alf Jakob Svendsen

G.nr/B.nr:
235/12

BYGGEPLASS:
Østhusmarka 31

KOMMUNE:
Stavanger

REV.	DATO	REVISJON	SIGN.
3	16.11.23	Oppstart Byggemeldingstegninger	VAK
2	07.11.23	Flytte tilbygg 1m vestover	VAK
1	18.10.23	Skisseutkast	VAK

TEGN, INNHOLD: Plan 02			FORMAT: A3	MÅLESTOKK: 1 : 100
PROSJEKT/HUSTYPE:			KONTR: -	PROSJEKT NR:
ARKITEKT: V. Klavenes	DATO: 01.04.21	TEGN: Author	REV: 3	TEGN.NR: 22-PL-21