


- MERKNADER:**
- For isolasjonsmengder, U-verdier og energiforsyning, se energidokumentasjon.
 - Arealer oppgitt i tabeller iht. NS3940
 - BYA er beregnet til utside kledning / underliggende søyle. Bygningsdeler mindre enn 5m over terreng, utkraget mer enn 1 meter tas med i sin helhet.
 - Arealer angitt i de enkelte rom er oppgitt som faktiske gulvareal.
 - Romhøyde er 2,4m dersom annet ikke er spesifisert.
 - I rom under skrå himling kan deler av dette areal ha lavere takhøyde enn 2,4m.
 - Målsetting på utside mur / stenderverk, utv. søyler til senter.
 - Gesims og mønehøyde er målt fra gjennomsnittlig planert terreng, plassert 0,35m under ferdig støpt plate.
 - Statiske beregninger for konstruksjonen er ikke utført. Forbehold om endringer av dimensjoner og plasseringer ved detaljprosjektering.
 - Innredninger og sanitærutstyr vist på tegning kun inkludert hvis angitt i kontrakt.
 - Evt. snøfangere monteres iht. Sintef bfs detaljblad 525.931
 - For bolig hvor sportsbod ikke prosjekteres tilknyttet bolig, forutsettes sportsbod (5m²) iht. TEK17, frittliggende eller i uthus/garasje, oppført samtidig med bolig.
- Ved tilgjengelig bolig:**
- Trinnfri adkomst til sportsbod.
 - Vridere (dører, vinduer etc.) plasseres mellom 0,8 – 1,2 m i fra gulv.

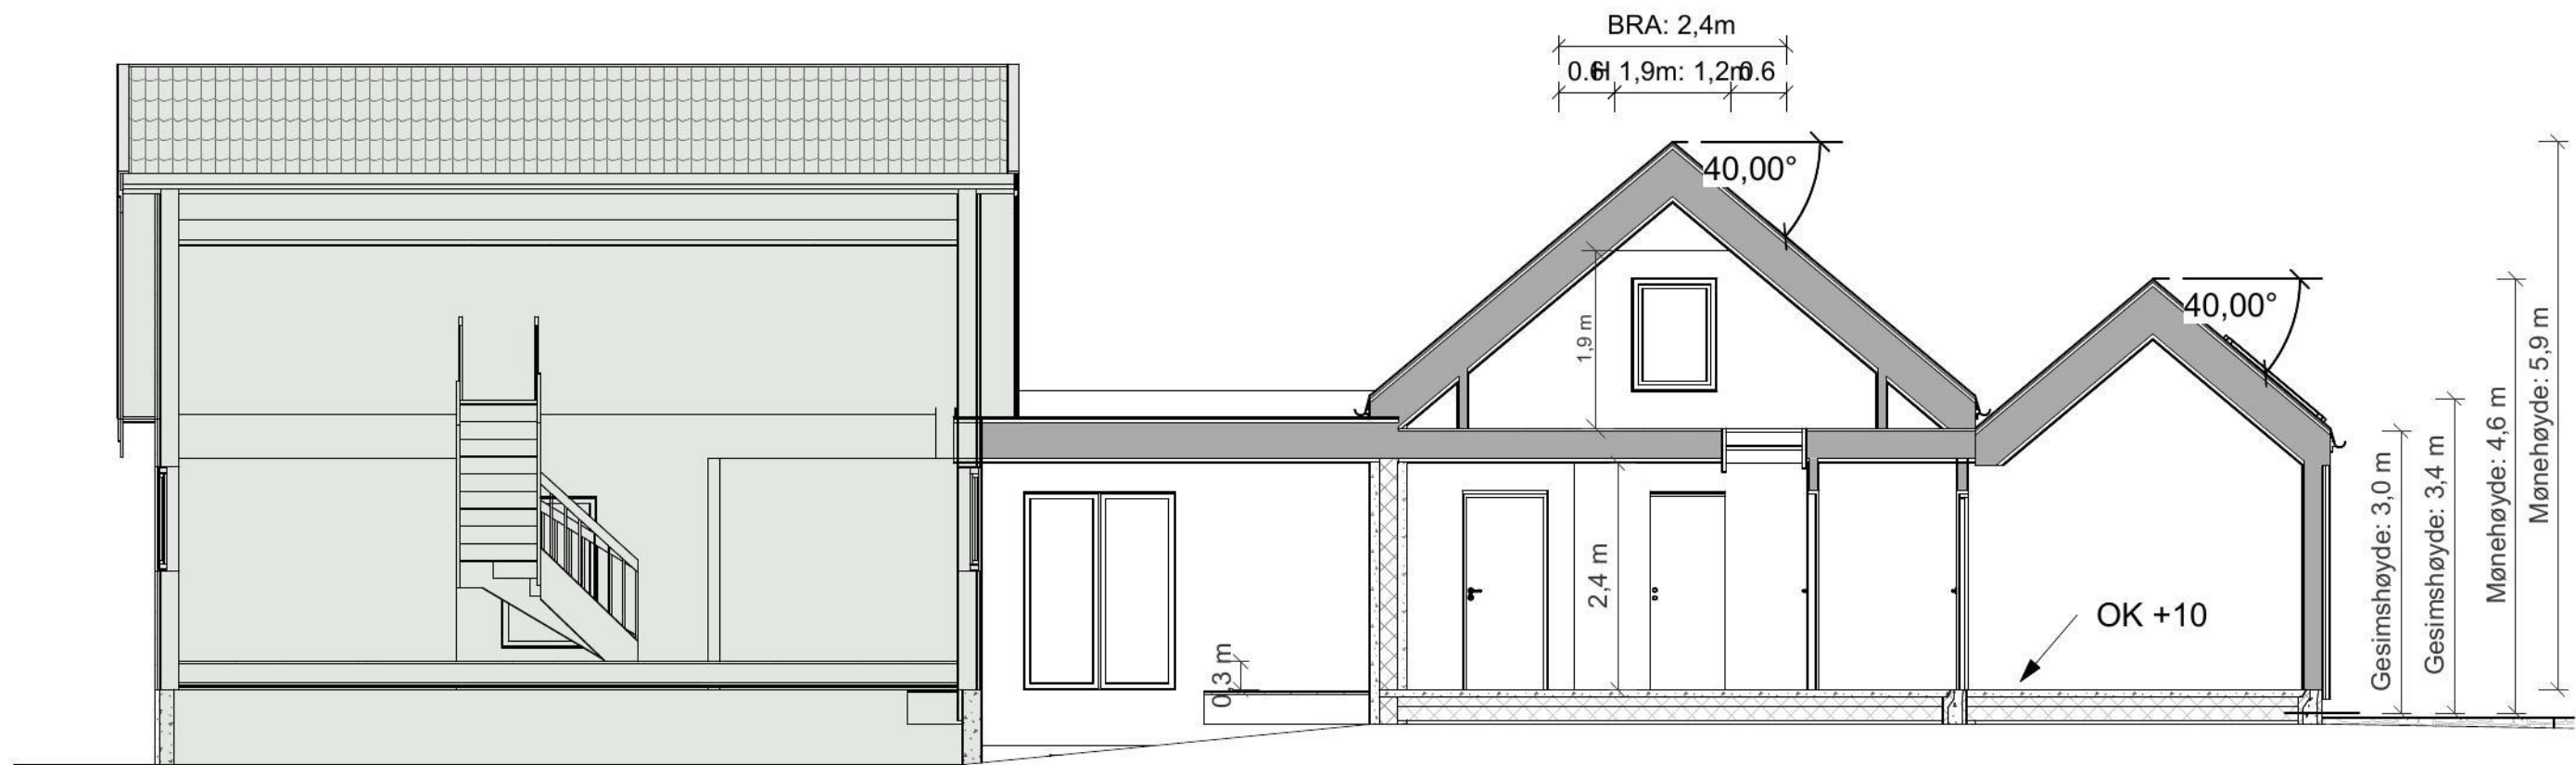

Section 1

BYGGEMELDINGSTEGNING



TILTAKSHAVER:
Alf Jakob Svendsen

G.nr/B.nr:
235/12

BYGGEPLASS:
Østhusmarka 31

KOMMUNE:
Stavanger

REV.	DATO	REVISJON	SIGN.
3	16.11.23	Oppstart Byggemeldingstegninger	VAK
2	07.11.23	Flytte tilbygg 1m vestover	VAK
1	18.10.23	Skisseutkast	VAK

TEGN, INNHOLD: Snitt			FORMAT: A3	MÅLESTOKK: 1 : 100
PROSJEKT/HUSTYPE:			KONTR: -	PROSJEKT NR:
ARKITEKT: V. Klavenes	DATO: 01.04.21	TEGN: Author	REV: 3	TEGN.NR: 42-SN-01