


NB!
Nedsenket gulv 5cm
Bad og vaskerom

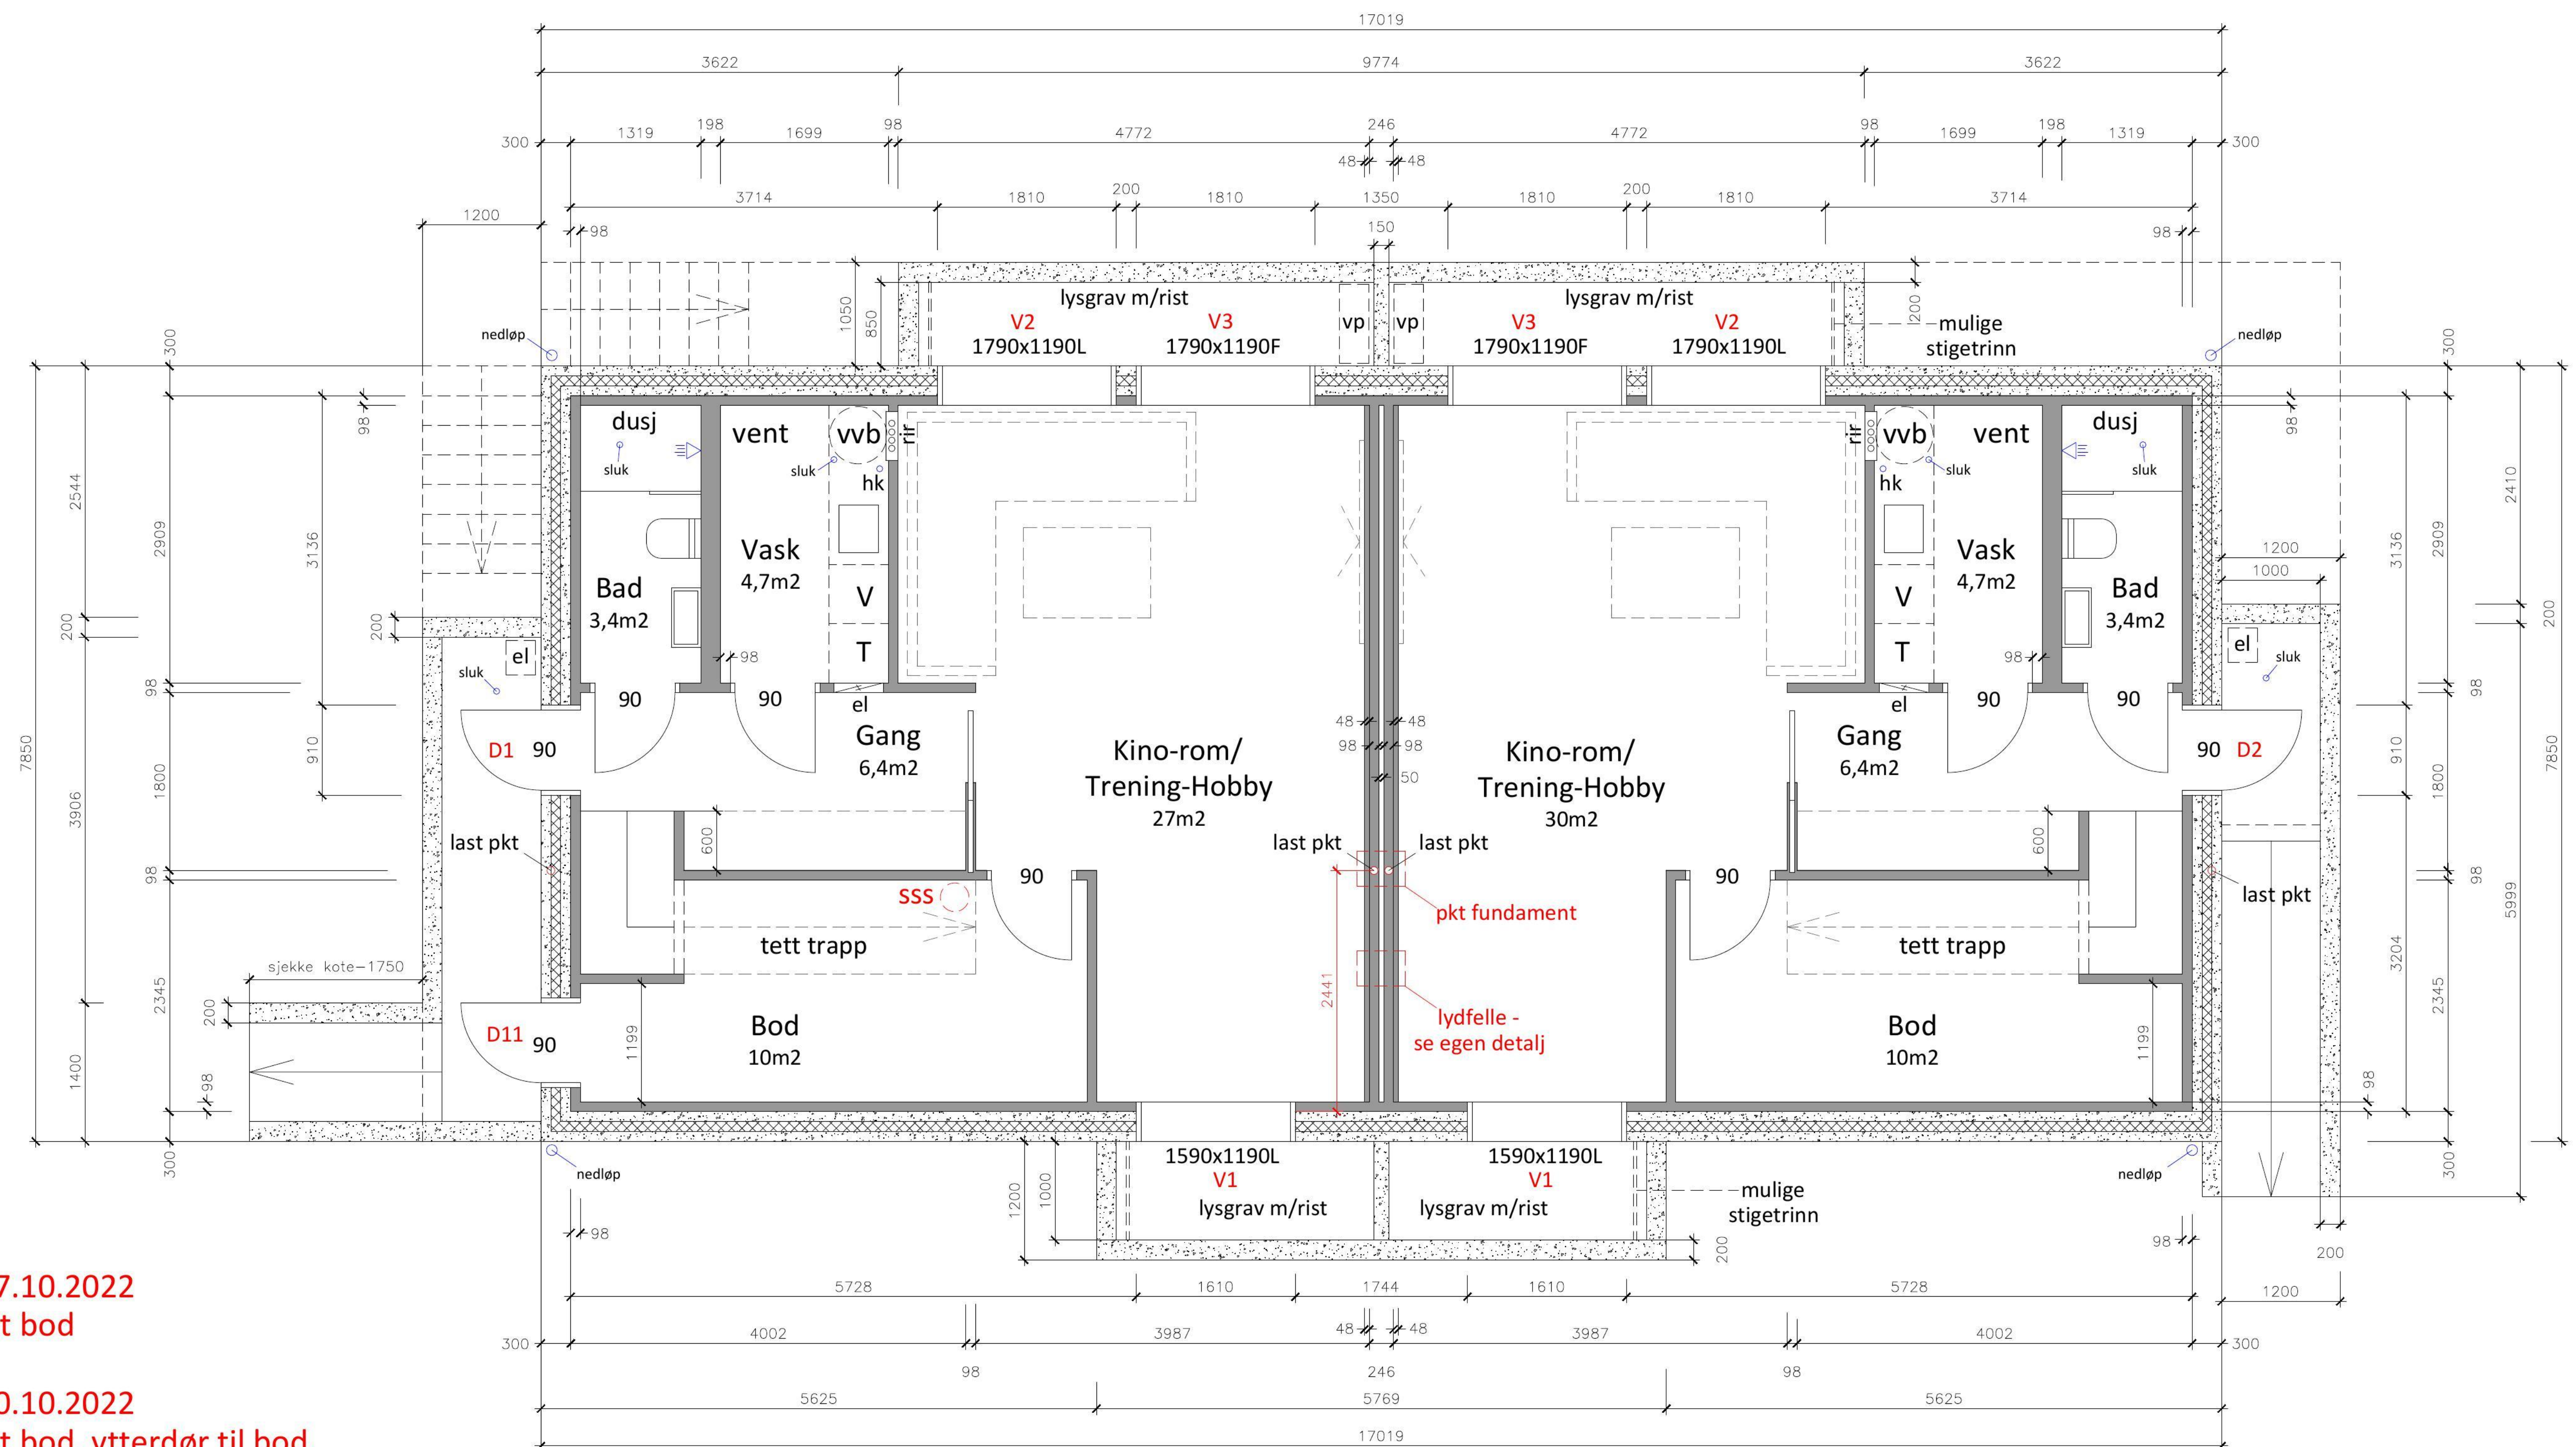

Rev: 17.10.2022
Utvidet bod

Rev: 10.10.2022
Utvidet bod, ytterdør til bod,
sentralstøvsug, sluker, pkt fundament, mm

KJELLERPLAN

UNDERLAG FOR ARBEIDSTEGNINGER
A2-1:50
11.08.2022
Arkitekt: Odd S Idland

Plutoveien 28 A og B - Stavanger Kommune
Gnr:24 Bnr: 154