



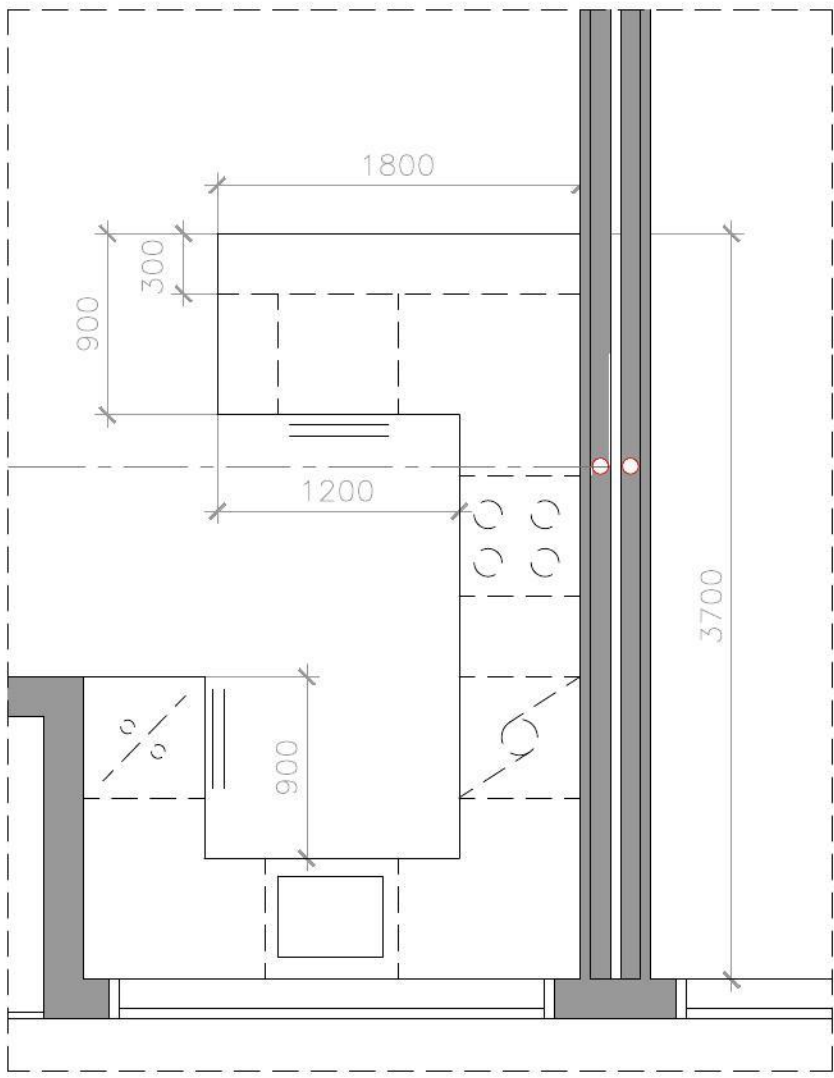

Foreløpige kjøkkenmål

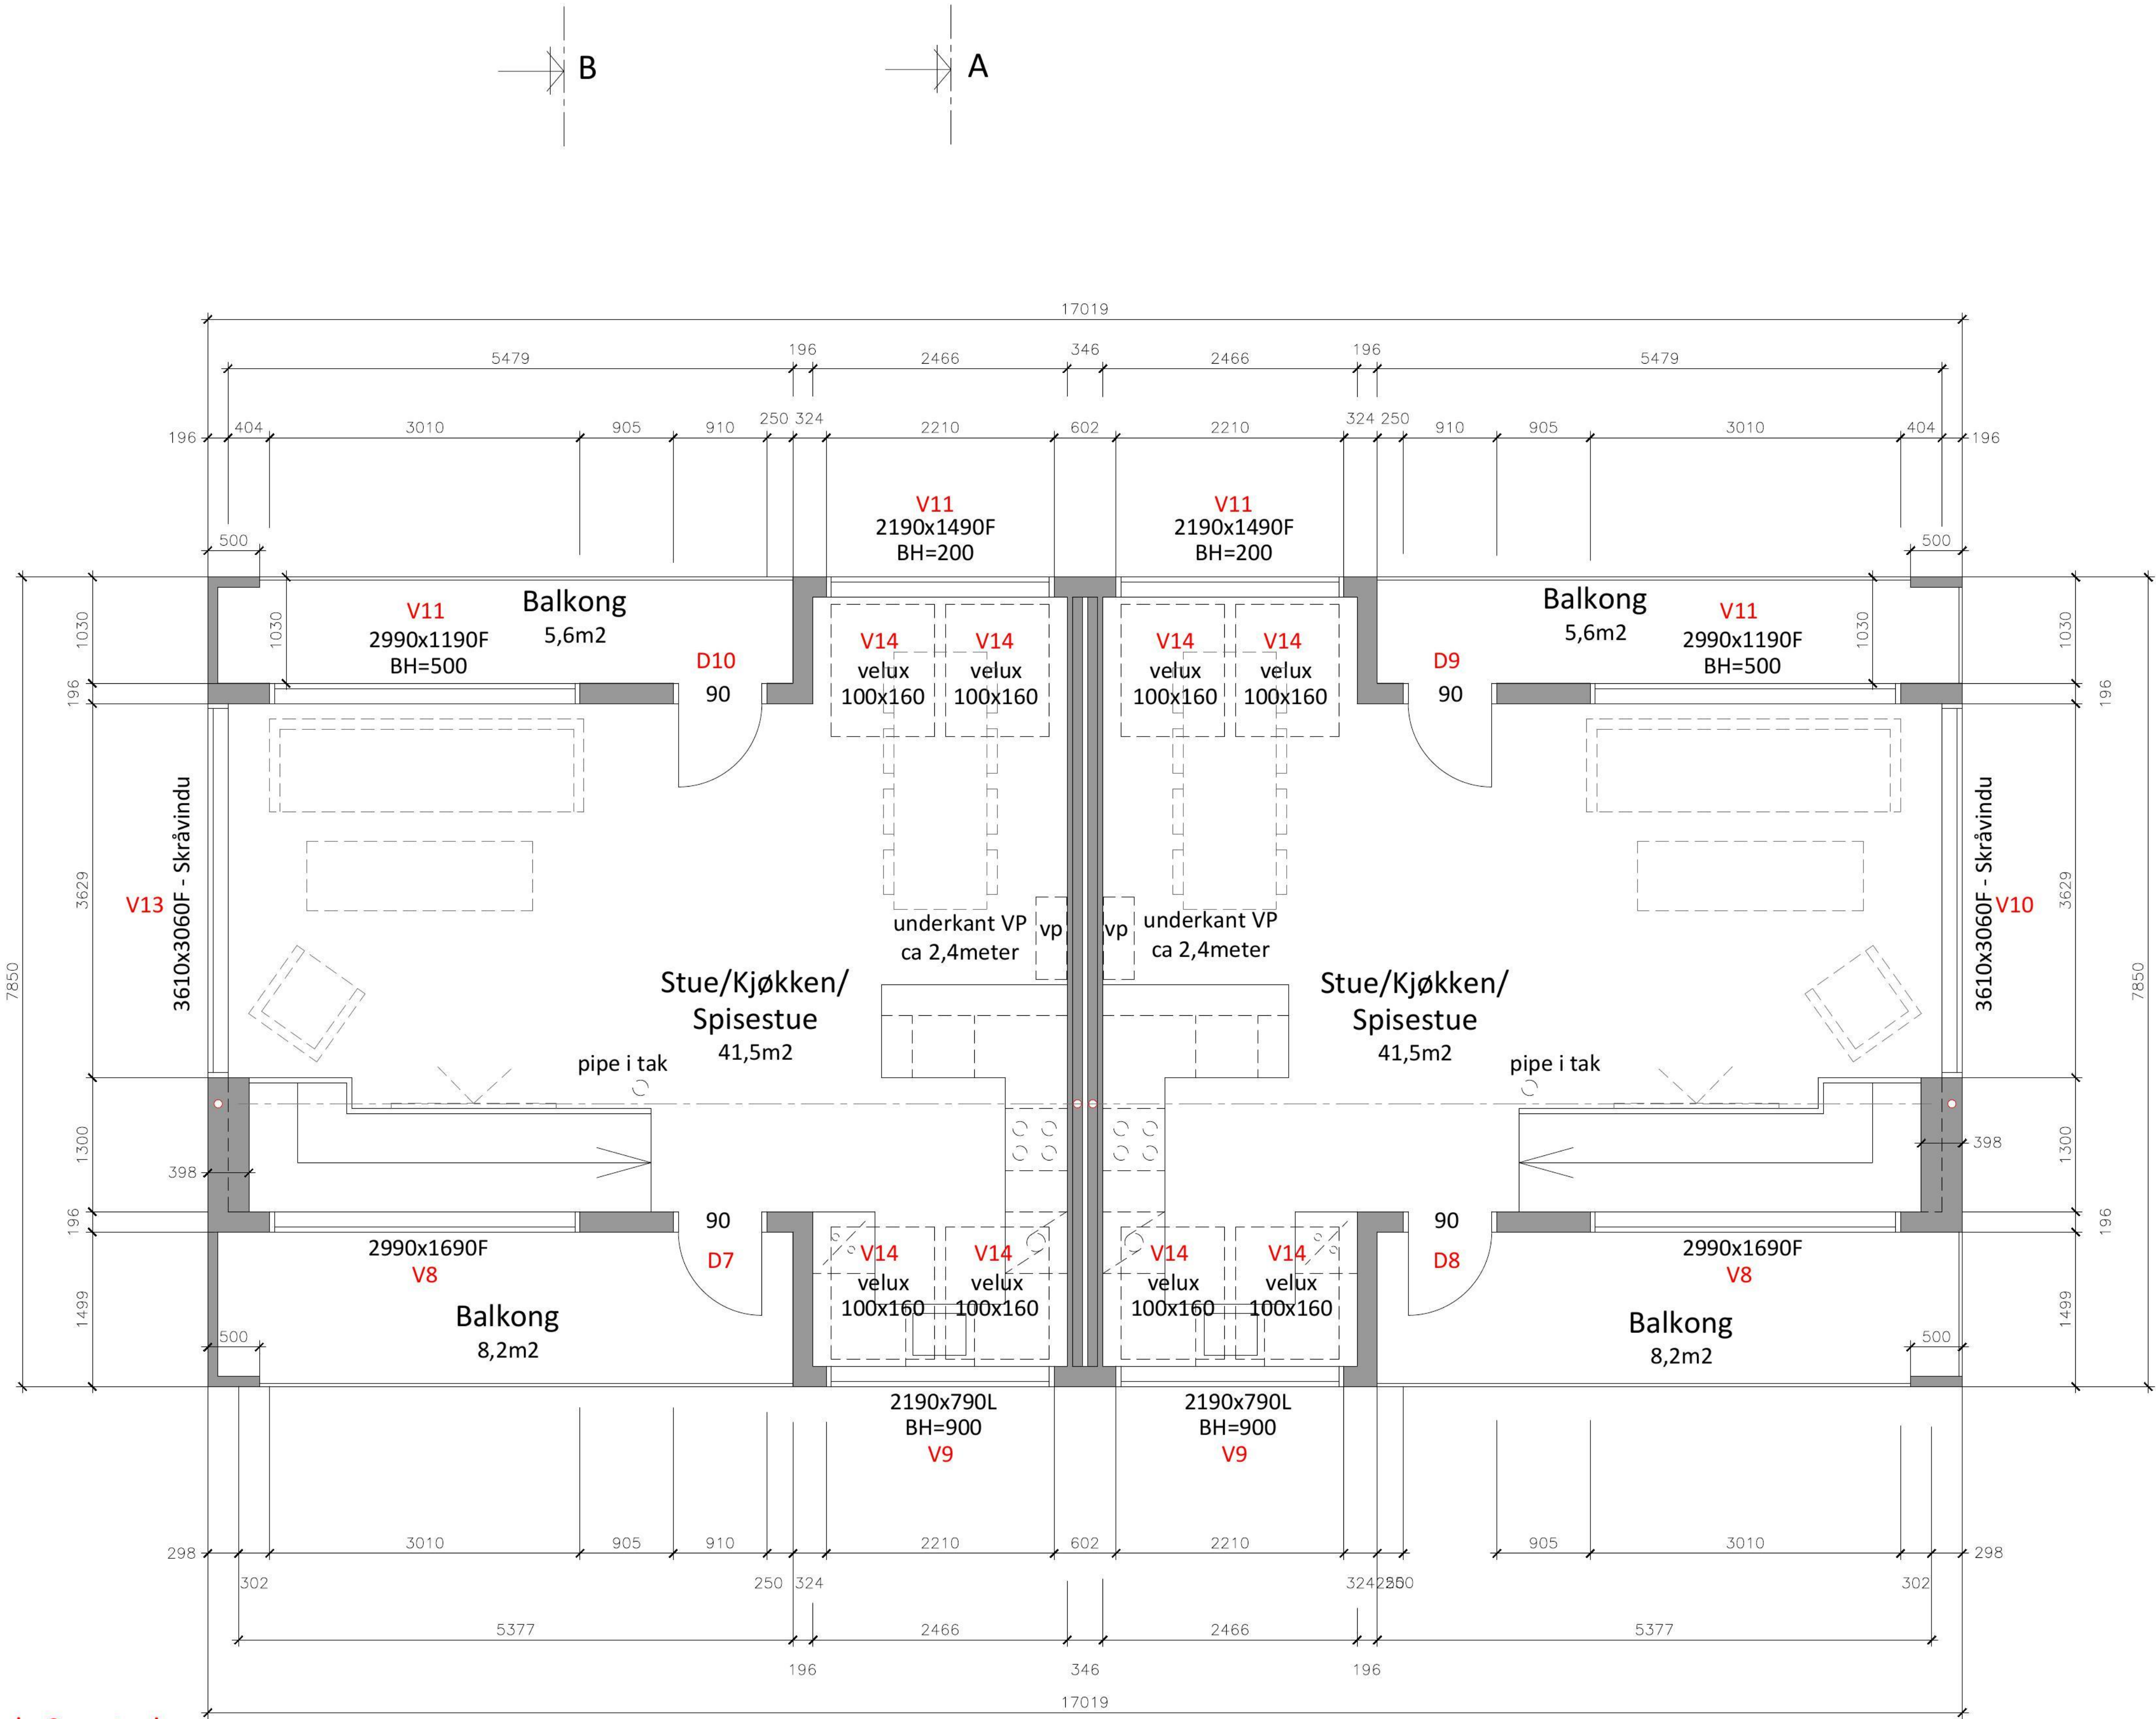

NB! - Terrassedører 2 etasje har høyde 2 meter!

2.ETASJE

UNDERLAG FOR ARBEIDSTEGNINGER
A2-1:50
11.08.2022
Arkitekt: Odd S Idland

Plutoveien 28 A og B - Stavanger Kommune
Gnr:24 Bnr: 154



BOLIG

Materialet. Tegningene er omfattet av åndsverklovens bestemmelser og er vernet åndsverk iht åndsverklovens §1. Uten særskilt avtale er enhver eksemplarframstilling og tilgjengeliggjøring, i opprinnelig eller endret skikkelse, ulovlig utnyttelse.