


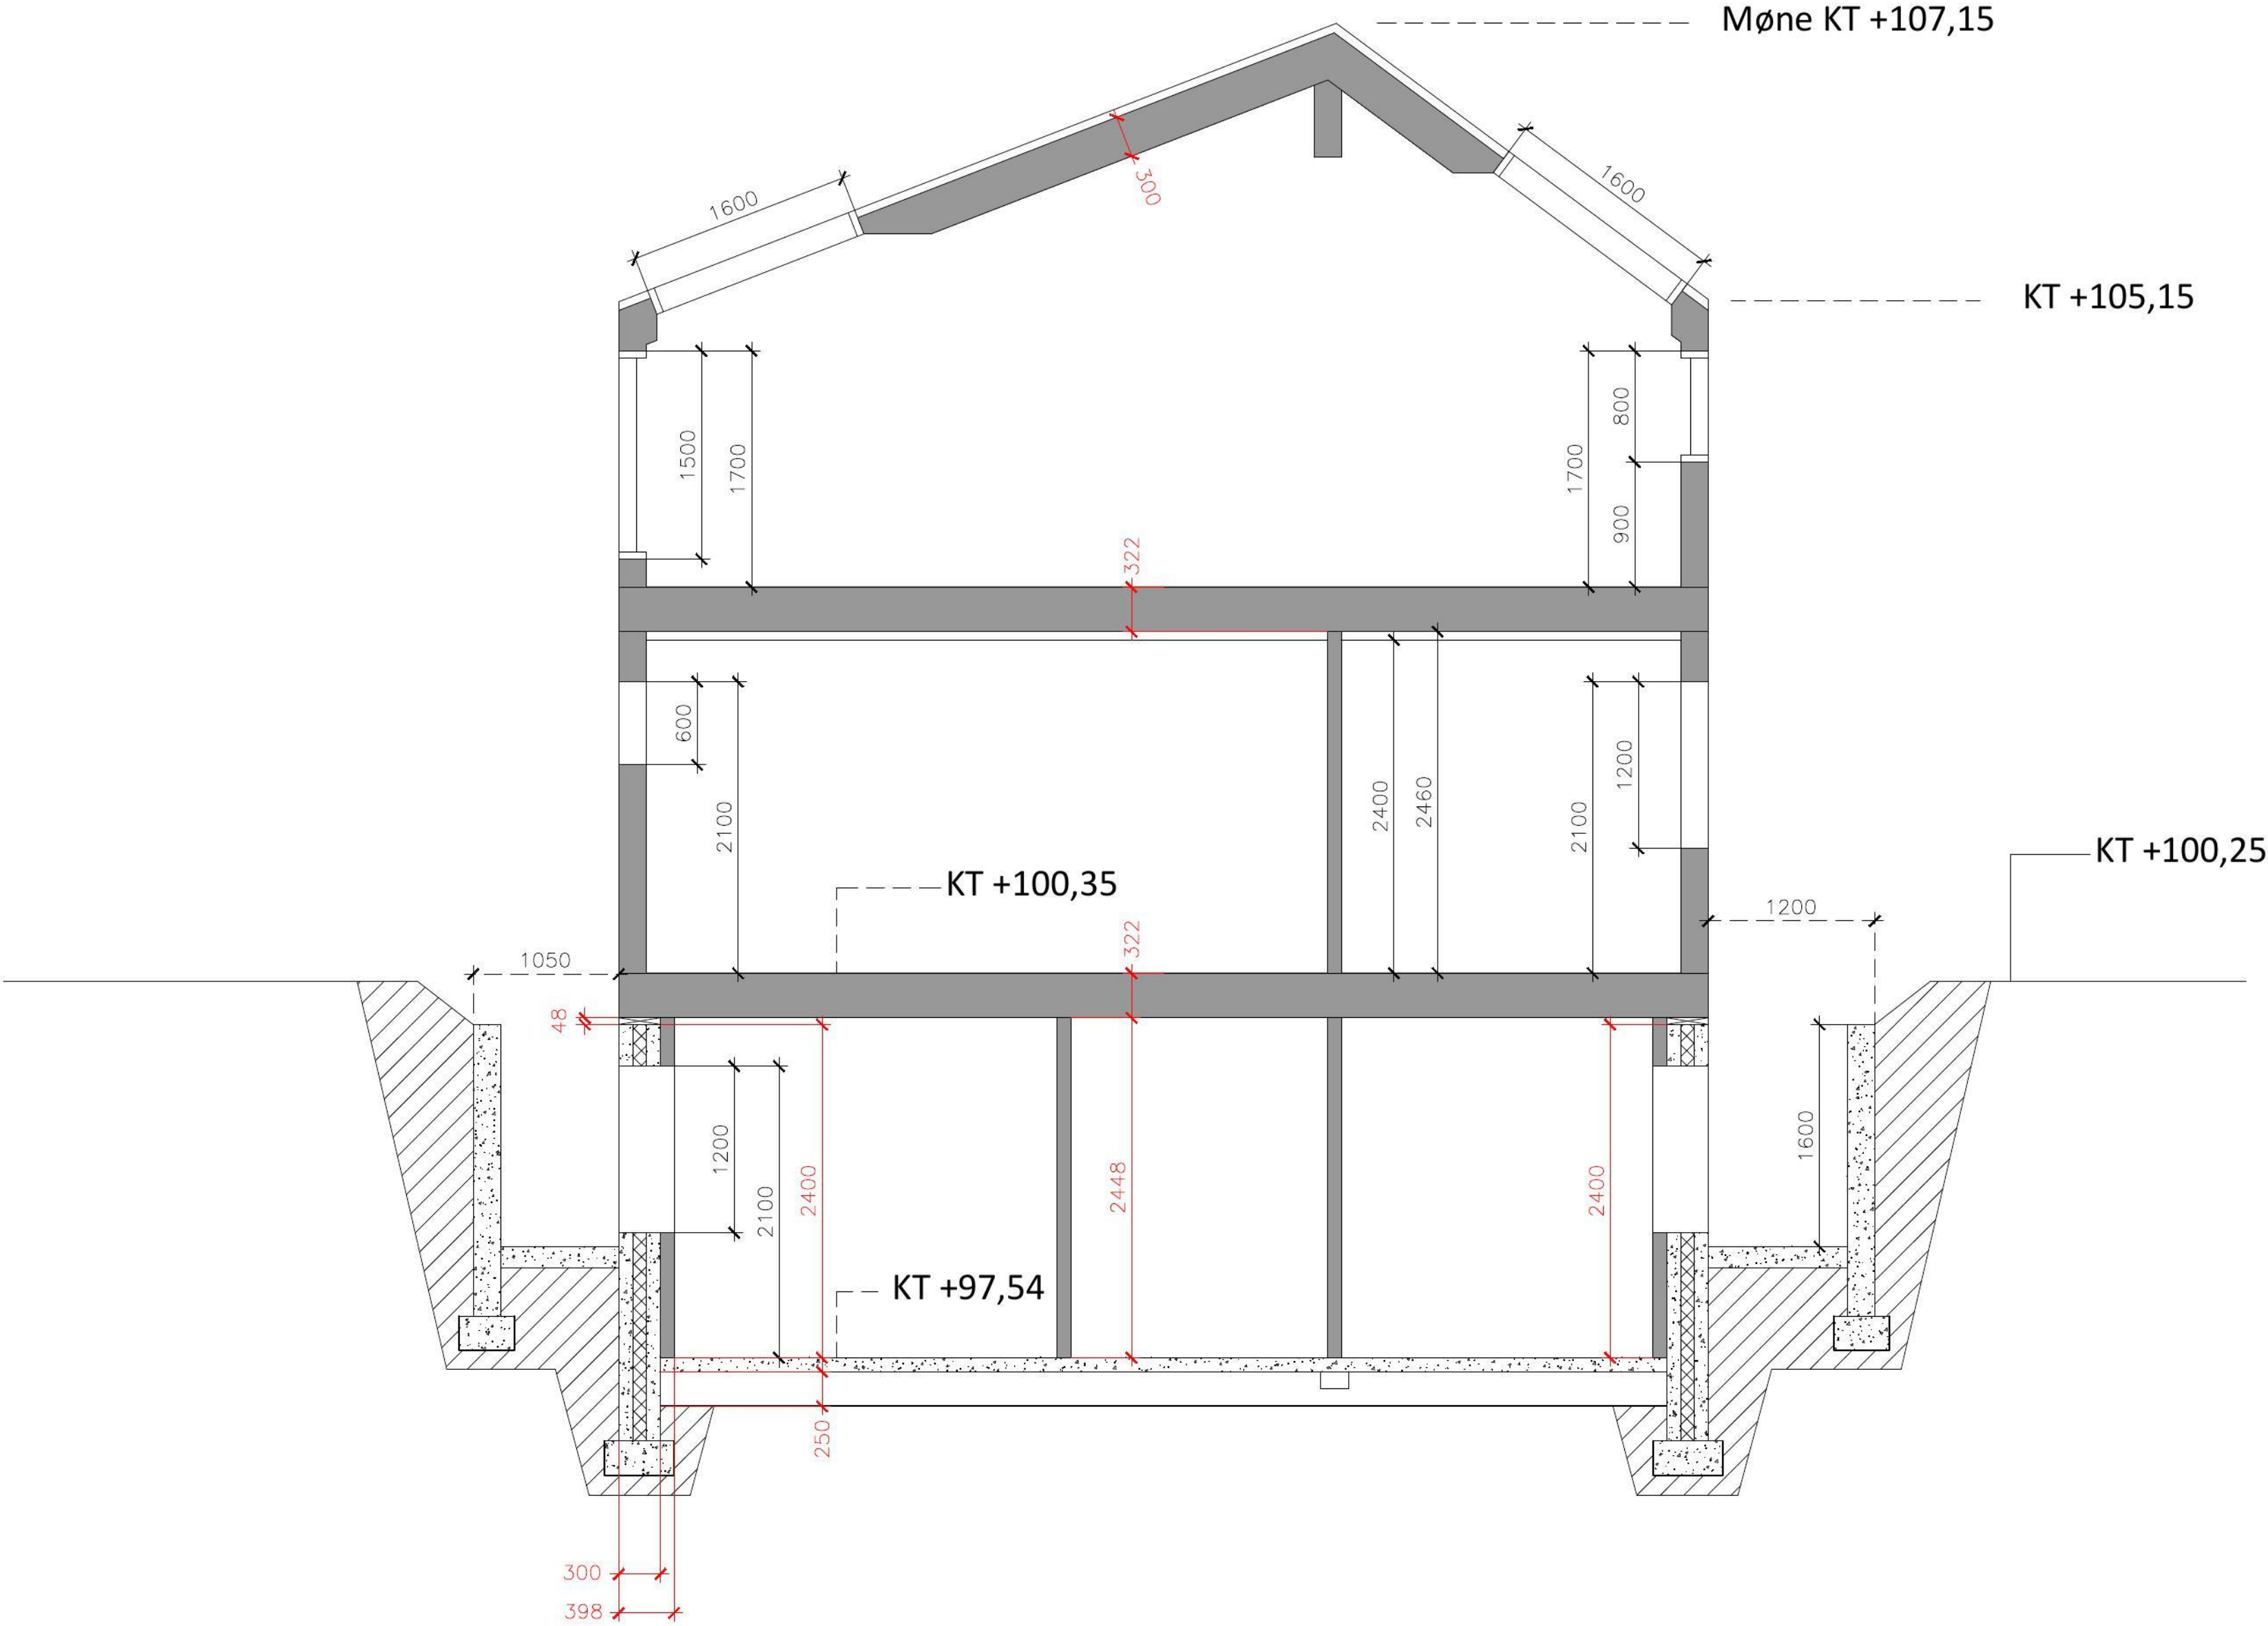

Rev: 1010.2022
Detalj mål påført, murer etc for kontroll!!!

SNITT A:A

SNITT A:A
UNDERLAG FOR ARBEIDSTEGNINGER
A2-1:50
11.08.2022
Arkitekt: Odd S Idland

Plutoveien 28 A og B - Stavanger Kommune
Gnr:24 Bnr: 154

Materialet. Tegningene er omfattet av åndsverklovens bestemmelser og er vernet åndsverk iht åndsverklovens §1. Uten særskilt avtale er enhver eksemplarframstilling og tilgjengeliggjøring, i opprinnelig eller endret skikkelse, ulovlig utnyttelse.